
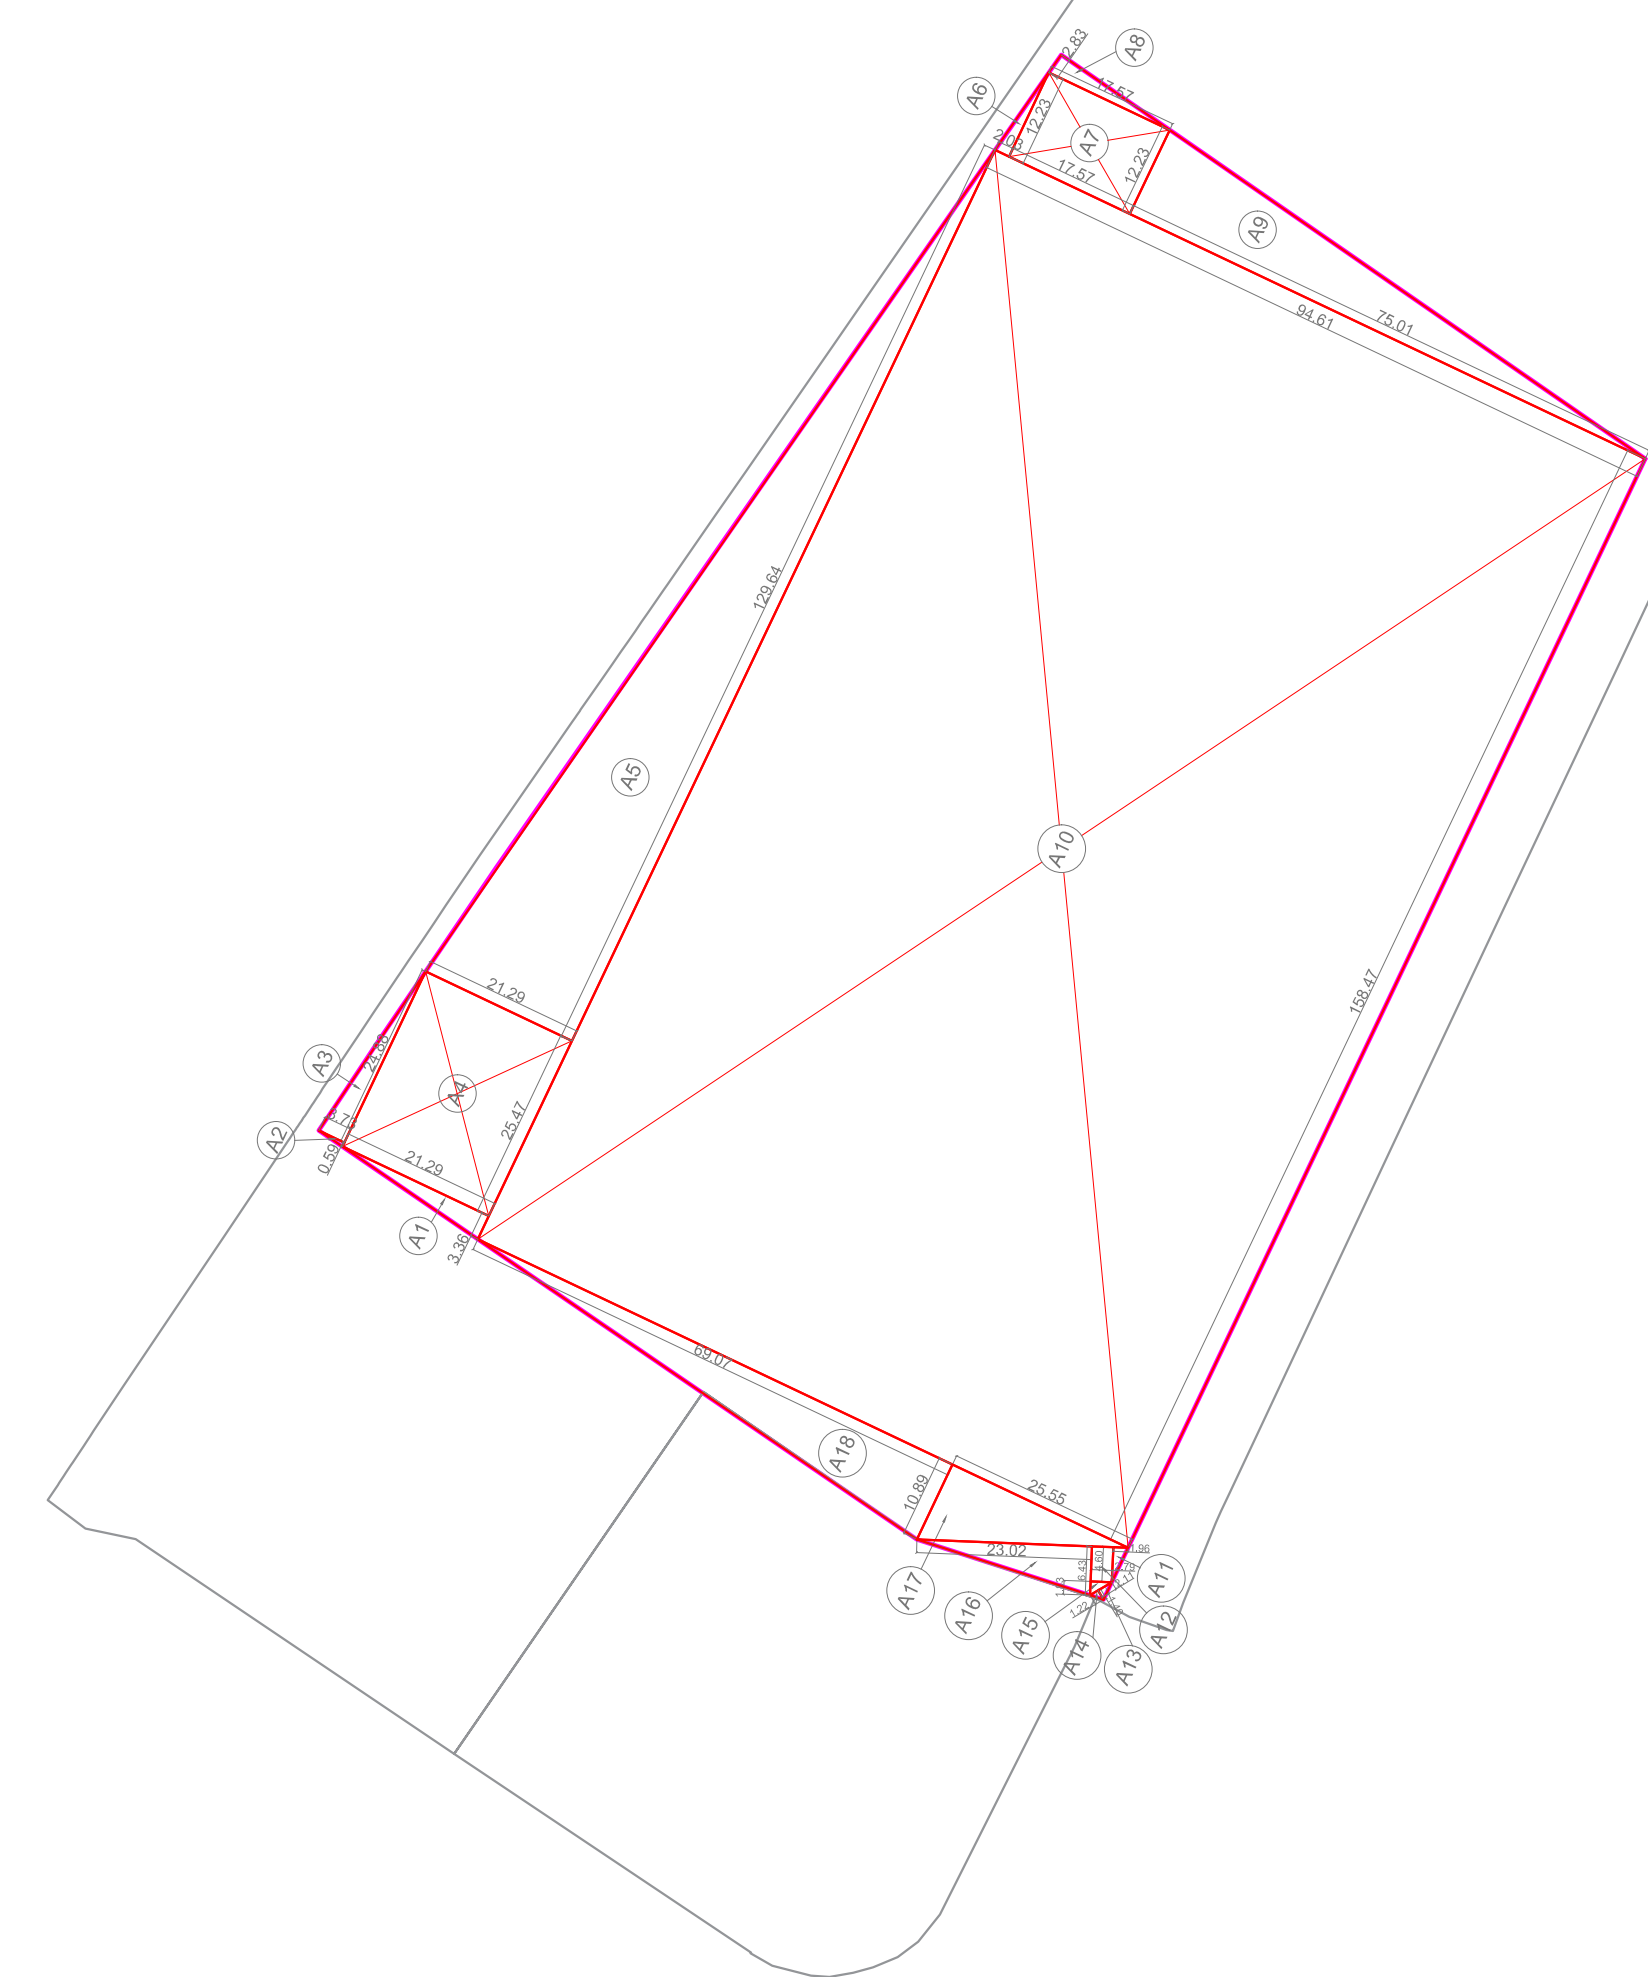


PODIUM AREA DIAGRAM
SCALE - 1:1000

AS PER CTS NO. 1,
CTS NO. 3

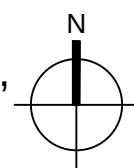

PODIUM LEVEL CALCULATION				
DESCRIPTION	DIMENSION (IN METERS)			AREA (IN)
	FACTOR	BASE	HEIGHT	
A1	0.5	3.36	21.23	35.767
A2	0.5	0.59	3.73	1.1004
A3	0.5	3.73	24.88	46.401
A4	1	21.23	25.47	542.26
A5	0.5	21.23	129.64	1380
A6	0.5	2.03	12.23	12.413
A7	1	17.57	12.23	214.88
A8	0.5	2.83	17.57	24.862
A9	0.5	12.23	75.01	458.63
A10	1	158.47	34.61	14333
A11	0.5	1.96	4.6	4.508
A12	1	2.73	4.6	12.834
A13	0.5	1.4	2.11	1.477
A14	0.5	1.22	1.4	0.854
A15	0.5	1.83	2.73	2.5529
A16	0.5	6.43	23.02	74.009
A17	0.5	10.89	25.55	139.12
A18	0.5	10.89	69.07	376.09
TOTAL AREA				18321

TOTAL AREA PER PODIUM LEVEL	18320.7 SQ.M
TOTAL AREA OF 3 PODIUM LEVELS	54962.1 SQ.M

PARKING REQUIREMENT		
BUILDINGS	TWO WHEELER	FOUR WHEELER
BUILDING 2	132	66
BUILDING 3	220	110
BUILDING 4	220	110
BUILDING 5	143	72
BUILDING 6	176	88
BUILDING 7	143	72
TOTAL PARKING	1034	518


PODIUM PARKING PROPOSED		
PODIUM	TWO WHEELER	FOUR WHEELER
P1	382	132
P2	387	234
P3	387	234
TOTAL PARKING	1156	600



- LEGENDS
- PODIUM BOUNDARY
 - PHASE 1 BOUNDARY
 - VEHICAL MOVEMENT AXIS
 - AXIS FOR RAMP
 - AXIS FOR INTERNAL MOVEMENT
 - ROAD

PODIUM LEVEL PLAN - P1
SCALE - 1:750

AS PER CTS NO. 1,
CTS NO. 3

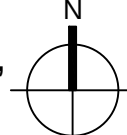

SHEET NO :

LOCATION PLAN SCALE 1:4000

CONTENT OF SHEET :

LOCATION PLAN, GIS PLAN, DP PLAN
BLOCK PLAN
STILT FLOOR PLAN
AREA, WATER AND PARKING CALCULATIONS

SITE

NALLAH

COLOURING OF PLANS AS PER DCPR-34

THICK BLACK PLOT BOUNDARY	RED DOTTED DRAINAGE & SEWERAGE WORK
GREEN EXISTING STREET	BLUE DOTTED THIN WATER SUPPLY
GREEN DOTTED FUTURE STREET	RED HATCHED DEVIATIONS
THICK BLACK DOTTED PERM. BLDG	GREEN WASH RECREATION GROUND
NO COLOUR OPEN SPACES	BURNT SIENNA ROADS & SETBACKS
YELLOW HATCHED DEMOLISHED WORK	APPROPRIATE COLOUR CODE RESERVATIONS
RED FILLED PROPOSED WORK	

CERTIFICATE

"THIS IS TO CERTIFY THAT THE SCOPE OF WORK HAS BEEN EXPLAINED TO ME BY THE ARCHITECT / CONSULTANT AND CONSIDERING THE BUDGET PROVISION THEREFORE I AM SATISFIED WITH THE PROJECT PROPOSAL."

NOTE : USER SIGNATURE IS PROVIDED IN THE SCANNED COPY OF THE PLANS AND HENCE IT IS REQUESTED THAT THE SAME IS NOT INSISTED ON DIGITAL PRINTS, IN CASE REQUIRED, THE SAME WILL BE OBTAINED BEFORE STARTING OF THE WORK.

ARCHITECT MASTER & ASSOCIATES MUNICIPAL ARCHITECT

R1	08-08-2022	AREA STATEMENT REVISED	URVASHI
R2	03-08-2022	PODIUM PARKING LAYOUT	URVASHI

FILE PATH :
PC NO. 11 D:\Drawings\MILONI\1896-- 600 TENEMENTS, DEONAR
TYPE OF DWG :
APPROVAL DRAWING
CLIENT:
MUNICIPAL CORPORATION OF GREATER MUMBAI (MCGM)
TITLE OF DRAWING PODIUM LEVEL PLAN - P1
PLAN, GIS PLAN & DP PLAN
PROPOSED REDEVELOPMENT ON OPEN PLOT, KNOWN AS '600 TENEMENTS PLOT BEARING CTS NO. 1(PT) & CTS NO. 3(PT) OF VILLAGE DEONAR IN M/EAST WARD IN MUMBAI JOB TITLE :

DRAWN BY : URVASHI PROJECT CODE: 1896

CHECKED BY : UDM DRAWING NO: 1896-508

SCALE: AS MENTIONED DATE : 1.08.2022 REVISION NO: R1

THIS DRAWING IS THE PROPERTY OF MASTER & ASSOCIATES ARCHITECTS, INTERIOR DESIGNERS & PROJECT MANAGEMENT CONSULTANTS AND IS NOT TO BE REPRODUCED, COPIED HANDED OVER TO A THIRD PARTY OR USED FOR ANY PURPOSE OTHER THAN FOR WHICH IT HAS BEEN LOANED

STATUS



MASTER & ASSOCIATES
ARCHITECTS, INTERIOR DESIGNERS & PROJECT MANAGEMENT CONSULTANTS

MUMBAI
HAWARI HOUSE 38-39 HAWARI, DODH MARG,
MUMBAI - 400 001, India.
PHONE NO: +91-22-2352 4004 / 4736 FAX: 22700273
EMAIL: ADD: info@masterandassociates.com
info@masterandassociates.com

ALGERIES
BLANQUE ABID ELAZIZ CITE 18 LOGEMENTS BLOC - B1, N°3,
CITE DE HERRANJA, ZERALEDA ALGERIES.
PHONE NO: 0033 03 20 61 87 00 04
EMAIL: ADD: info@masterandassociates.com
MOBILE : 723 937958


PODIUM AREA DIAGRAM
SCALE - 1:1000

AS PER CTS NO. 1,
CTS NO. 3

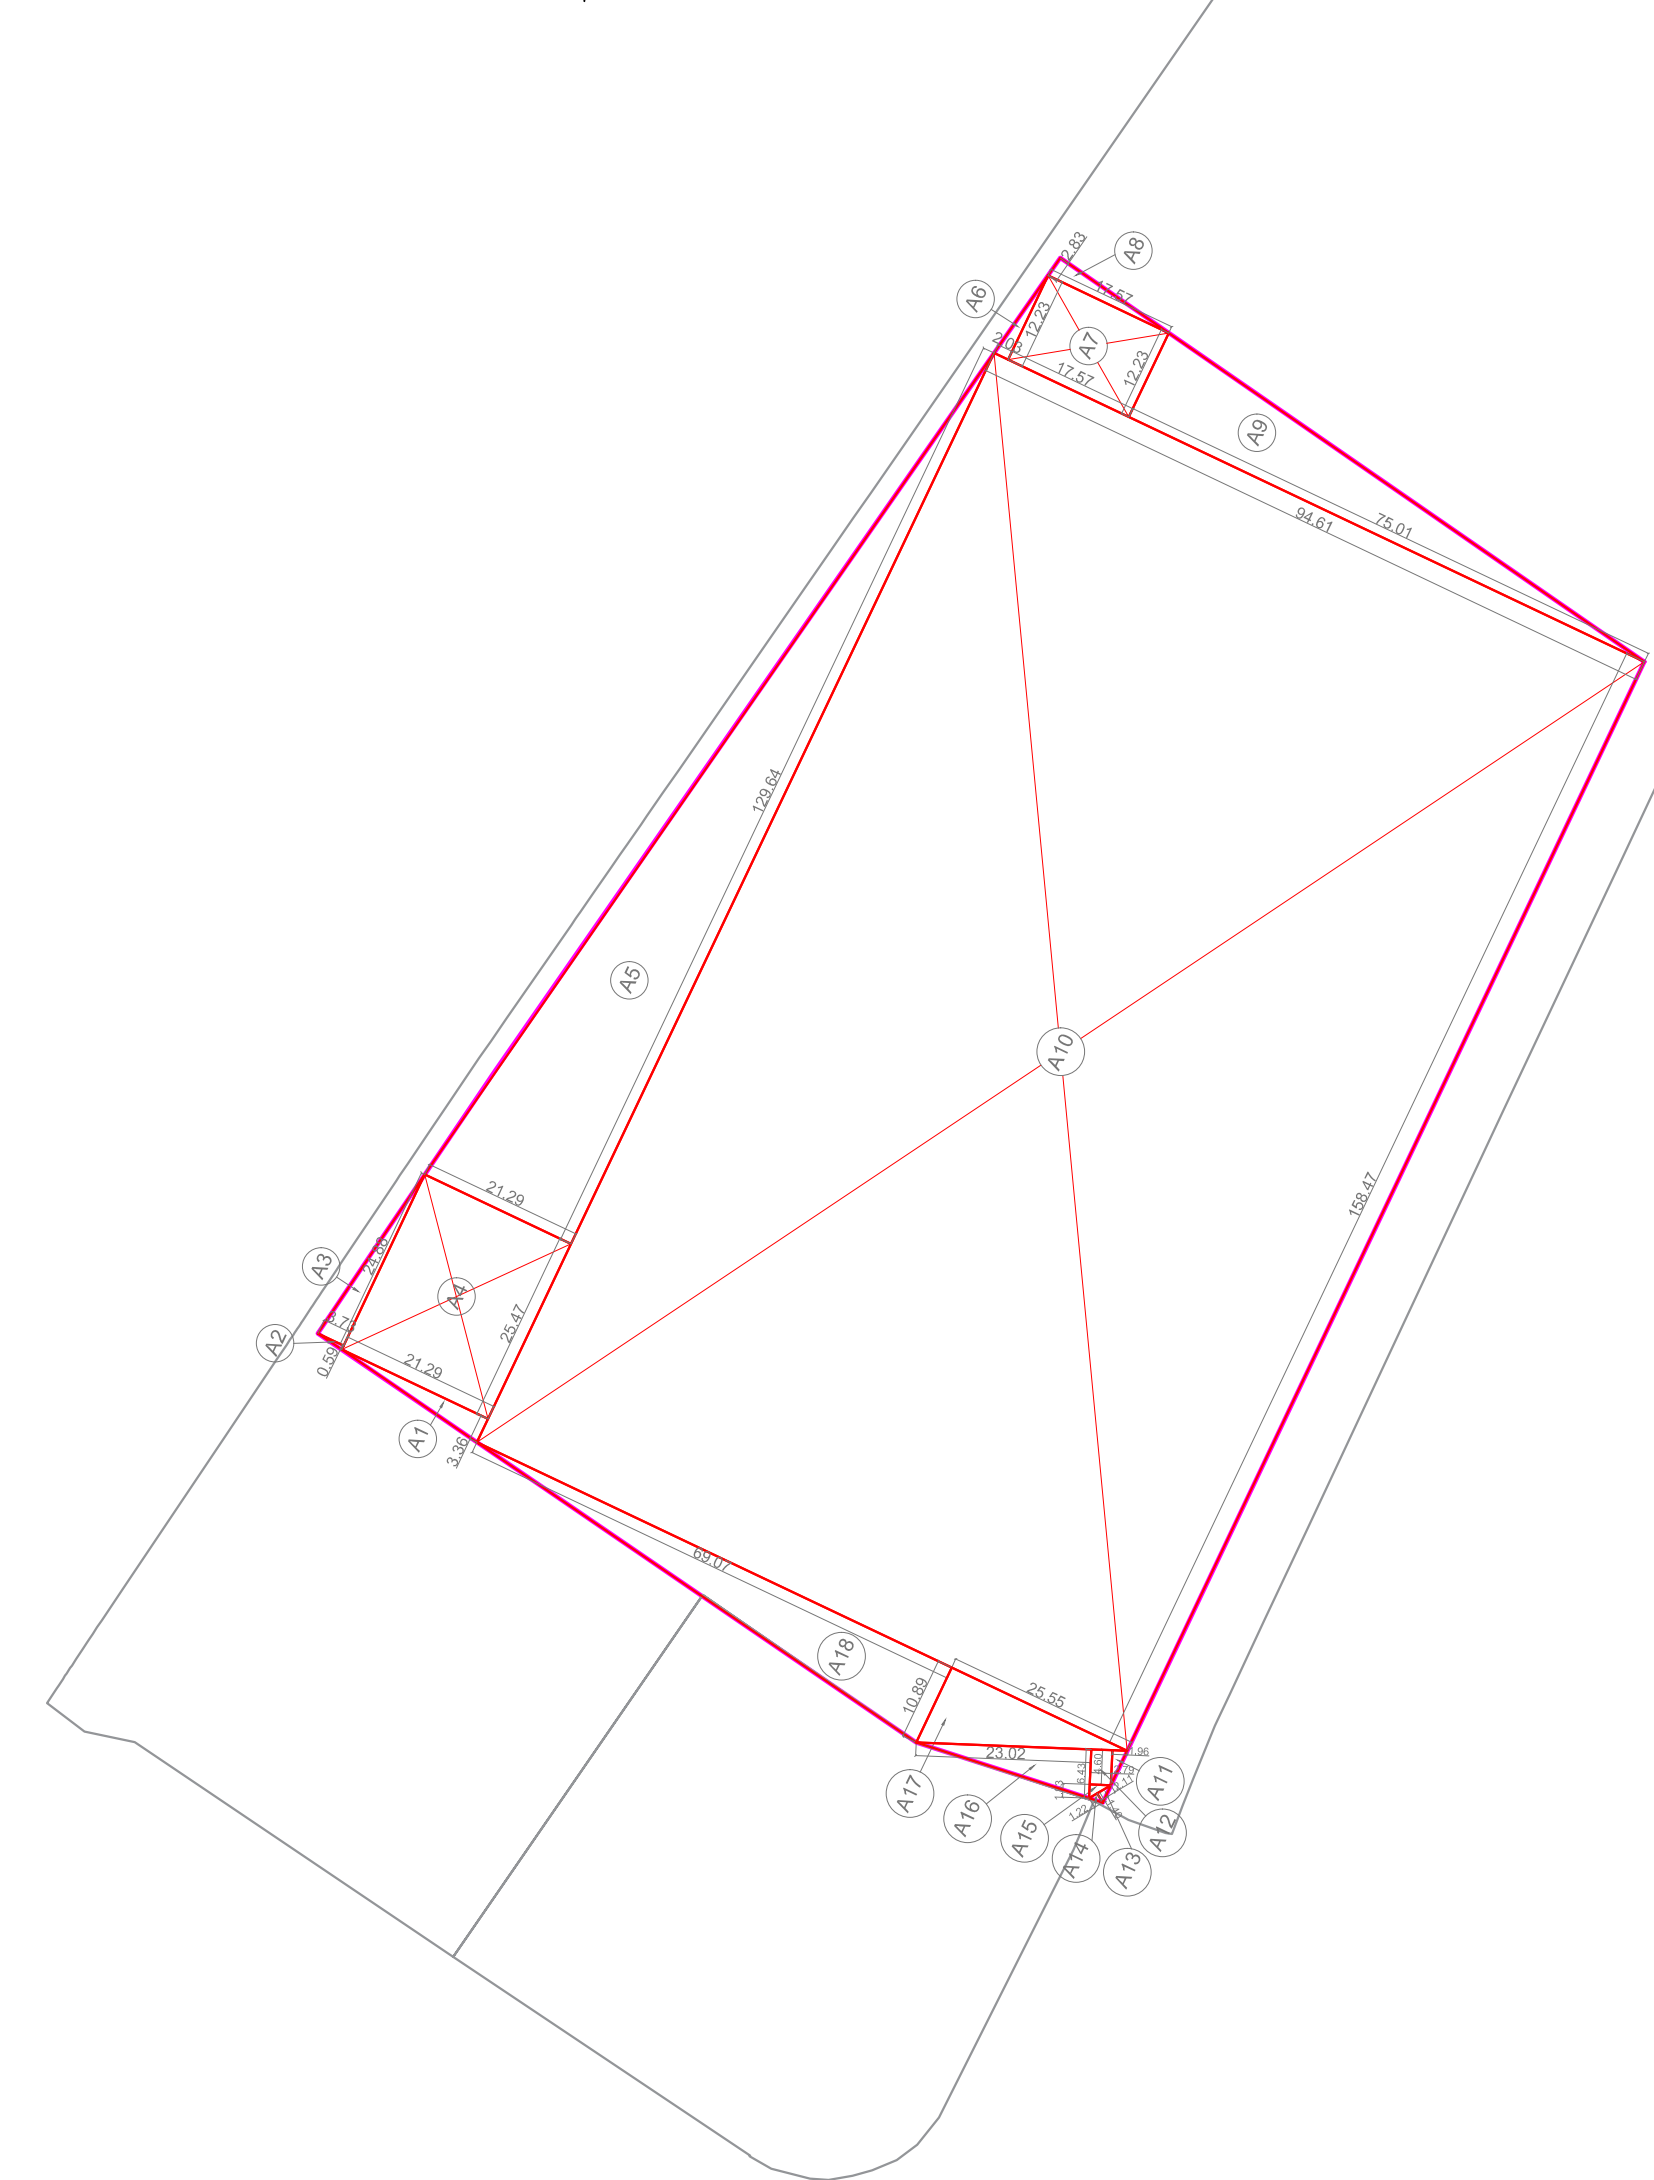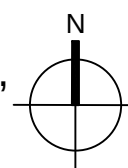

PODIUM LEVEL CALCULATION				
DESCRIPTION	DIMENSION (IN METERS)			AREA (IN)
	FACTOR	BASE	HEIGHT	
A1	0.5	3.36	21.29	35.767
A2	0.5	0.59	3.73	1.1004
A3	0.5	3.73	24.88	46.401
A4	1	21.29	25.47	542.26
A5	0.5	21.29	129.64	1380
A6	0.5	2.03	12.23	12.413
A7	1	17.51	12.23	214.88
A8	0.5	2.83	17.57	24.862
A9	0.5	12.23	75.01	458.69
A10	1	158.47	34.61	14933
A11	0.5	1.96	4.6	4.508
A12	1	2.79	4.6	12.834
A13	0.5	1.4	2.11	1.477
A14	0.5	1.22	1.4	0.854
A15	0.5	1.83	2.79	2.5529
A16	0.5	6.43	23.02	74.009
A17	0.5	10.89	25.55	139.12
A18	0.5	10.89	63.07	376.09
TOTAL AREA				18320.7
TOTAL AREA PER PODIUM LEVEL				18320.7 SQ.M
TOTAL AREA OF 3 PODIUM LEVELS				54962.1 SQ.M

PARKING REQUIREMENT		
BUILDINGS	TWO WHEELER	FOUR WHEELER
BUILDING 2	132	66
BUILDING 3	220	110
BUILDING 4	220	110
BUILDING 5	143	72
BUILDING 6	176	88
BUILDING 7	143	72
TOTAL PARKING	1034	518
PODIUM PARKING PROPOSED		
PODIUM	TWO WHEELER	FOUR WHEELER
P1	382	132
P2	387	234
P3	387	234
TOTAL PARKING	1156	600

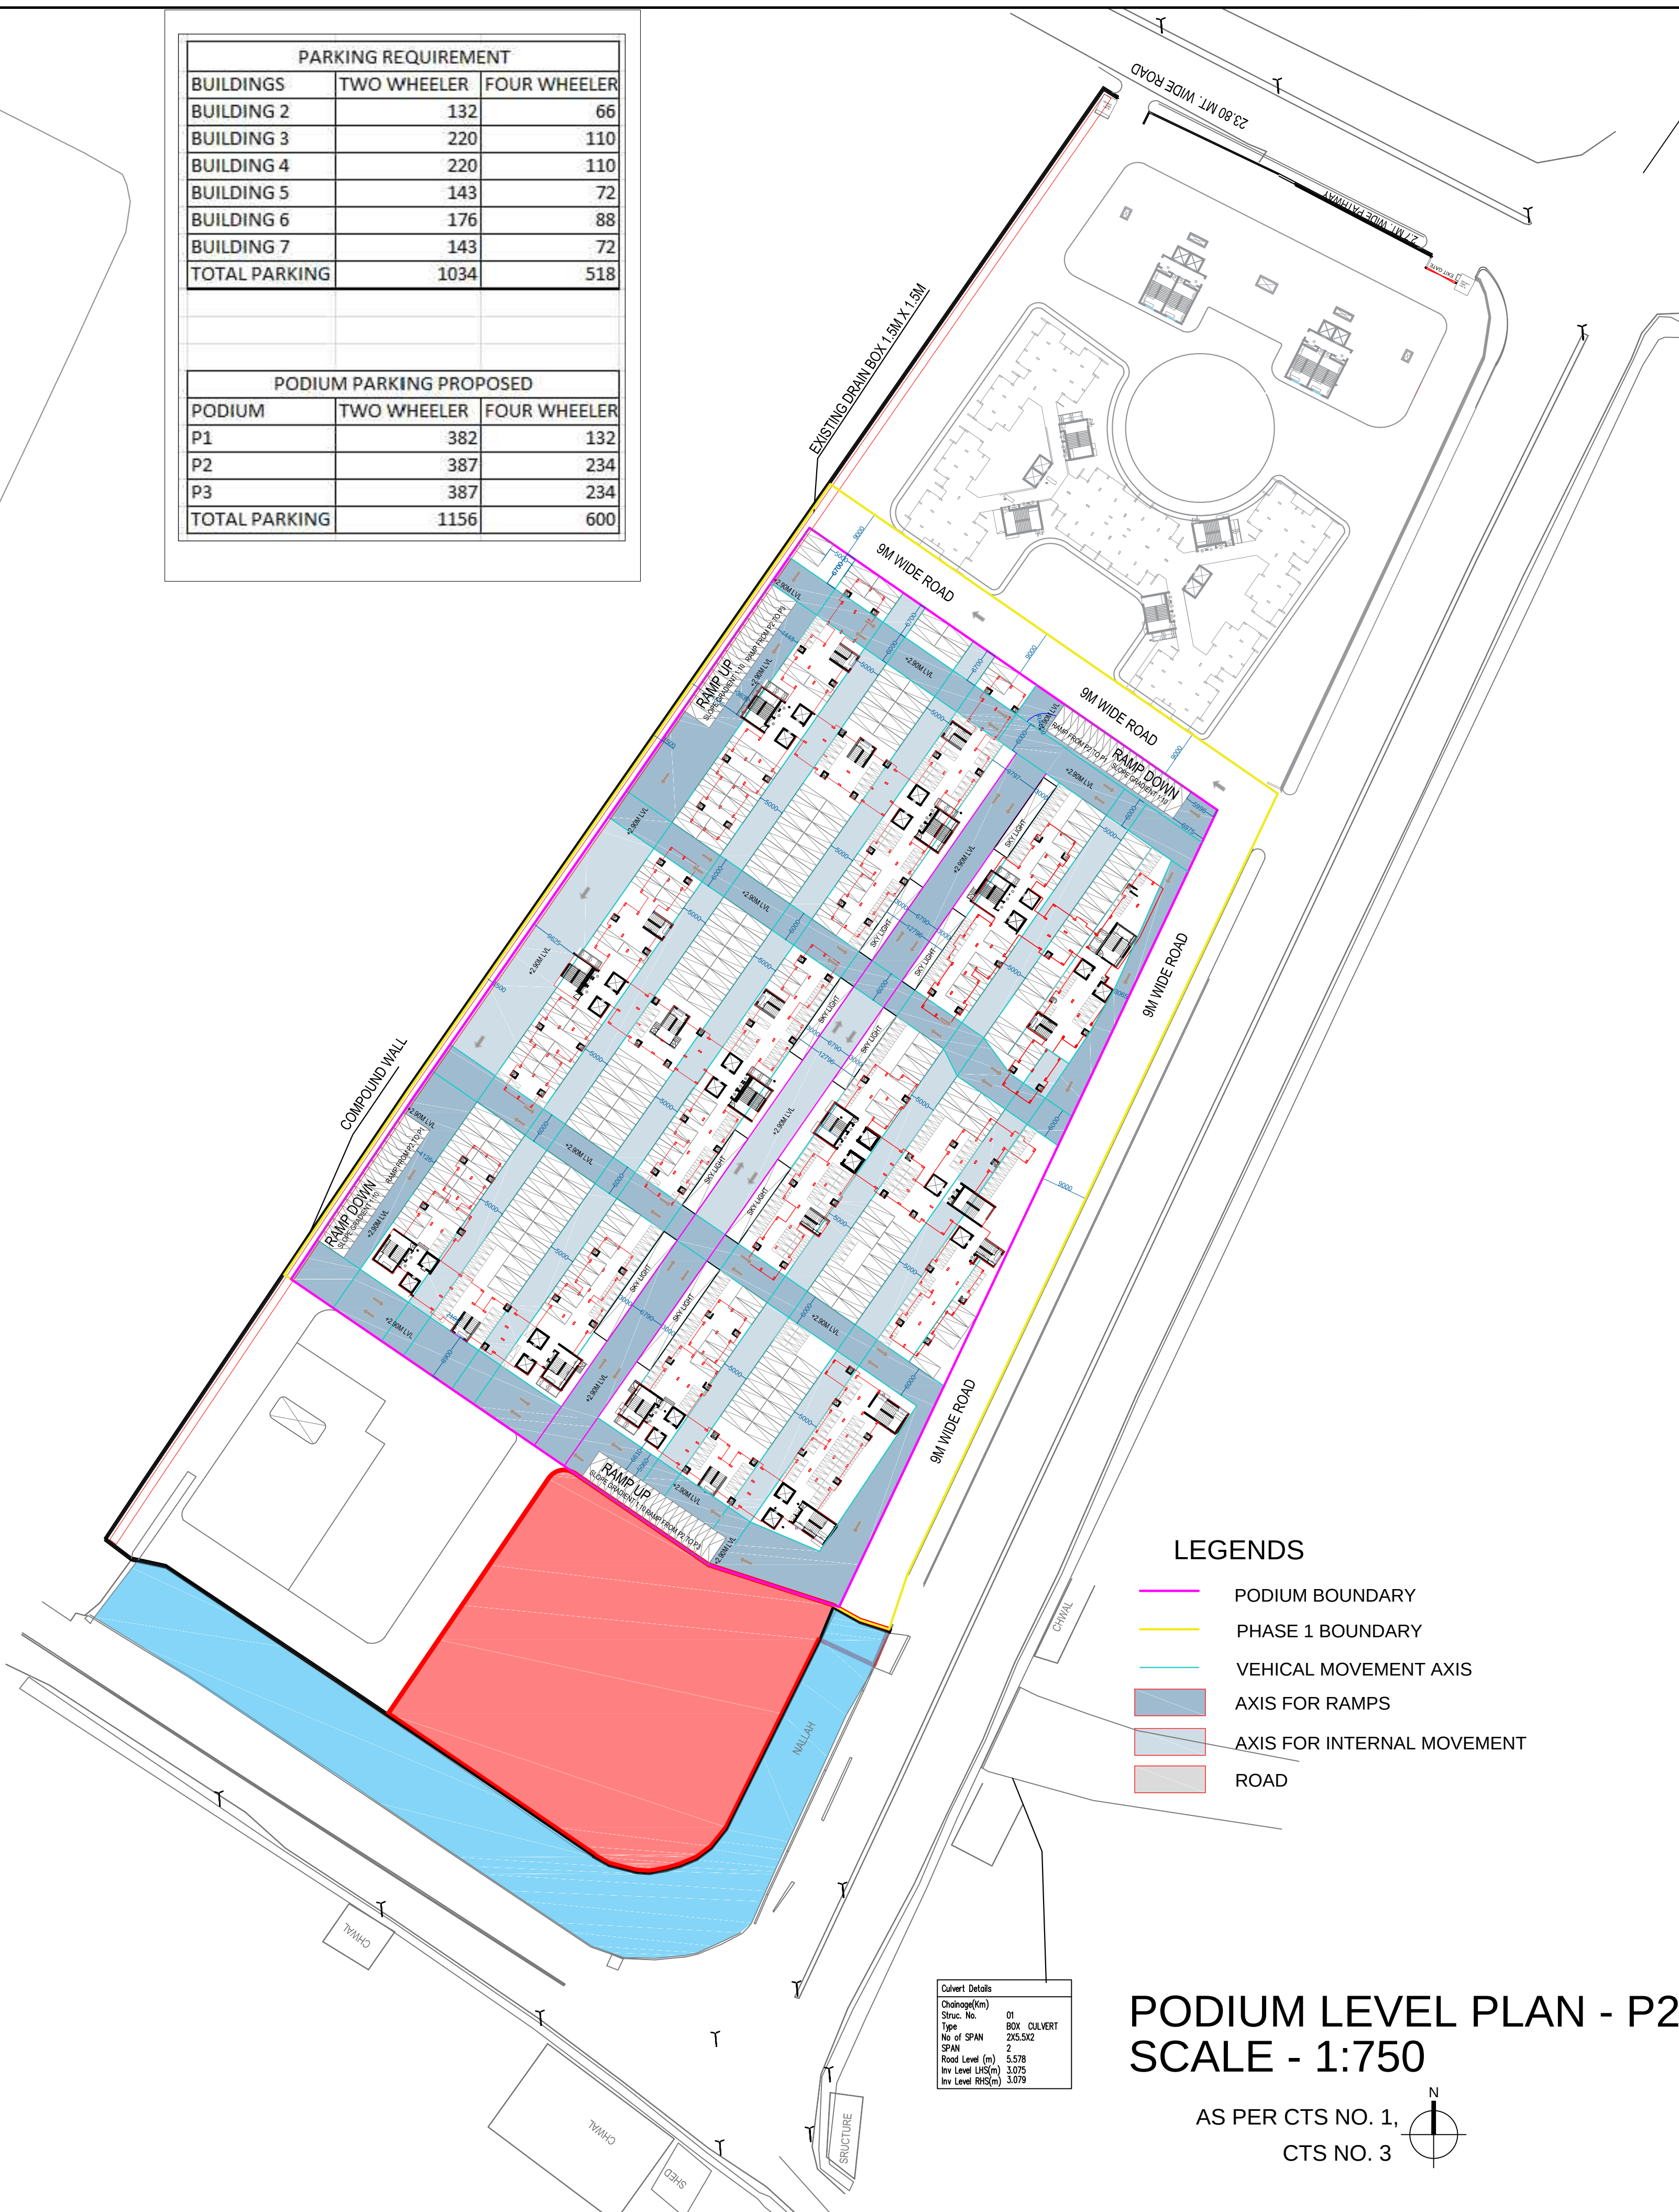


LEGENDS

- PODIUM BOUNDARY
- PHASE 1 BOUNDARY
- VEHICAL MOVEMENT AXIS
- AXIS FOR RAMP
- AXIS FOR INTERNAL MOVEMENT
- ROAD

PODIUM LEVEL PLAN - P2
SCALE - 1:750

AS PER CTS NO. 1,
CTS NO. 3

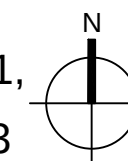

SHEET NO :

LOCATION PLAN SCALE 1:4000

CONTENT OF SHEET :

LOCATION PLAN, GIS PLAN, DP PLAN
BLOCK PLAN
STILT FLOOR PLAN
AREA, WATER AND PARKING CALCULATIONS

SITE

NALLAH

COLOURING OF PLANS AS PER DCPR-34

THICK BLACK PLOT BOUNDARY	RED DOTTED DRAINAGE AND SEWERAGE WORK
GREEN EXISTING STREET	BLUE DOTTED THIN WATER SUPPLY
GREEN DOTTED FUTURE STREET	RED HATCHED DEVIATIONS
THICK BLACK DOTTED PERM. BLDG	GREEN WASH RECREATION GROUND
NO COLOUR OPEN SPACES	BURNT SIENNA ROADS & SETBACKS
YELLOW HATCHED DEMOLISHED WORK	APPROPRIATE COLOUR CODE RESERVATIONS
RED FILLED PROPOSED WORK	

CERTIFICATE

"THIS IS TO CERTIFY THAT THE SCOPE OF WORK HAS BEEN EXPLAINED TO ME BY THE ARCHITECT / CONSULTANT AND CONSIDERING THE BUDGET PROVISION THEREFORE I AM SATISFIED WITH THE PROJECT PROPOSAL."

NOTE : USER SIGNATURE IS PROVIDED IN THE SCANNED COPY OF THE PLANS AND HENCE IT IS REQUESTED THAT THE SAME IS NOT INSISTED ON DIGITAL PRINTS, IN CASE REQUIRED, THE SAME WILL BE OBTAINED BEFORE STARTING OF THE WORK.

ARCHITECT MASTER & ASSOCIATES

MUNICIPAL ARCHITECT

R1	08-08-2022	AREA STATEMENT REVISED	URVASHI
R2	03-08-2022	PODIUM PARKING LAYOUT	URVASHI

FILE PATH :
PC NO. 11 D:\Drawings\MILONI\1896- 600 TENEMENTS,
DEONAR
TYPE OF DWG :
APPROVAL DRAWING
CLIENT:
MUNICIPAL CORPORATION OF GREATER MUMBAI (MCGM)
TITLE OF DRAWING PODIUM LEVEL PLAN - P2

PROPOSED REDEVELOPMENT ON OPEN PLOT,
KNOWN AS '600 TENEMENTS PLOT BEARING CTS NO. 1(PT) &
CTS NO. 3(PT) OF VILLAGE DEONAR IN M/EAST WARD IN MUMBAI
JOB TITLE :

DRAWN BY : URVASHI

CHECKED BY : UDM

SCALE: AS MENTIONED

DATE : 1.08.2022

PROJECT CODE: 1896

DRAWING NO: 1896-509

REVISION NO: R1

THIS DRAWING IS THE PROPERTY OF
MASTER & ASSOCIATES
ARCHITECTS, INTERIOR DESIGNERS &
PROJECT MANAGEMENT CONSULTANTS

AND IS NOT TO BE REPRODUCED, COPIED HANDED
OVER TO A THIRD PARTY OR USED FOR ANY PURPOSE
OTHER THAN FOR WHICH IT HAS BEEN LOANED

STATUS



MASTER & ASSOCIATES
ARCHITECTS, INTERIOR DESIGNERS &
PROJECT MANAGEMENT CONSULTANTS

MUMBAI
HARANI HOUSE 2B 3B HARANI, DODHI MARG,
MUMBAI - 400 001, INDIA.
PHONE NO +91 22 225 4858 / 4756 FAX 22700273
EMAIL ADD : masterandassociates@gmail.com
info@masterandassociates.com

ALGERES
SIKANE ABDELAZIZ CITE 18 LOGEMENTS BLOC - B1 N°3,
CITE DE REHMANIA, ZERALEKA ALGERES.
PHONE NO 0033 03 20 51 51 51
EMAIL ADD : info@masterandassociates.com
MOBILE : 333 9397666

PODIUM AREA DIAGRAM
SCALE - 1:1000


AS PER CTS NO. 1,
CTS NO. 3

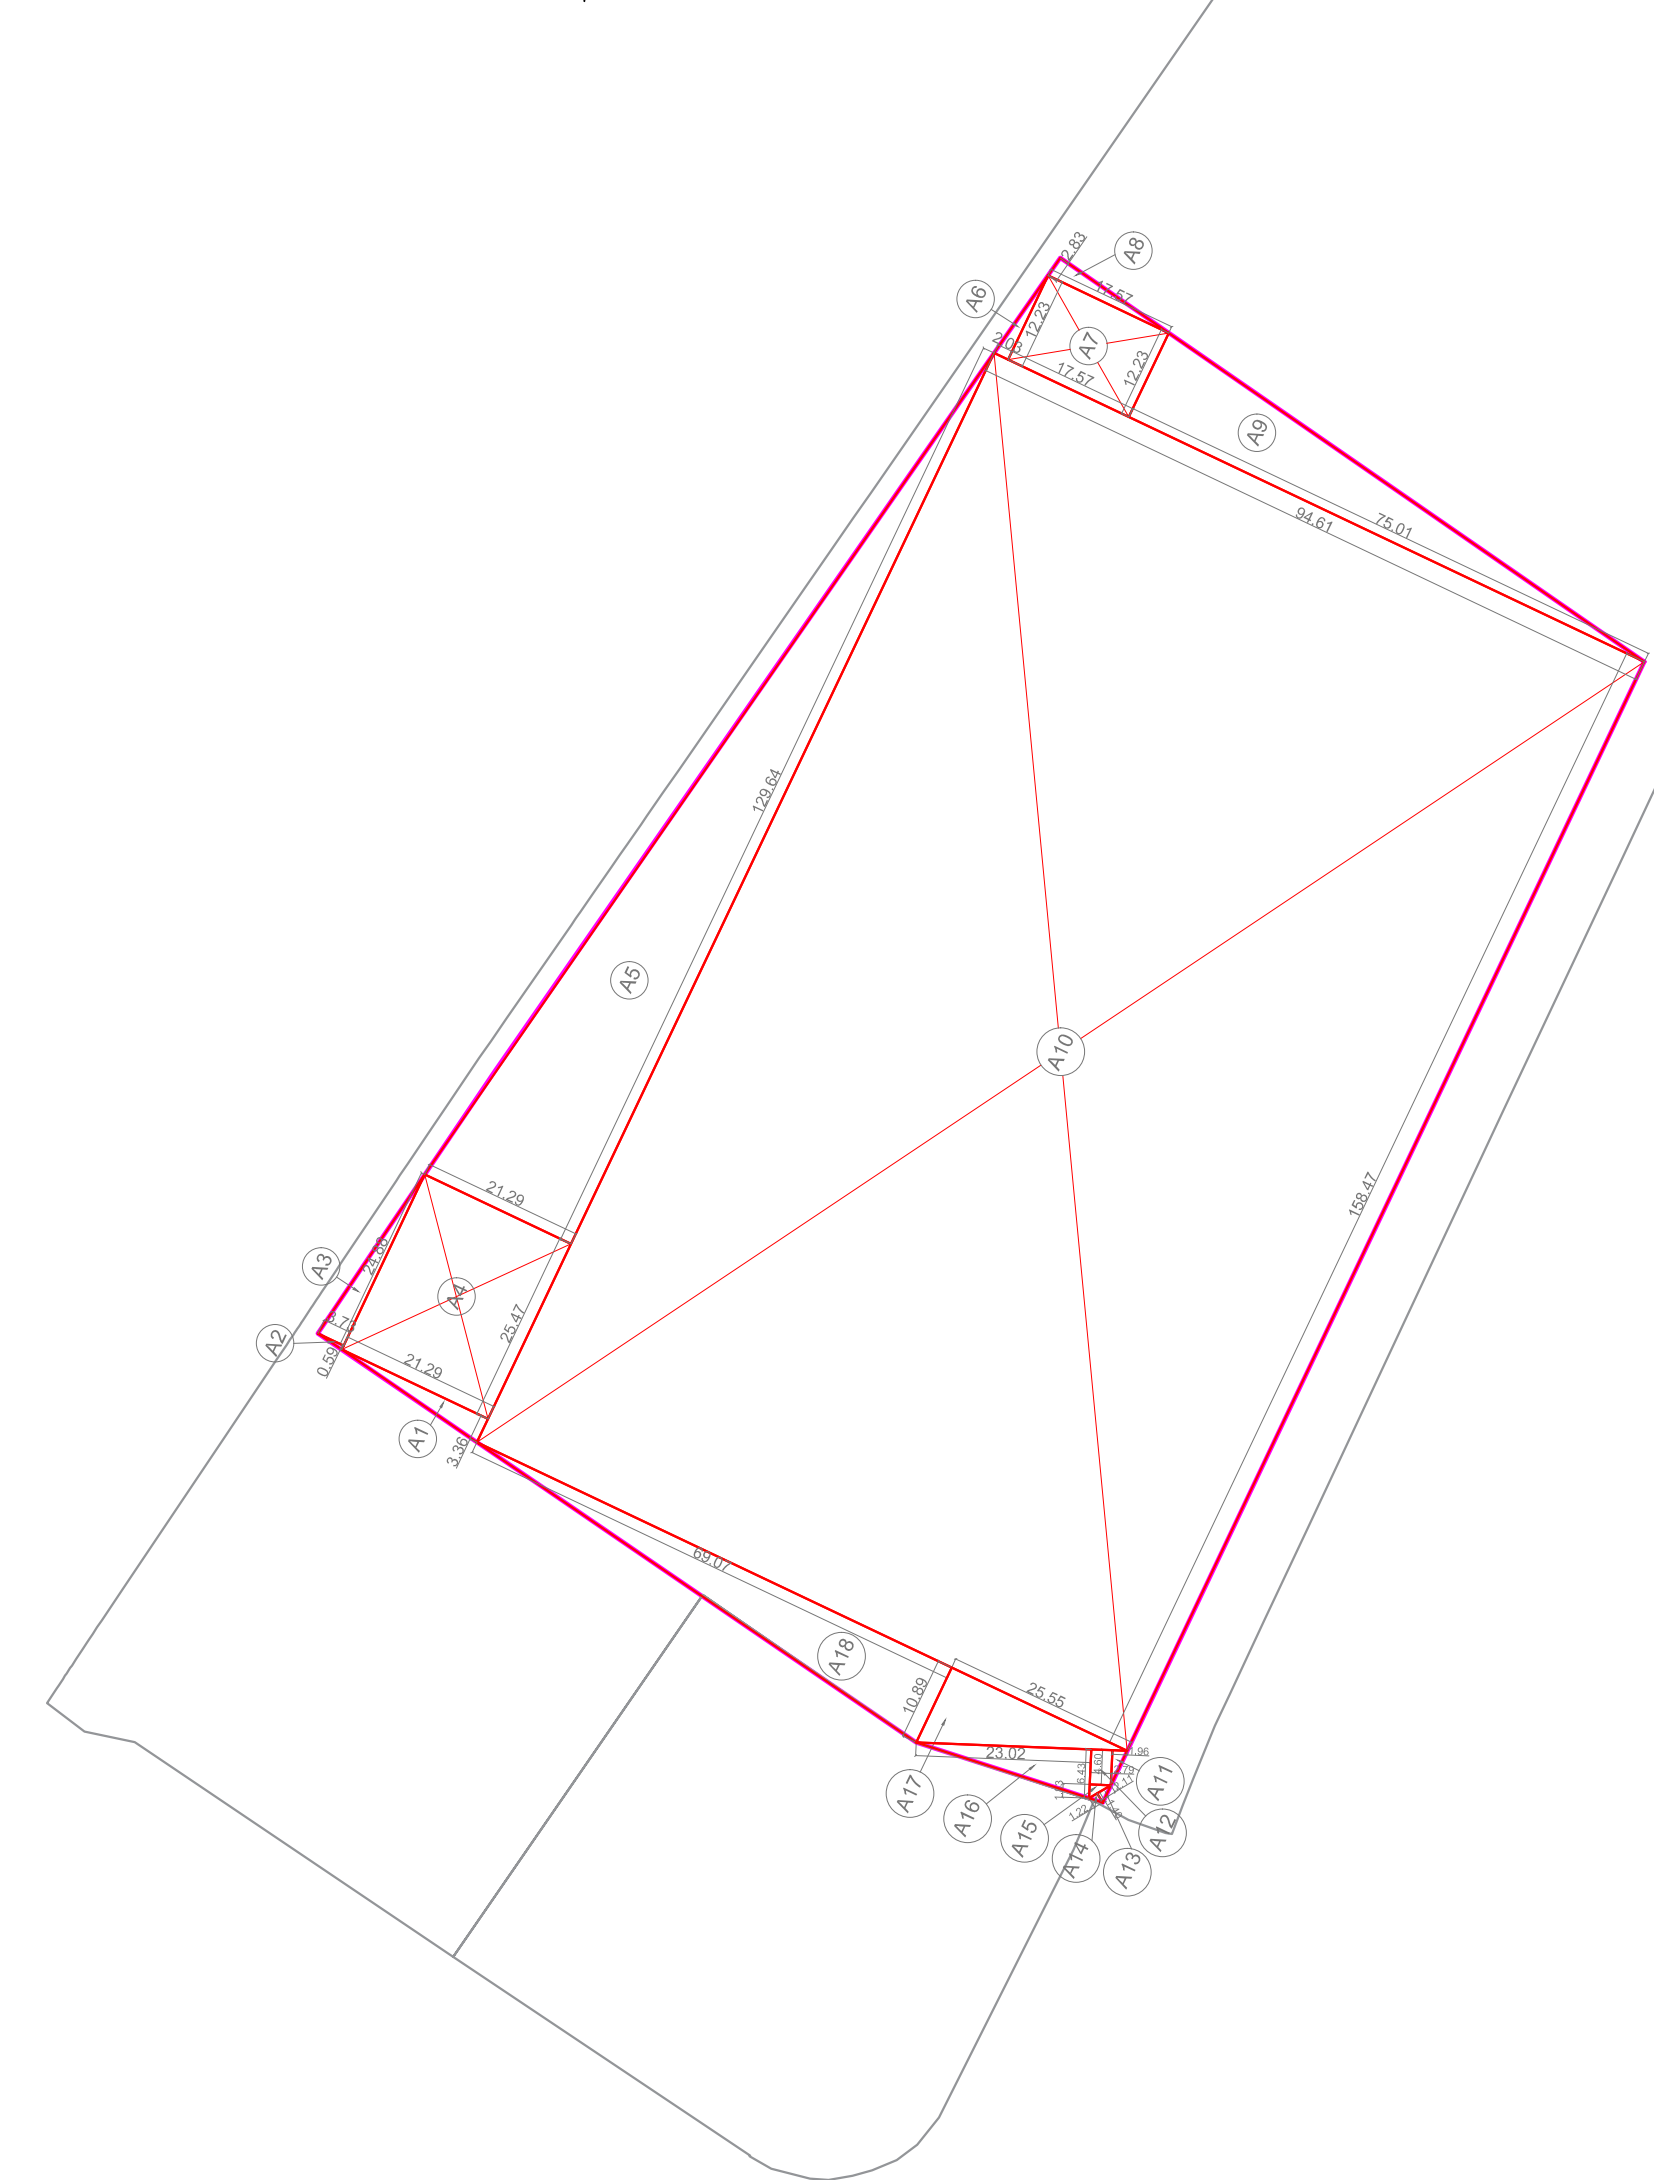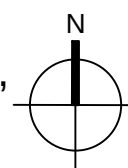

PODIUM LEVEL CALCULATION				
DESCRIPTION	DIMENSION (IN METERS)			AREA (IN)
	FACTOR	BASE	HEIGHT	
A1	0.5	3.36	21.23	35.767
A2	0.5	0.53	3.73	1.1004
A3	0.5	3.73	24.88	46.401
A4	1	21.23	25.47	542.26
A5	0.5	21.23	123.64	1380
A6	0.5	2.03	12.23	12.413
A7	1	17.57	12.23	214.88
A8	0.5	2.83	17.57	24.862
A9	0.5	12.23	75.01	458.63
A10	1	158.47	34.61	14333
A11	0.5	1.96	4.6	4.508
A12	1	2.73	4.6	12.834
A13	0.5	1.4	2.11	1.477
A14	0.5	1.22	1.4	0.854
A15	0.5	1.83	2.73	2.5529
A16	0.5	6.43	23.02	74.009
A17	0.5	10.83	25.55	133.12
A18	0.5	10.83	69.07	376.09
TOTAL AREA				18320.7
TOTAL AREA PER PODIUM LEVEL				18320.7 SQ.M
TOTAL AREA OF 3 PODIUM LEVELS				54962.1 SQ.M

PARKING REQUIREMENT		
BUILDINGS	TWO WHEELER	FOUR WHEELER
BUILDING 2	132	66
BUILDING 3	220	110
BUILDING 4	220	110
BUILDING 5	143	72
BUILDING 6	176	88
BUILDING 7	143	72
TOTAL PARKING	1034	518

PODIUM PARKING PROPOSED		
PODIUM	TWO WHEELER	FOUR WHEELER
P1	382	132
P2	387	234
P3	387	234
TOTAL PARKING	1156	600

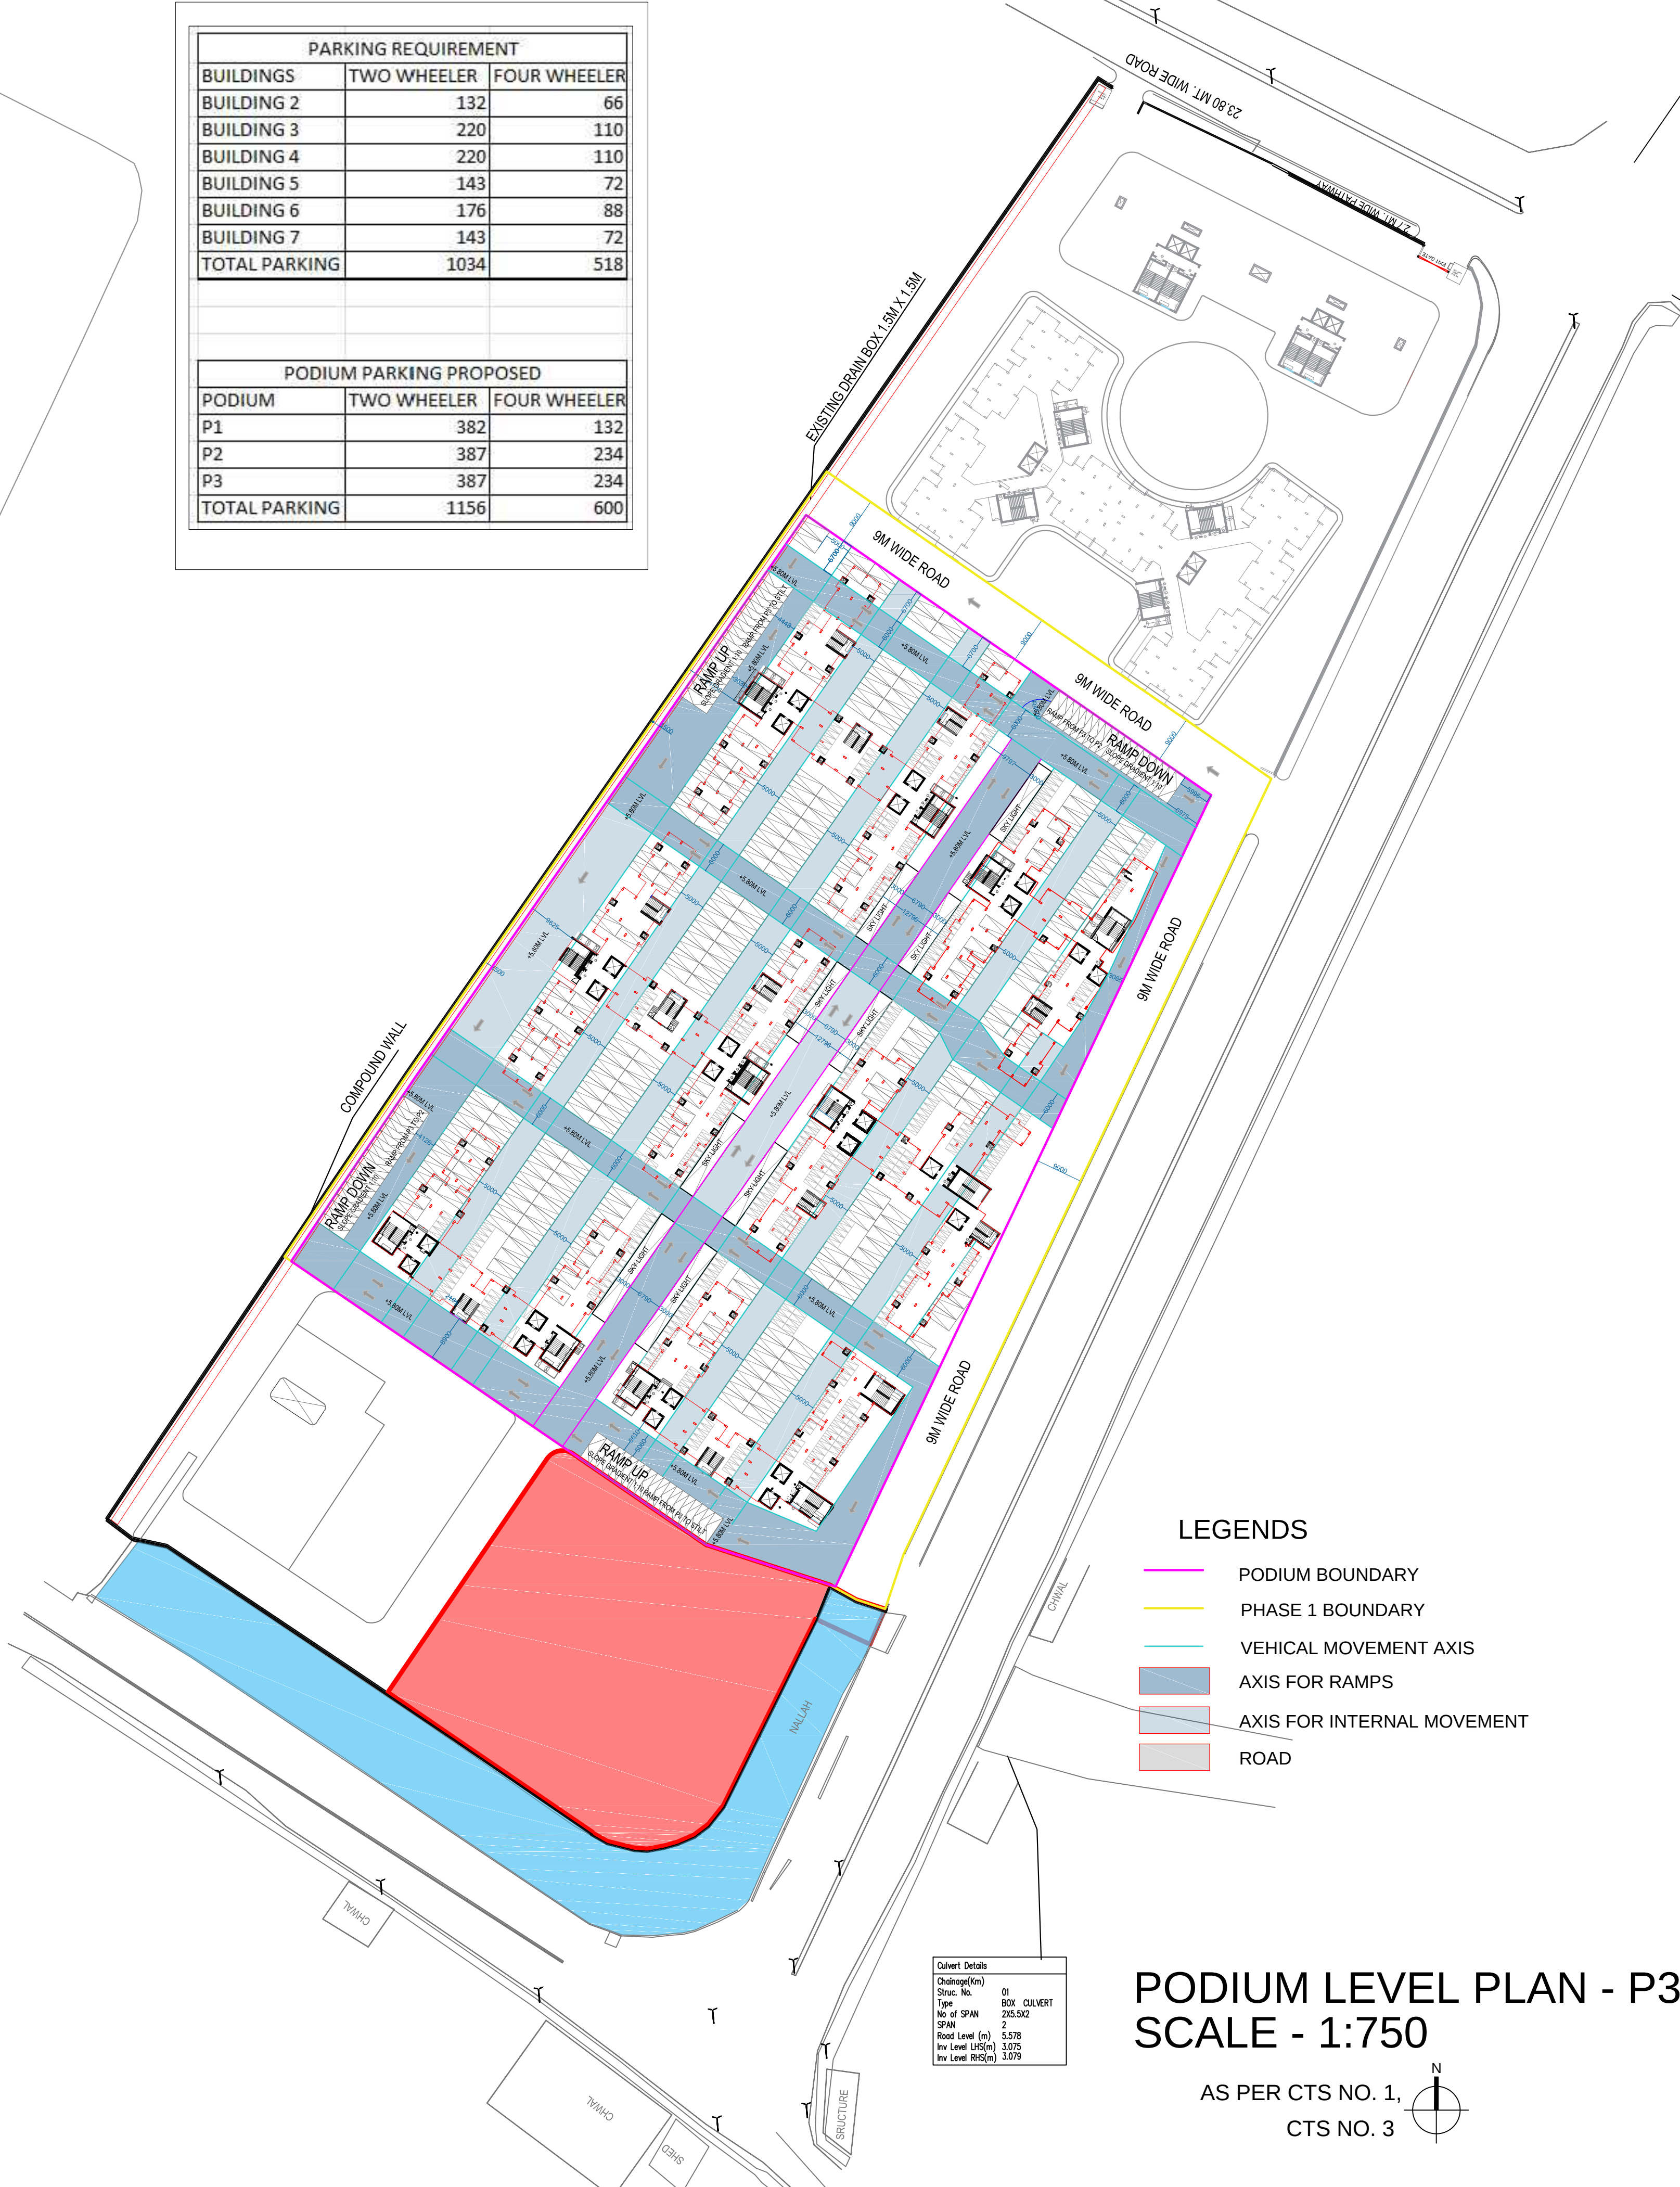


LEGENDS

- PODIUM BOUNDARY
- PHASE 1 BOUNDARY
- VEHICAL MOVEMENT AXIS
- AXIS FOR RAMP
- AXIS FOR INTERNAL MOVEMENT
- ROAD

Culvert Details	
Drainage (mm)	01
Span No.	BOX CULVERT
Type	25.502
No. of SPAN	2
Span	
Road Level (m)	5.578
Inv Level (LHS) (m)	3.02
Inv Level (RHS) (m)	3.079

PODIUM LEVEL PLAN - P3
SCALE - 1:750

AS PER CTS NO. 1,
CTS NO. 3

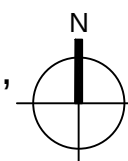

SHEET NO :

LOCATION PLAN SCALE 1:4000

CONTENT OF SHEET :

LOCATION PLAN, GIS PLAN, DP PLAN
BLOCK PLAN
STILT FLOOR PLAN
AREA, WATER AND PARKING CALCULATIONS

SITE

NALLAH

COLOURING OF PLANS AS PER DCPR-34

THICK BLACK PLOT BOUNDARY	RED DOTTED DRAINAGE & SEWERAGE WORK
GREEN EXISTING STREET	BLUE DOTTED THIN WATER SUPPLY
GREEN DOTTED FUTURE STREET	RED HATCHED DEVIATIONS
THICK BLACK DOTTED PERM. BLDG	GREEN WASH RECREATION GROUND
NO COLOUR OPEN SPACES	BURNT SIENNA ROADS & SETBACKS
YELLOW HATCHED DEMOLISHED WORK	APPROPRIATE COLOUR CODE RESERVATIONS
RED FILLED PROPOSED WORK	

CERTIFICATE

"THIS IS TO CERTIFY THAT THE SCOPE OF WORK HAS BEEN EXPLAINED TO ME BY THE ARCHITECT / CONSULTANT AND CONSIDERING THE BUDGET PROVISION THEREFORE I AM SATISFIED WITH THE PROJECT PROPOSAL."

NOTE : USER SIGNATURE IS PROVIDED IN THE SCANNED COPY OF THE PLANS AND HENCE IT IS REQUESTED THAT THE SAME IS NOT INSISTED ON DIGITAL PRINTS, IN CASE REQUIRED, THE SAME WILL BE OBTAINED BEFORE STARTING OF THE WORK.

ARCHITECT MASTER & ASSOCIATES

MUNICIPAL ARCHITECT

R1	08-08-2022	AREA STATEMENT REVISED	URVASHI
R2	03-08-2022	PODIUM PARKING LAYOUT	URVASHI

FILE PATH :
PC NO. 11 D:\Drawings\MILONI\1896- 600 TENEMENTS, DEONAR
TYPE OF DWG :
APPROVAL DRAWING
CLIENT:
MUNICIPAL CORPORATION OF GREATER MUMBAI (MCGM)
TITLE OF DRAWING PODIUM LEVEL PLAN - P3

PROPOSED REDEVELOPMENT ON OPEN PLOT, KNOWN AS '600 TENEMENTS PLOT BEARING CTS NO. 1(PT) & CTS NO. 3(PT) OF VILLAGE DEONAR IN M/EAST WARD IN MUMBAI JOB TITLE :

DRAWN BY : URVASHI

CHECKED BY : UDM

SCALE: AS MENTIONED

DATE : 1.08.2022

PROJECT CODE: 1896

DRAWING NO: 1896-510

REVISION NO: R1

THIS DRAWING IS THE PROPERTY OF
MASTER & ASSOCIATES
ARCHITECTS, INTERIOR DESIGNERS &
PROJECT MANAGEMENT CONSULTANTS


AND IS NOT TO BE REPRODUCED, COPIED HANDED
OVER TO A THIRD PARTY OR USED FOR ANY PURPOSE
OTHER THAN FOR WHICH IT HAS BEEN LOANED

STATUS

MASTER & ASSOCIATES
ARCHITECTS, INTERIOR DESIGNERS &
PROJECT MANAGEMENT CONSULTANTS

MUMBAI
HARANI HOUSE 2B 3B HARANI, DODI MARG,
MUMBAI - 400 001, INDIA.
PHONE NO +91 22 225 488 4756 FAX 22700712
EMAIL ADD : masterandassociates@gmail.com
info@masterandassociates.com

ALGERIES
SUARANE ABD ELAZIZ CITE 18 LOGEMENTS BLOC - B1 N°3,
CITE DE REHMANIA, ZERALEKA ALGERIES.
PHONE NO 0033 078 5757554
EMAIL ADD : info@masterandassociates.com
MOBILE : 333 9339766

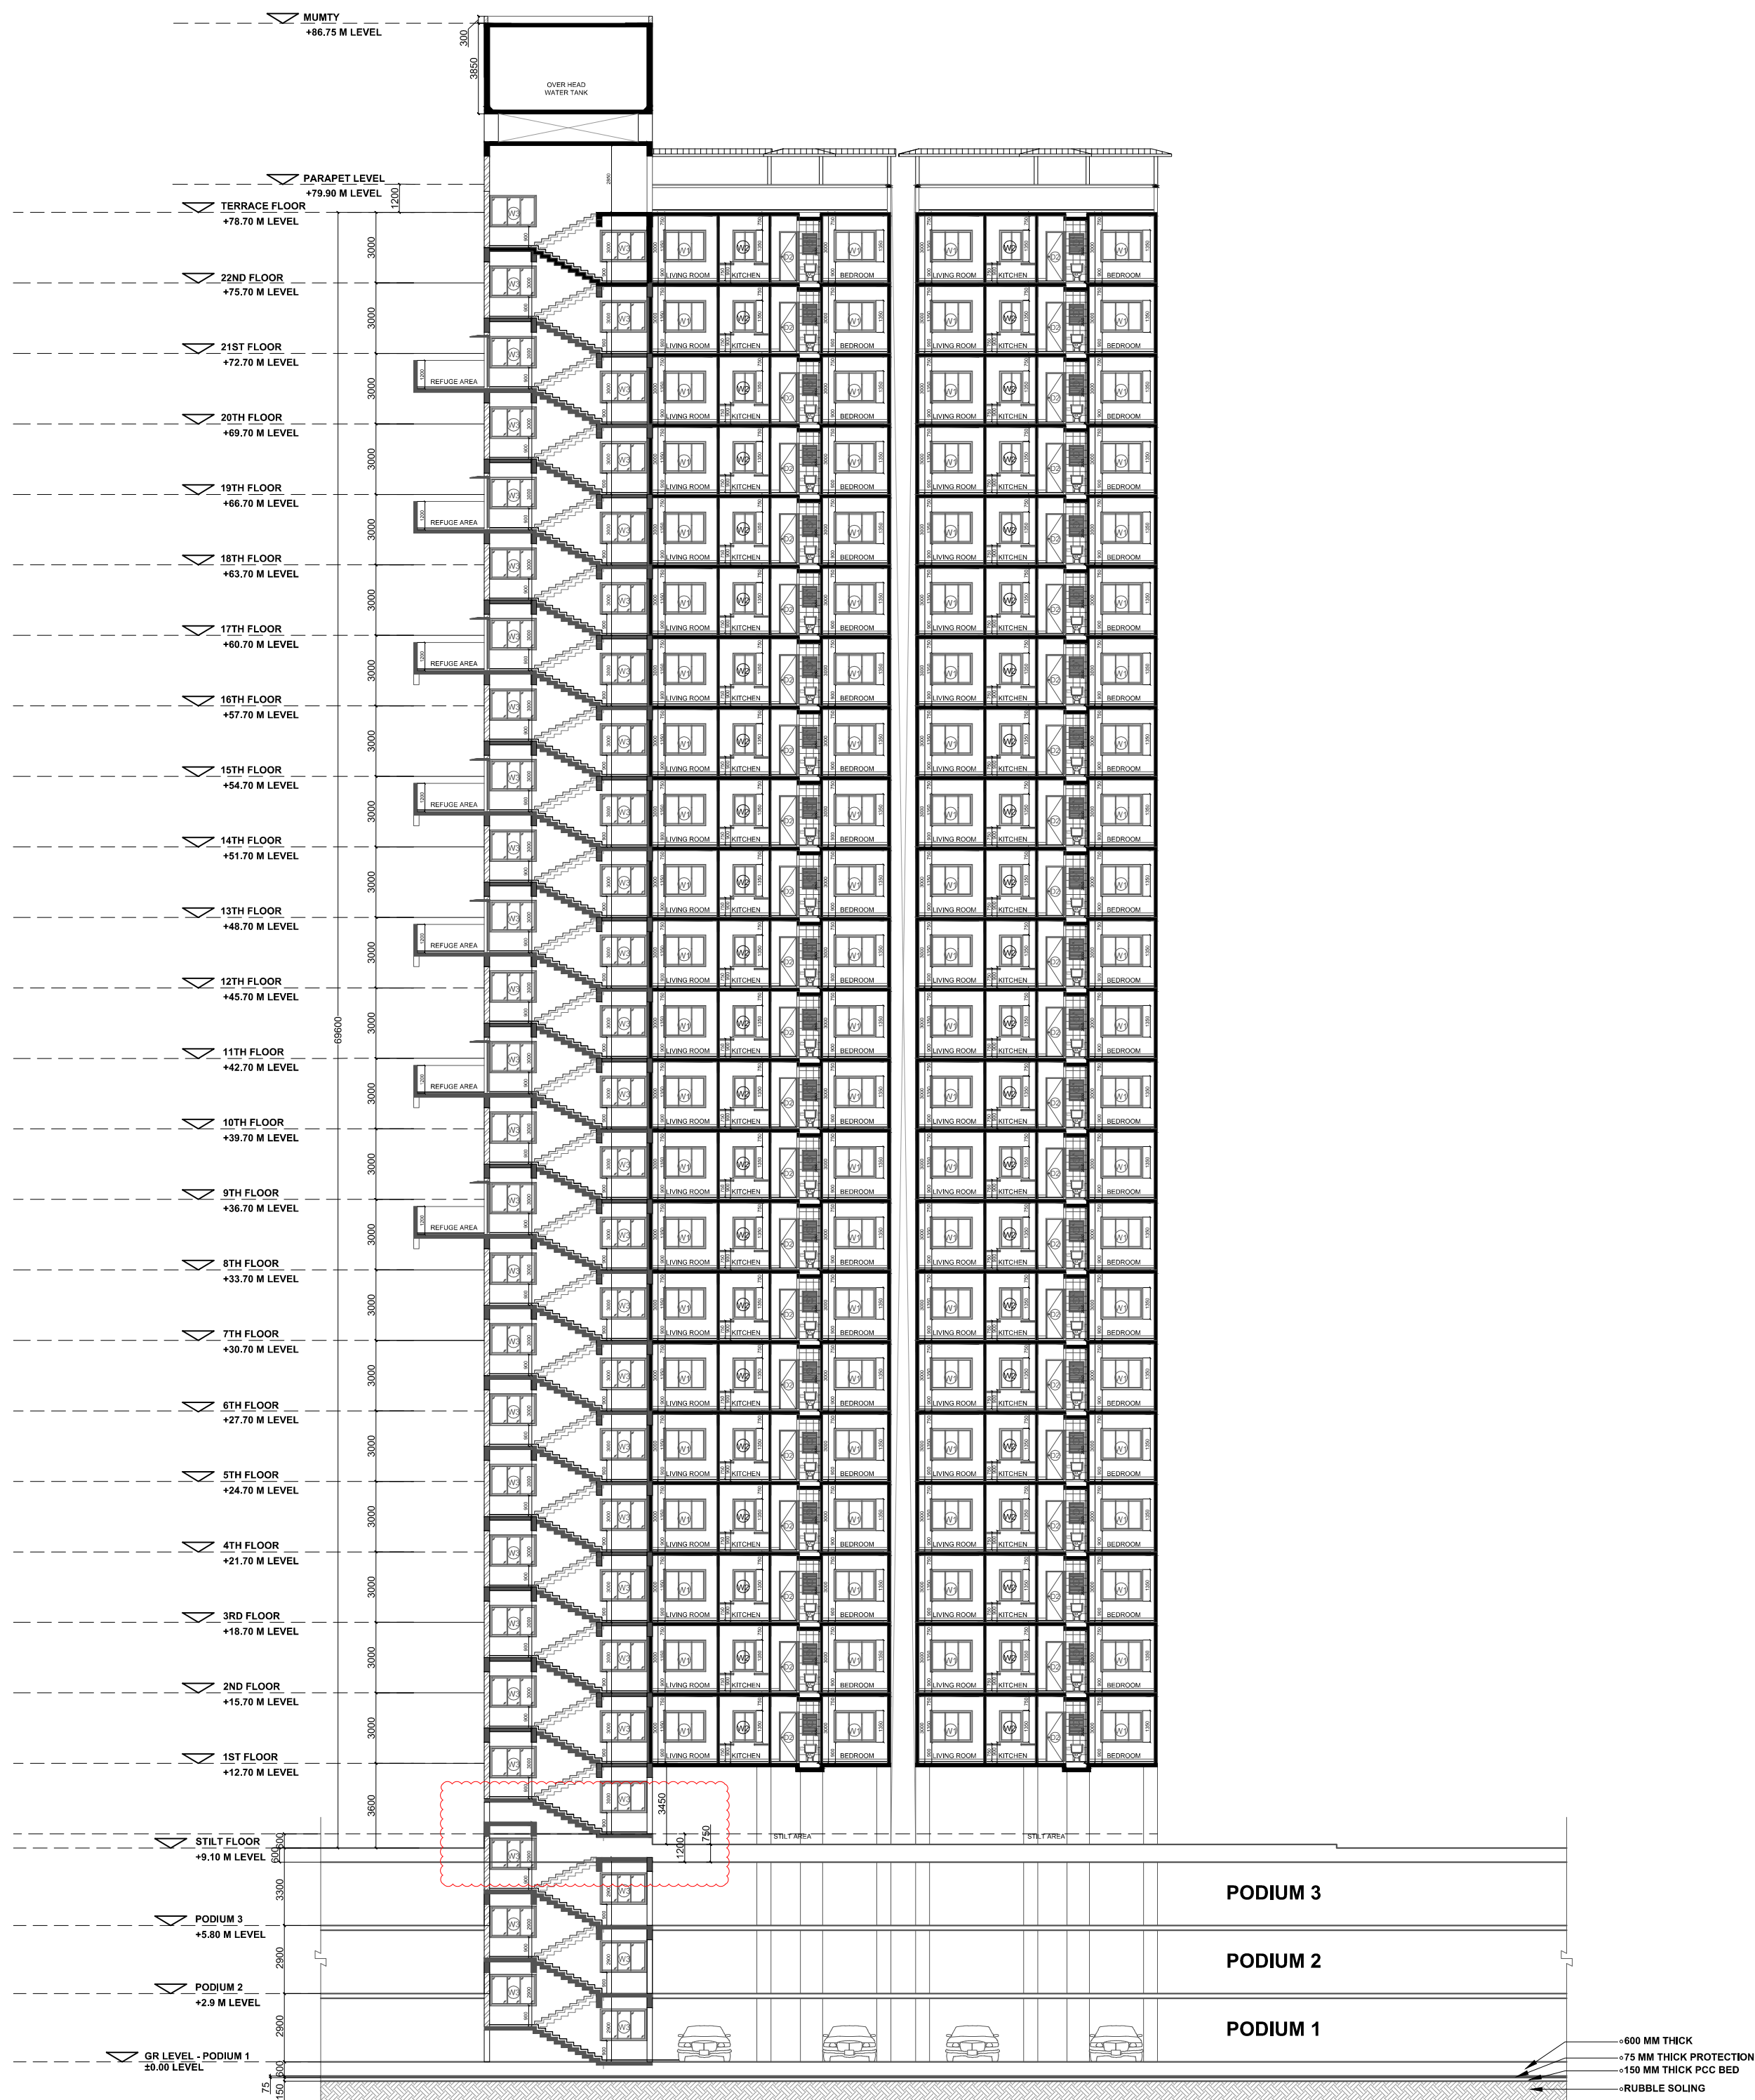

SECTION - BB'

SECTION B-B'
SCALE 1:100


COLOURING OF PLANS AS PER DCPR-34

THICK BLACK PLOT BOUNDARY	RED DOTTED DRAINAGE & SEWERAGE WORK
GREEN EXISTING STREET	BLUE DOTTED THIN WATER SUPPLY
GREEN DOTTED FUTURE STREET	RED HATCHED DEVIATIONS
THICK BLACK DOTTED PERM. BLDG	GREEN WASH RECREATION GROUND
NO COLOUR OPEN SPACES	BURNT SIENNA ROADS & SETBACKS
YELLOW HATCHED DEMOLISHED WORK	APPROPRIATE COLOUR CODE RESERVATIONS
RED FILLED PROPOSED WORK	

THIS DRAWING IS THE PROPERTY OF
MASTER & ASSOCIATES, ARCHITECTS, INTERIOR DESIGNERS &
PROJECT MANAGEMENT CONSULTANTS
AND IS NOT TO BE REPRODUCED, COPIED, HANDED OVER
TO A THIRD PARTY OR USED FOR ANY PURPOSE OTHER
THAN THAT FOR WHICH IT HAS BEEN LOANED

STATUS


BUILDING 02 - SHEET NO : 04 OF 06

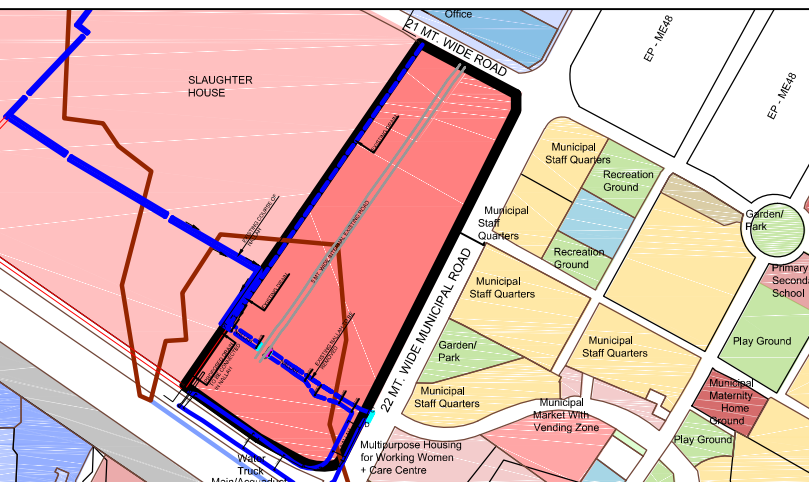

LOCATION PLAN SCALE 1:4000

CONTENT OF SHEET :
SECTION B-B'
SECTION C-C'

KEY PLAN SCALE 1:500

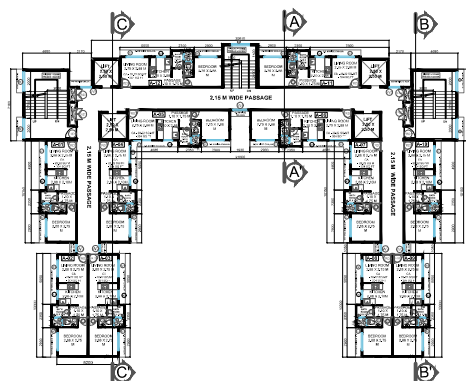

AD-FO

D-FO

DY-CFO

SE-BP

AE-BP

EE-BP

CERTIFICATE

"THIS IS TO CERTIFY THAT THE SCOPE OF WORK HAS BEEN EXPLAINED TO ME
BY THE ARCHITECT / CONSULTANT AND CONSIDERING THE BUDGET
PROVISION THEREFORE I AM SATISFIED WITH THE PROJECT PROPOSAL."

NOTE: USER SIGNATURE IS PROVIDED IN THE SCANNED COPY OF THE PLANS AND
HENCE IT IS REQUESTED THAT THE SAME IS NOT INSISTED ON DIGITAL PRINTS, IN CASE
REQUIRED, THE SAME WILL BE OBTAINED BEFORE STARTING OF THE WORK.

AC-Estate

ARCHITECT MASTER & ASSOCIATES

MUNICIPAL ARCHITECT

REVISION R0 12-08-2022 BUILDING 02 - SECTION B-B' & SECTION C-C' URVASHI

DATE DESCRIPTION BY

FILE PATH : PC NO. 11 D:\Drawings\MILONI1896- 600 STAFF QUARTERS, DEONAR

TYPE OF DWG : APPROVAL DRAWING

CLIENT: MUNICIPAL CORPORATION OF GREATER MUMBAI (MCGM)

TITLE OF DRAWING : TYPICAL SECTION B-B'

PROPOSED REDEVELOPMENT ON OPEN PLOT, KNOWN AS '600 TENEMENTS PLOT BEARING CTS NO. 1(PT) & CTS NO. 3(PT) OF VILLAGE DEONAR IN M/EAST WARD IN MUMBAI

JOB TITLE :

DRAWN BY : URVASHI

CHECKED BY :

SCALE: AS MENTIONED

DATE: 24-02-2022

PROJECT CODE: 1896

DRAWING NO: 1896-512

REVISION NO: R0

THIS DRAWING IS THE PROPERTY OF MASTER & ASSOCIATES, ARCHITECTS, INTERIOR DESIGNERS & PROJECT MANAGEMENT CONSULTANTS

AND IS NOT TO BE REPRODUCED, COPIED, HANDED OVER TO A THIRD PARTY OR USED FOR ANY PURPOSE OTHER THAN FOR WHICH IT HAS BEEN LOANED

STATUS

THIS DRAWING IS THE PROPERTY OF MASTER & ASSOCIATES, ARCHITECTS, INTERIOR DESIGNERS & PROJECT MANAGEMENT CONSULTANTS

AND IS NOT TO BE REPRODUCED, COPIED, HANDED OVER TO A THIRD PARTY OR USED FOR ANY PURPOSE OTHER THAN FOR WHICH IT HAS BEEN LOANED

PRINTS ISSUED TO

PRINTS ISSUED FOR

NO. OF PRINTS

DATE

BY

MASTER & ASSOCIATES
ARCHITECTS, INTERIOR DESIGNERS &
PROJECT MANAGEMENT CONSULTANTS
HARAM HOUSE, 20-28 MARIAL DASH MARG,
MUMBAI - 400 001, INDIA
PHONE NO: +91-22-2385 4000 / 4788 FAX: 22705173
EMAIL: ADD: msa@masterandassociates.com
ALIGERS
SILVERLINE ARIEL BLAZZ: CTS 18 LOCATIONS BLDC- B1, N° 3,
ARCHITECTS, INTERIOR DESIGNERS &
PROJECT MANAGEMENT CONSULTANTS
PHONE NO: 0033 07037648
EMAIL: ADD: msa@masterandassociates.com
MOBILE: 213 92397648