

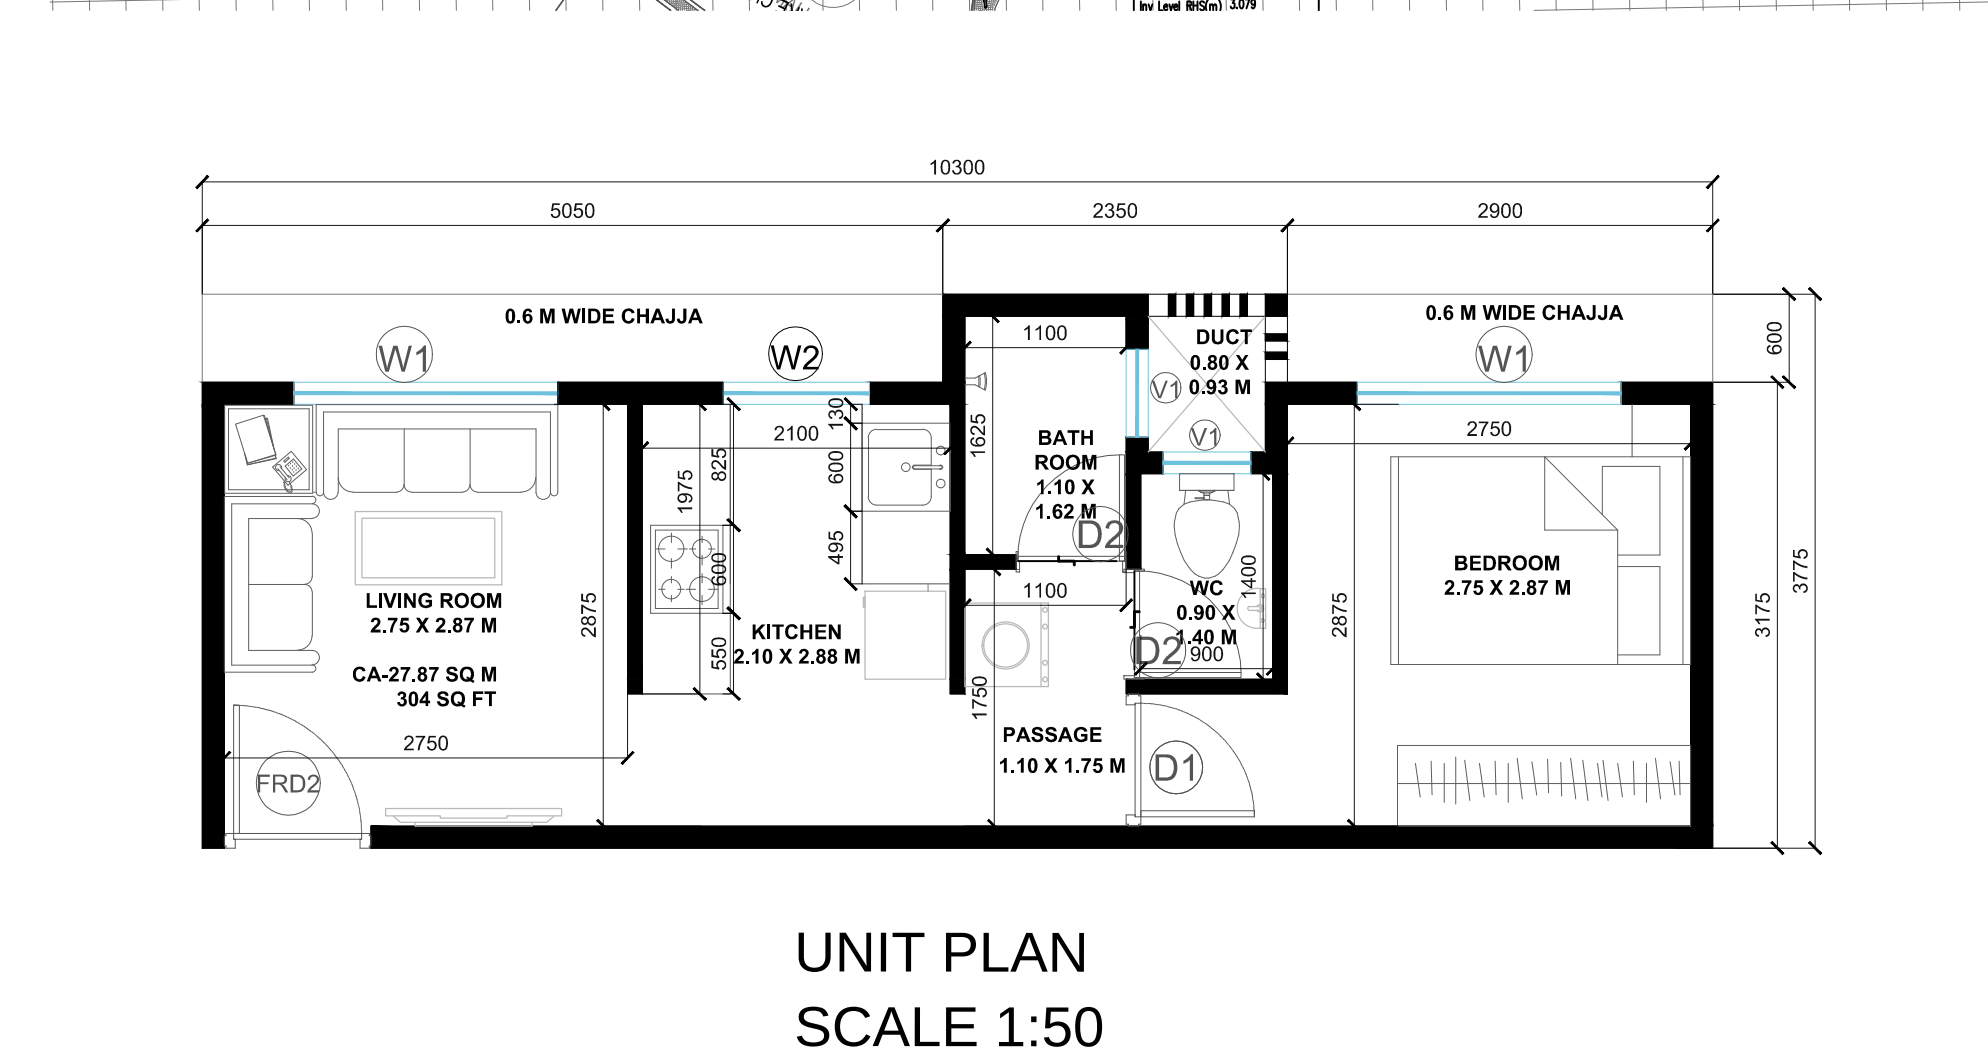
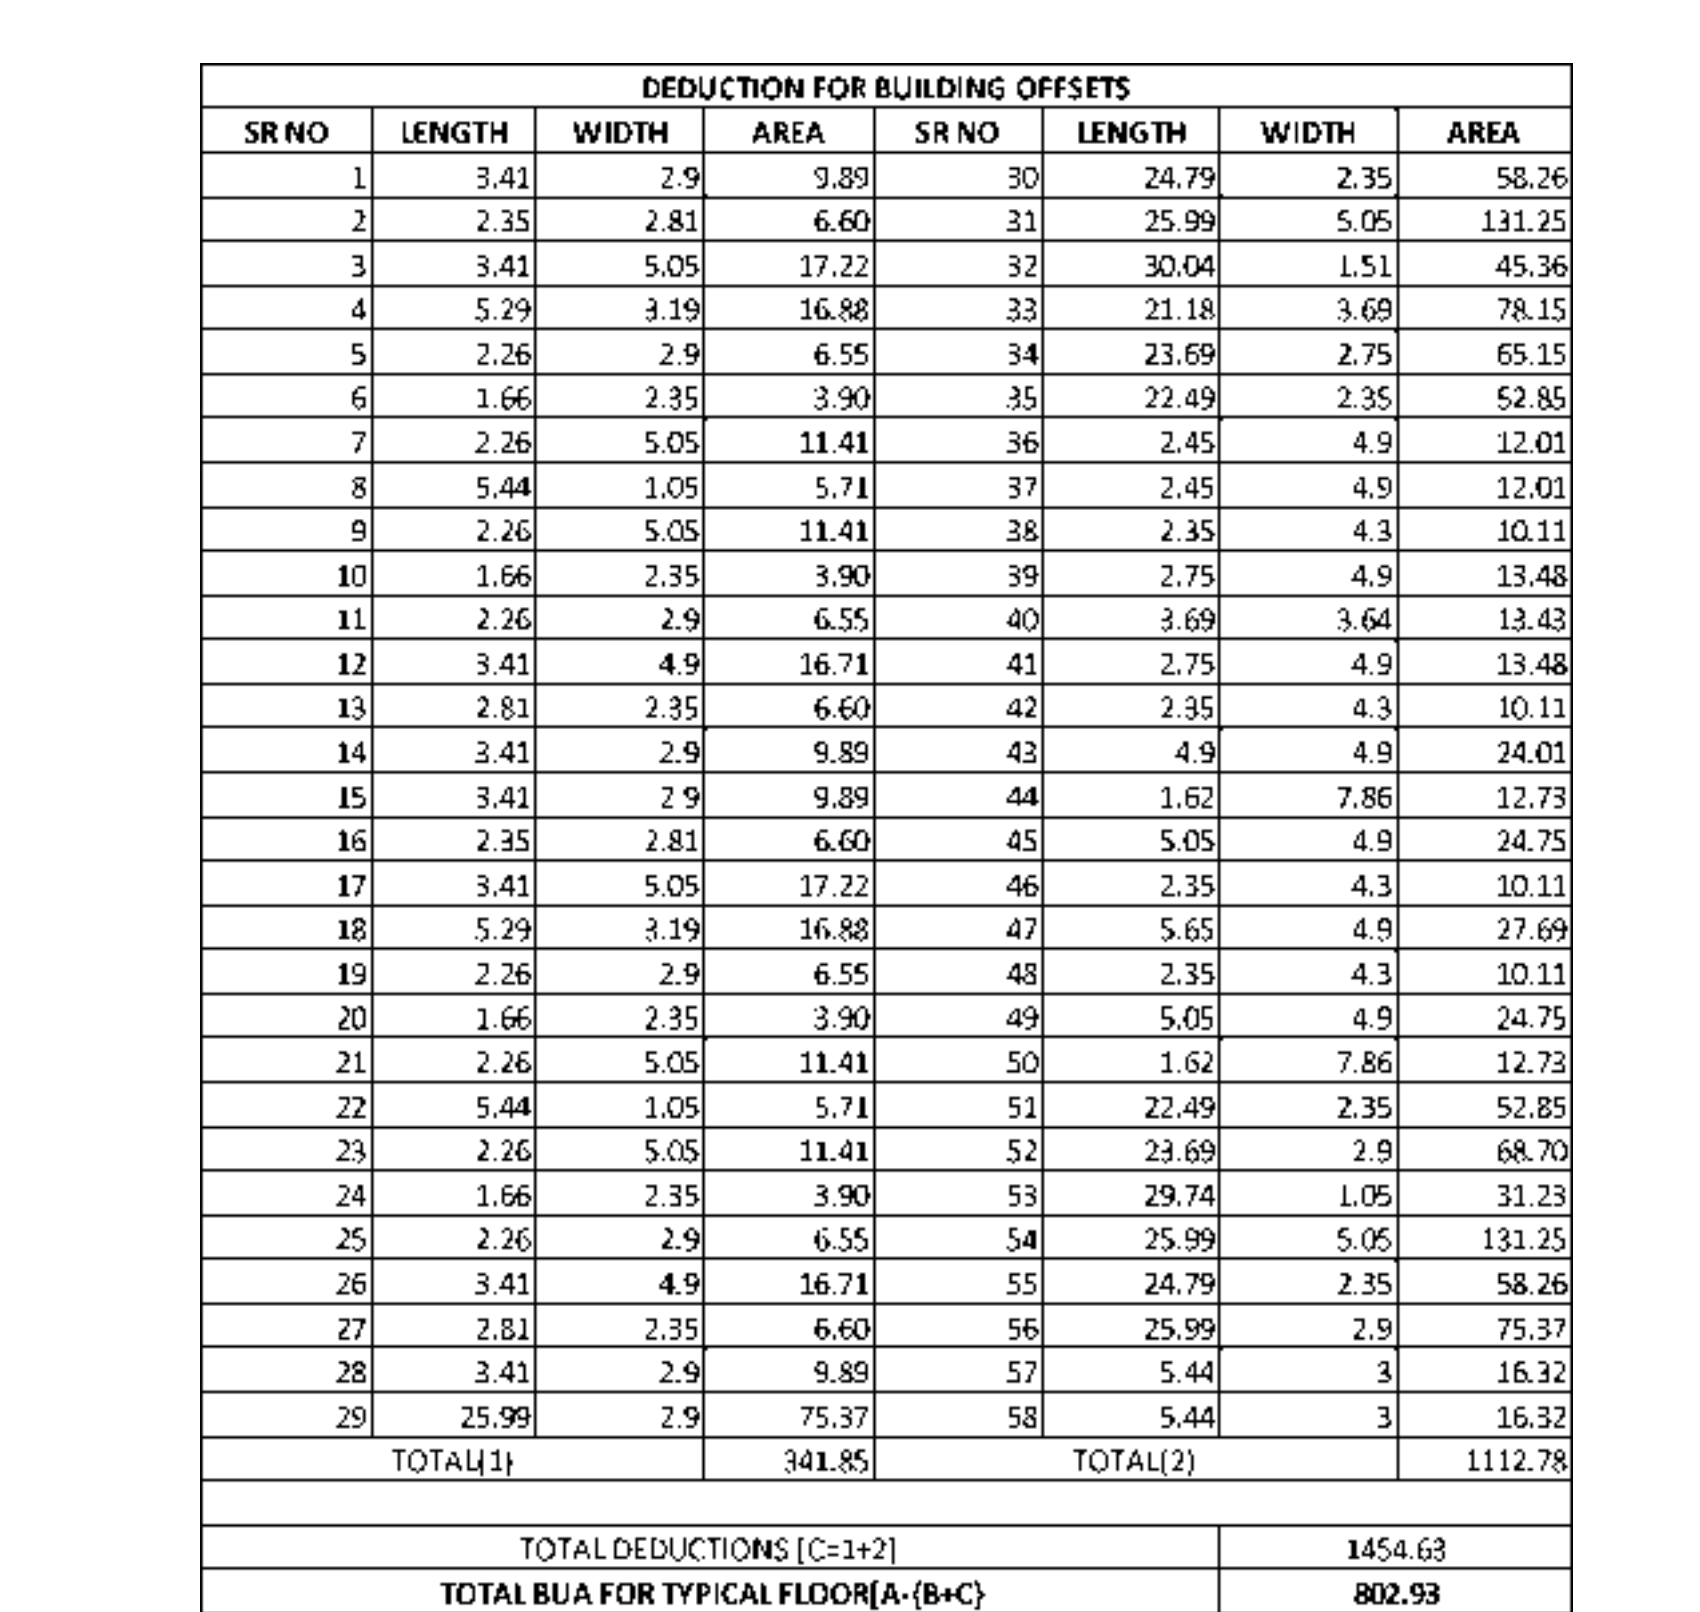
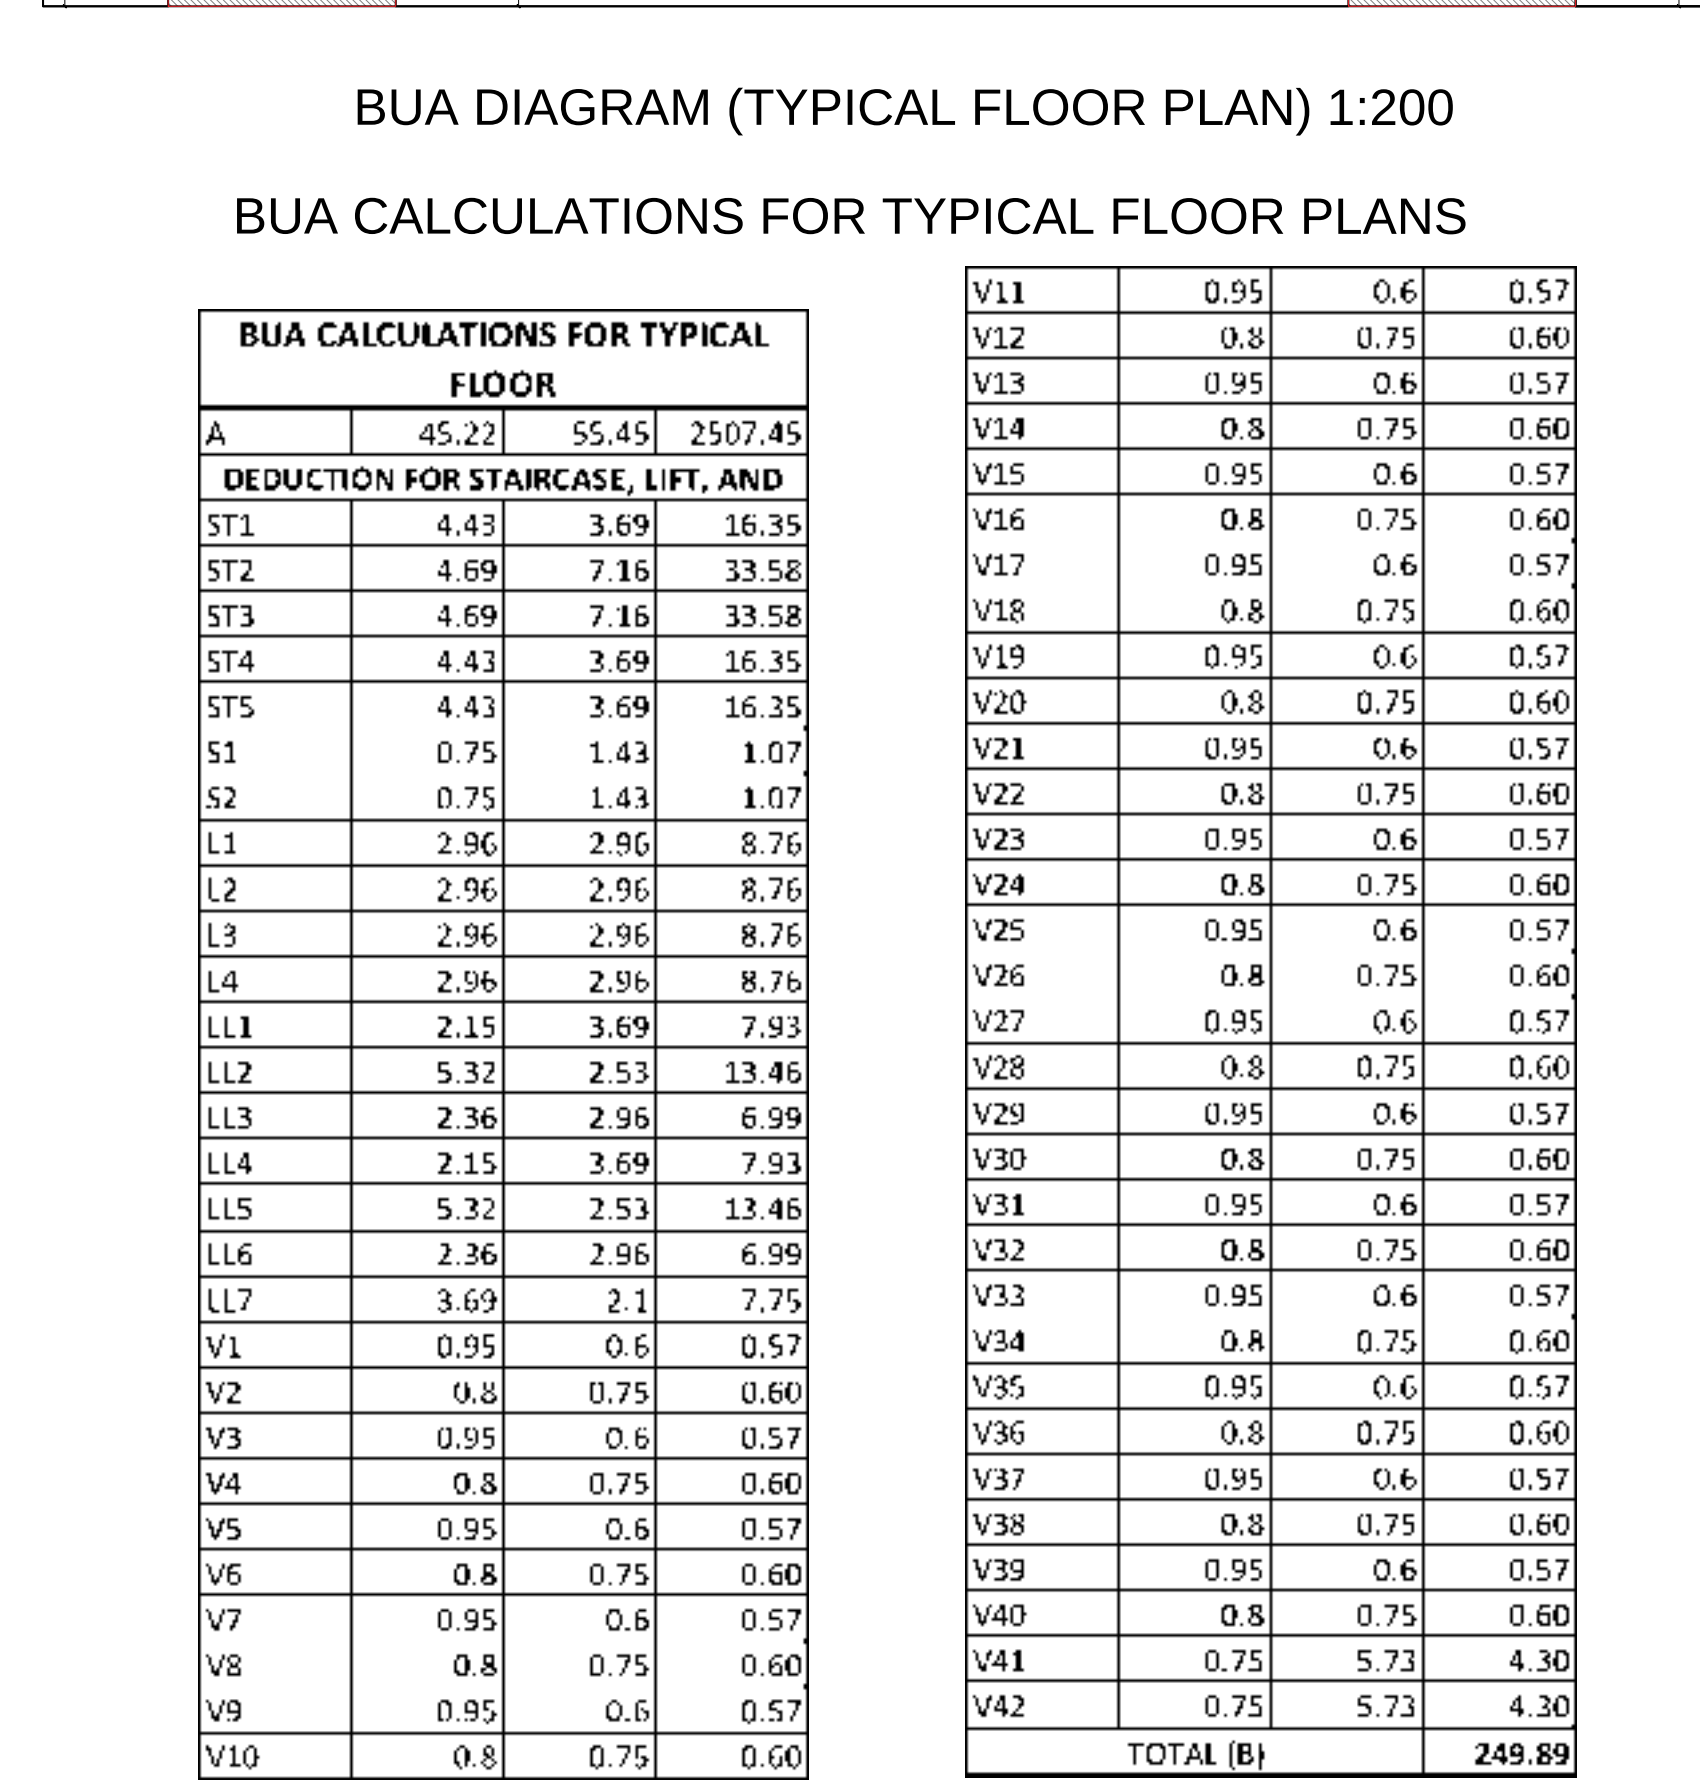


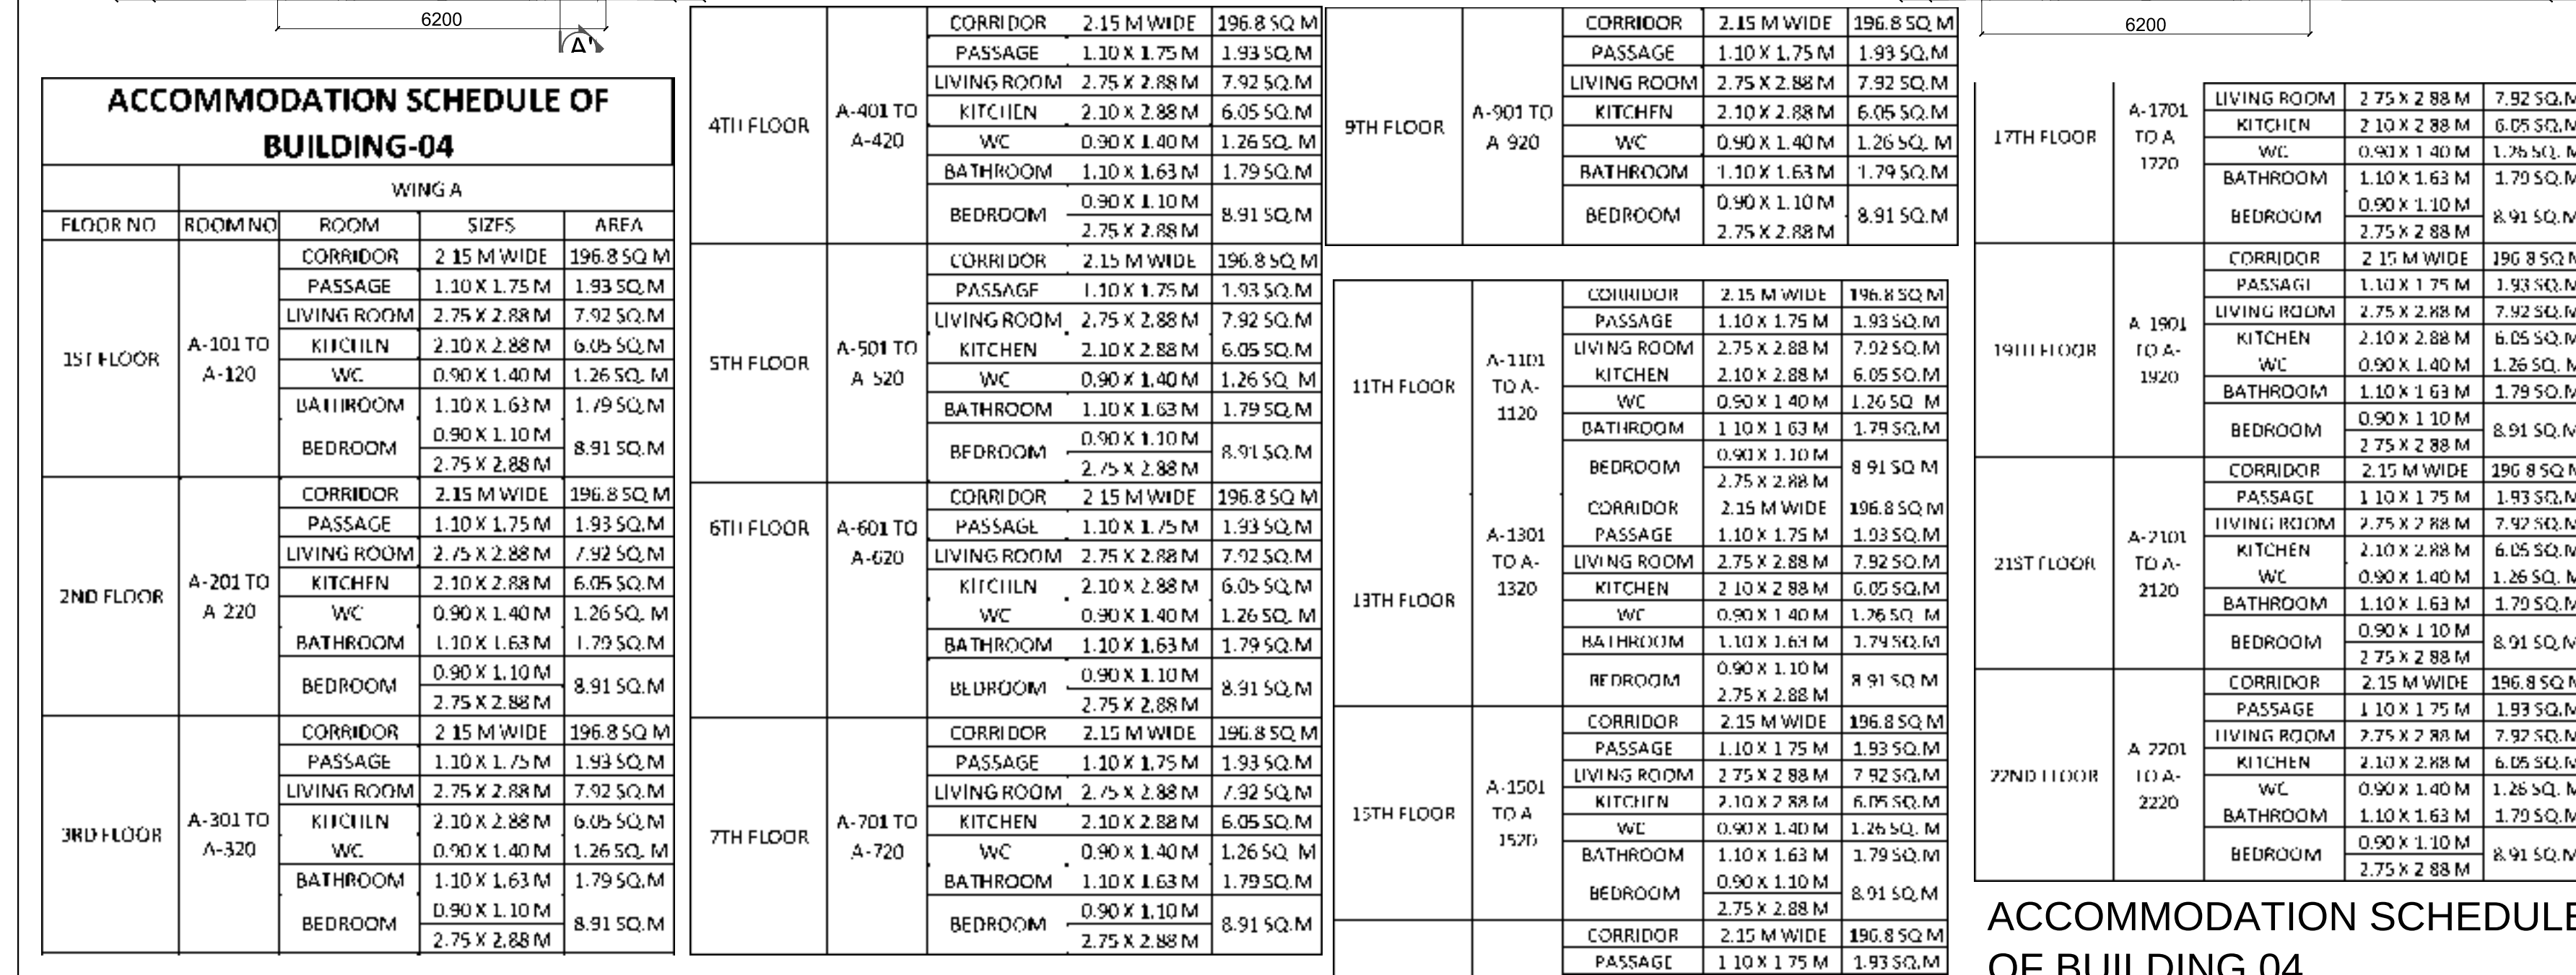


FINISHES SCHEDULE													
DESCRIPTION		FLOOR			SKIRTING		WALL		CEILING				
		VITRIFIED (NON SKID)	KOTA#	CERAMIC (NON SKID)	GRANITE BLACK	KOTA STONE (UP TO 150 MM)	CERAMIC (UP TO 2100 MM)	VITRIFIED (UP TO 150 MM)	OIL BASED DISTEMPER	SYNTHETIC ENAMEL	ACRYLIC PAINT (EXTERIOR WALLS)	OIL BASED DISTEMPER	SYNTHETIC ENAMEL
ENTRANCE LOBBY		●					●					●	
METER ROOM			●							●			●
SOCIETY OFFICE		●						●	●	●		●	●
STAIRCASE			●			●			●	●		●	●
LIVING ROOM		●					●	●	●	●		●	●
BEDROOM		●					●	●	●	●		●	●
KITCHEN		●					●	●	●	●		●	●
KITCHEN PLATFORM				●									
WC				●			●		●			●	●
BATH				●			●		●			●	●
PASSAGE		●						●	●	●		●	●
CORRIDOR		●						●	●	●		●	●


FINISHES SCHEDULE



THIS DRAWING IS THE PROPERTY OF
MASTER & ASSOCIATES ARCHITECTS, INTERIOR DESIGNERS &
PROJECT MANAGEMENT CONSULTANTS
AND IS NOT TO BE REPRODUCED, COPIED, HANDED OVER
TO A THIRD PARTY OR USED FOR ANY PURPOSE OTHER
THAN THAT FOR WHICH IT HAS BEEN LOANED

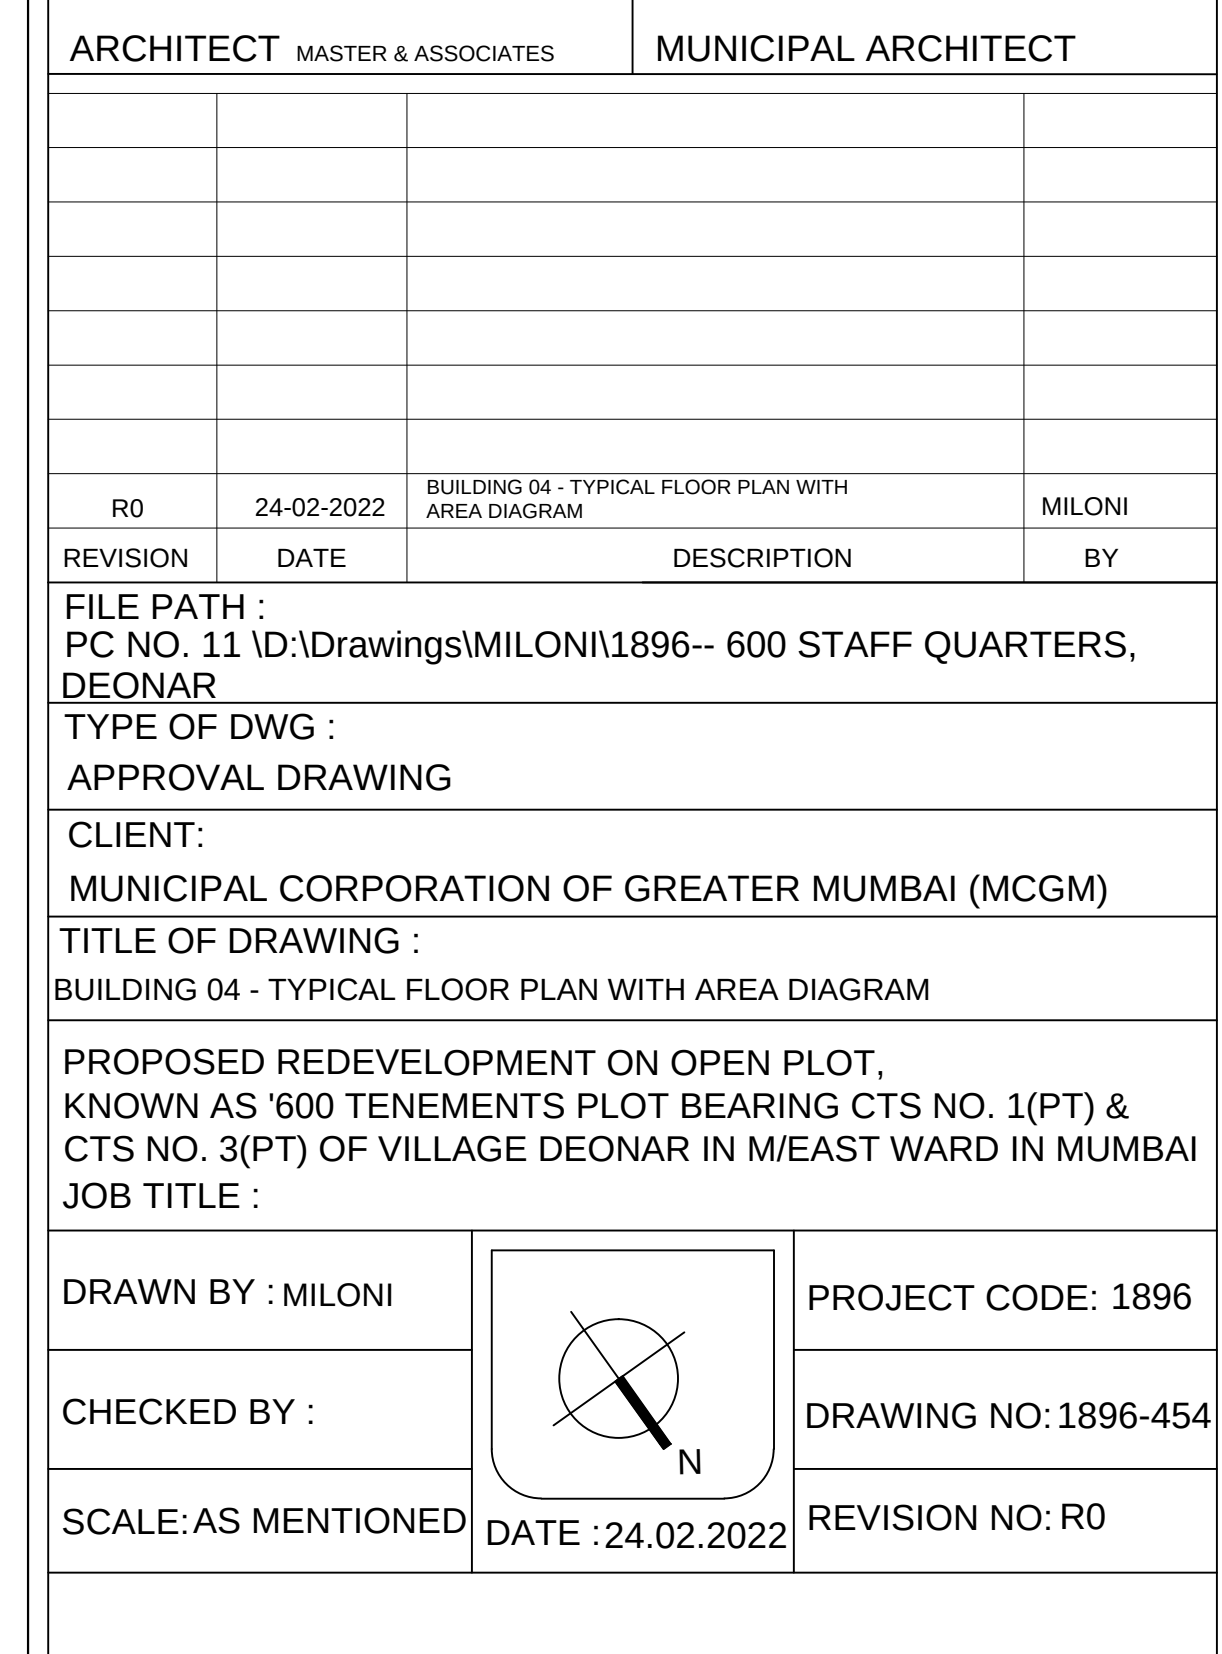

AND IS NOT TO BE REPRODUCED, COPIED HANDED
OVER TO A THIRD PARTY OR USED FOR ANY PURPOSE
OTHER THAN FOR WHICH IT HAS BEEN LOANED

 	<u>MEMBERS</u> HAMAM HOJSEJ, 38 AMBAL, DOŠI MARO, NO. MAYA - 400101, INDO PHONE NO 91-22-2905 4040 : FAX NO 91-22-2903173 EMAIL ADD : info@masterindia.com info@masterindia.com info@masterindia.com
<u>MASTER & ASSOCIATES</u> ARCHITECTS, INTERIOR DESIGNERS & PROJECT MANAGEMENT CONSULTANTS	<u>AL GUERINS</u> BLANKE AR ELAZZI, CITE 18 LOGEMENTS BLOC : N° 3, CITE DE BERMAHA, ZIADALA ALGUERINS PHONE NO 00213-01706569 EMAIL ADD : alguerins@yahoo.fr MOBILE E : 213-9397666

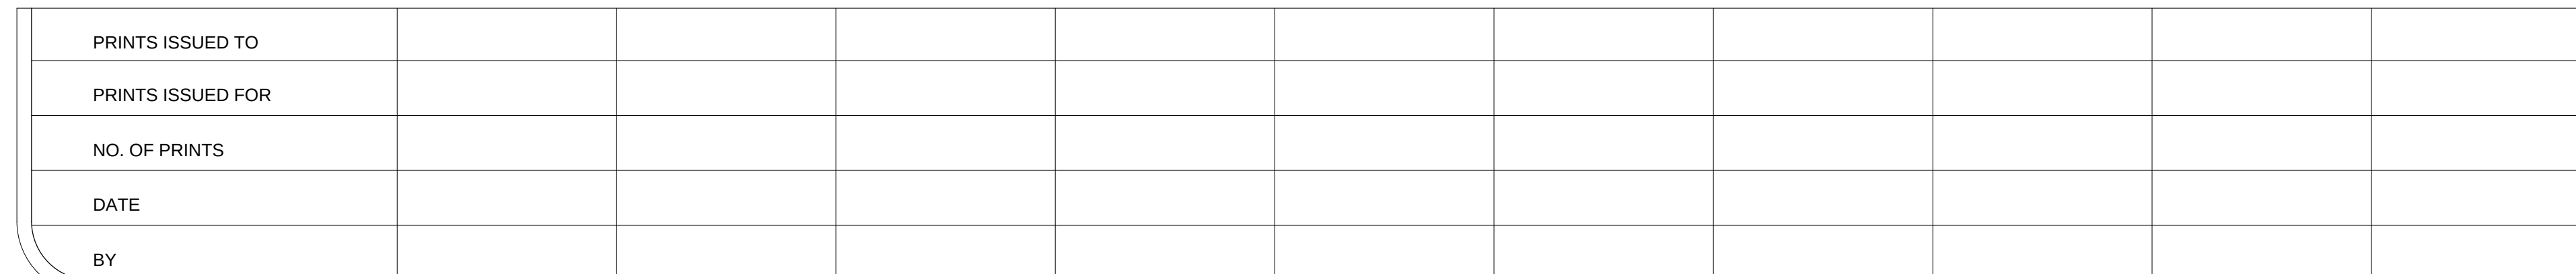

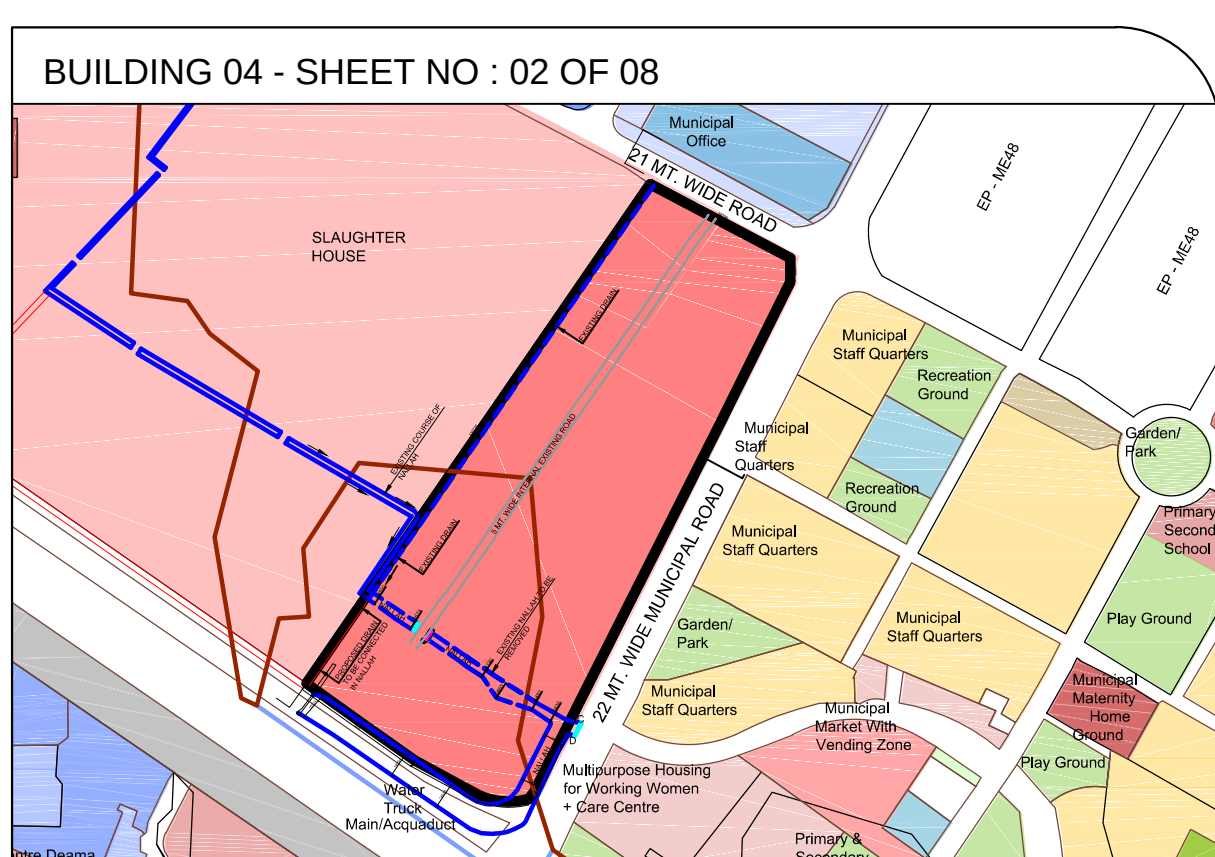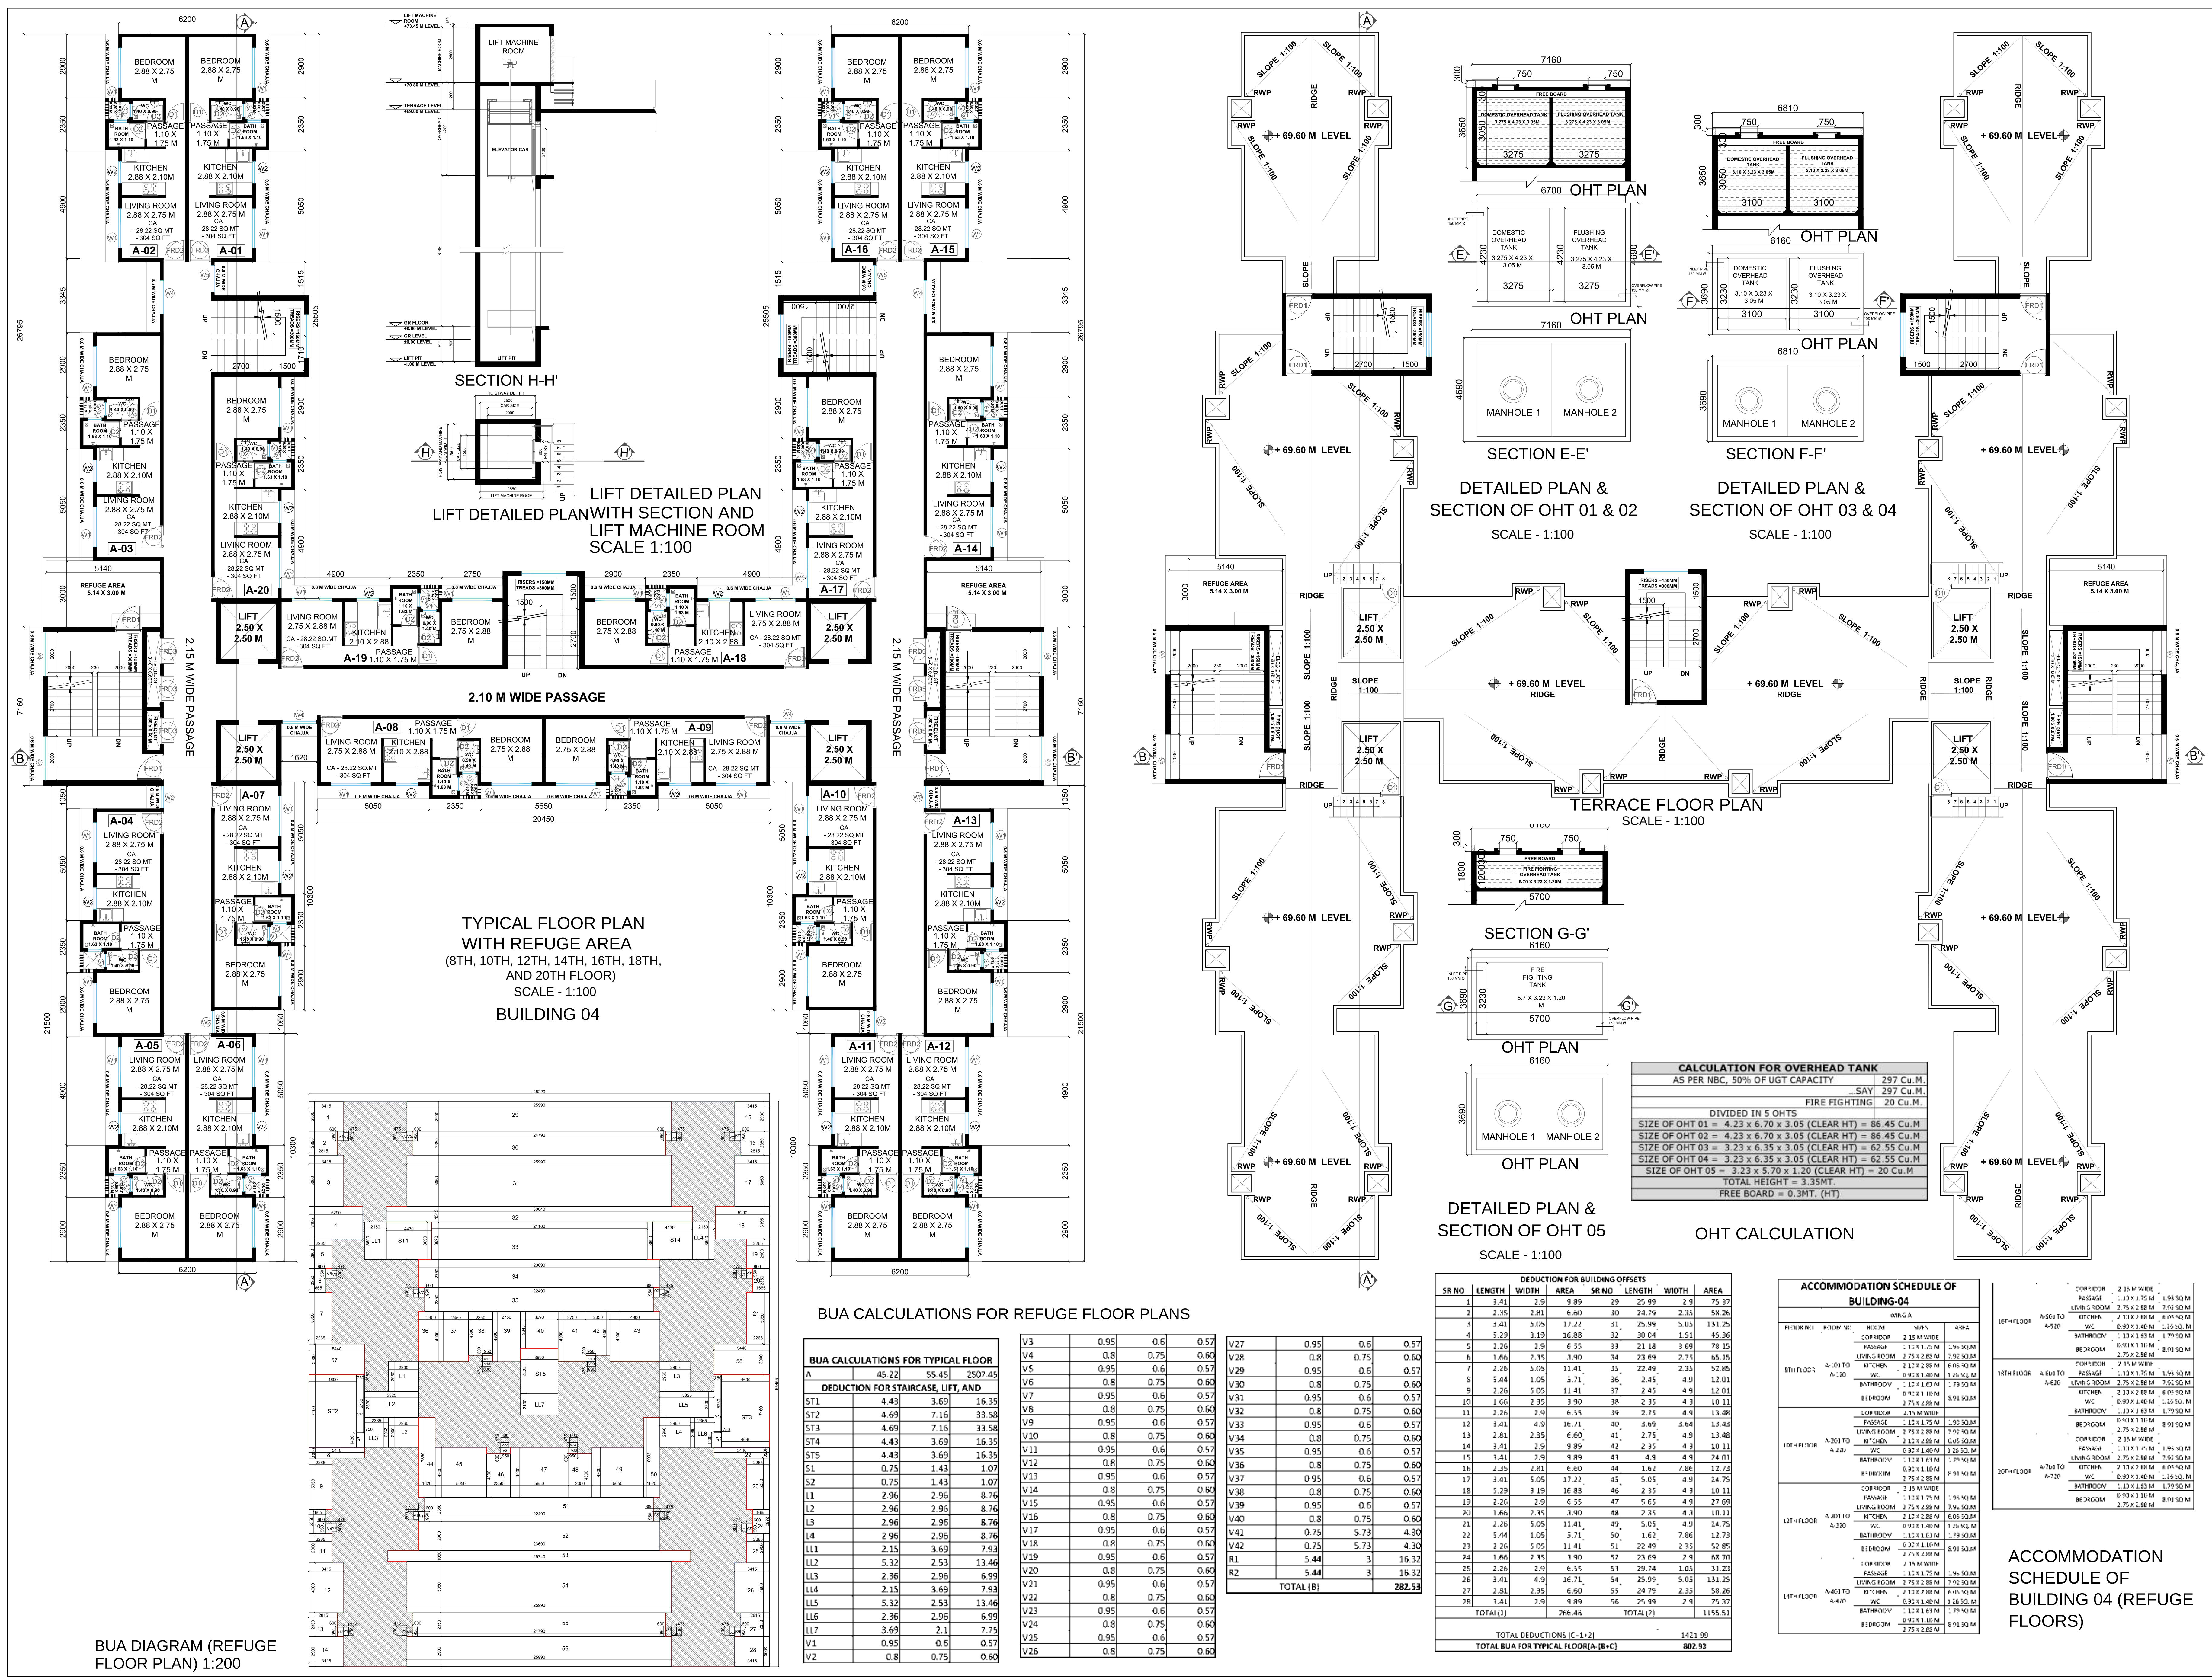

LOCATION PLAN SCALE 1:4000

CONTENT OF SHEET :

- REFUGE FLOOR PLAN
- AREA DIAGRAM FOR REFUGE FLOOR PLAN
- AREA CALCULATION FOR REFUGE FLOOR PLAN
- LIFT DETAILS
- TERRACE FLOOR PLAN
- OHT DETAILED PLAN AND SECTIONS
- OHT CALCULATIONS
- ACCOMMODATION TABLE (REFUGE FLOORS)

AD-FO	D-FO	DY-CFO
SE-BP	AE-BP	EE-BP
CERTIFICATE		
"THIS IS TO CERTIFY THAT THE SCOPE OF WORK HAS BEEN EXPLAINED TO ME BY THE ARCHITECT / CONSULTANT AND CONSIDERING THE BUDGET PROVISION THEREFORE I AM SATISFIED WITH THE PROJECT PROPOSAL."		
NOTE : USER SIGNATURE IS PROVIDED IN THE SCANNED COPY OF THE PLANS AND HENCE IT IS REQUESTED THAT THE SAME IS NOT INSISTED ON DIGITAL PRINTS, IN CASE REQUIRED , THE SAME WILL BE OBTAINED BEFORE STARTING OF THE WORK.		
AC-Estate		

ARCHITECT MASTER & ASSOCIATES MUNICIPAL ARCHITECT		
R0 24-02-2022 BUILDING 04 - REFUGE FLOOR PLAN WITH AREA DIAGRAM TERRACE FLOOR PLAN, OHT DETAILED PLAN AND SECTION MILONI		
REVISION	DATE	DESCRIPTION
FILE PATH :	PC NO. 11 ID: Drawings\MILONI\1896- 600 STAFF QUARTERS, DEONAR	
TYPE OF DWG :	APPROVAL DRAWING	
CLIENT :	MUNICIPAL CORPORATION OF GREATER MUMBAI (MCGM)	
TITLE OF DRAWING :	BUILDING 04 - REFUGE FLOOR PLAN WITH AREA DIAGRAM, TERRACE PLAN	
PROPOSED REDEVELOPMENT ON OPEN PLOT, KNOWN AS '600 TENEMENTS' PLOT BEARING CTS NO. 1(PT) & CTS NO. 3(PT) OF VILLAGE DEONAR IN M/EAST WARD IN MUMBAI	JOB TITLE :	
DRAWN BY : MILONI	PROJECT CODE: 1896	
CHECKED BY :	DRAWING NO: 1896-455	
SCALE: AS MENTIONED	DATE : 24.02.2022	REVISION NO: R0

THIS DRAWING IS THE PROPERTY OF MASTER & ASSOCIATES ARCHITECTS, INTERIOR DESIGNERS & PROJECT MANAGEMENT CONSULTANTS		
AND IS NOT TO BE REPRODUCED, COPIED, HAND-HELD, OVER TO A THIRD PARTY OR USED FOR ANY PURPOSE OTHER THAN FOR WHICH IT HAS BEEN LOANED		
STATUS		
MUMBAI HARBOR HOUSE, 34-38 ARAVALI DASH MARG, PUNE - 411 001, INDIA. PHONE NO: +91-22-2595 8006 / 4736 FAX 22700373 EMAIL: AD@masterandassociates.com		
ALGERIES BLANQUE ALBAZ, CITE VA LOUAGNONS BLANC - BT. N° 1, CITE EL BEHMA, DEONAR ALGERIES. PHONE NO: 0213-21717049 EMAIL: AD@masterandassociates.com MOBILE : 213-9397968		

PRINTS ISSUED TO	
------------------	--	--	

STILT FLOOR PLAN
SCALE - 1:100

DOOR SCHEDULE FOR BUILDING 4

SR NO.	DOOR TYPE	DIMENSION	DESCRIPTION	NO.	ROOM
1	DOOR	2.00 X 2.00 M	DOOR TO STAIRS	1	STAIRS
2	DOOR	2.00 X 2.00 M	DOOR TO STAIRS	2	STAIRS
3	DOOR	2.00 X 2.00 M	DOOR TO STAIRS	3	STAIRS
57	DOOR	2.00 X 2.00 M	DOOR TO STAIRS	57	STAIRS
58					

WINDOW SCHEDULE

DOOR SCHEDULE

ACCOMODATION SCHEDULE OF STILT FLOOR

THIS DRAWING IS THE PROPERTY OF
MASTER & ASSOCIATES ARCHITECTS, INTERIOR DESIGNERS &
PROJECT MANAGEMENT CONSULTANTS
AND IS NOT TO BE REPRODUCED, COPIED, HANDED OVER
TO A THIRD PARTY OR USED FOR ANY PURPOSE OTHER
THAN THAT FOR WHICH IT HAS BEEN LOANED

FIRE FIGHTING PLAN

FIRE FIGHTING DETAILED PLAN AND SECTION
SCALE - 1:100

UGT PLAN

UGT PLAN

SECTION C-C'

PARKING CALCULATION		
AS PER DCPR, 2034 :		
UNDER REGULATION 33(11),		
4 WHEELER PARKING REQUIREMENT		
1	1 CAR PARK SPACE FOR EVERY 4 TENEMENTS	
2	TOTAL NO. FLATS	440
3	NO OF PARKING REQUIRED	110
4	25% CAR PARKS FOR VISITORS	27.5
5	TOTAL NO OF 4 WHEELER PARKING REQUIRED	138
2 WHEELER PARKING REQUIREMENT		
6	1 TWO WHEELER PARK FOR EVERY 2 RESIDENTIAL TENEMENTS	
7	TOTAL NO OF 2 WHEELER PARKING REQUIRED	220
PROPOSED PARKING		
8	TOTAL NO. OF SMALL CAR PARK	8
9	TOTAL NO. OF BIG CAR PARK	6
10	TOTAL NO. OF 4 WHEELER PARKING	14
11	TOTAL NO. OF 2 WHEELER PARKING	90

PARKING CALCULATION

CALCULATION FOR UNDERGROUND TANK			
DESCRIPTION	NO OF PEOPLE	PER DAY REQUIRE	TOTAL (LITS)
RESIDENTIAL USE (Considering 4 People for 1 BHK)	1760	135	237600
TOTAL ONE DAY REQUIREMENT			237600
LANDSCAPE (25%)		...	59400
1 DAY SPARE CAPACITY			297000
GROSS CAPACITY			594000
AS PER NBC, TOTAL UGT CAPACITY			594 Cu.M.
SAY			594 Cu.M.
SIZE OF UGT = 13.2 x 15.0 x 3.0 (HT) = 594 Cu.M			
SIZE OF FIRE FIGHTING = 8.34 x 8.0 x 3.0 (HT) = 200 Cu.M			
TOTAL HEIGHT = 3.3MT.			
FREE BOARD = 0.3MT. (HT)			

UGT CALCULATION AND FIRE FIGHTING CALCULATIONS

UGT CALCULATION AND FIRE FIGHTING CALCULATIONS

LOCATION PLAN SCALE 1:4000

CONTENT OF SHEET

STILT FLOOR PLAN
PARKING CALCULATIONS
WATER CALCULATIONS
UGT DETAILS

CERTIFICATE

"THIS IS TO CERTIFY THAT THE SCOPE OF WORK HAS BEEN EXPLAINED TO ME
BY THE ARCHITECT / CONSULTANT AND CONSIDERING THE BUDGET
PROVISION THEREFORE I AM SATISFIED WITH THE PROJECT PROPOSAL"

NOTE : USER SIGNATURE IS PROVIDED IN THE SCANNED COPY OF THE PLANS AND SINCE IT IS REQUESTED THAT THE SAME IS NOT INSISTED ON DIGITAL PRINTS, IN CASE REQUIRED , THE SAME WILL BE OBTAINED BEFORE STARTING OF THE WORK.

AC-Esta

R0	24-02-2022	BUILDING 04 - STILT FLOOR PLAN, UGT DETAILED PLAN AND SECTIONS, CALCULATIONS AND SCHEDULES	MIL
----	------------	--	-----

FILE PATH :
PC NO. 11 \D:\Drawings\MILONI\1896-- 600 STAFF QUARTERS,

DEONAR
TYPE OF DWG : APPROVAL DRAWING

CLIENT: MUNICIPAL CORPORATION OF GREATER MUMBAI (MCGM)
TITLE OF DRAWING : BUILDING 04 - STILT FLOOR PLAN, UGT DETAILED PLAN AND SECTIONS, CALCULATIONS AND SCHEDULES

PROPOSED REDEVELOPMENT ON OPEN PLOT,
KNOWN AS '600 TENEMENTS PLOT BEARING CTS NO. 1(PT) &
CTS NO. 3(PT) OF VILLAGE DEONAR IN M/EAST WARD IN MUMBAI
JOB TITLE :

DRAWN BY : MILONI	PROJECT CODE: 1896
-------------------	--------------------

CHECKED BY :		DRAWING NO: 1896-456
--------------	---	----------------------

SCALE:AS MENTIONED DATE :24.02.2022 REVISION NO: R0

THIS DRAWING IS THE PROPERTY OF

MASTER & ASSOCIATE
ARCHITECTS, INTERIOR DESIGNERS &
PROJECT MANAGEMENT CONSULTANTS

IS NOT TO BE REPRODUCED, COPI


OTHER THAN FOR WHICH IT HAS BEEN LOANED

STATUS



MUMBAI
MAMI HOUSE, 34-38 AMBALAL DOSHI MARG,
MUMBAI - 400 001, India.
PHONE NO +91-22-2265 4906 / 4736 FAX 22750173
EMAIL ADD : udaymaster@rediffmail.com
 udaymaster@gmail.com

ALGIERS
E AB ELAZIZ, CITE 18 LOGEMENTS BLOC - B1, N° 1
CITILE DE REHMANIA, ZERALOA ALGIERS
PHONE NO 00213-071076049
MAIL ADD : udaymasteralgerie@gmail.com
MOBILE : 213-55397568

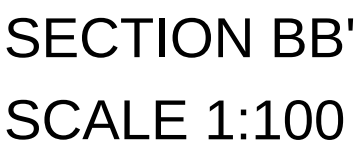


COLOURING OF PLANS AS PER DCPR-34

THIS DRAWING IS THE PROPERTY OF
MASTER & ASSOCIATES ARCHITECTS, INTERIOR DESIGNERS &
PROJECT MANAGEMENT CONSULTANTS
AND IS NOT TO BE REPRODUCED, COPIED, HANDED OVER
TO A THIRD PARTY OR USED FOR ANY PURPOSE OTHER
THAN THAT FOR WHICH IT HAS BEEN LOANED

STATUS



CONTENT OF SHEET : SECTION BB

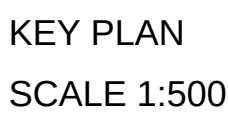

SCALE 1:500



D-FO

DY-CFO

SE-BP

AE-BP

EE-BP

CERTIFICATE

"THIS IS TO CERTIFY THAT THE SCOPE OF WORK HAS BEEN EXPLAINED TO ME
BY THE ARCHITECT / CONSULTANT AND CONSIDERING THE BUDGET
PROVISION THEREFORE I AM SATISFIED WITH THE PROJECT PROPOSAL"

NOTE : USER SIGNATURE IS PROVIDED IN THE SCANNED COPY OF THE PLANS AND
HENCE IT IS REQUESTED THAT THE SAME IS NOT INSISTED ON DIGITAL PRINTS, IN CASE
REQUIRED , THE SAME WILL BE OBTAINED BEFORE STARTING OF THE WORK.

AC-Estate

ARCHITECT MASTER & ASSOCIATES

MUNICIPAL ARCHITECT

R0	24-02-2022	BUILDING 04 - SECTION B-B'	MILONI
REVISION	DATE	DESCRIPTION	BY

FILE PATH :
PC NO. 11 \D:\Drawings\MILON\1896-- 600 STAFF QUARTERS,
DEONAR

TYPE OF DWG :

APPROVAL DRAWING

CLIENT

MUNICIPAL CORPORATION OF GREATER MUMBAI (MCGM)

TITLE OF DRAWING :

BUILDING 04 - SECTION B-B'

PROPOSED REDEVELOPMENT ON OPEN PLOT,
KNOWN AS '600 TENEMENTS PLOT BEARING CTS NO. 1(PT) &
CTS NO. 3(PT) OF VILLAGE DEONAR IN M/EAST WARD IN MUMBAI
JOB TITLE :

DRAWN BY : MILONI

PROJECT CODE: 1896

CHECKED BY :

DRAWING NO: 1896-458

SCALE:AS MENTIONED

DATE : 24.02.2022

REVISION NO: R0

THIS DRAWING IS THE PROPERTY OF
MASTER & ASSOCIATES
ARCHITECTS, INTERIOR DESIGNERS &
PROJECT MANAGEMENT CONSULTANTS

AND IS NOT TO BE REPRODUCED, COPIED HANDED
OVER TO A THIRD PARTY OR USED FOR ANY PURPOSE
OTHER THAN FOR WHICH IT HAS BEEN LOANED


STATUS




MASTER & ASSOCIATES
ARCHITECTS, INTERIOR DESIGNERS &
PROJECT MANAGEMENT CONSULTANTS

MUMBAI
HAMAM HOUSE, 34-38 AMBALAL DOSHI MARG,
MUMBAI - 400 001, India.
PHONE NO +91-22-2205 4606 / 4736 FAX 227500173
EMAIL ADD: usdaymaster@hotmail.com
usdaymaster@gmail.com

ALGIERS
ANE ABD ELAZIZ, CITE 18 LOGEMENTS BLOC - B1, N°3,
CILLE DE REHMANIA, ZERALDA ALGIERS.
PHONE NO 00213-071076049
EMAIL ADD: usdaymasteralgeria@gmail.com

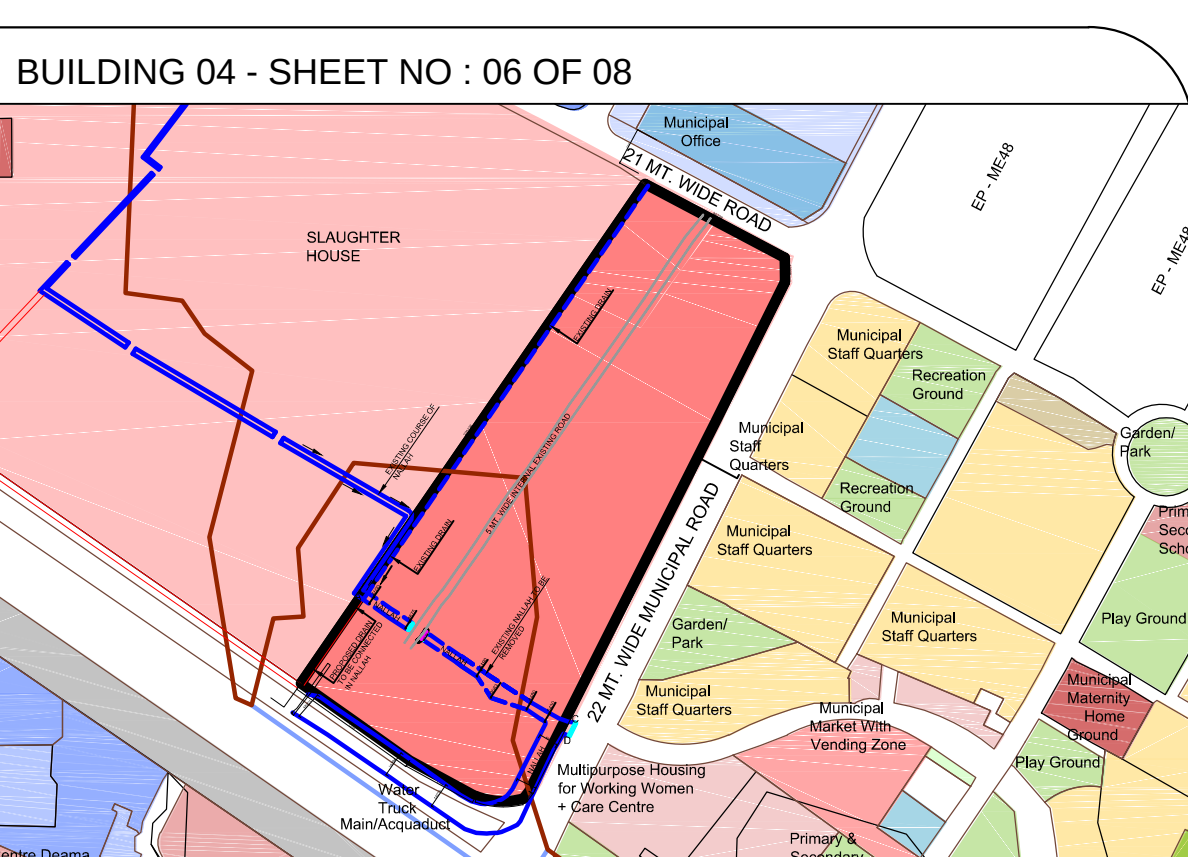

LOCATION PLAN SCALE 1:4000
CONTENT OF SHEET : NORTH- EAST ELEVATION SOUTH- WEST ELEVATION

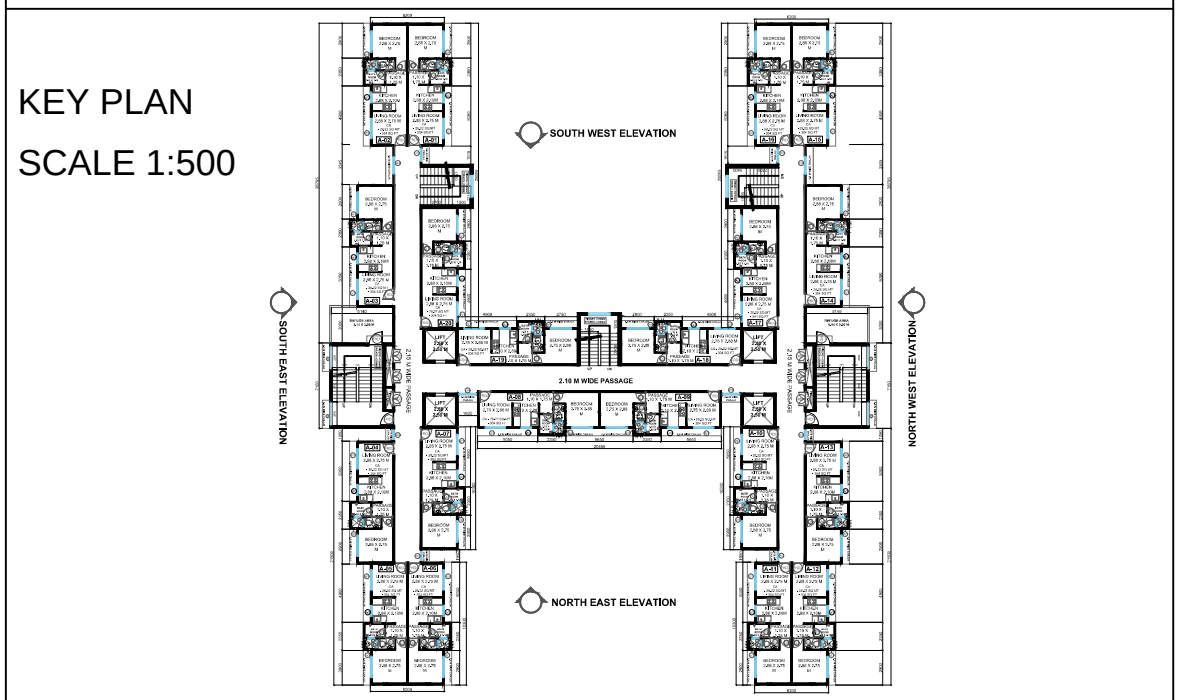

AD-FO	D-FO	DY-CFO
SE-BP	AE-BP	EE-BP

<u>CERTIFICATE</u> "THIS IS TO CERTIFY THAT THE SCOPE OF WORK HAS BEEN EXPLAINED TO ME BY THE ARCHITECT / CONSULTANT AND CONSIDERING THE BUDGET PROVISION THEREFORE I AM SATISFIED WITH THE PROJECT PROPOSAL" NOTE : USER SIGNATURE IS PROVIDED IN THE SCANNED COPY OF THE PLANS AND HENCE IT IS REQUESTED THAT THE SAME IS NOT INSISTED ON DIGITAL PRINS, IN CASE REQUIRED , THE SAME WILL BE OBTAINED BEFORE STARTING OF THE WORK.
--

		AC-Estate

ARCHITECT MASTER & ASSOCIATES	MUNICIPAL ARCHITECT
--	----------------------------

[illegible]

R0	24-02-2022	BUILDING 04 - NORTH EAST AND SOUTH WEST ELEVATIONS	MILONI
REVISION	DATE	DESCRIPTION	BY
FILE PATH :			

PC NO: 11 ID: Drawings\MILONI\1896-- 600 STAFF QUARTERS, DEONAR
TITLE OF DWG : APPROVAL DRAWING
CLIENT: MUNICIPAL CORPORATION OF GREATER MUMBAI (MCGM)
TITLE OF DRAWING : BUILDING 04 - NORTH EAST AND SOUTH WEST ELEVATIONS
PROPOSED REDEVELOPMENT ON OPEN PLOT, KNOWN AS '600 TENEMENTS' PLOT BEARING CTS NO. 1(P/T) & CTS NO. 3(P/T) OF VILLAGE DEONAR IN M/EAST WARD IN MUMBAI JOB TITLE :

DRAWN BY : MILONI		PROJECT CODE: 1896
CHECKED BY :		DRAWING NO: 1896-459
SCALE: AS MENTIONED		REVISION NO: R0
DATE : 24.02.2022		

THIS DRAWING IS THE PROPERTY OF <u>MASTER & ASSOCIATES</u> ARCHITECTS, INTERIOR DESIGNERS &	STATUS

AND IS NOT TO BE REPRODUCED, COPIED OR OVER TO A THIRD PARTY OR USED FOR ANY PURPOSE OTHER THAN FOR WHICH IT WAS LOANED	
	
MASTER & ASSOCIATES ARCHITECTS, INTERIOR DESIGNERS & PROJECT MANAGEMENT CONSULTANTS	
MUMBAI HAMAM HOUSE, 18, ANARALI, DASHI MARG, MUMBAI - 400 003, India. PHONE NO: 91-22-2205-8858 / 8858 / FAX 22003713 EMAIL ADD: - citymaster@rediffmail.com - citymaster@mastergroup.com	
ALGERIA SULMANE AB ELHAZI, CITE EL TOUGHEMMENI BLOC - N° 13, CITE EL REHMANIA, ZENEDDA ALGERIES PHONE NO: 213-21-78203378690 EMAIL ADD: - citymasteralgeria@gmail.com MOBILE : 213-9387998	

PRINTS ISSUED TO									
PRINTS ISSUED FOR									
NO. OF PRINTS									
DATE									
BY									

	THICK BLACK PLOT BOUNDARY		RED DOTTED DRAINAGE & SEWERAGE WORK
	GREEN EXISTING STREET		BLUE DOTTED THIN WATER SUPPLY
	GREEN DOTTED FUTURE STREET		RED HATCHED DEVIATIONS
	THICK BLACK DOTTED PERM. BLDG		GREEN WASH RECREATION GROUND
	NO COLOUR OPEN SPACES		BURNT SIENNA ROADS & SETBACKS
	YELLOW HATCHED DEMOLISHED WORK		APPROPRIATE COLOUR CODE RESERVATION
	RED FILLED PROPOSED WORK		

THIS DRAWING IS THE PROPERTY OF
MASTER & ASSOCIATES, ARCHITECTS, INTERIOR DESIGNERS &
PROJECT MANAGEMENT CONSULTANTS
AND IS NOT TO BE REPRODUCED, COPIED, HANDED OVER
TO A THIRD PARTY OR USED FOR ANY PURPOSE OTHER
THAN THAT FOR WHICH IT HAS BEEN LOANED

STATUS


NORTH-WEST ELEVATION SCALE- 1:100

[illegible]

COLOURING OF PLANS AS PER DCPR-34			
	THICK BLACK PLOT BOUNDARY		RED DOTTED DRAINAGE & SEWERAGE WORK
	GREEN EXISTING STREET		BLUE DOTTED THIN WATER SUPPLY
	GREEN DOTTED FUTURE STREET		RED HATCHED DEVIATIONS
	THICK BLACK DOTTED PERM. BLDG		GREEN WASH RECREATION GROUND
	NO COLOUR OPEN SPACES		BURNT SIENNA ROAD & SETBACKS
	YELLOW HATCHED DEMOLISHED WORK		APPROPRIATE COLOUR CODE RESERVATIONS
	RED FILLED PROPOSED WORK		

THIS DRAWING IS THE PROPERTY OF
MASTER & ASSOCIATES ARCHITECTS, INTERIOR DESIGNERS &
PROJECT MANAGEMENT CONSULTANTS
AND IS NOT TO BE REPRODUCED, COPIED, HANDED OVER
TO A THIRD PARTY OR USED FOR ANY PURPOSE OTHER
THAN THAT FOR WHICH IT HAS BEEN LOANED


STATUS

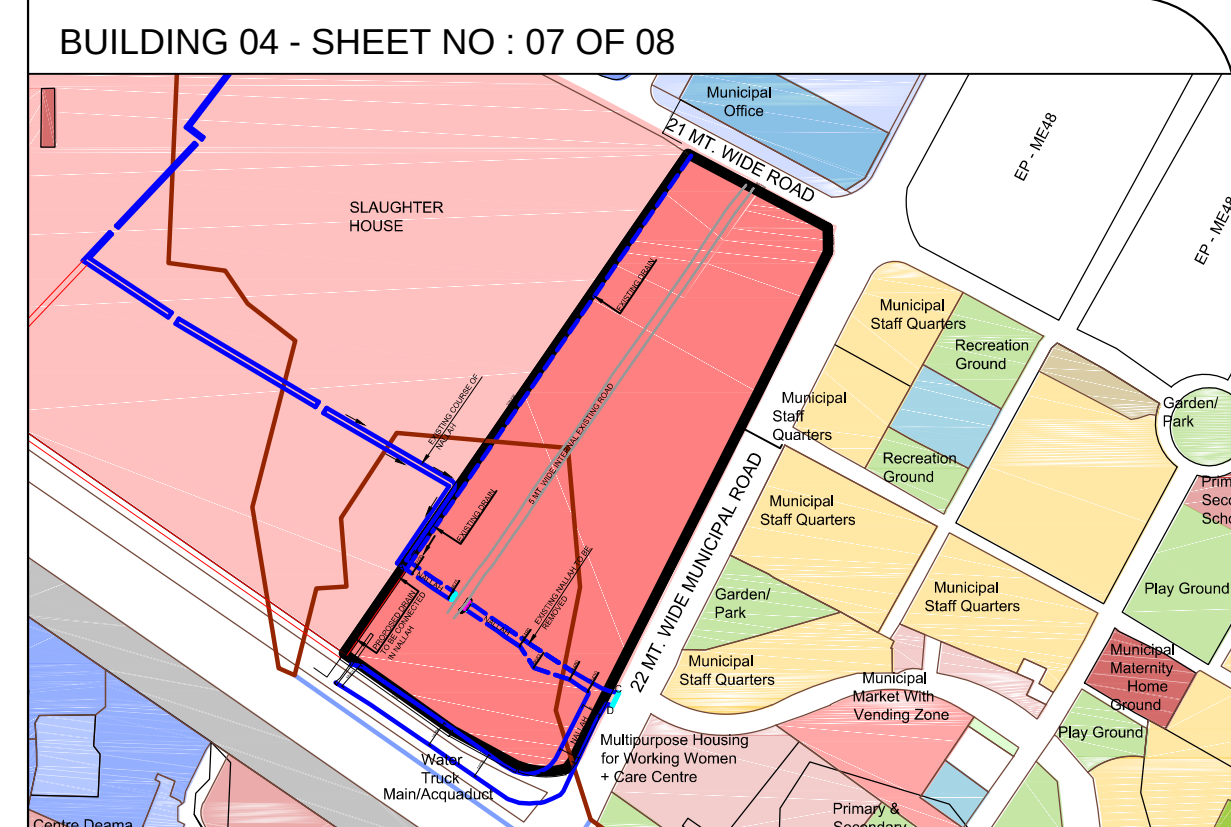

LOCATION PLAN SCALE 1:4000

CONTENT OF SHEET : NORTH- WEST ELEVATION

KEY PLAN
SCALE 1:500

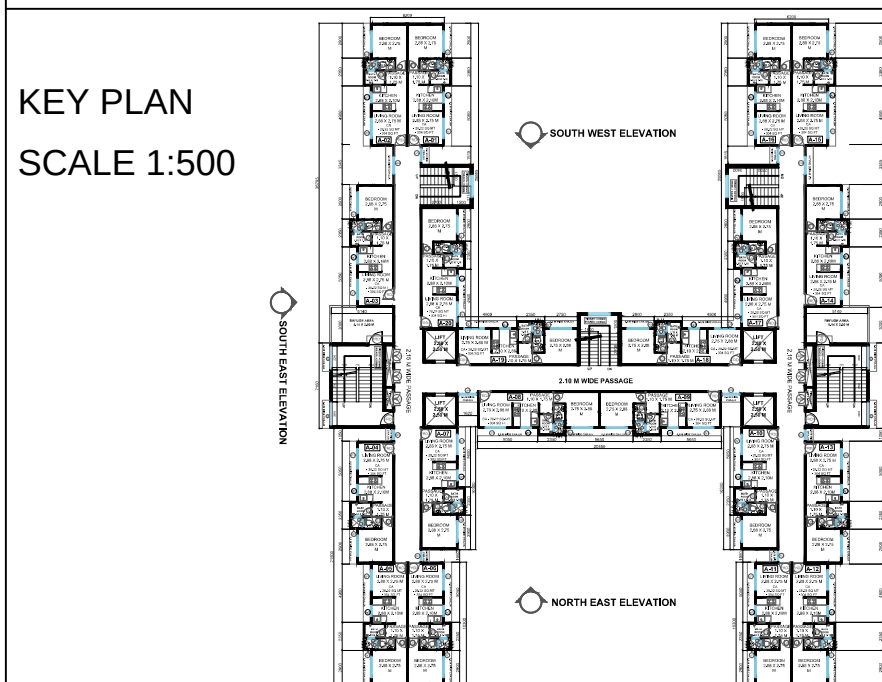

AD-FO	D-FO	DY-CFO
SE-BP	AE-BP	EE-BP

CERTIFICATE

"THIS IS TO CERTIFY THAT THE SCOPE OF WORK HAS BEEN EXPLAINED TO ME
BY THE ARCHITECT / CONSULTANT AND CONSIDERING THE BUDGET
PROVISION THEREFORE I AM SATISFIED WITH THE PROJECT PROPOSAL"

NOTE : USER SIGNATURE IS PROVIDED IN THE SCANNED COPY OF THE PLANS AND
HENCE IT IS REQUESTED THAT THE SAME IS NOT INSISTED ON DIGITAL PRINTS, IN CASE
REQUIRED. THE SAME WILL BE OBTAINED BEFORE STARTING OF THE WORK.

		AC-Estate
--	--	-----------

ARCHITECT MASTER & ASSOCIATES MUNICIPAL ARCHITECT

R0	24-02-2022	BUILDING 04 - NORTH WEST ELEVATION	MILONI
REVISION	DATE	DESCRIPTION	BY

FILE PATH :
PC NO. 11 \D:\Drawings\MILON\1896-- 600 STAFF QUARTERS,
DEONAR

TYPE OF DWG :

APPROVAL DRAWING

CLIENT:

MUNICIPAL CORPORATION OF GREATER MUMBAI (MCGM)

TITLE OF DRAWING :

BUILDING 04 - NORTH WEST ELEVATION

PROPOSED REDEVELOPMENT ON OPEN PLOT,
KNOWN AS '600 TENEMENTS PLOT BEARING CTS NO. 1(PT) &
CTS NO. 3(PT) OF VILLAGE DEONAR IN M/EAST WARD IN MUMBAI
JOB TITLE :

DRAWN BY : MILONI		PROJECT CODE: 1896
CHECKED BY :		DRAWING NO: 1896-460
SCALE: AS MENTIONED		REVISION NO: R0
DATE : 24.02.2022		

THIS DRAWING IS THE PROPERTY OF

MASTER & ASSOCIATE
ARCHITECTS, INTERIOR DESIGNERS &
PROJECT MANAGEMENT CONSULTANTS

AND IS NOT TO BE REPRODUCED, COPIED HANDED
OVER TO A THIRD PARTY OR USED FOR ANY PURPOSE
OTHER THAN FOR WHICH IT HAS BEEN LOANED

STATUS



MASTER & ASSOCIATES
ARCHITECTS, INTERIOR DESIGNERS &
PROJECT MANAGEMENT CONSULTANTS

MUMBAI
HAMAM HOUSE, 34-38 AMBALSAL DOSHI MARG,
MUMBAI - 400 001, India.
PHONE NO +91-22-2265 4606 / 4736 FAX 22750173
EMAIL ADD : udaymaster@rediffmail.com
• udaymaster@gmail.com

ALGIERS
MANE ABD ELAZIZ, CITE 18 LOGEMENTS BLOC - 81, N°3,
CILLE DE REHMANIA, ZERALDA ALGIERS.
PHONE NO 00213-071076049
• EMAIL ADD : udaymasteralgeria@gmail.com