


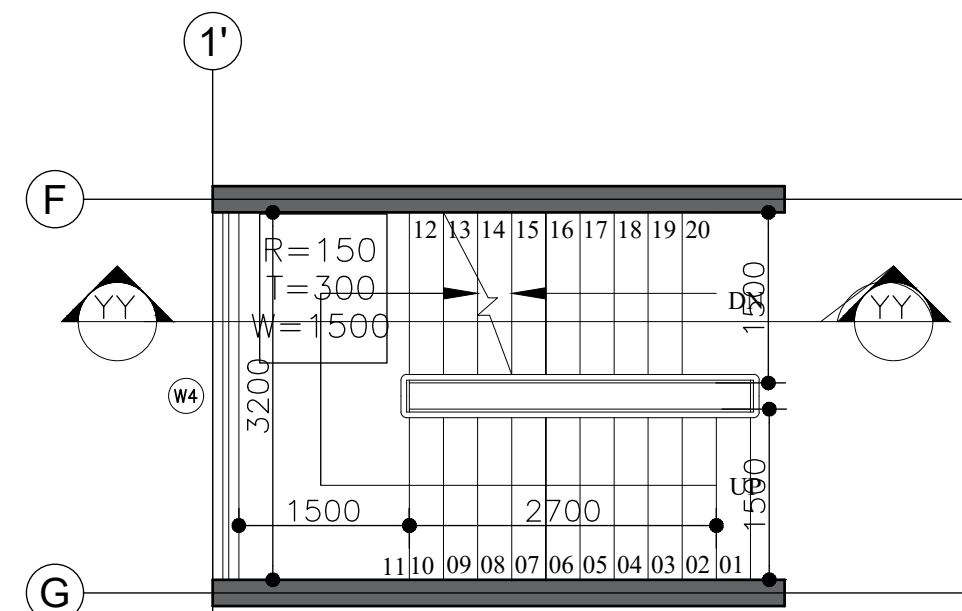


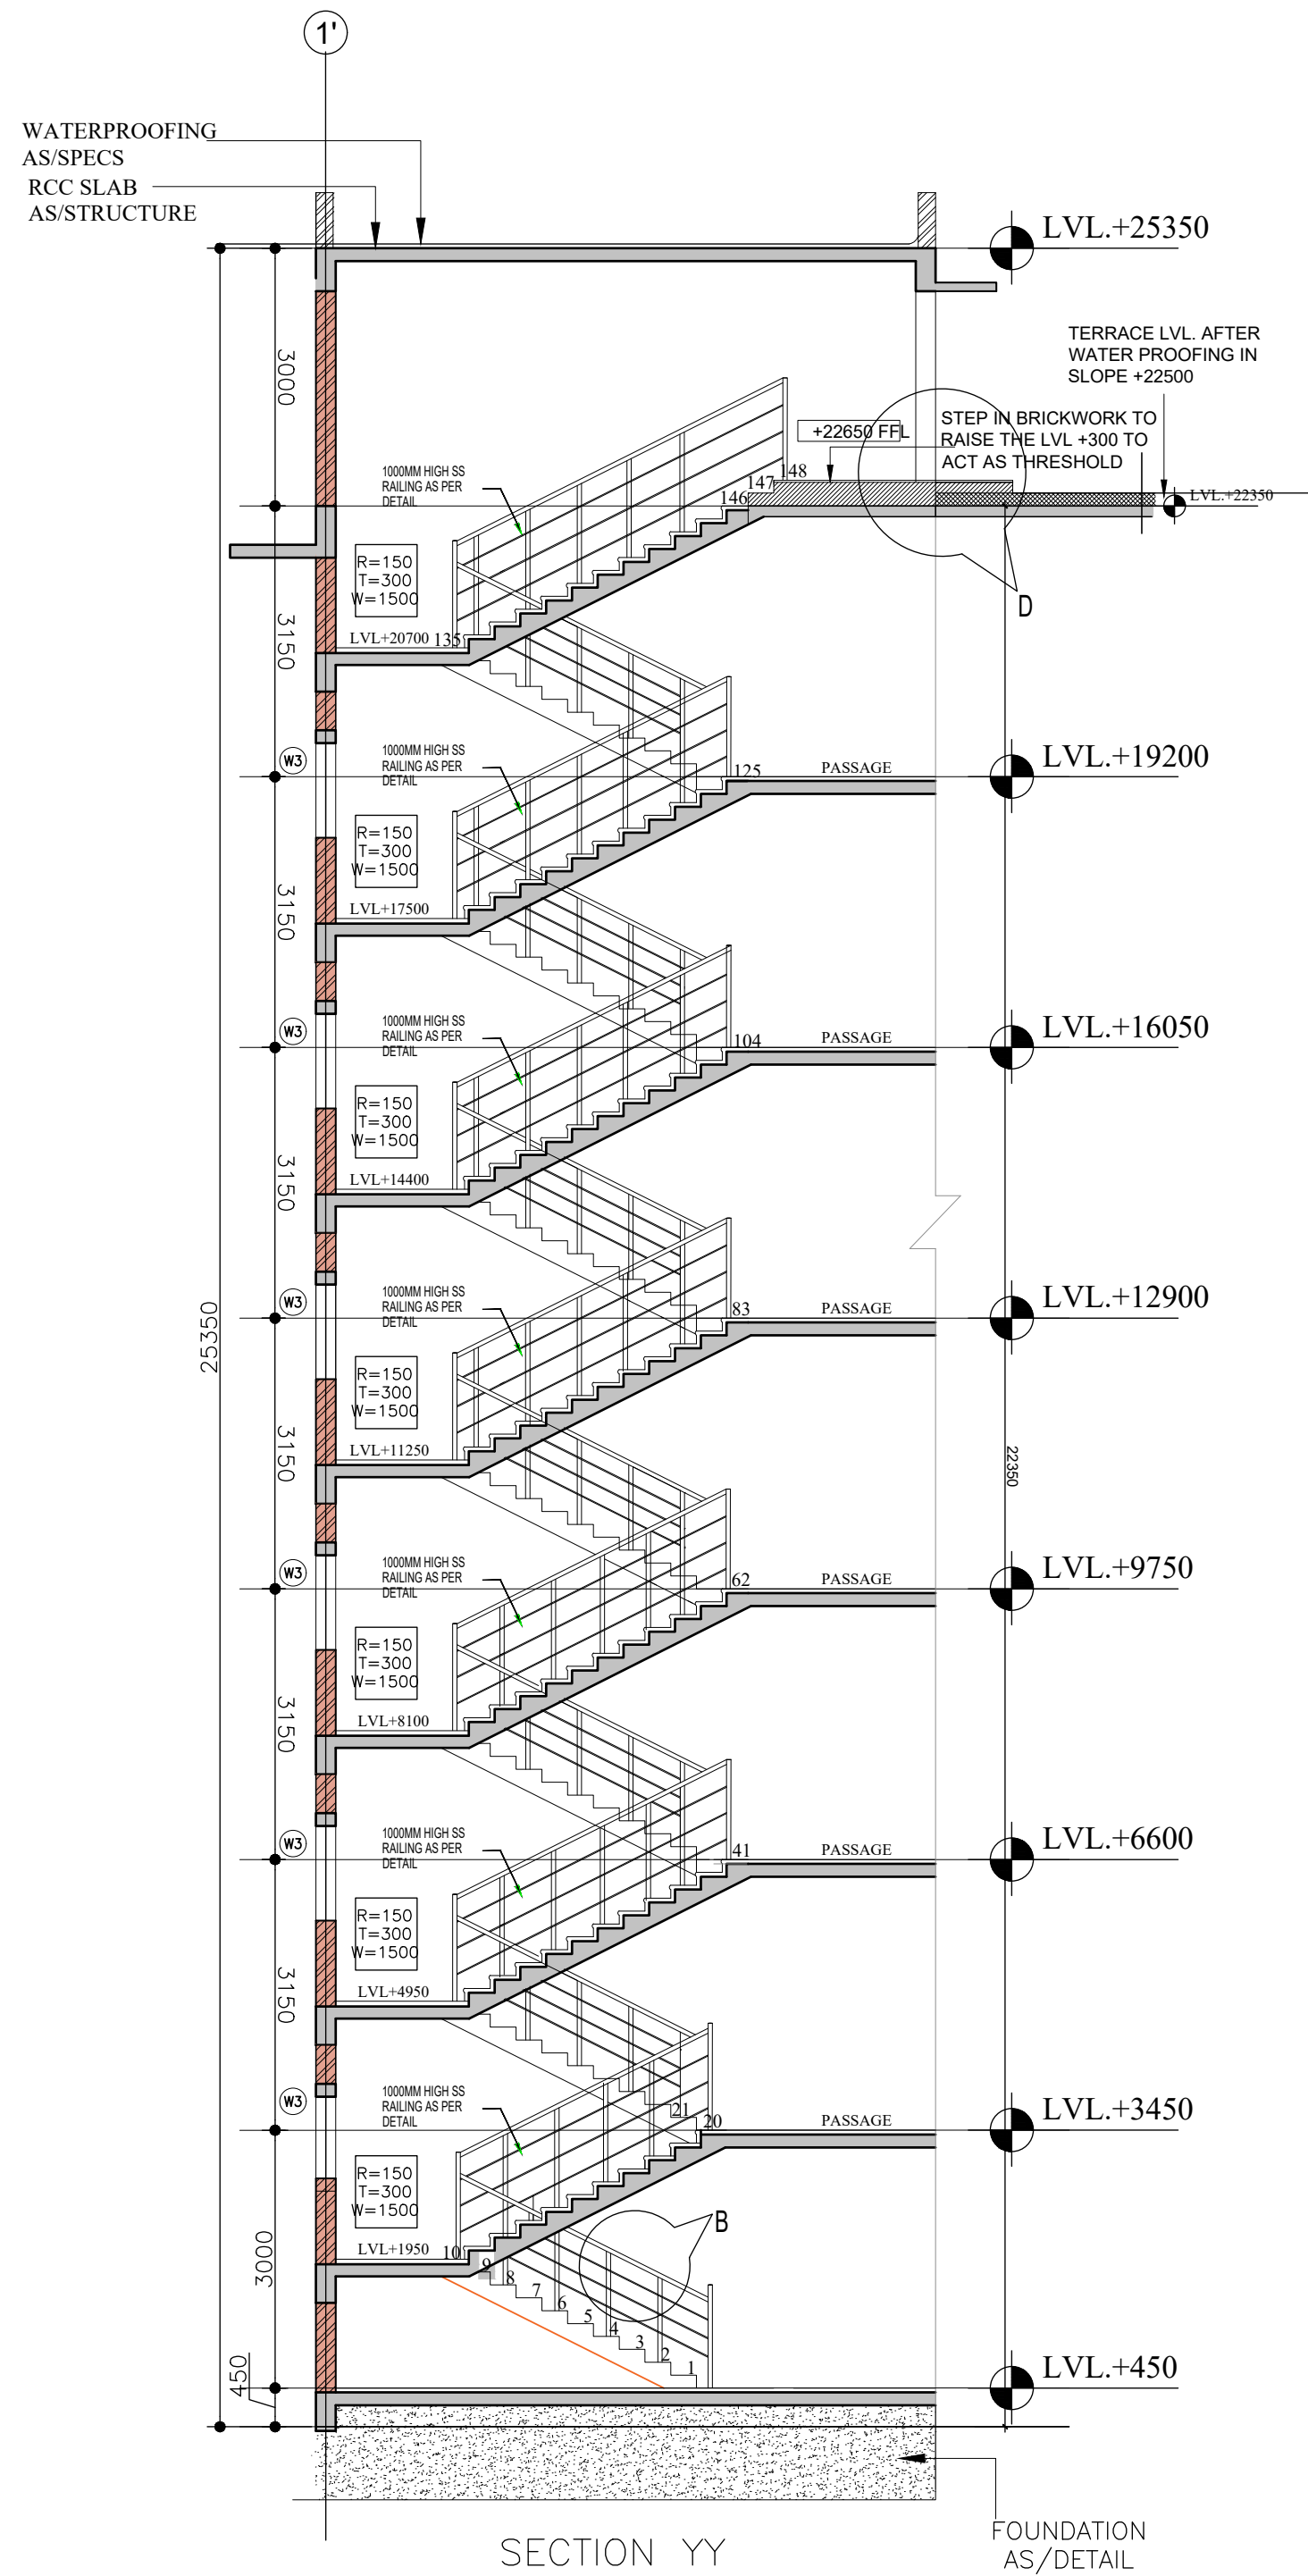


TYPICAL STAIRCASE PLAN AT GROUND
FLOOR

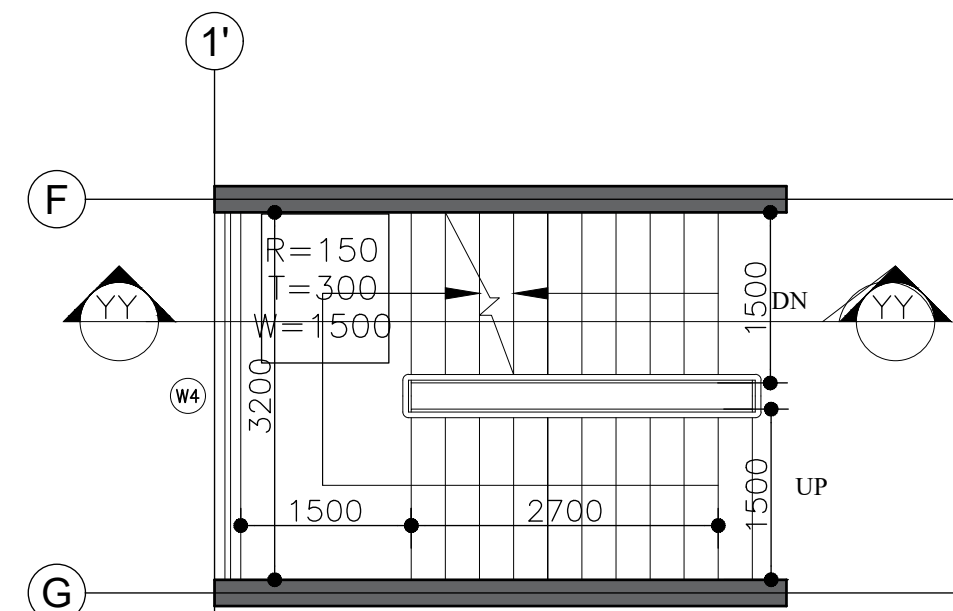


STAIRCASE PLAN AT TYPICAL FLOOR

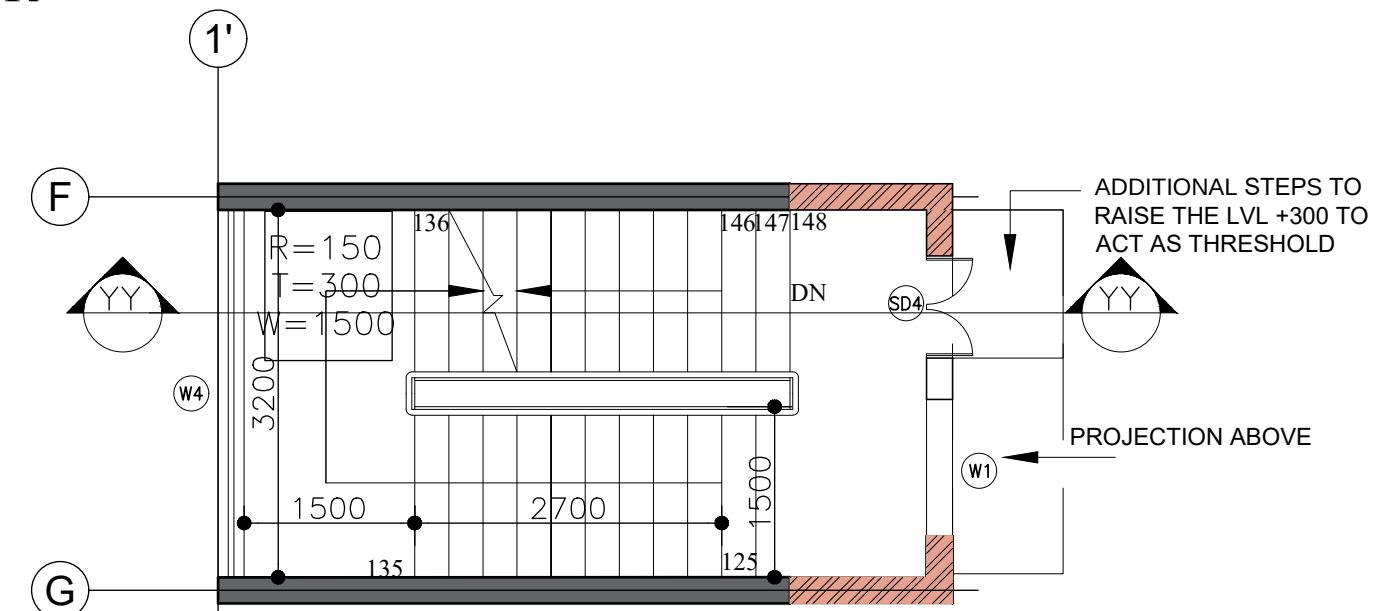


STAIRCASE PLAN AT SIXTH FLOOR

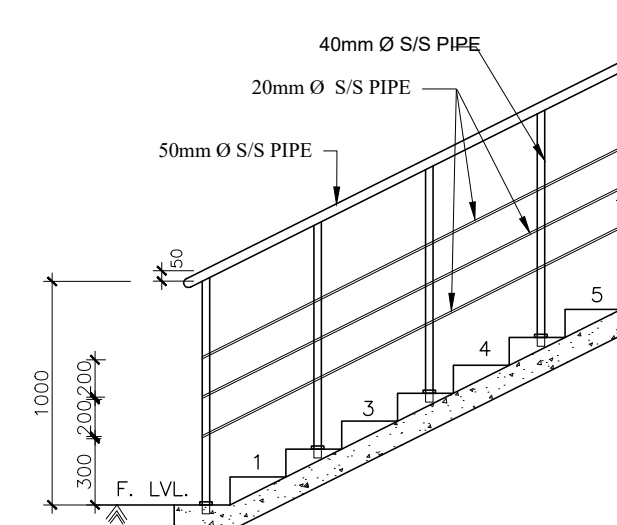

STAIRCASE RAILING DETAIL

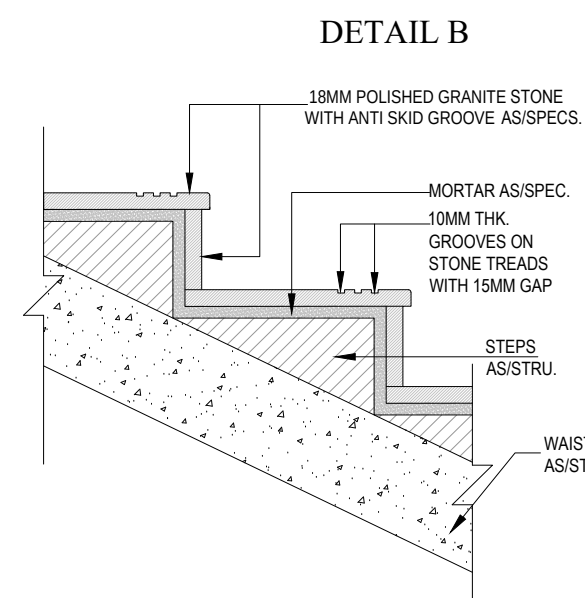

STAIRCASE DETAIL

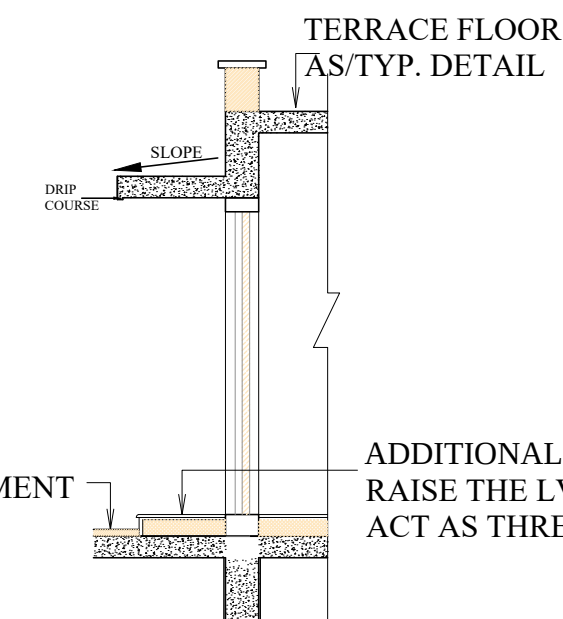

ROOF TREATMENT
AS/SPECS

ADDITIONAL STEPS TO
RAISE THE LVL +300 TO
ACT AS THRESHOLD

DETAIL D

NOTES

1. ALL DIMENSIONS ARE IN MM; UNLESS NOTED OTHERWISE.
2. WRITTEN DIMENSIONS ARE TO BE FOLLOWED. DRAWINGS ARE NOT TO BE SCALED.
3. ANY DISCREPANCY IN THE DRAWING SHALL BE BROUGHT TO THE NOTICE OF THE ENGINEER.
4. THIS DRAWING SHALL BE READ IN CONJUNCTION WITH OTHER RELEVANT DRAWINGS.

TENDER DRAWING

CLIENT
OIL INDIA LIMITED
(A Govt. of India Enterprise)

CONSULTANT
IRITES
THE INFRASTRUCTURE PEOPLE
(A Govt. of India Enterprise)

PROJECT
BQ WORKMEN HOUSING





BUILDING
HOUSING BLOCK (G+6)

DRAWING TITLE
TYPICAL STAIRCASE DETAIL

DRG. NO.
BITES/BLD/AR/TD/022

NORTH

SCALE
NTS
DATE
JULY 2025

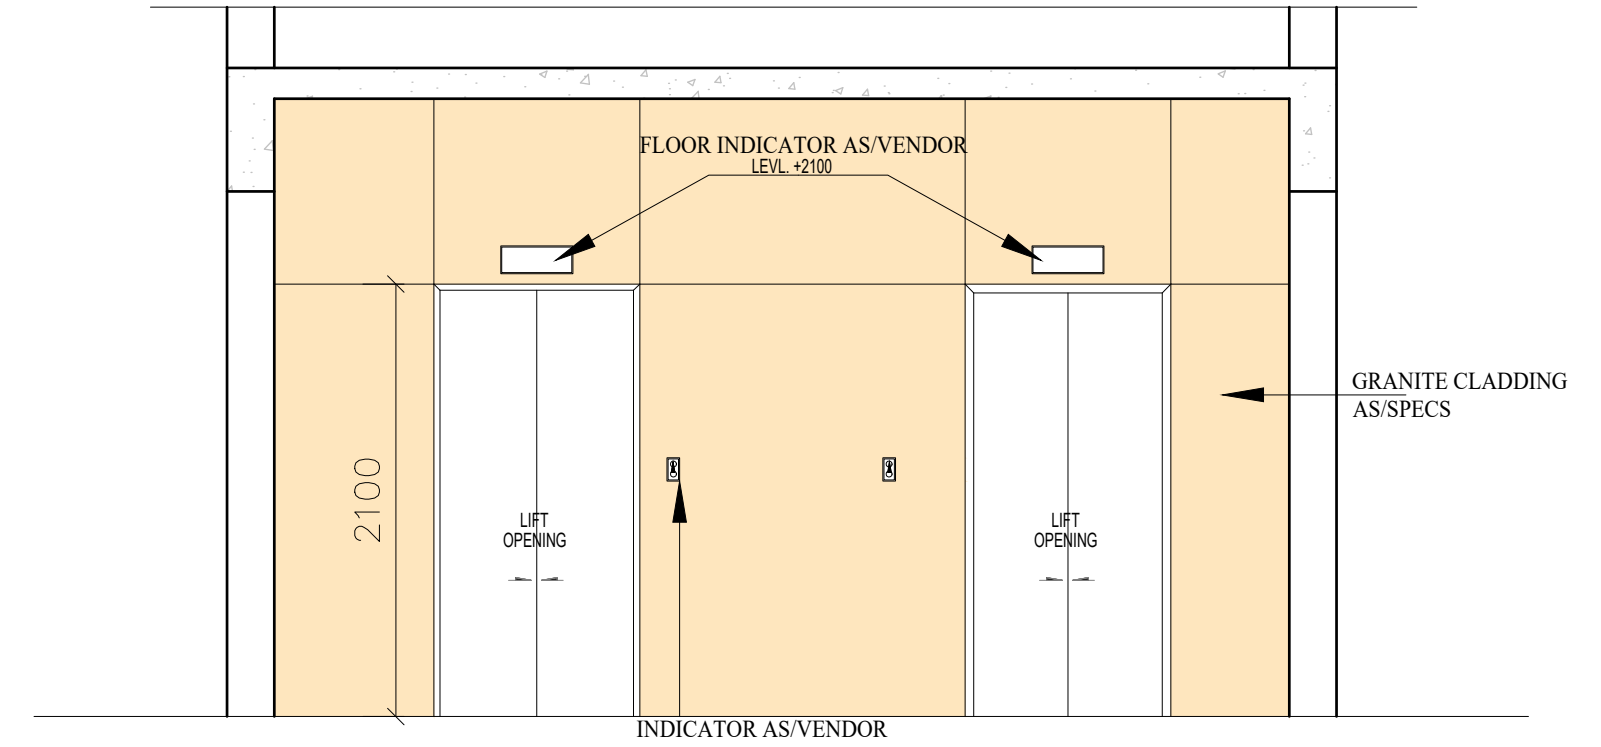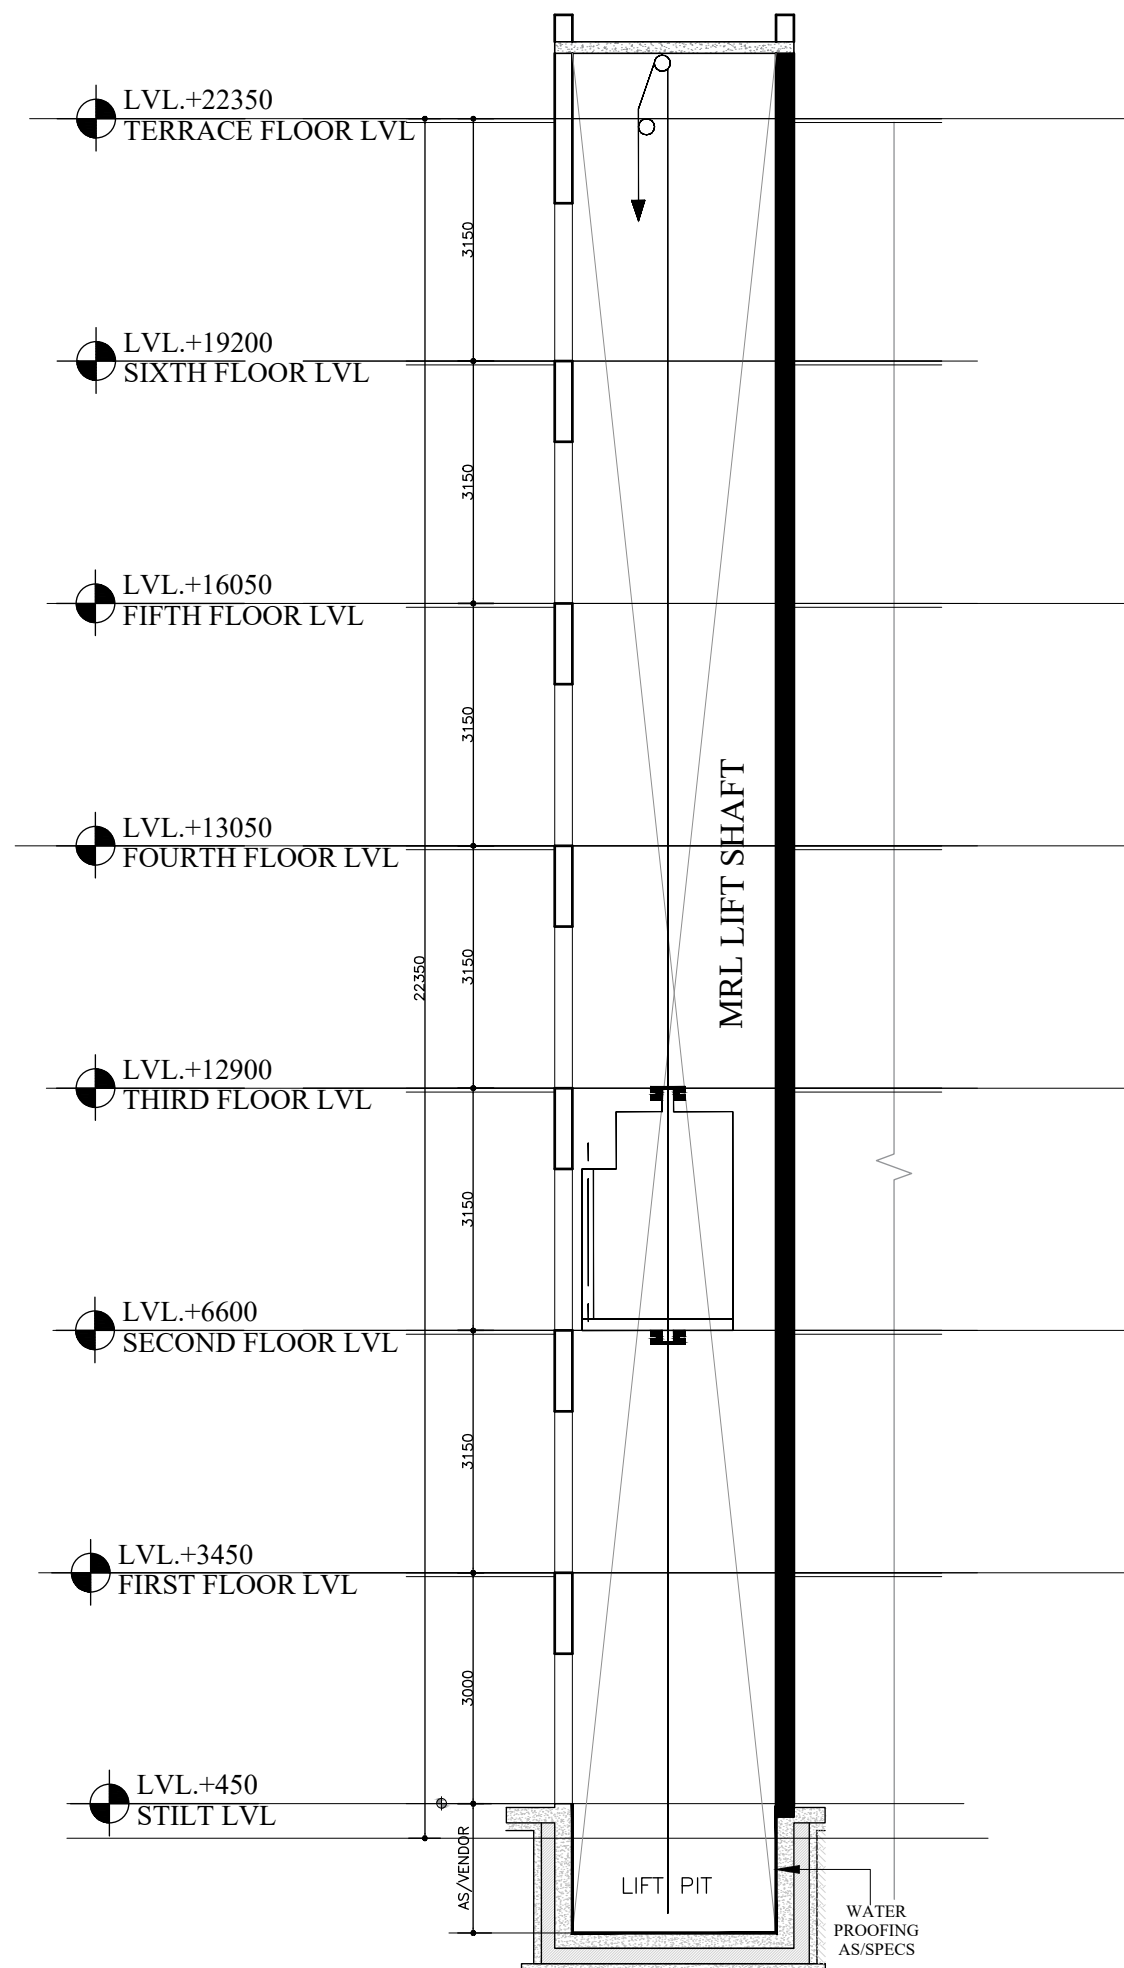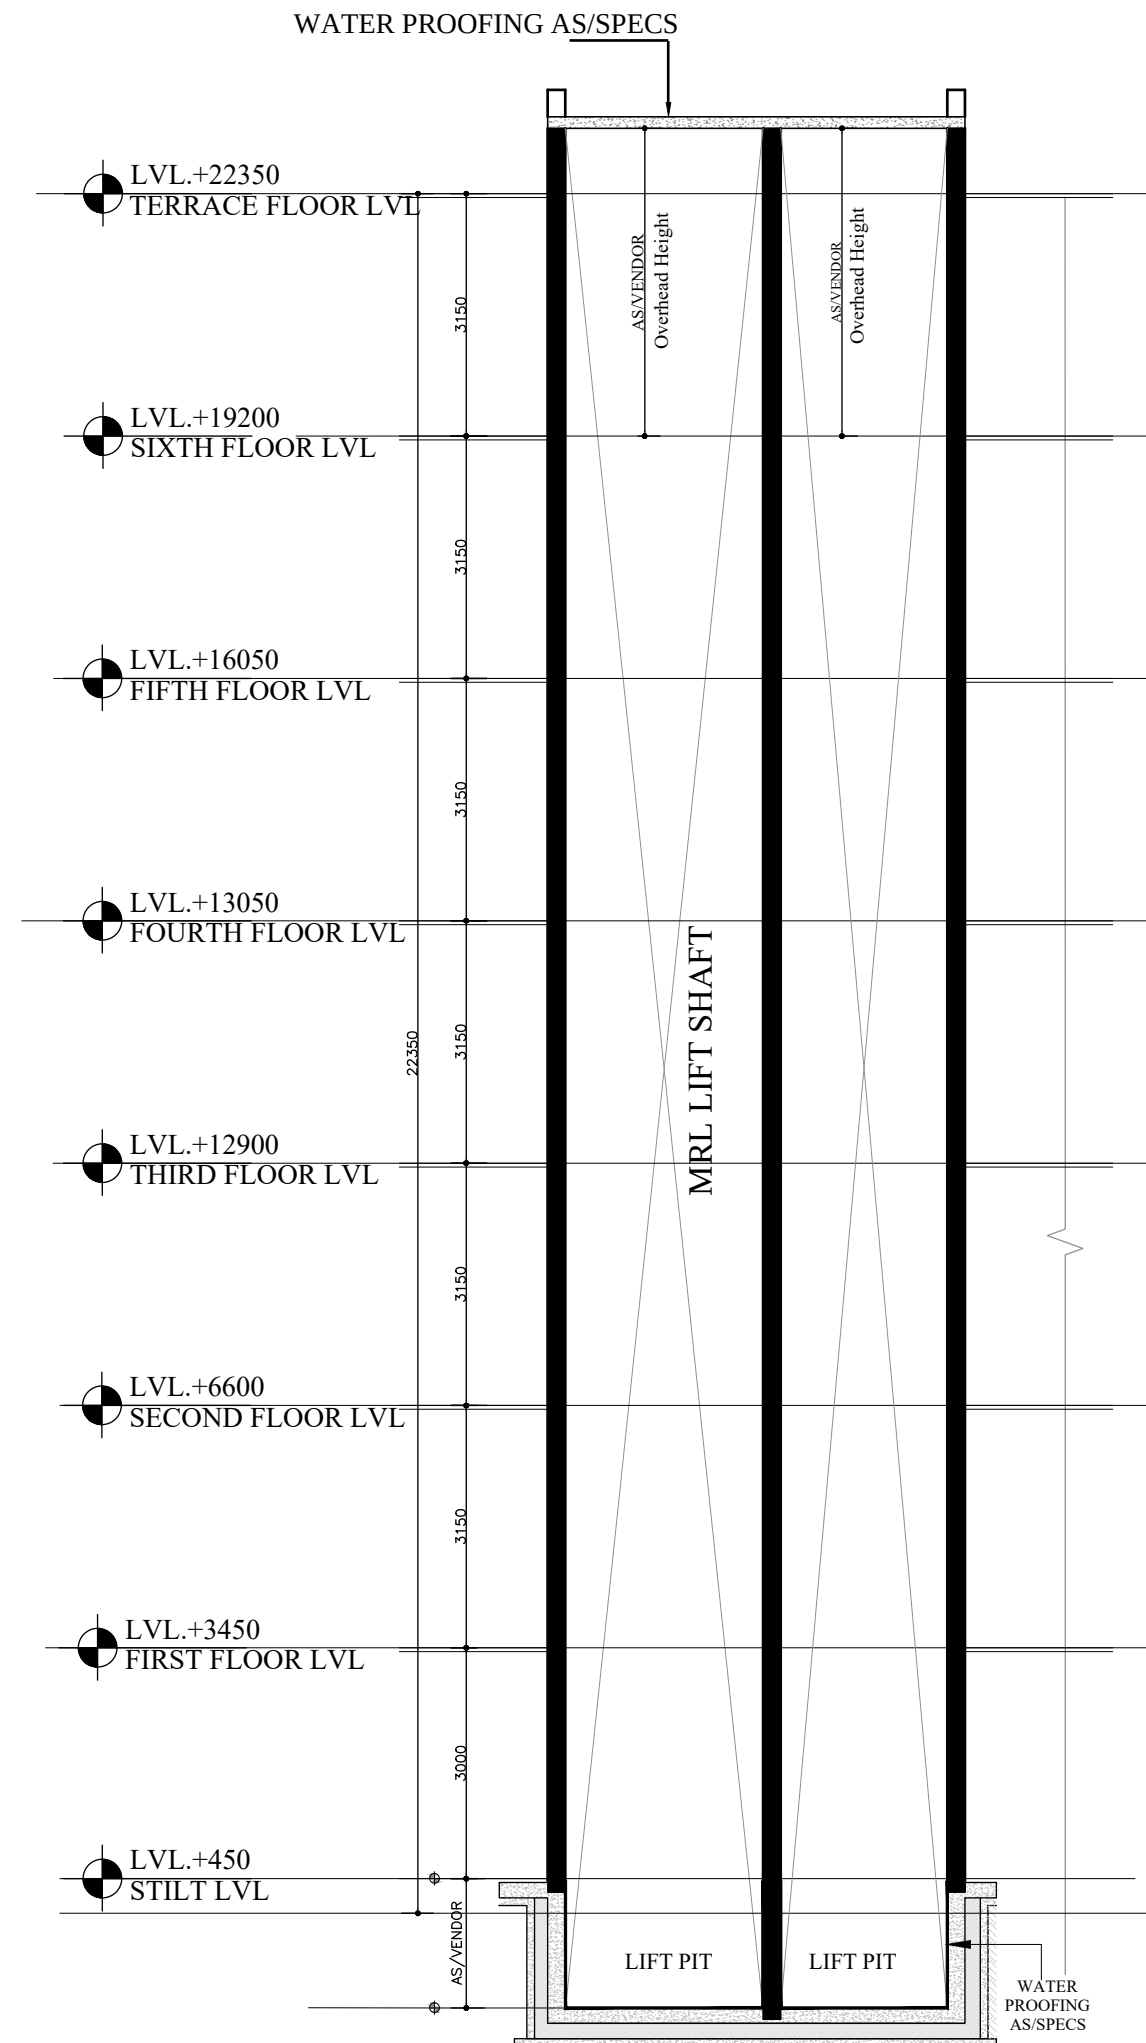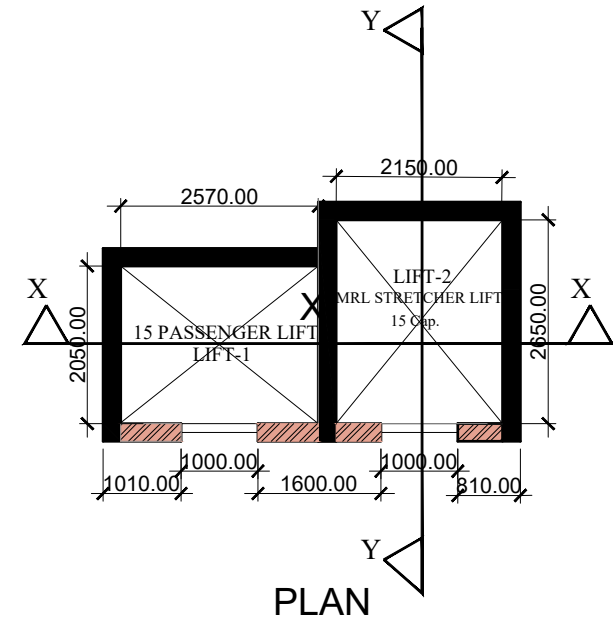

NOTES

1. ALL DIMENSIONS ARE IN MM; UNLESS NOTED OTHERWISE.
2. WRITTEN DIMENSIONS ARE TO BE FOLLOWED. DRAWINGS ARE NOT TO BE SCALED.
3. ANY DISCREPANCY IN THE DRAWING SHALL BE BROUGHT TO THE NOTICE OF THE ENGINEER.
4. THIS DRAWING SHALL BE READ IN CONJUNCTION WITH OTHER RELEVANT DRAWINGS.
5. SHAFT SIZES ARE TAKEN FROM NBC 2016 FOR MRL LIFTS
6. THE DRAWING IS INDICATIVE ONLY.
6. SHOP DRAWING TO BE PREPARED FOR APPROVAL.

TENDER DRAWING

CLIENT  **OIL INDIA LIMITED**
(A Govt. of India Enterprise)


CONSULTANT  **IRITES**
THE INFRASTRUCTURE PEOPLE
(A Govt. of India Enterprise)





PROJECT **BQ WORKMEN HOUSING**

BUILDING **HOUSING BLOCK (G+6)**

DRAWING TITLE **TYPICAL LIFT DETAIL**








DRG. NO. **MITES/BLD/AR/TD/023**

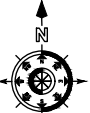NORTH 	SCALE NTS	DATE JULY 2025
---	---------------------	--------------------------

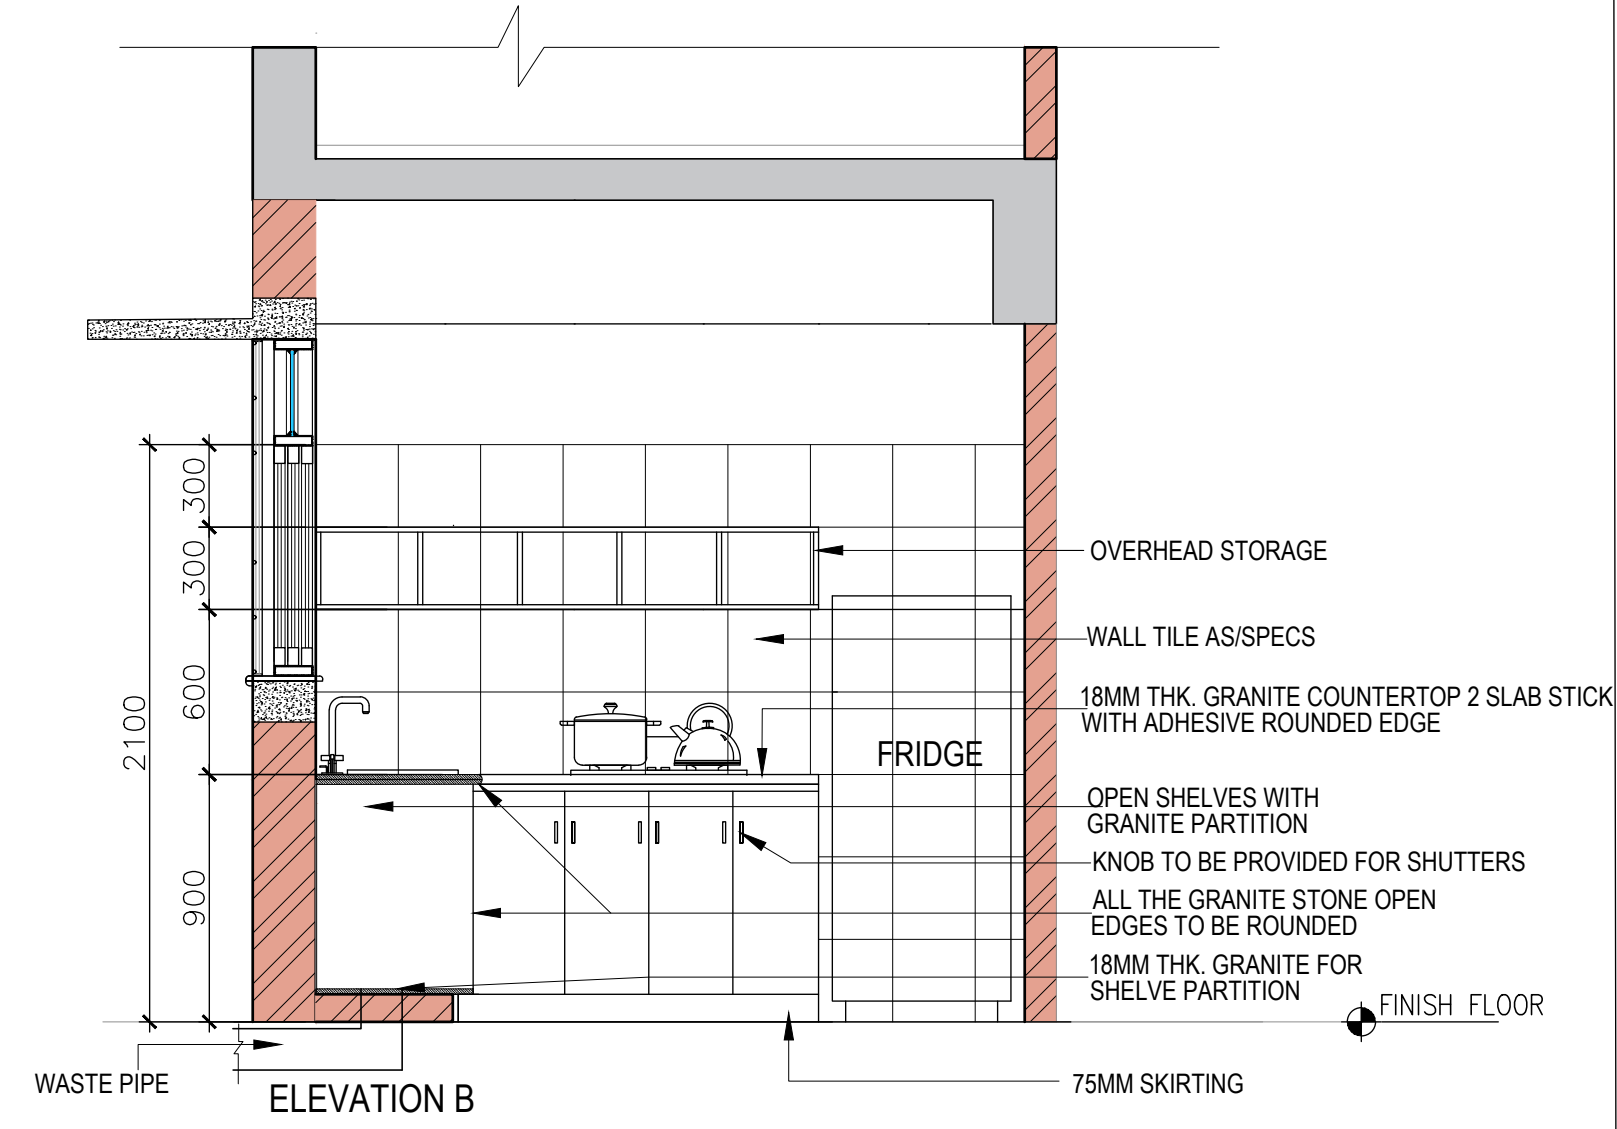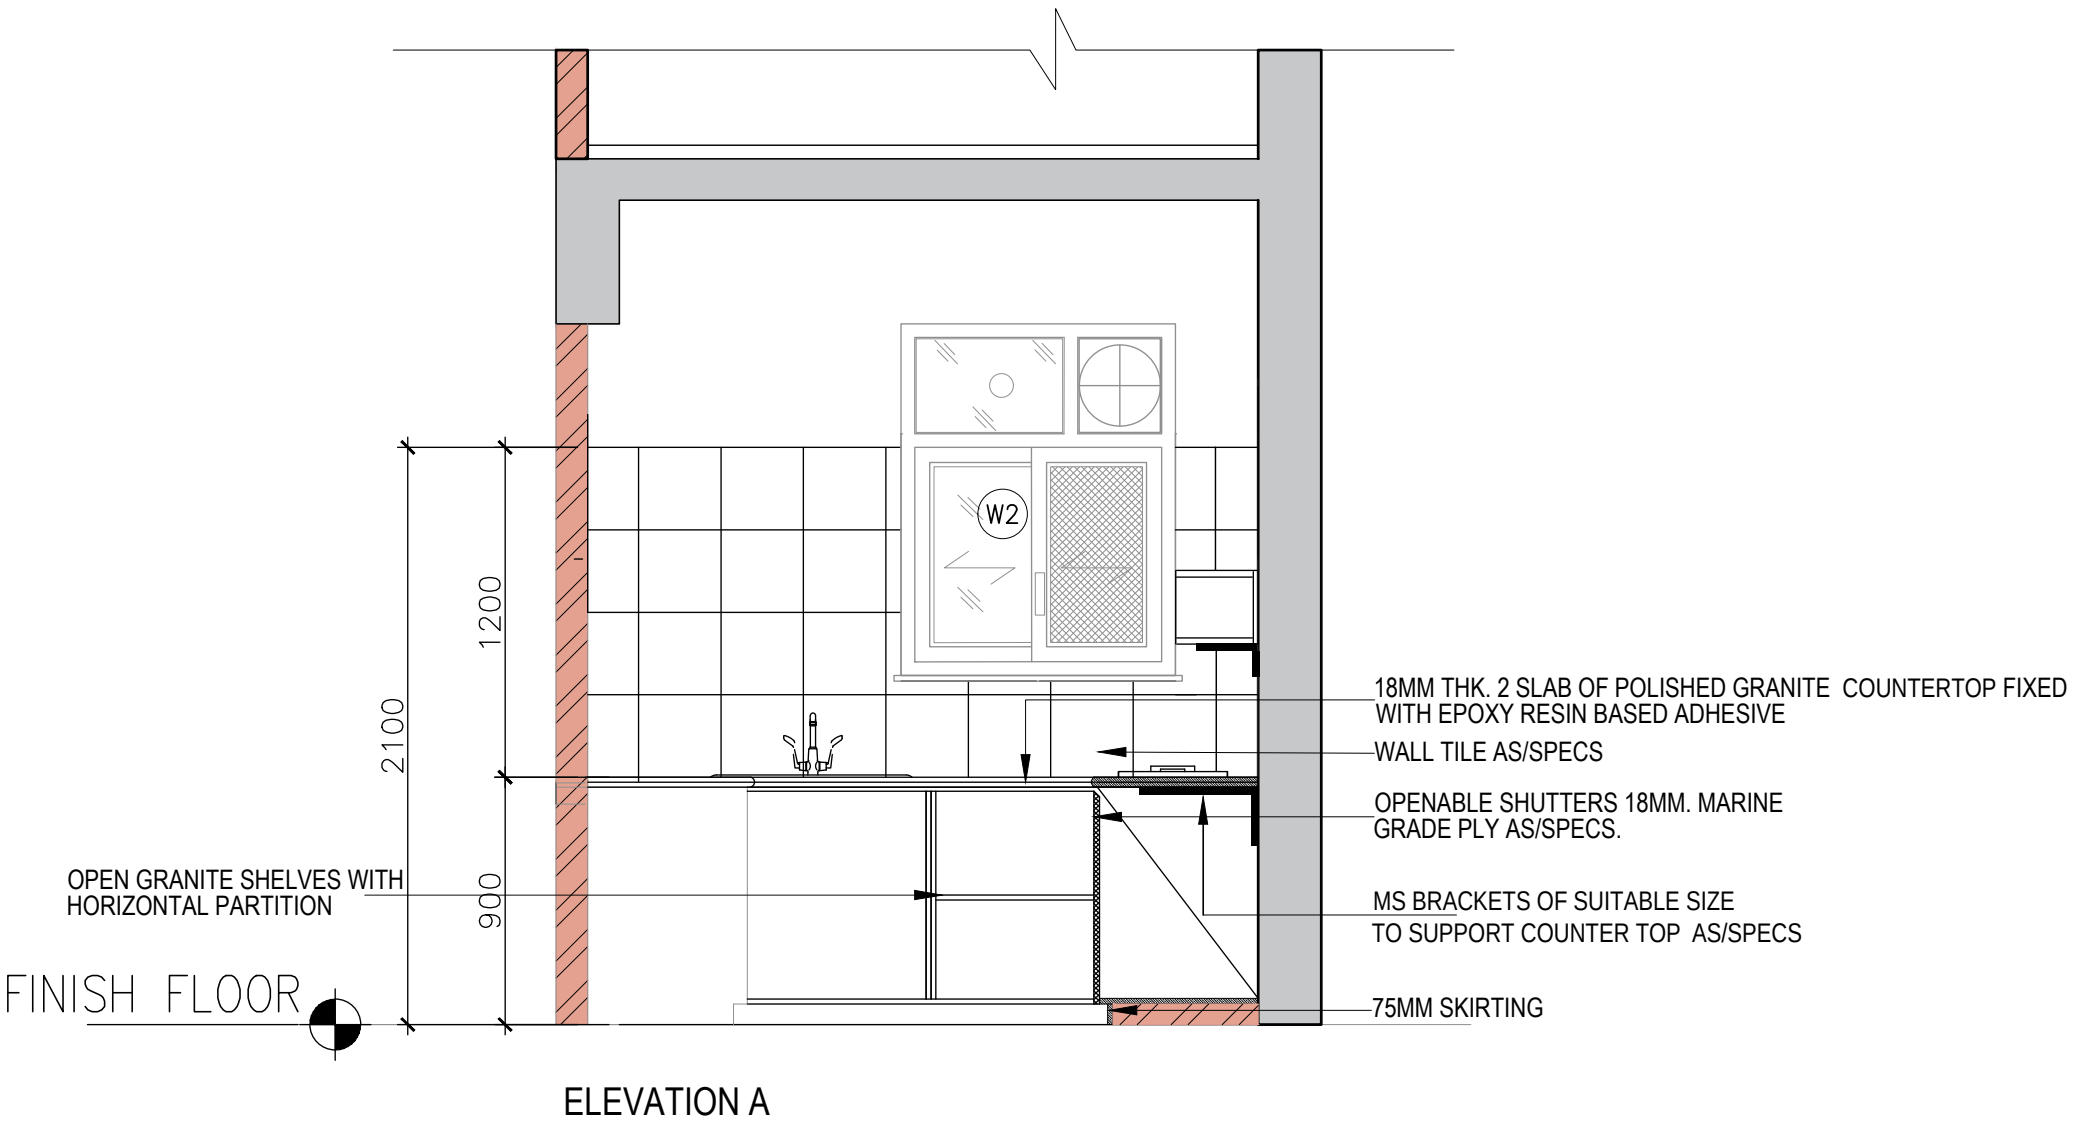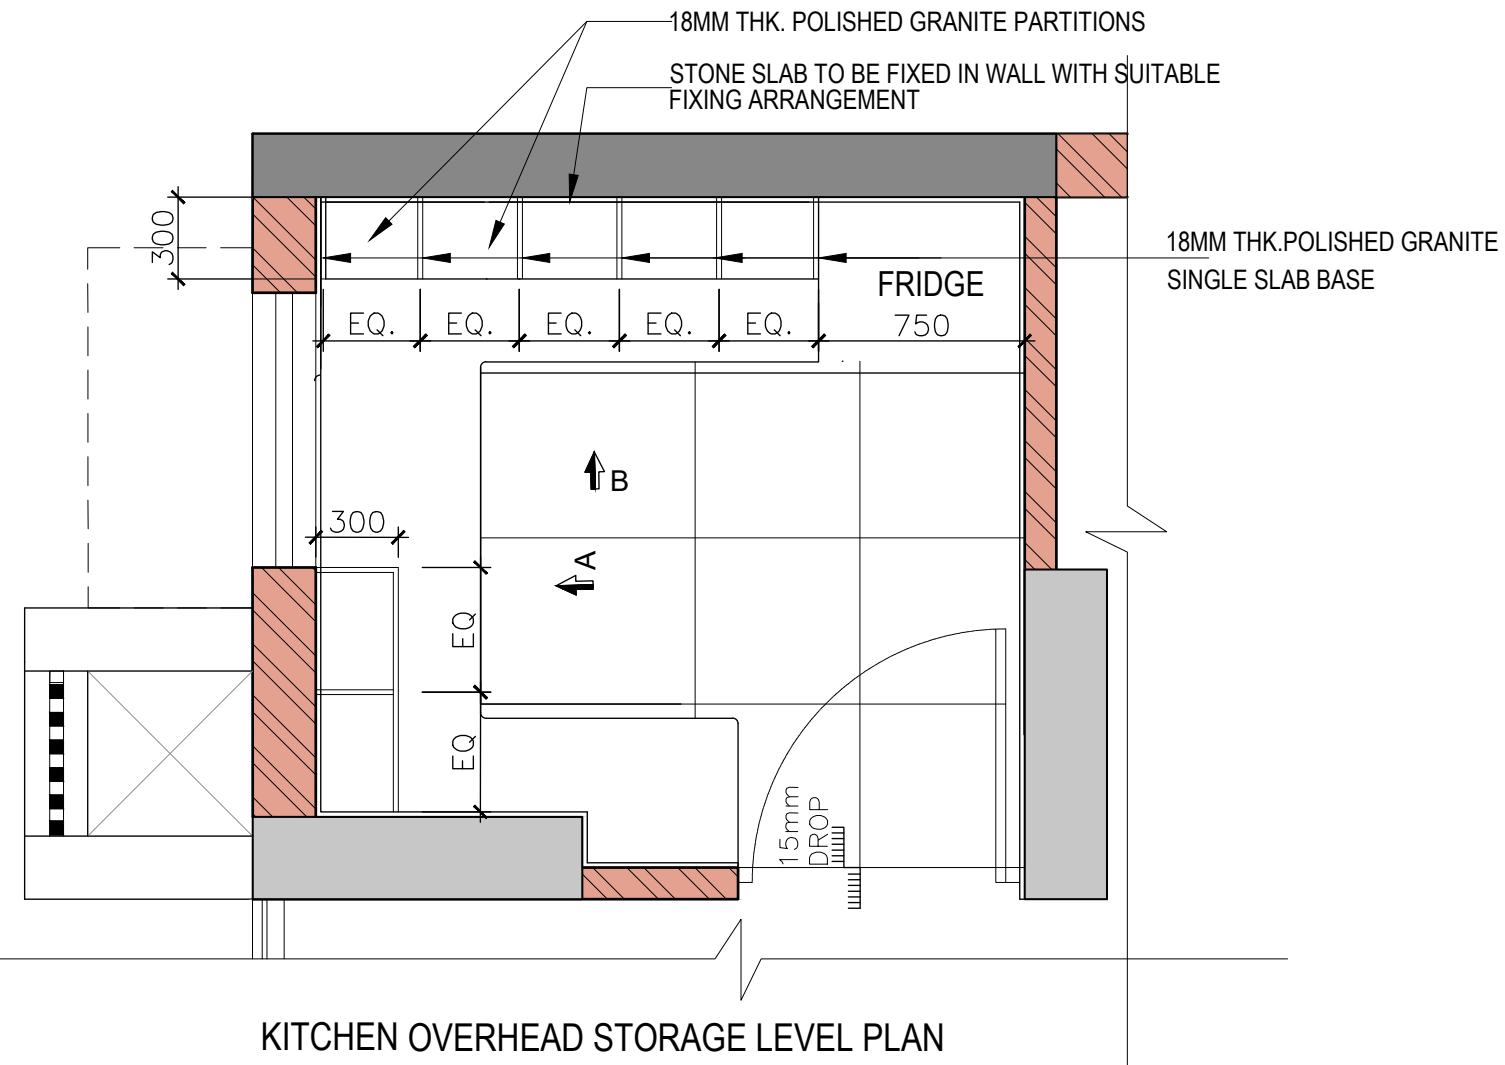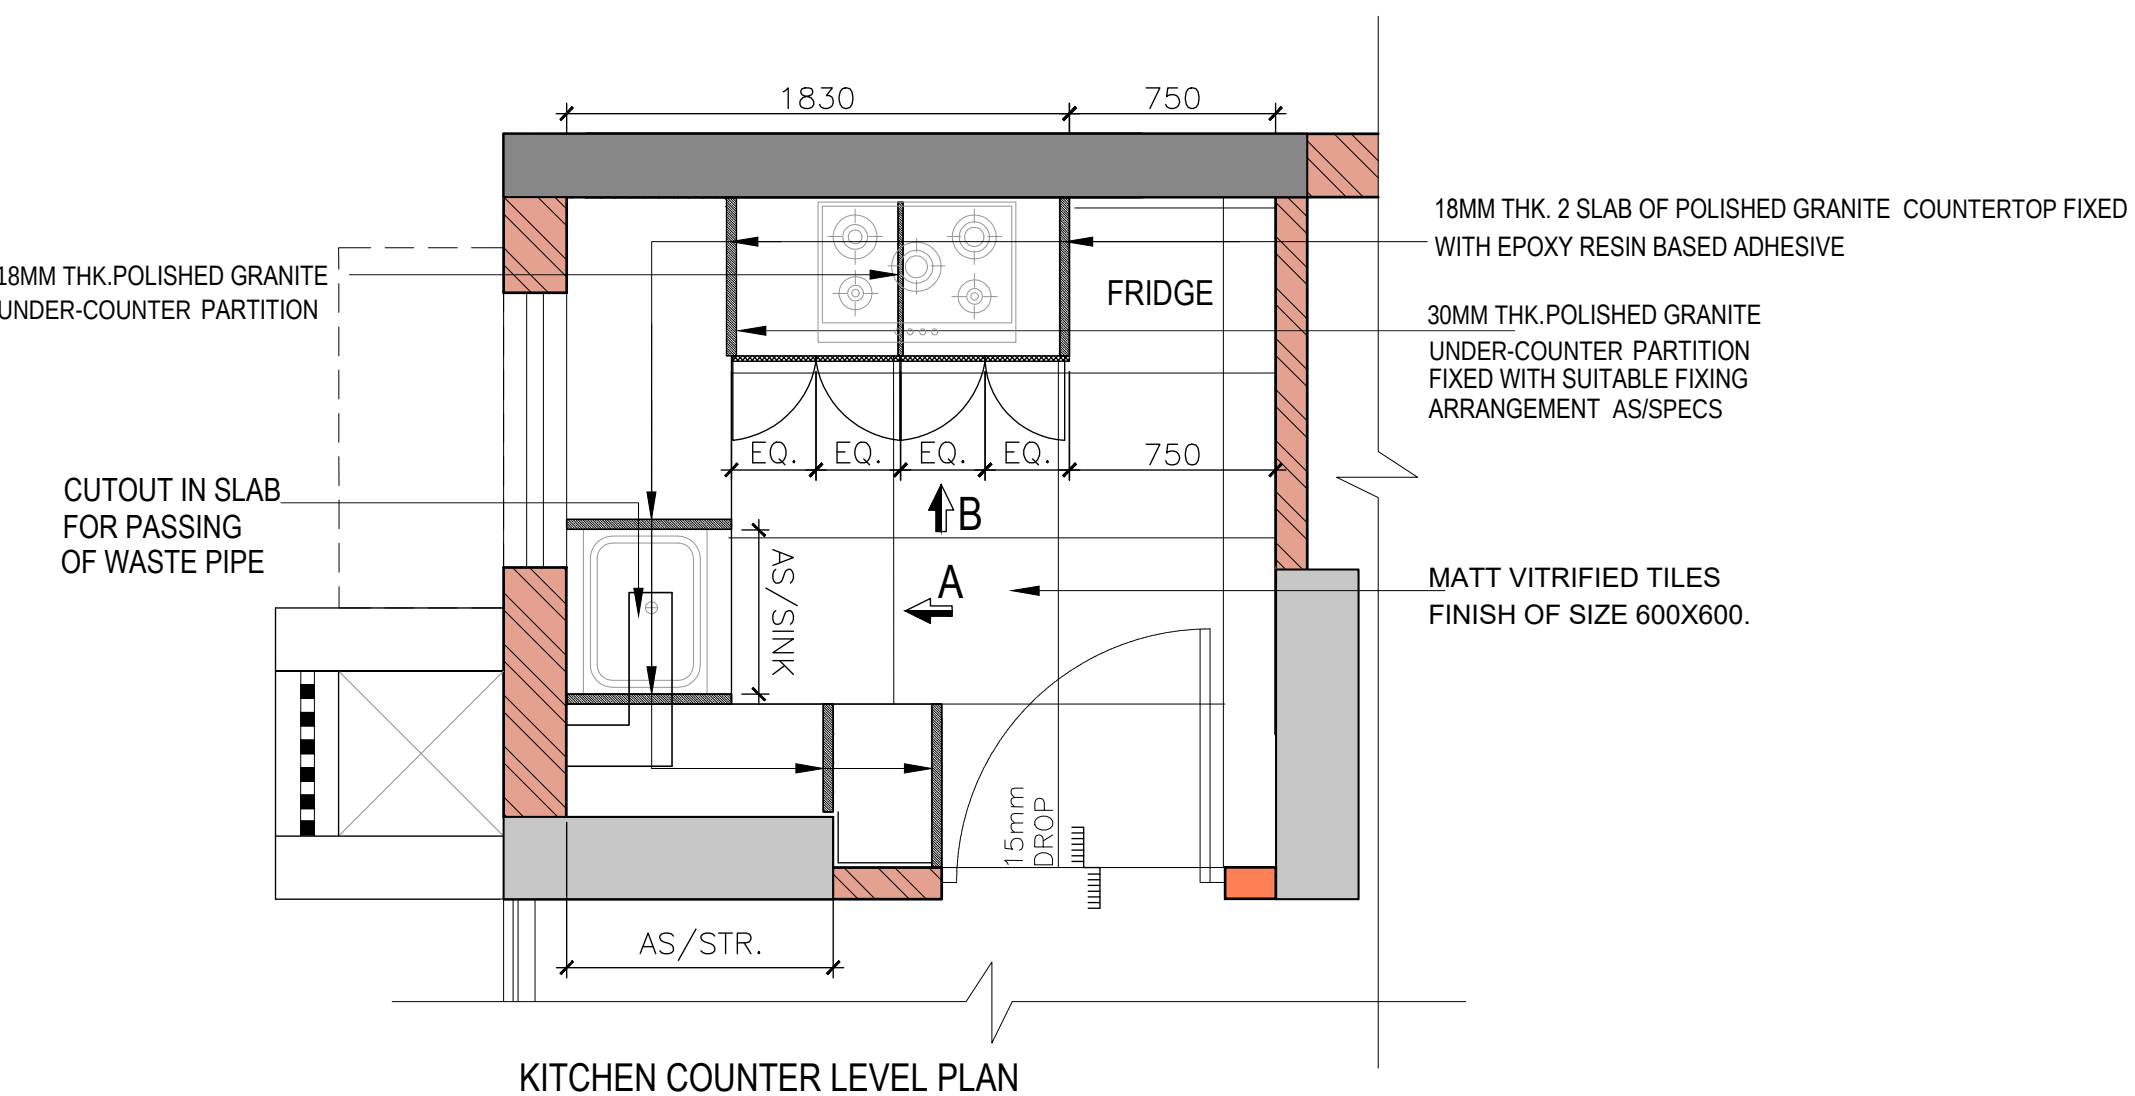

- NOTES
1. ALL DIMENSIONS ARE IN MM; UNLESS NOTED OTHERWISE.
 2. WRITTEN DIMENSIONS ARE TO BE FOLLOWED. DRAWINGS ARE NOT TO BE SCALED.
 3. ANY DISCREPANCY IN THE DRAWING SHALL BE BROUGHT TO THE NOTICE OF THE ENGINEER.
 4. THIS DRAWING SHALL BE READ IN CONJUNCTION WITH OTHER RELEVANT DRAWINGS.
 5. REFER SPECIFICATION AND SCHEDULE OF FINISH

TENDER DRAWING		
CLIENT	 OIL INDIA LIMITED (A Govt. of India Enterprise)	
CONSULTANT	 IRITES THE INFRASTRUCTURE PEOPLE (A Govt. of India Enterprise)	
PROJECT	BQ WORKMEN HOUSING	
BUILDING	HOUSING BLOCK (G+6)	
DRAWING TITLE	TYPICAL KITCHEN DETAIL	
DRG. NO.	RITES/BLD/AR/TD/024	
NORTH	SCALE	DATE
	NTS	JULY 2025

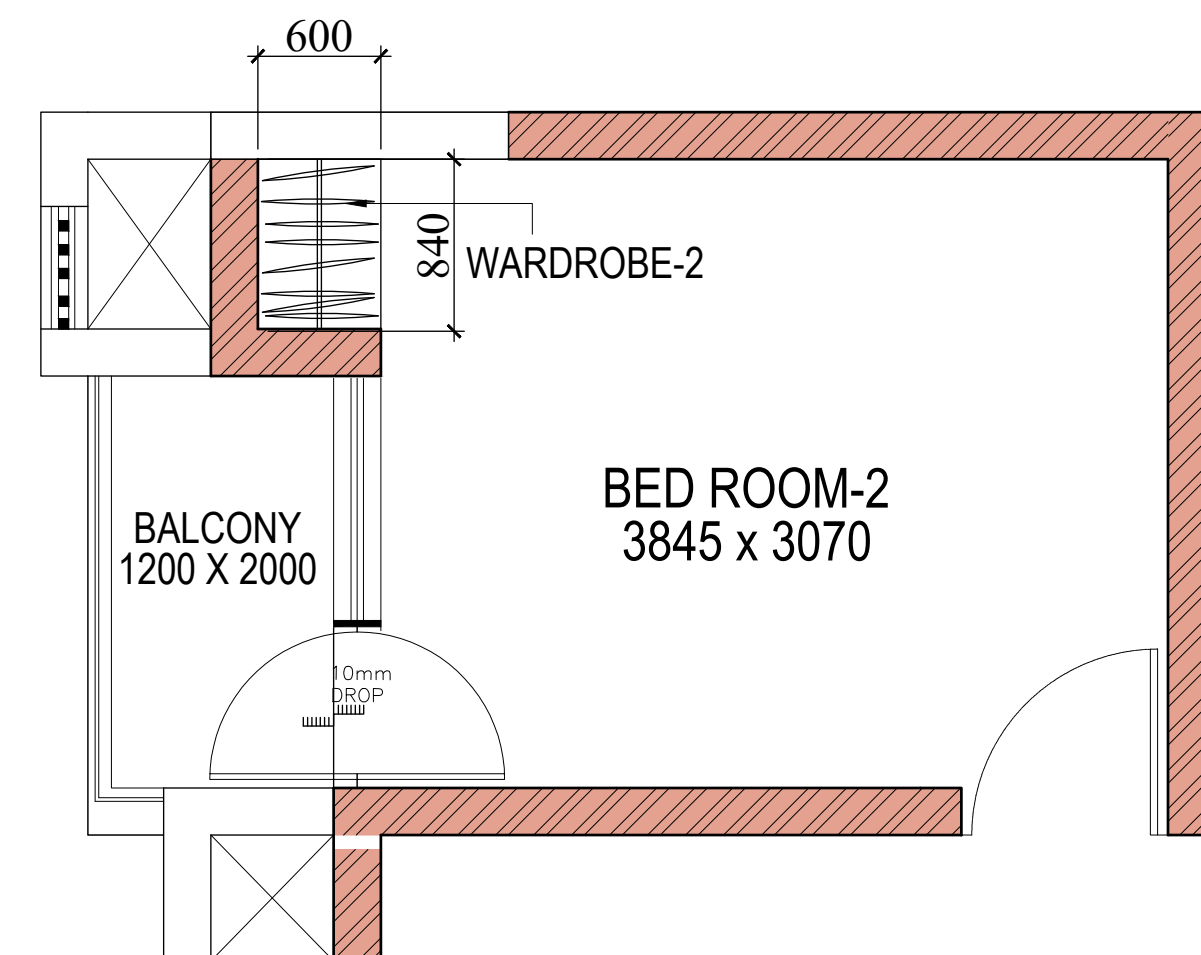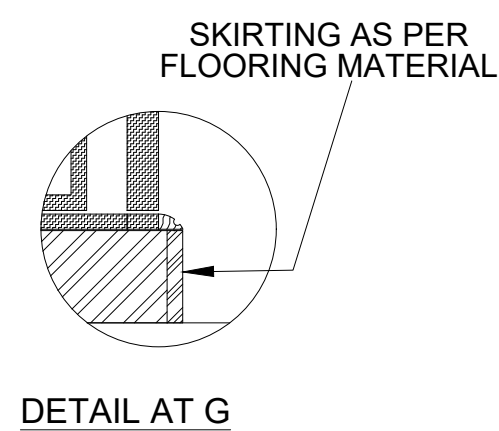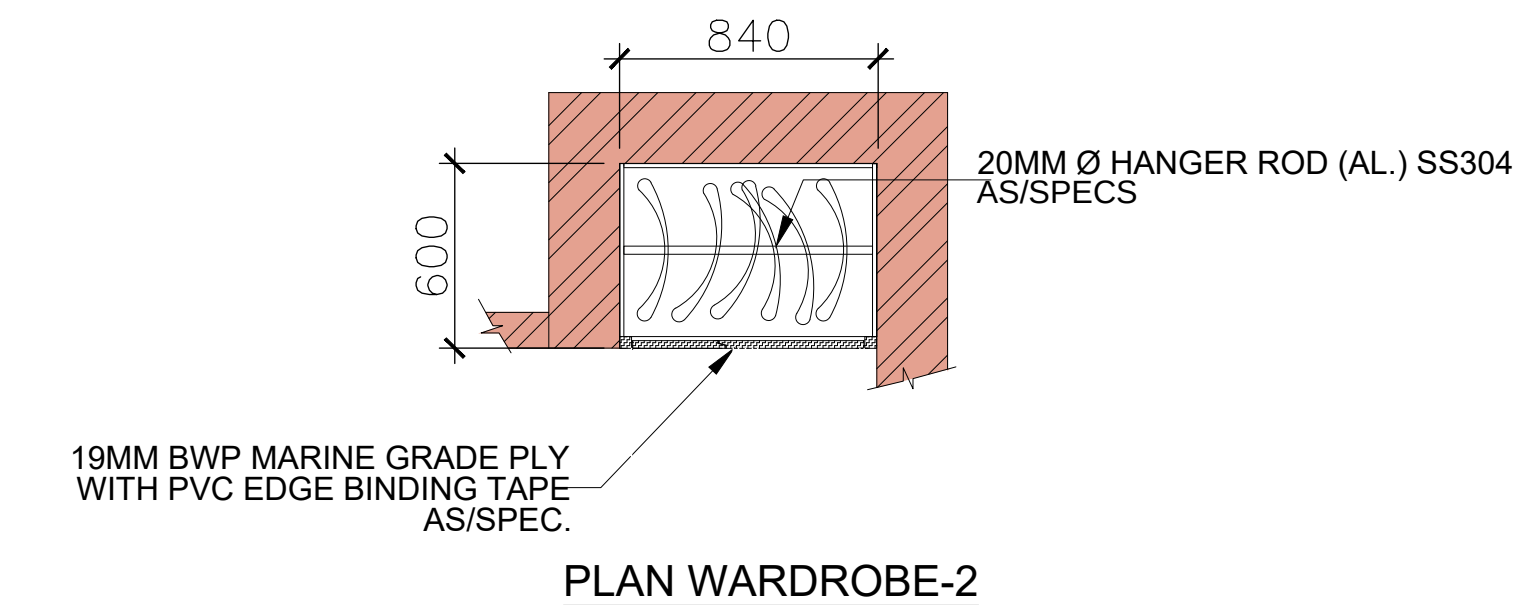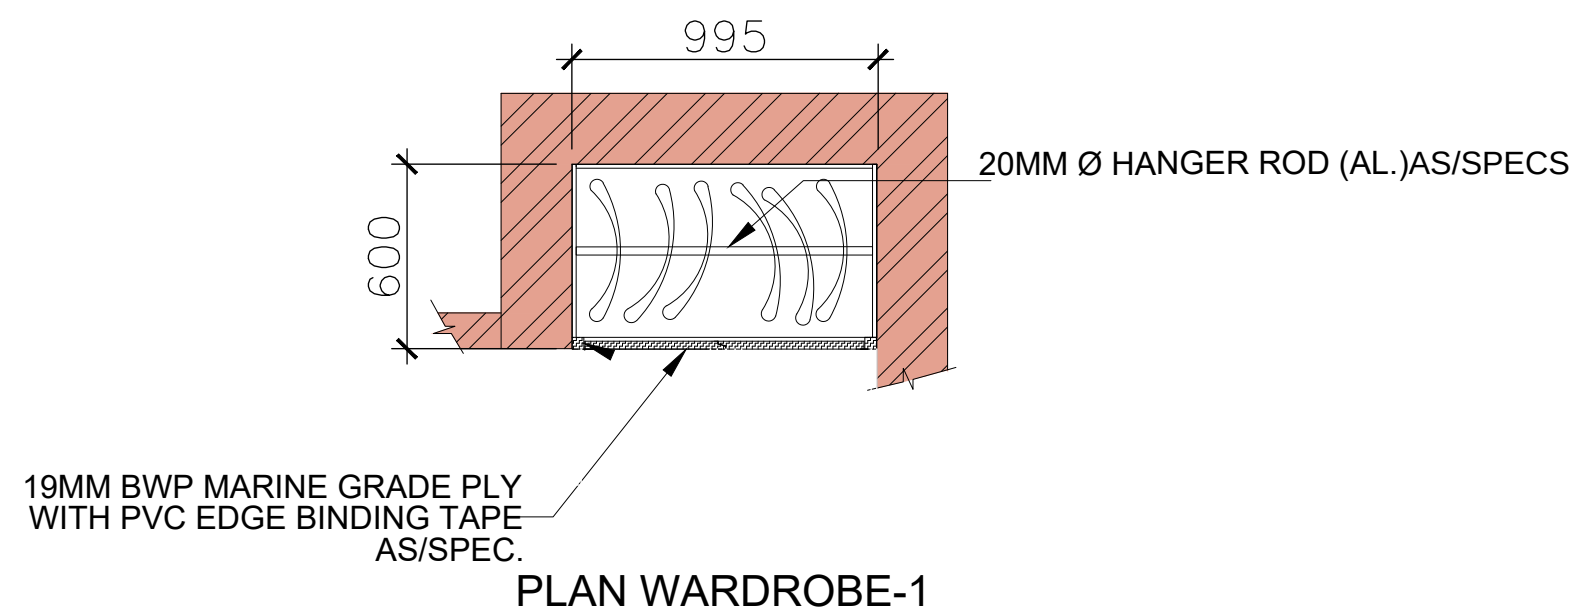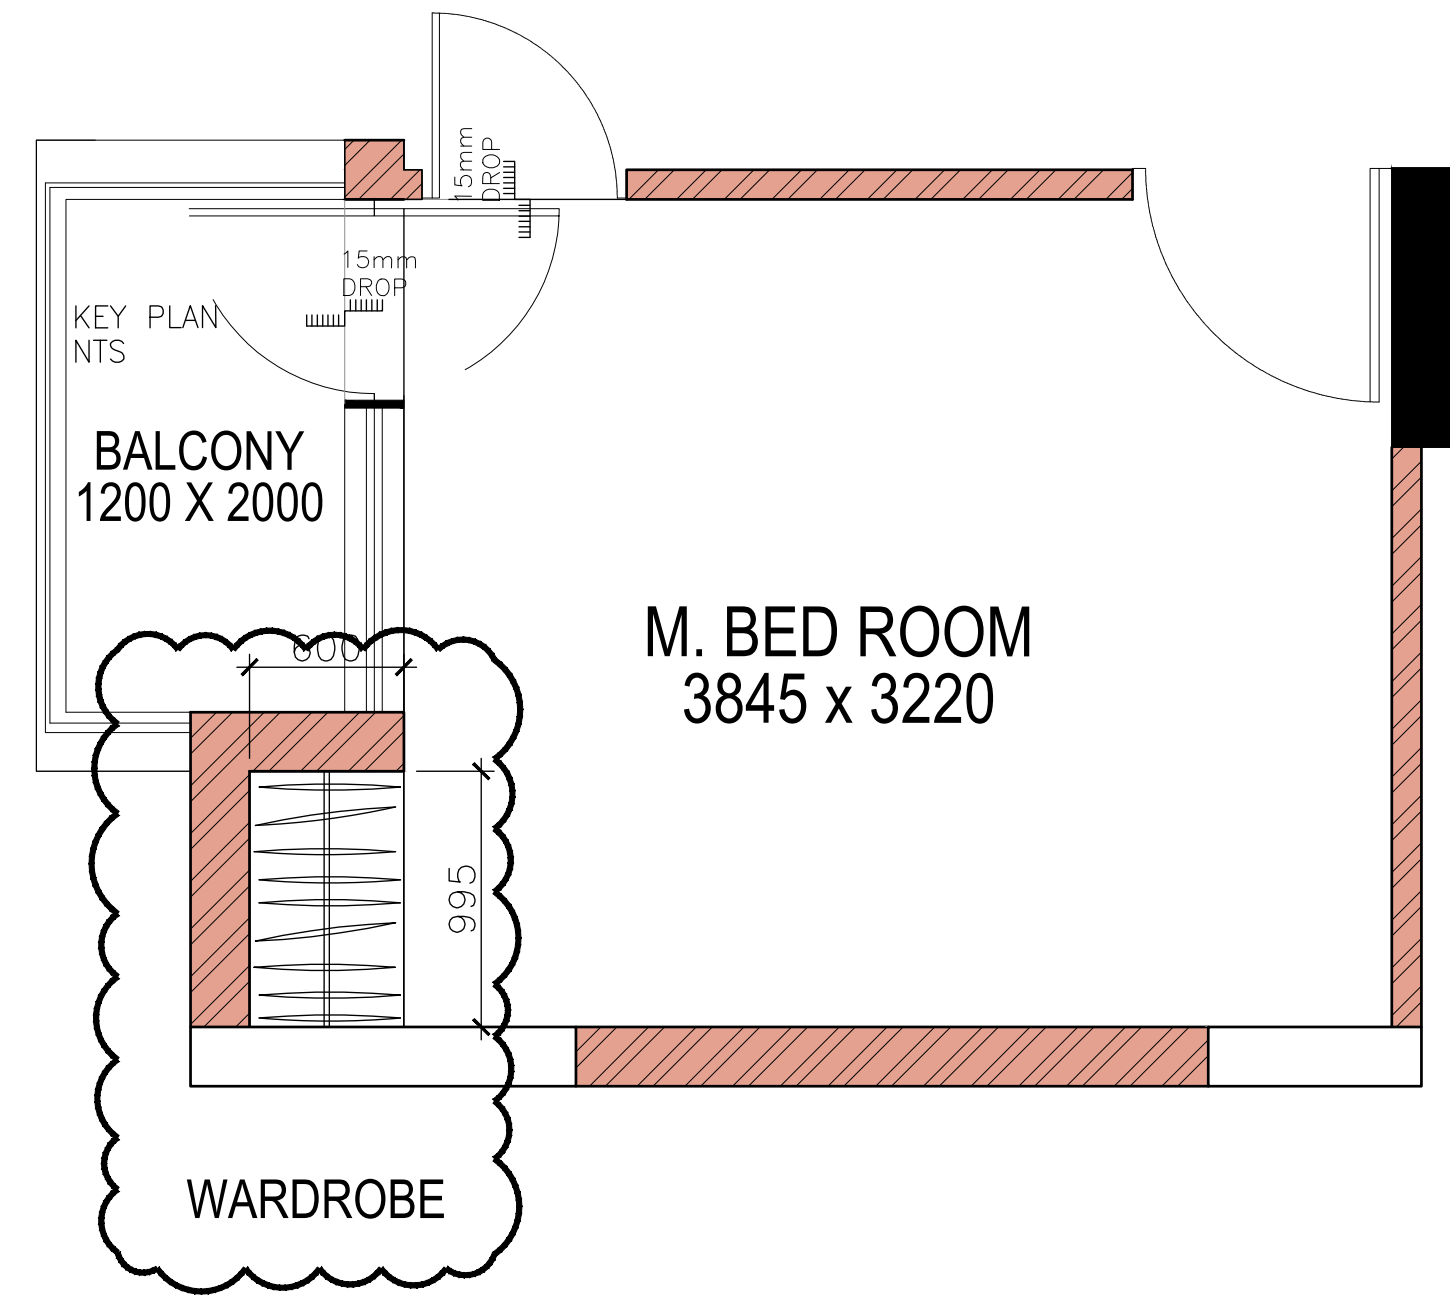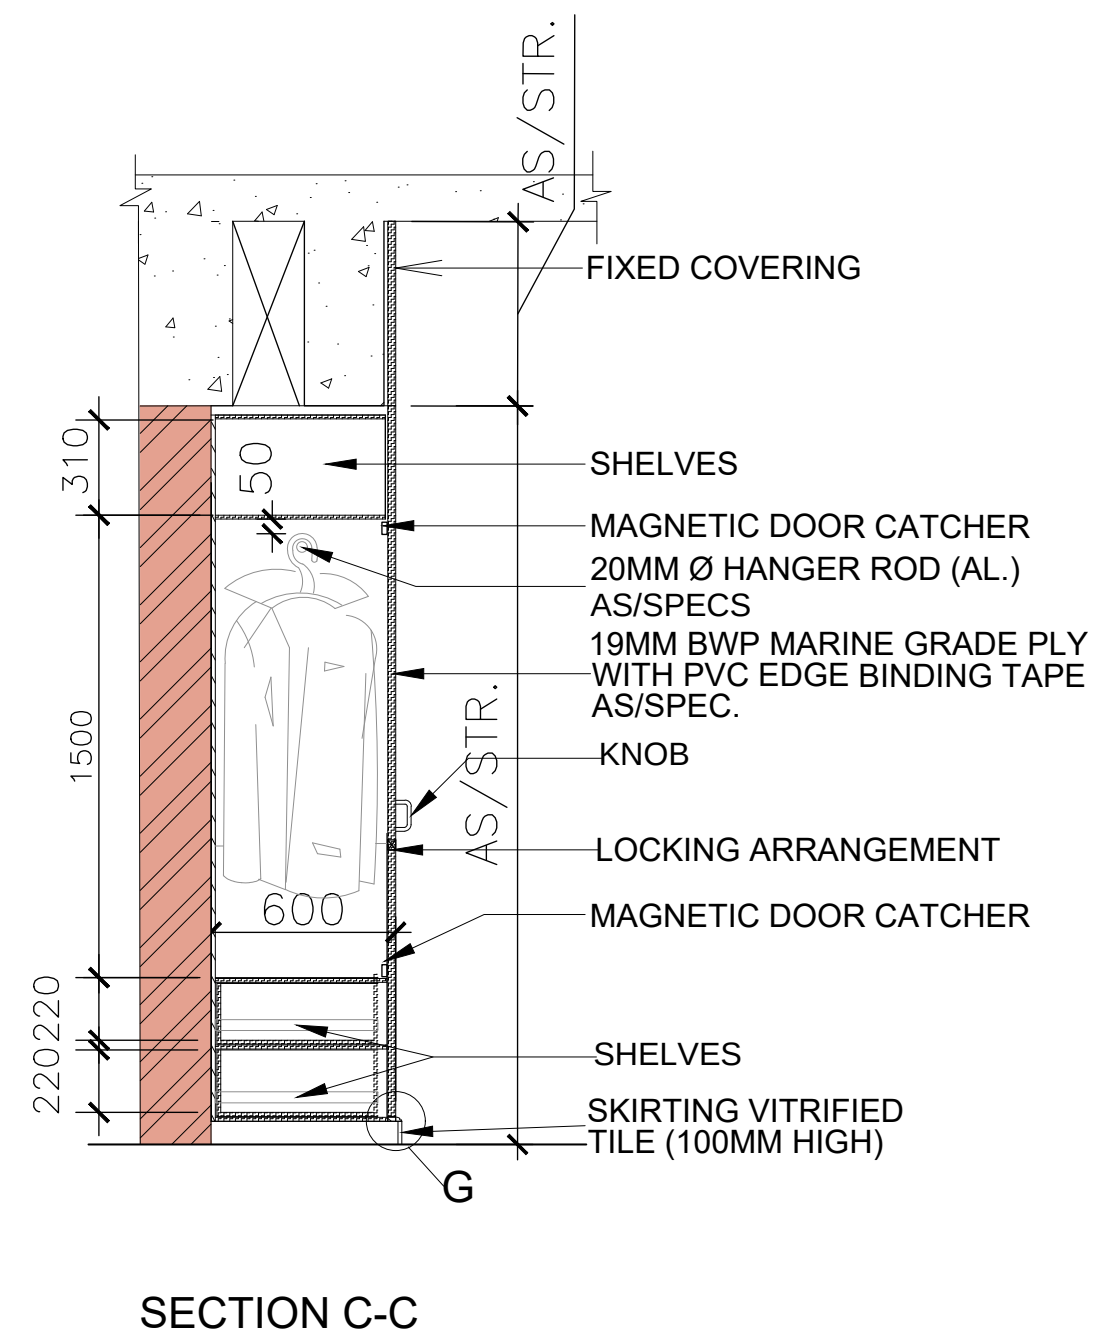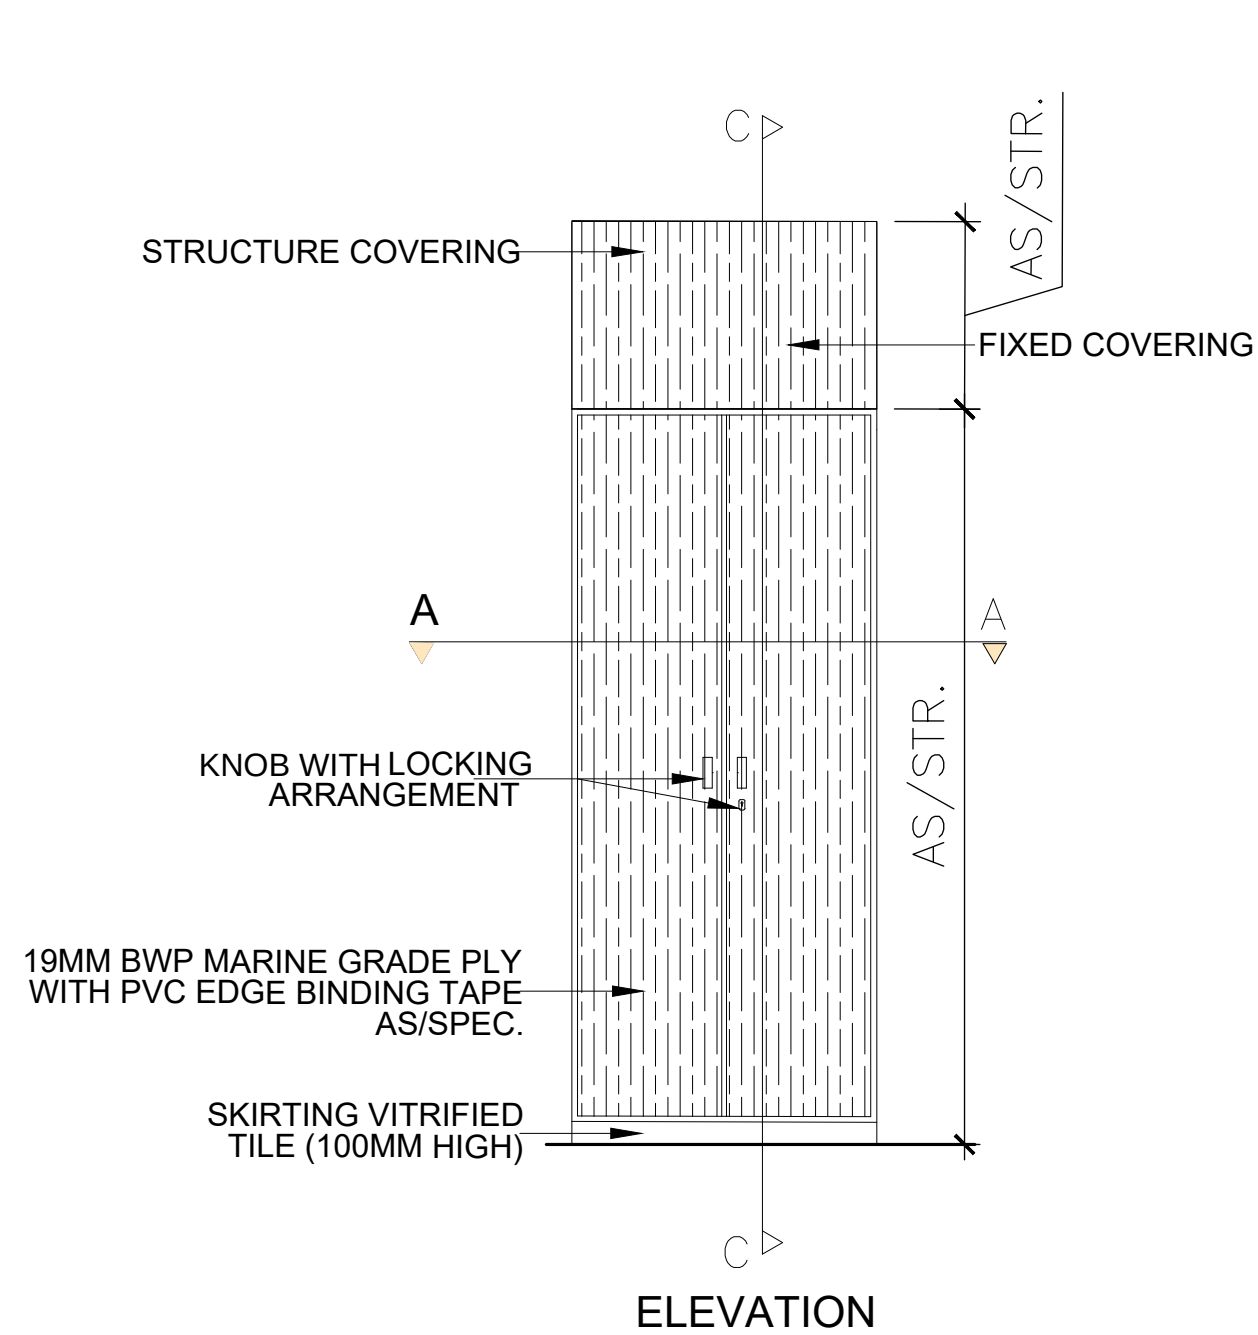

NOTES

1. ALL DIMENSIONS ARE IN MM; UNLESS NOTED OTHERWISE.
2. WRITTEN DIMENSIONS ARE TO BE FOLLOWED. DRAWINGS ARE NOT TO BE SCALED.
3. ANY DISCREPANCY IN THE DRAWING SHALL BE BROUGHT TO THE NOTICE OF THE ENGINEER.
4. THIS DRAWING SHALL BE READ IN CONJUNCTION WITH OTHER RELEVANT DRAWINGS.
5. THE DRAWING IS INDICATIVE ONLY.
6. SHOP DRAWING TO BE PREPARED FOR APPROVAL.
7. REFER SPECIFICATION AND SCHEDULE OF FINISH.

TENDER DRAWING

CLIENT  **OIL INDIA LIMITED**
(A Govt. of India Enterprise)

CONSULTANT  **IRITES**
THE INFRASTRUCTURE PEOPLE
(A Govt. of India Enterprise)







PROJECT **BQ WORKMEN HOUSING**

BUILDING **HOUSING BLOCK (G+6)**

DRAWING TITLE **TYPICAL WARDROBE DETAIL**

DRG. NO. **BITES/BLD/AR/TD/025**

NORTH 	SCALE NTS	DATE JULY 2025
---	---------------------	--------------------------

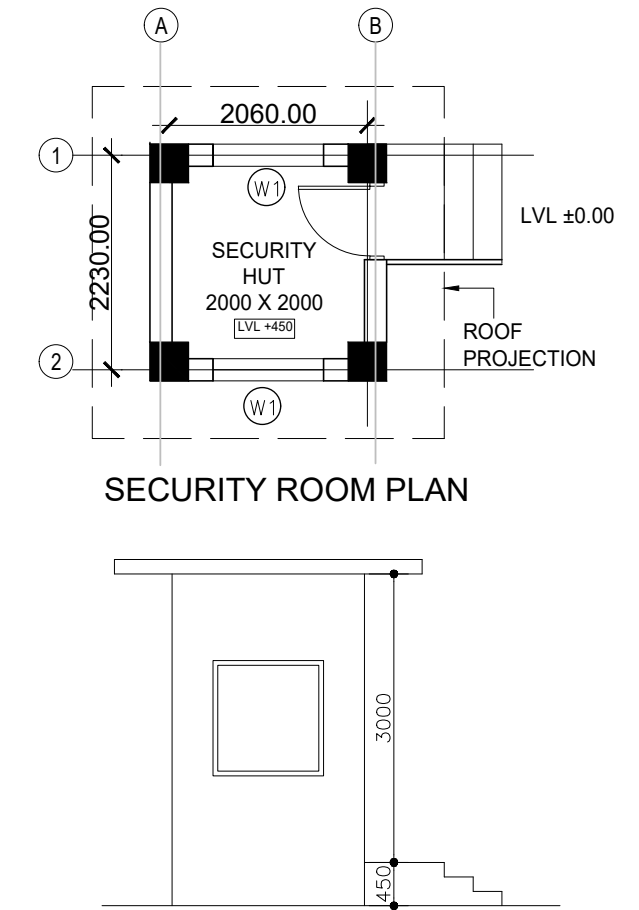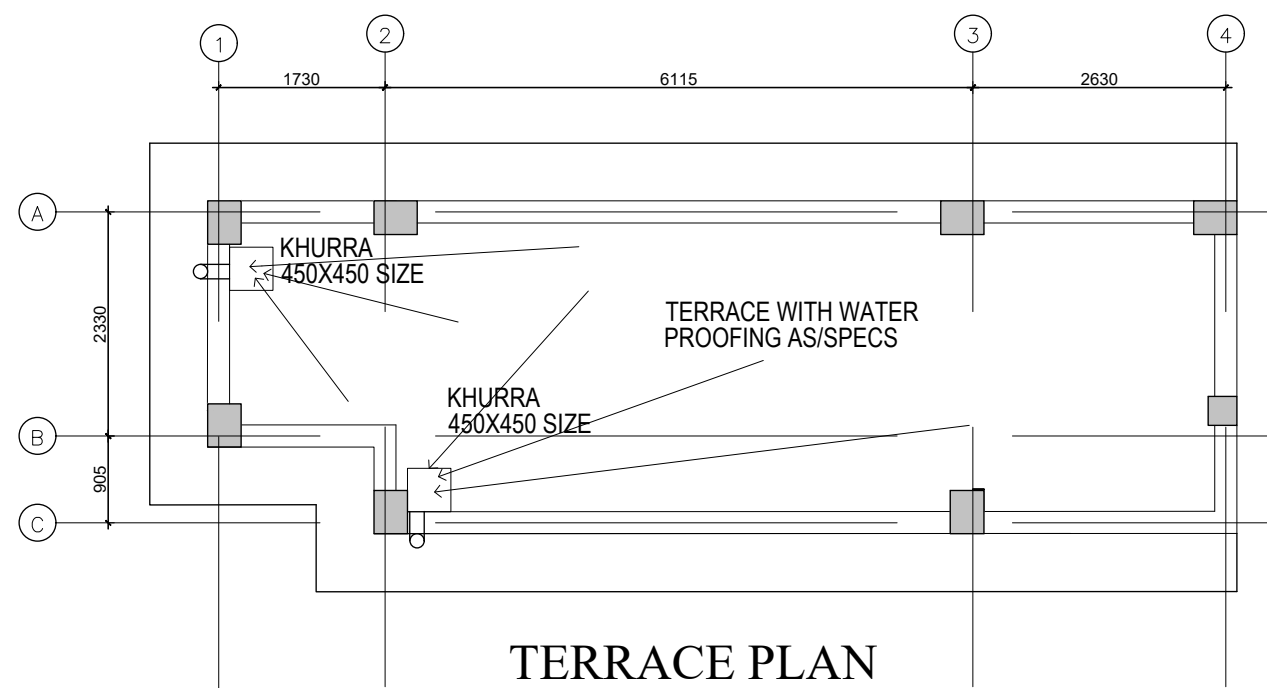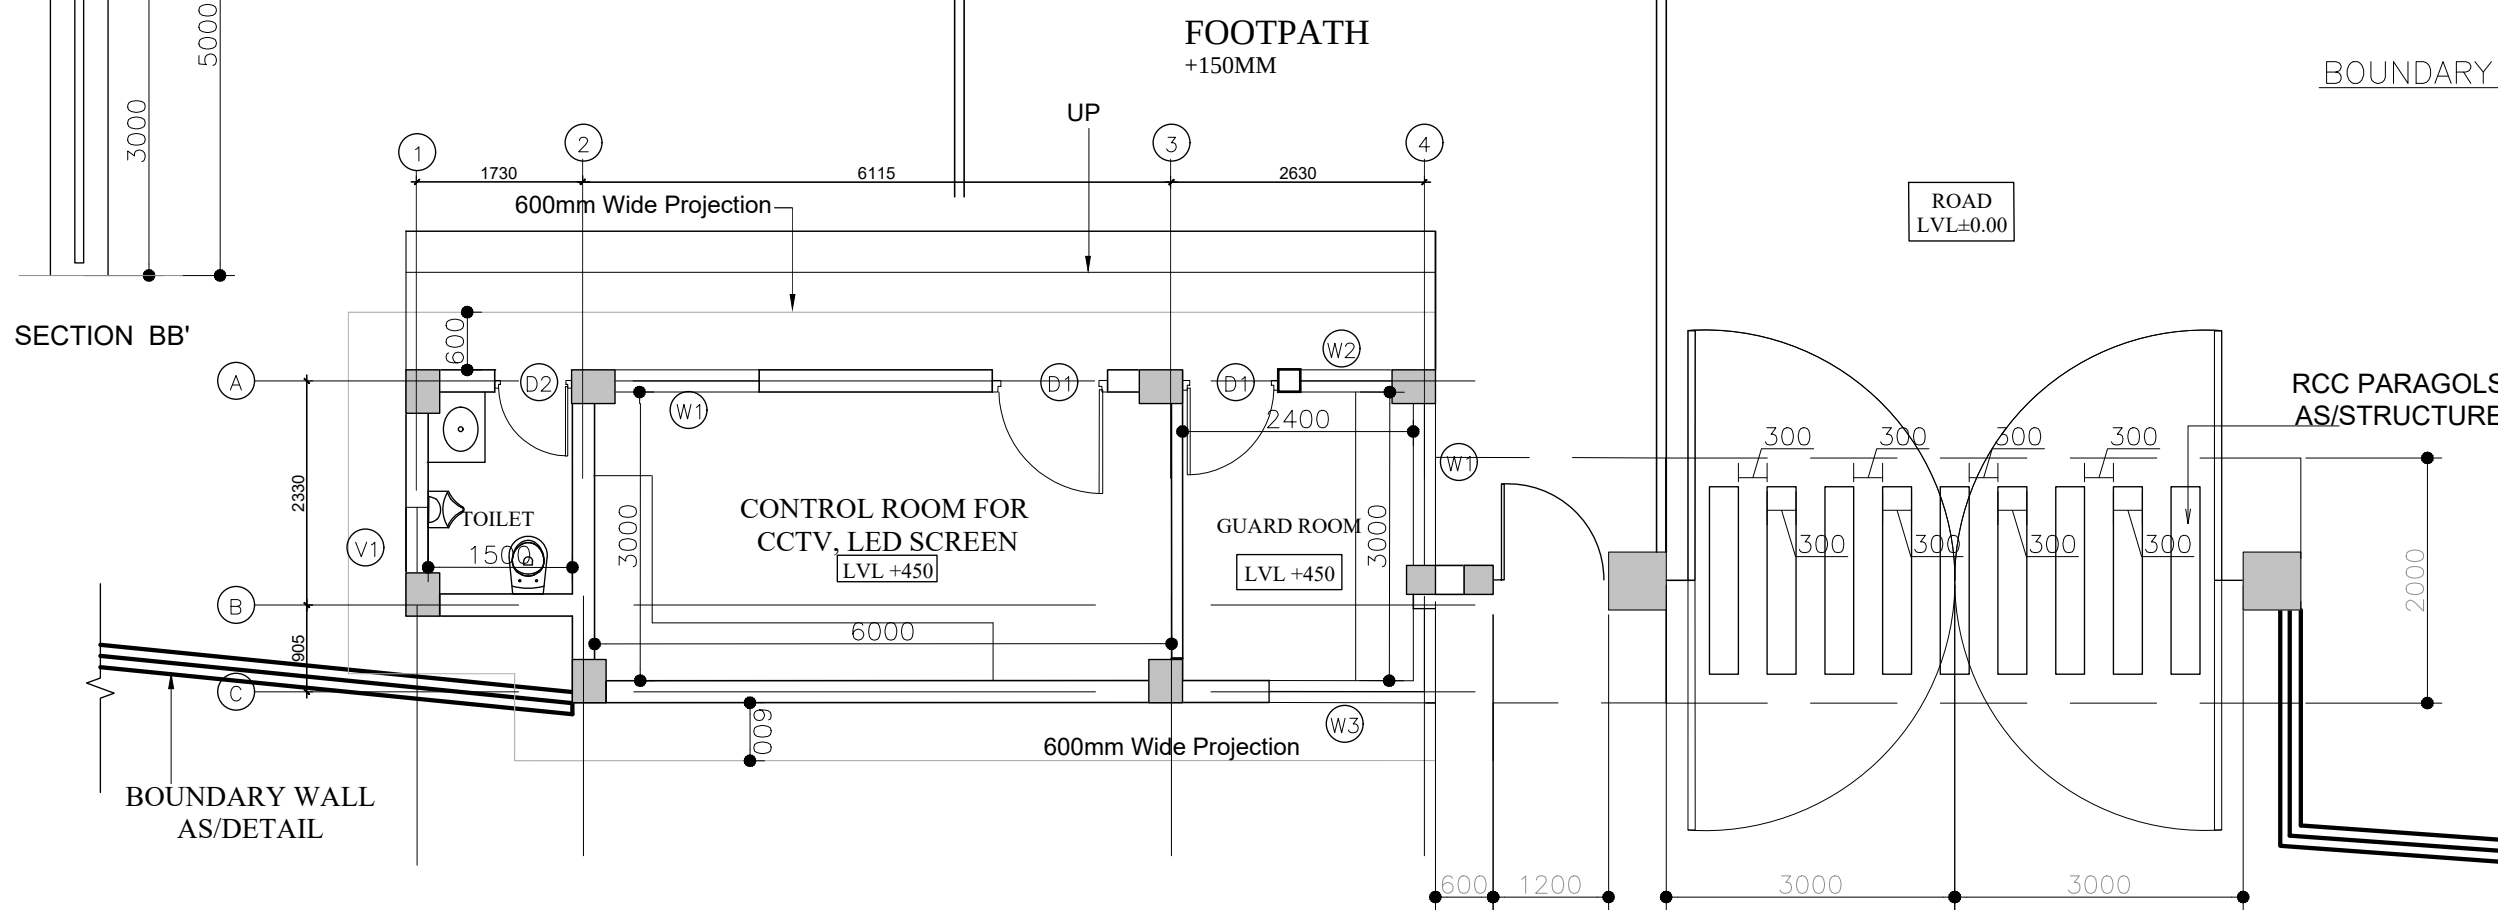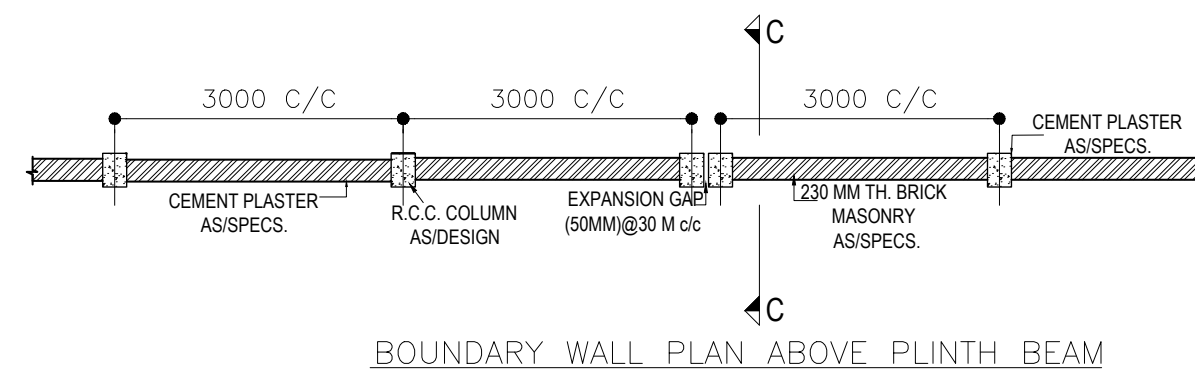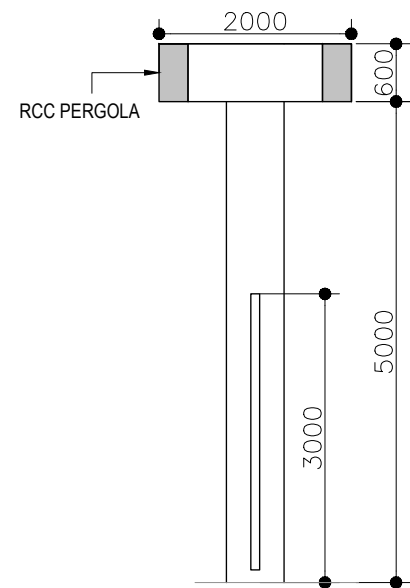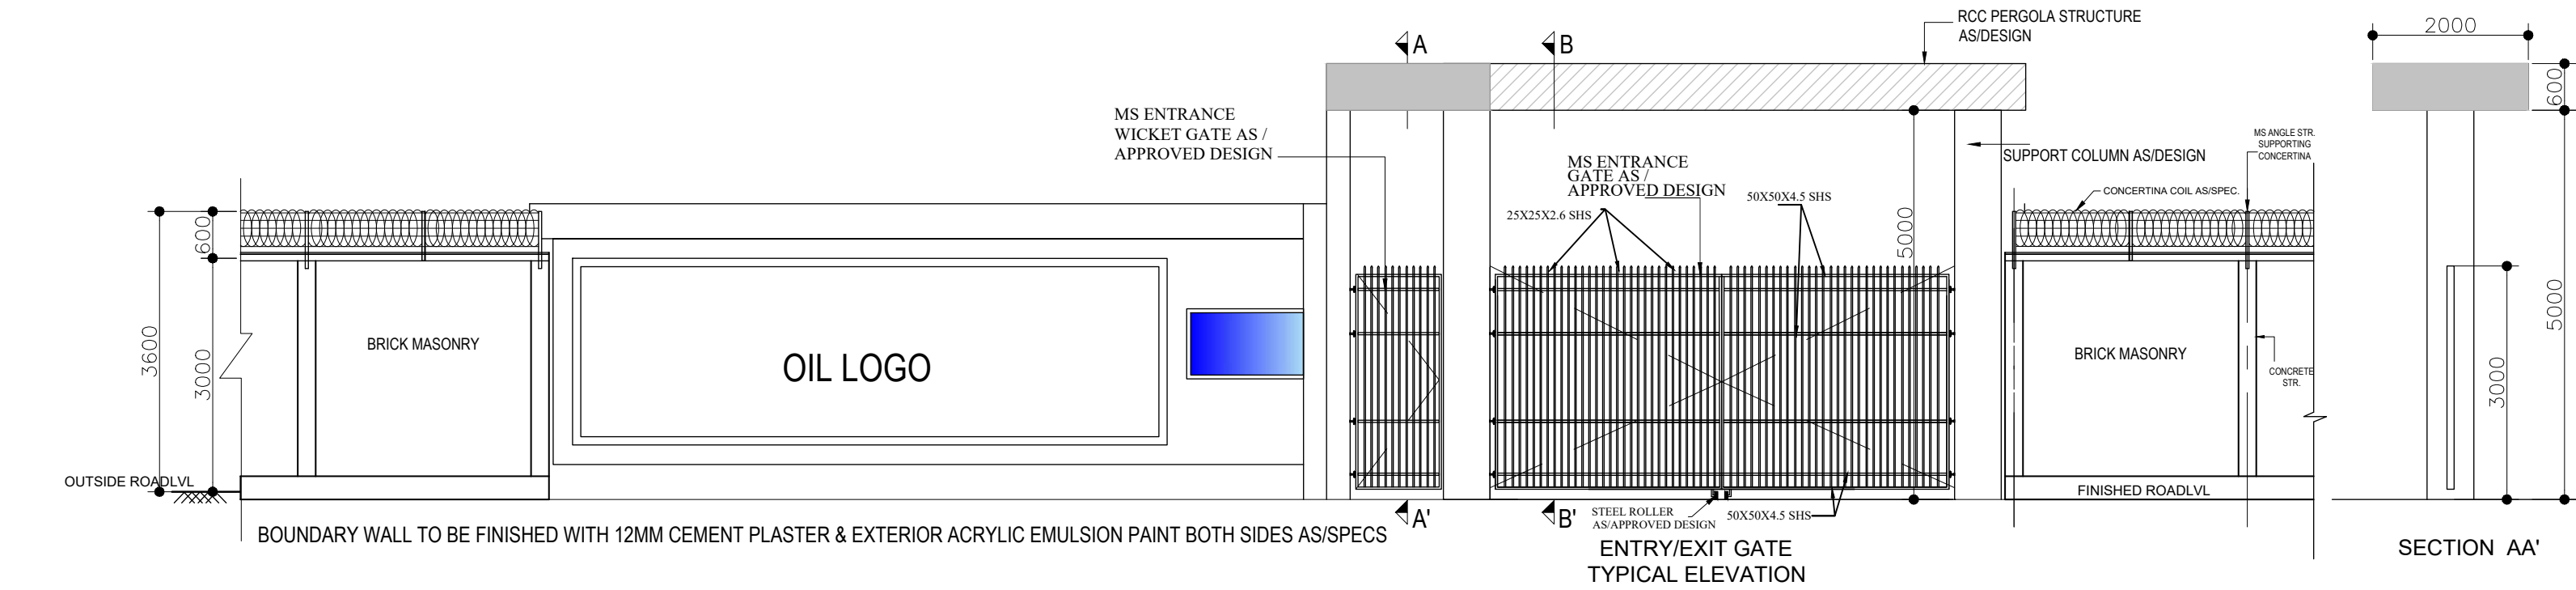

DOORS						
S.NO	TYPE	OPENINGS	SILL	LINTEL	DESCRIPTION	LOCATION
1	D1	1000x2100	00	2100	WPC DOOR FRAME WITH SHUTTER	GUARD ROOM
1	D2	800x2100	00	2100	WPC DOOR FRAME WITH SHUTTER	TOILET
WINDOWS						
1	W1	1200x1050	1050	2100	ALUMINUM SLIDING 3 TRACK WINDOW WITH WIRE MESH	GUARD ROOM
2	W2	800x1050	1050	2100	ALUMINUM SLIDING 3 TRACK WINDOW WITH WIRE MESH	GUARD ROOM
3	W3	2630x1050	1050	2100	L-SHAPED ALUMINUM SLIDING/PARTIALLY FIXED 3 TRACK WINDOW WITH WIRE MESH	GUARD ROOM
VENTILATOR						
1	V1	600x975	1225	2100	ALUMINUM FRAME- VENTILATORS FIXED PANELS WITH EXHUST FAN AS/DRAWING	GUARD ROOM

- NOTES
- ALL DIMENSIONS ARE IN MM; UNLESS NOTED OTHERWISE.
 - WRITTEN DIMENSIONS ARE TO BE FOLLOWED. DRAWINGS ARE NOT TO BE SCALED.
 - ANY DISCREPANCY IN THE DRAWING SHALL BE BROUGHT TO THE NOTICE OF THE ENGINEER.
 - THIS DRAWING SHALL BE READ IN CONJUNCTION WITH OTHER RELEVANT DRAWINGS.

TENDER DRAWING

CLIENT
OIL INDIA LIMITED
(A Govt. of India Enterprise)

CONSULTANT
IRITES
THE INFRASTRUCTURE PEOPLE
(A Govt. of India Enterprise)

PROJECT
BQ WORKMEN HOUSING



BUILDING
HOUSING BLOCK (G+6)

DRAWING TITLE
GUARD ROOM, CONTROL ROOM & BOUNDARY WALL DETAIL

DRG. NO.
IRITES/BLD/AR/TD/026


NORTH

SCALE
NTS
DATE
JULY 2025

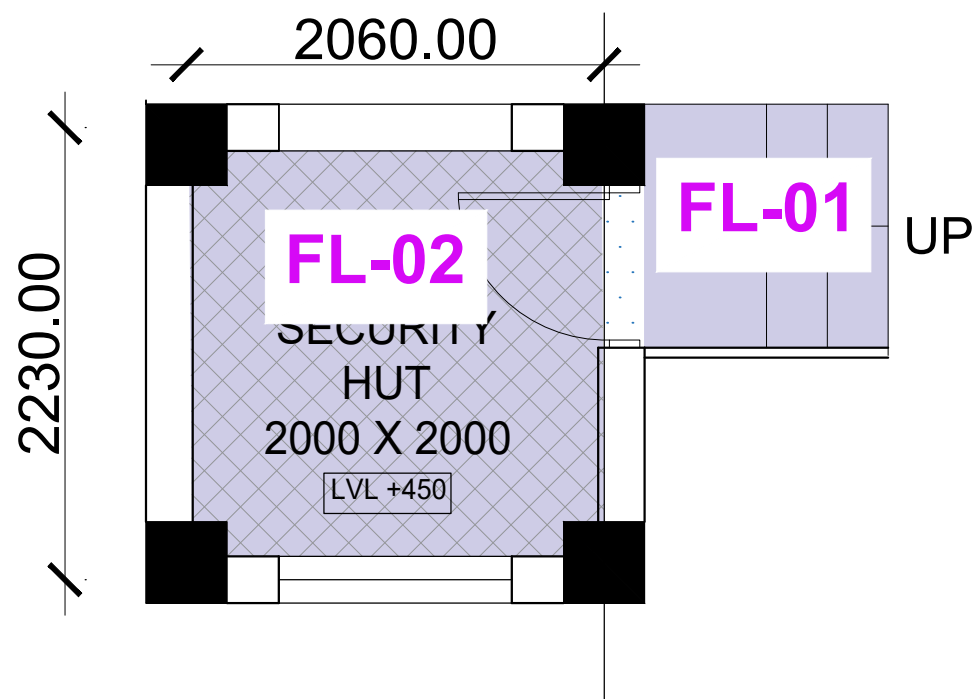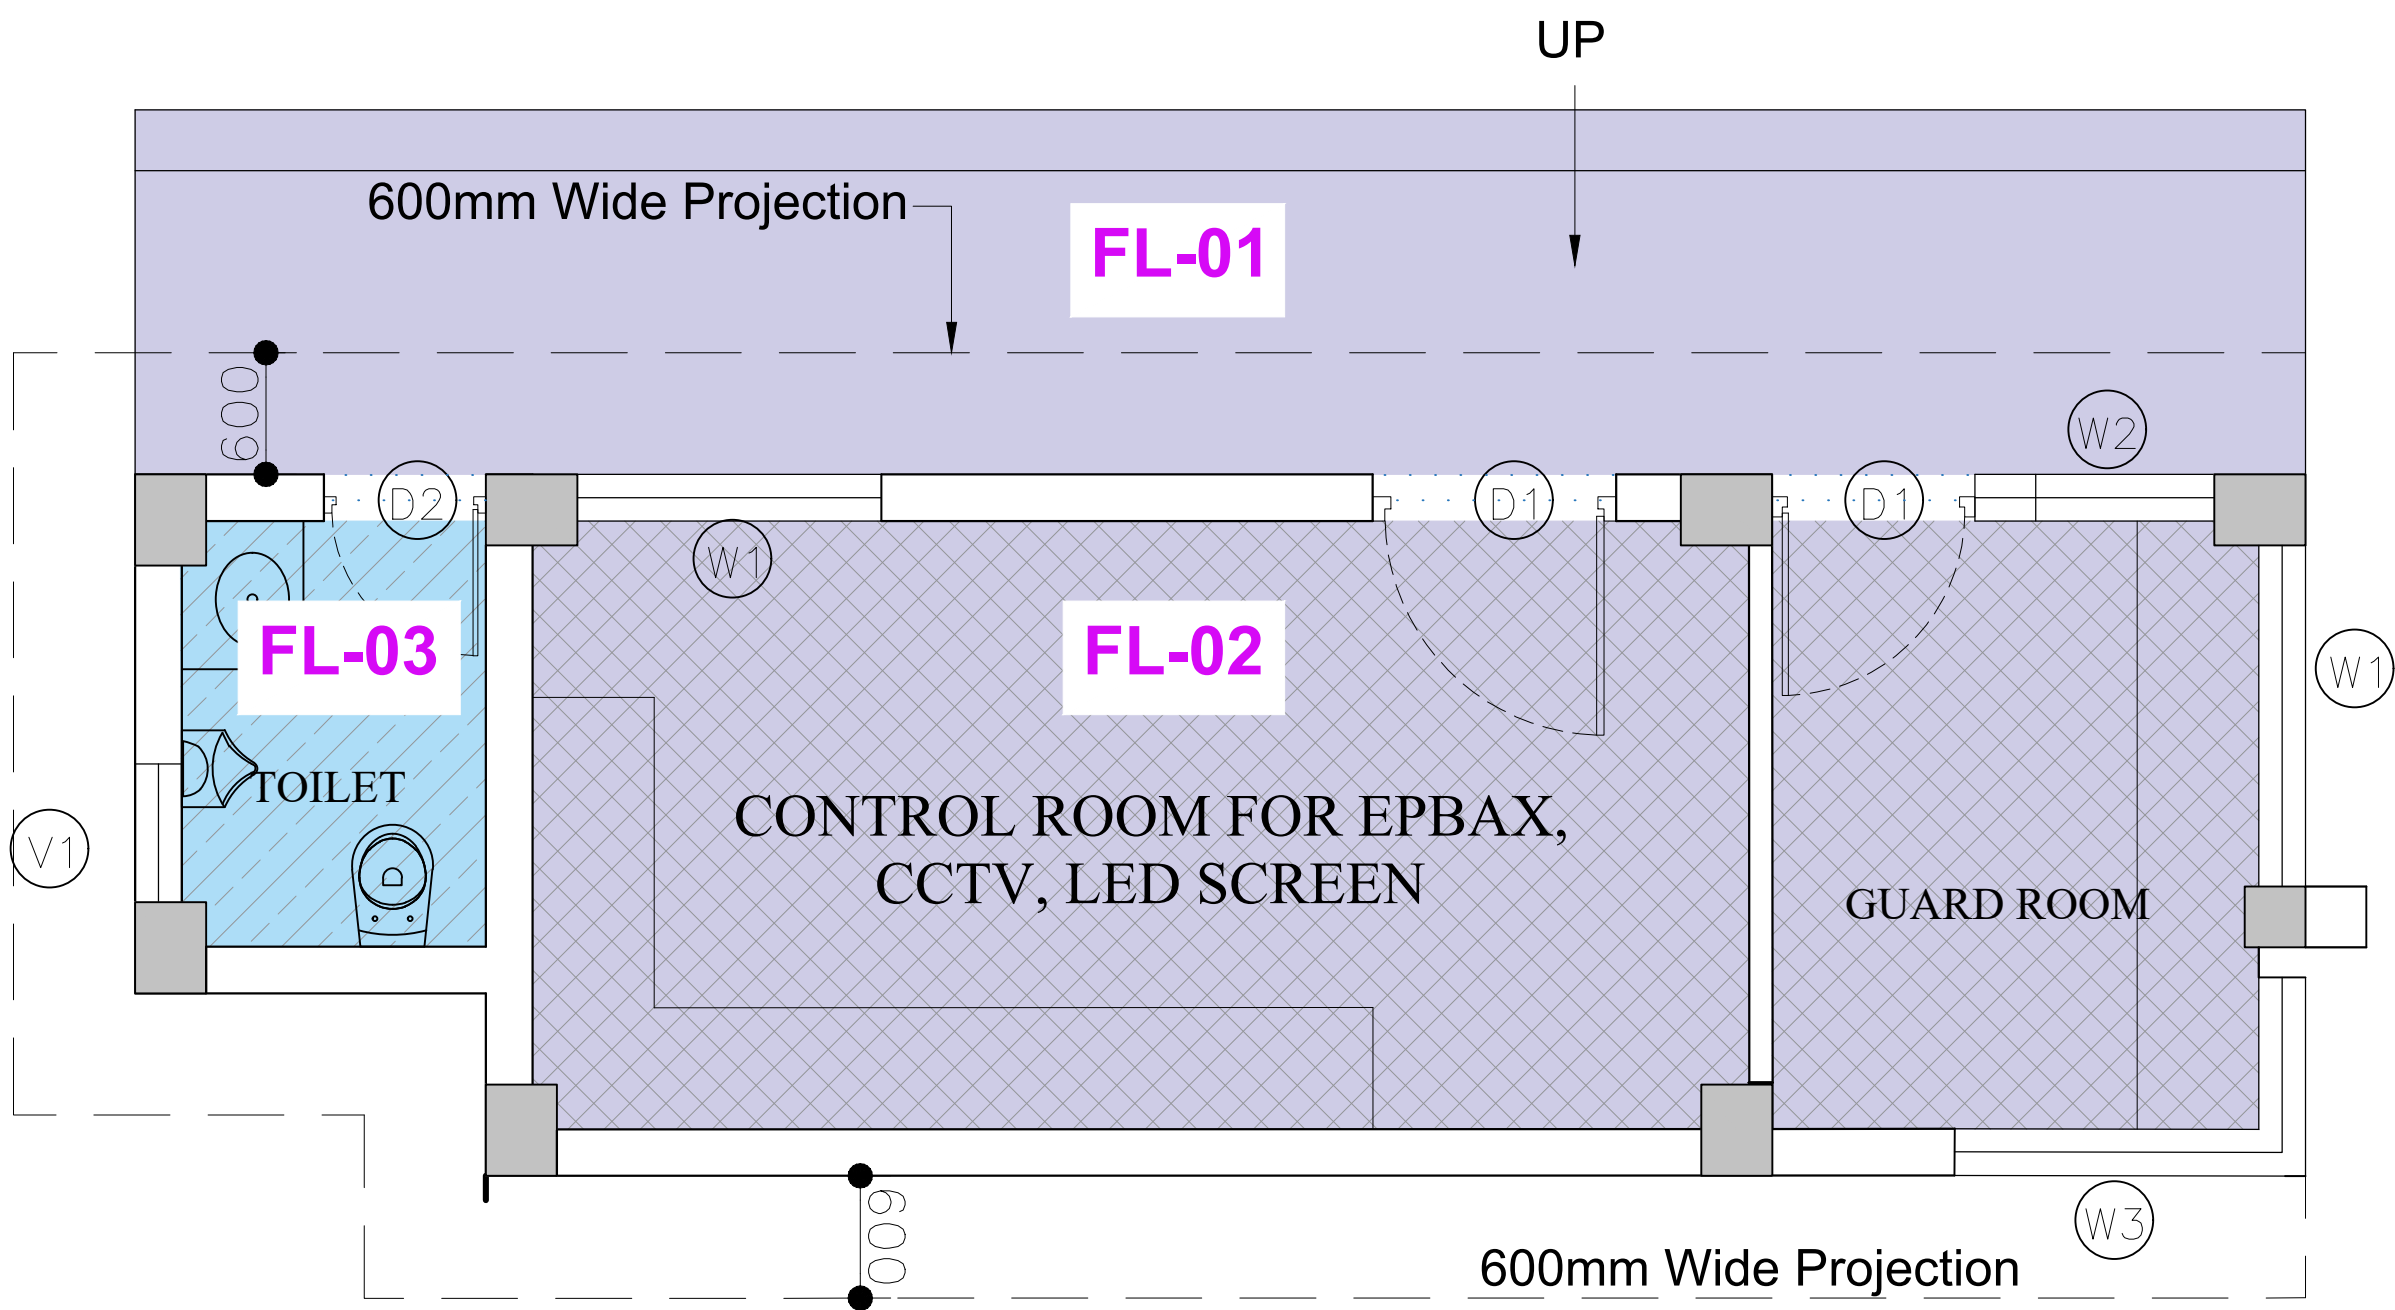

LEGEND FOR FLOORING				
S.NO.	HATCH SYMBOL	ICON	MATERIAL	AREA OF APPLICATION
01		FL-01	25MM THK. KOTA STONE	ENTRY RAMP/STEPS
02		FL-02	POLISHED GLAZED VITRIFIED TILE (800 X 800)	- GUARD ROOM - CONTROL ROOM - SECURITY HUT
03		FL-03	RECTIFIED ANTI SKID CERAMIC TILES (300 X 300)	TOILET
04		FL-04	LIQUID RUBBER WATER PROOFING, LAYING CC 1:2:4 CONCRETE FOR ROOF GRADING, HEAT RESISTANT SRI TILES AS PER SPECIFICATIONS.	TERRACE
05	SKIRTING 100 MM HIGH, MATCHING THE FLOOR FINISH; DADO IN TOILETS UP TO FALSE CEILING LEVEL A ALL AS PER SPECIFICATIONS			

KEY PLAN

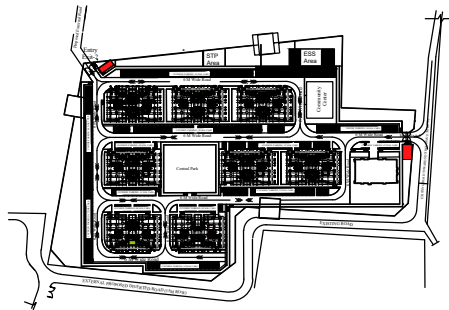

NOTES

- ALL DIMENSIONS ARE IN MM; UNLESS NOTED OTHERWISE.
- WRITTEN DIMENSIONS ARE TO BE FOLLOWED. DRAWINGS ARE NOT TO BE SCALED.
- ANY DISCREPANCY IN THE DRAWING SHALL BE BROUGHT TO THE NOTICE OF THE ENGINEER.
- THIS DRAWING SHALL BE READ IN CONJUNCTION WITH OTHER RELEVANT DRAWINGS.

TENDER DRAWING

CLIENT
 OIL INDIA LIMITED
(A Govt. of India Enterprise)


CONSULTANT
 RITES
THE INFRASTRUCTURE PEOPLE
(A Govt. of India Enterprise)

PROJECT
BQ WORKMEN HOUSING

BUILDING
GUARD ROOM WITH CCTV
CONTROL ROOM & SECURITY HUT


DRAWING TITLE
FLOORING DETAIL

DRG. NO.
RITES/BLD/AR/TD/027

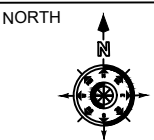

SCALE
NTS

DATE
JULY 2025

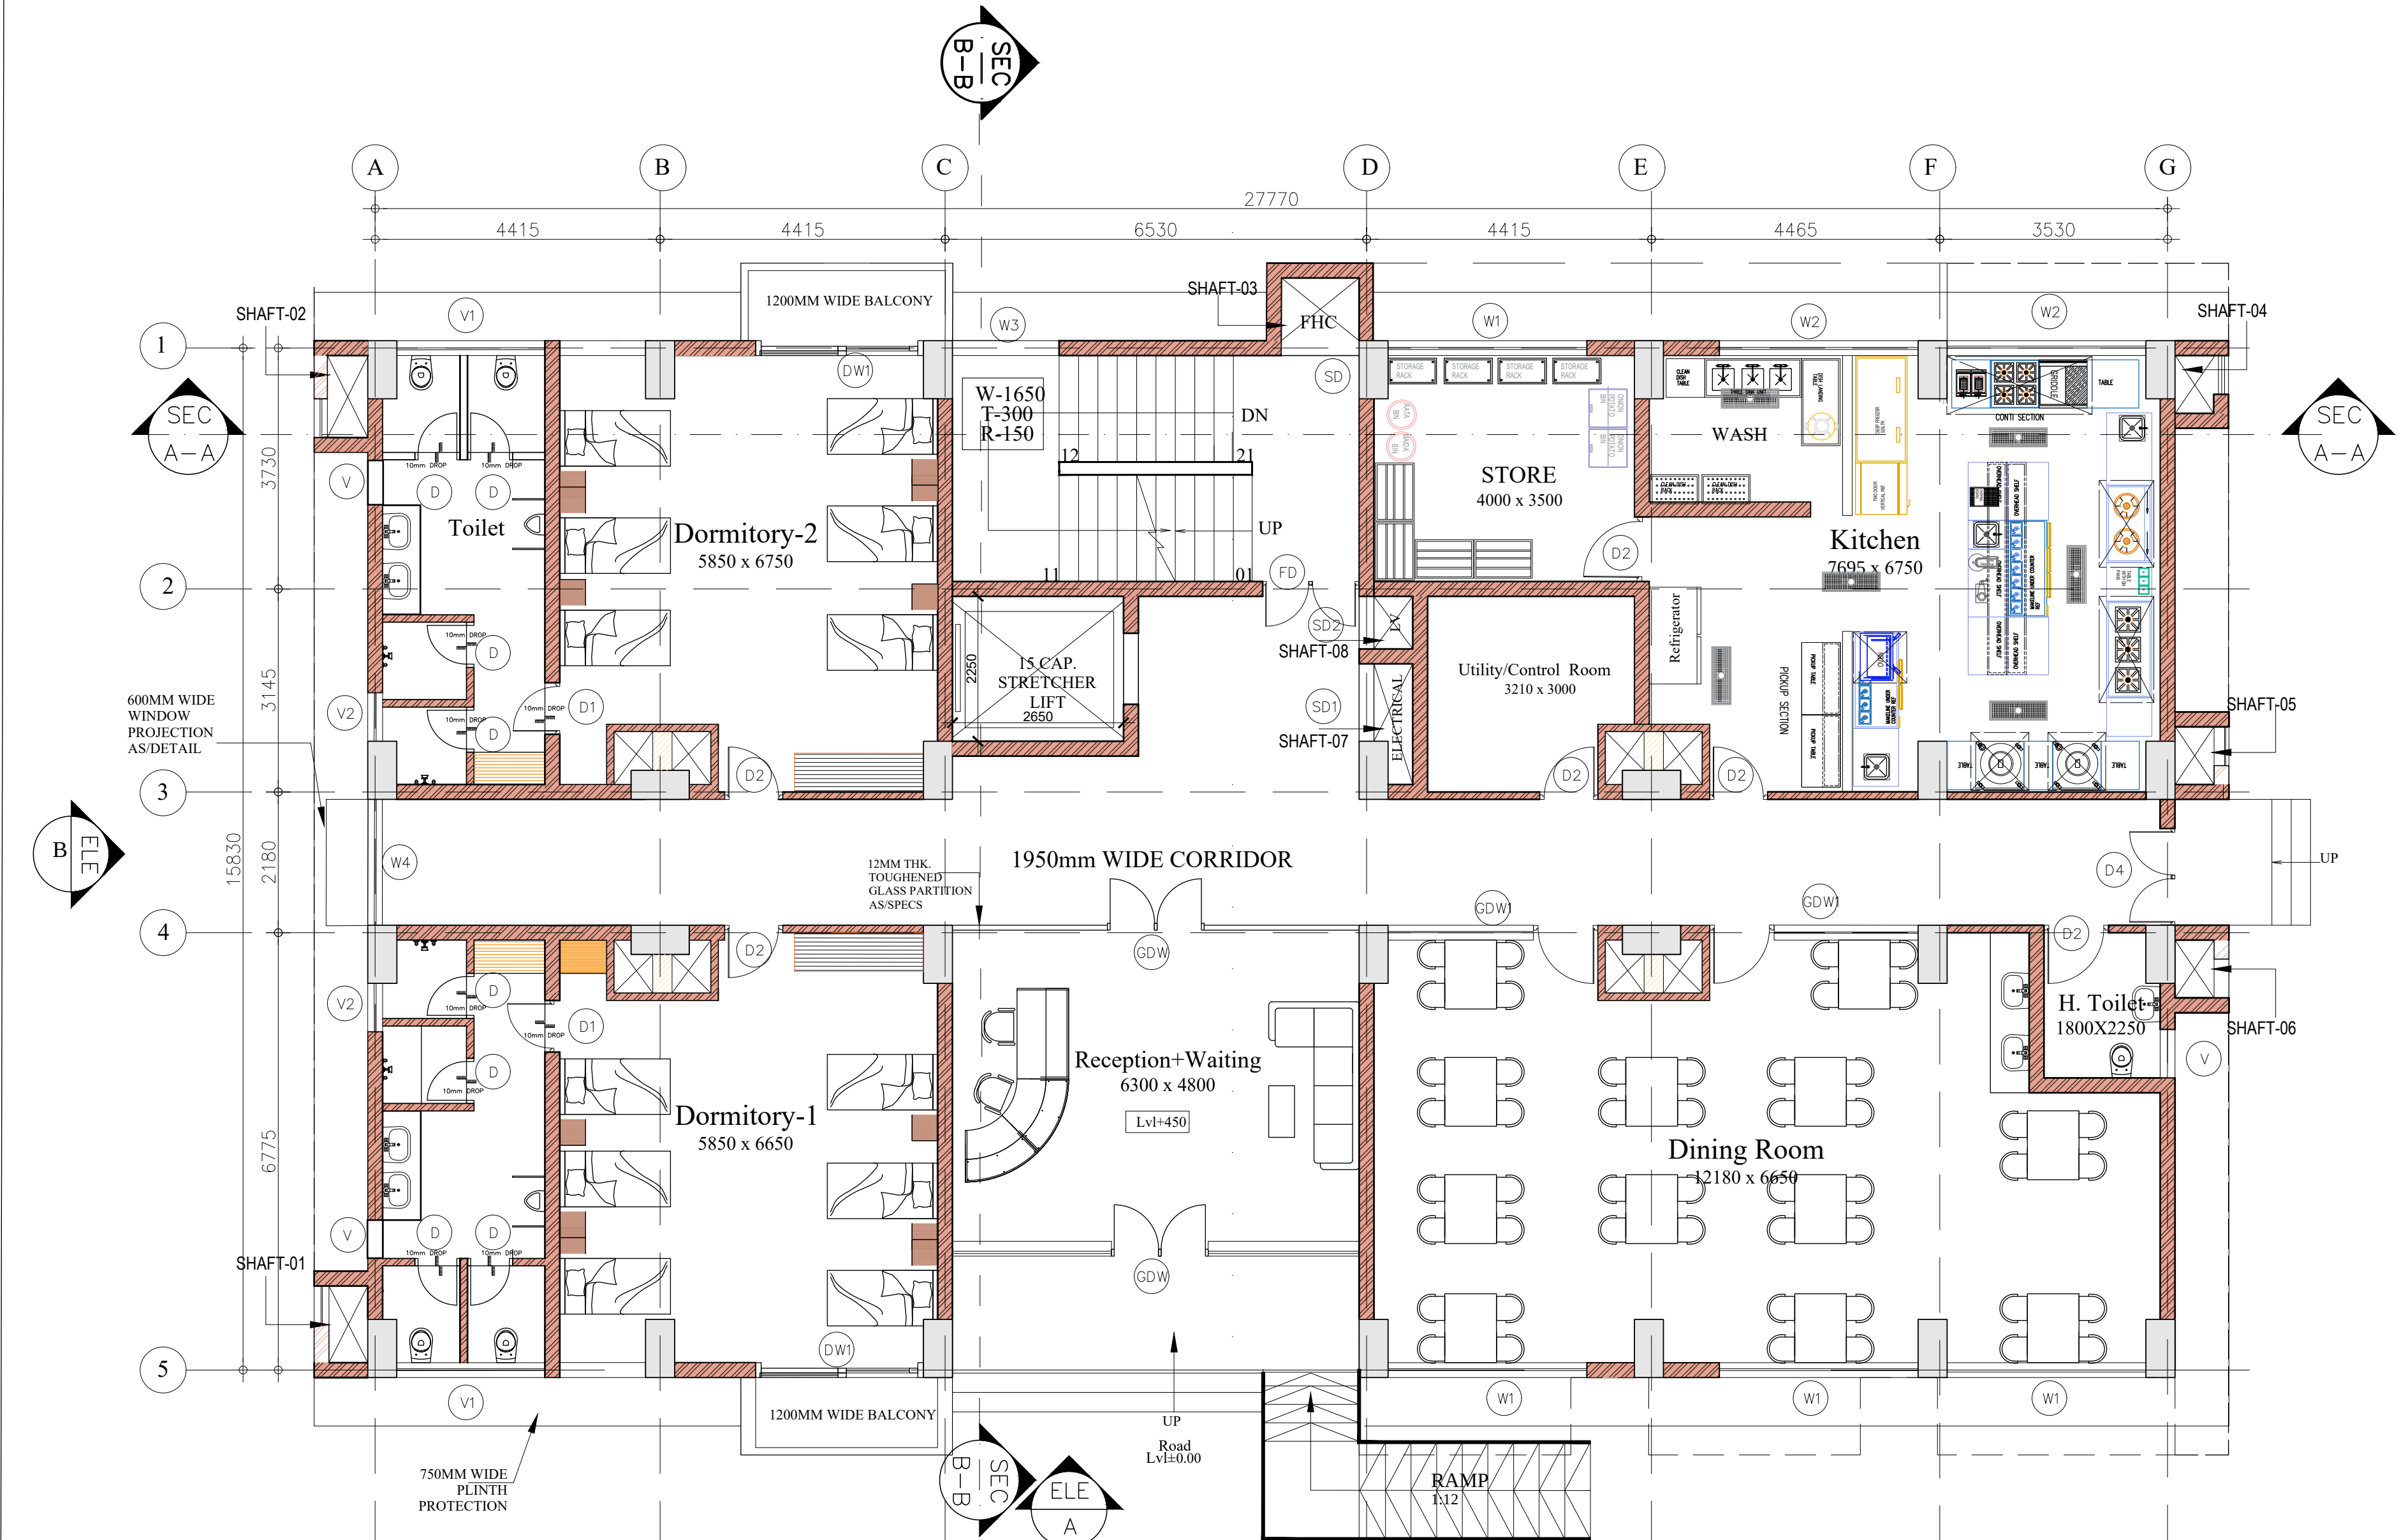

SCHEDULE OF DOORS - (Ground floor to Terrace floor)							
SL. NO	TYPE	NOS.	WIDTH	HEIGHT	CILL (from FFL)	LINTEL (from FFL)	LOCATION
1.	D	---	750	2100	00	2100	WC AND BATH
2.	D1	---	900	2100	00	2100	TOILETS
3.	D2	---	1000	2100	00	2100	ROOMS
4.	D3	---	1050	2100	00	2100	PWD TOILET
5.	D4	---	1500	2100	00	2100	SERVICE ENTRY
6.	DW1	---	2600	2100	00	2100	ROOM BALCONY
7.	GDW	---	6300	2400	00	2400	ENTRY
8.	GDW1	---	3230	2400	00	2400	BALCONY, DINING ENTRY
9.	FD	---	1500	2100	00	2100	STAIRCASE
10.	SD	---	900	2100	100	2100	FHC SHAFT
11.	SD1	---	900	2100	100	2100	ELE. SHAFT
12.	SD2	---	600	2100	100	2100	LV. SHAFT

SCHEDULE OF DOORS - (Ground floor to Terrace floor)							
SL. NO	TYPE	NOS.	WIDTH	HEIGHT	CILL (from FFL)	LINTEL (from FFL)	LOCATION
1.	D	---	750	2100	00	2100	WC AND BATH
2.	D1	---	900	2100	00	2100	TOILETS
3.	D2	---	1000	2100	00	2100	ROOMS
4.	D3	---	1050	2100	00	2100	PWD TOILET
5.	D4	---	1500	2100	00	2100	SERVICE ENTRY
6.	DW1	---	2600	2100	00	2100	ROOM BALCONY
7.	GDW	---	6300	2400	00	2400	ENTRY
8.	GDW1	---	3230	2400	00	2400	BALCONY, DINING ENTRY
9.	FD	---	1500	2100	00	2100	STAIRCASE
10.	SD	---	900	2100	100	2100	FHC SHAFT
11.	SD1	---	900	2100	100	2100	ELE. SHAFT
12.	SD2	---	600	2100	100	2100	LV. SHAFT

SCHEDULE OF DOORS - (Ground floor to Terrace floor)							
SL. NO	TYPE	NOS.	WIDTH	HEIGHT	CILL (from FFL)	LINTEL (from FFL)	LOCATION
1.	D	---	750	2100	00	2100	WC AND BATH
2.	D1	---	900	2100	00	2100	TOILETS
3.	D2	---	1000	2100	00	2100	ROOMS
4.	D3	---	1050	2100	00	2100	PWD TOILET
5.	D4	---	1500	2100	00	2100	SERVICE ENTRY
6.	DW1	---	2600	2100	00	2100	ROOM BALCONY
7.	GDW	---	6300	2400	00	2400	ENTRY
8.	GDW1	---	3230	2400	00	2400	BALCONY, DINING ENTRY
9.	FD	---	1500	2100	00	2100	STAIRCASE
10.	SD	---	900	2100	100	2100	FHC SHAFT
11.	SD1	---	900	2100	100	2100	ELE. SHAFT
12.	SD2	---	600	2100	100	2100	LV. SHAFT

SCHEDULE OF WINDOWS - (Ground floor to Terrace floor)							
SL. NO	TYPE	NOS.	WIDTH	HEIGHT	SILL (from FFL)	LINTEL (from FFL)	REMARKS
1.	W1	---	3100	1200	900	2100	POWDER COATED ALUMINUM FRAMED SLIDING WINDOW - THREE TRACK SYSTEM WITH WIRE MESH AS/DRAWING
2.	W2	---	3100	875	1225	2100	POWDER COATED ALUMINUM FRAMED SLIDING WINDOW - THREE TRACK SYSTEM WITH WIRE MESH AS/DRAWING/SPECS
3.	W3	---	1650	1100	1000	2100	POWDER COATED ALUMINUM FRAMED SLIDING WINDOW - TWO TRACK SYSTEM AS/DRAWING/SPECS
4.	W4	---	1950	1200	900	2100	POWDER COATED ALUMINUM FRAMED SLIDING WINDOW - THREE TRACK SYSTEM AS/DRAWING/SPECS

SCHEDULE OF VENTILATORS - (Ground floor to Terrace floor)							
SL. NO	TYPE	NOS.	WIDTH	HEIGHT	SILL (from FFL)	LINTEL (from FFL)	REMARKS
1.	V	---	600	875	1225	2100	POWDER-COATED ALUMINUM FRAME VENTILATOR WITH FIXED FROSTED GLASS PANELS AND INTEGRATED EXHAUST FAN AS/DRAWING/SPECS
2.	V1	---	2295	450	2100	AS/SITE	POWDER-COATED ALUMINUM FRAME VENTILATOR WITH FIXED FROSTED GLASS PANELS AND INTEGRATED EXHAUST FAN AS/DRAWING/SPECS
2.	V2	---	900	450	2100	AS/SITE	POWDER-COATED ALUMINUM FRAME VENTILATOR WITH FIXED FROSTED GLASS PANELS AND INTEGRATED EXHAUST FAN AS/DRAWING/SPECS

SCHEDULE OF SHAFT JALI - (Ground floor to Terrace floor)							
SL. NO	TYPE	NOS.	WIDTH	HEIGHT	SILL (from FFL)	LINTEL (from FFL)	REMARKS
1.	JL	---	600	2550	+00	BEAM BOTTOM/AS PER STR.	ALUMINUM OPENABLE LOUVERED PANEL

KEY PLAN

NOTES

- ALL DIMENSIONS ARE IN MM. UNLESS NOTED OTHERWISE.
- WRITTEN DIMENSIONS ARE TO BE FOLLOWED. DRAWINGS ARE NOT TO BE SCALED.
- ANY DISCREPANCY IN THE DRAWING SHALL BE BROUGHT TO THE NOTICE OF THE ENGINEER.
- THIS DRAWING SHALL BE READ IN CONJUNCTION WITH OTHER RELEVANT DRAWINGS.
- MOVABLE EQUIPMENT AND FURNISHINGS SUCH AS BED, WARDROBE, GEYSERS, TV, TABLE CHAIRS, ETC. ARE SHOWN FOR ILLUSTRATIVE PURPOSES ONLY (FOR MEP DETAILING) AND ARE NOT TO BE PROVIDED. REFER TENDER DOCUMENT FOR DETAILS OF FUR./EQP. TO BE PROVIDED.
- STRUCTURE DRAWING TO BE FOLLOWED FOR COLUMN SIZES

Sn.No.	Description	Area (Sqm)
01	Ground Floor Area	465 sqm
02	First Floor Area	495 sqm
03	Second Floor Area	500 sqm
04	Third Floor Area	500 sqm
05	Mumty Area	30 sqm

SHAFT SCHEDULE

SL. NO	TYPE	WIDTH	LENGTH	REMARKS
1.	SH-01	1200	600	PLUMBING SHAFT
2.	SH-02	1200	600	RAIN WATER SHAFT
3.	SH-03	970	1200	FHC SHAFT
4.	SH-04	900	600	RAIN WATER SHAFT
5.	SH-05	900	600	PLUMBING SHAFT
6.	SH-06	900	600	PLUMBING SHAFT
7.	SH-07	1200	600	ELECTRICAL SHAFT
8.	SH-08	800	600	LV SHAFT

TENDER DRAWING

CLIENTOIL INDIA LIMITED
(A Govt. of India Enterprise)

CONSULTANTRITES
THE INFRASTRUCTURE PEOPLE
(A Govt. of India Enterprise)


PROJECTBQ WORKMEN HOUSING

BUILDINGGUEST HOUSE (G+3)

DRAWING TITLEGROUND FLOOR PLAN

DRG. NO.RITES/BLD/AR/TD/028

NORTH	SCALENTS	DATEJULY 2025
-------	----------	---------------

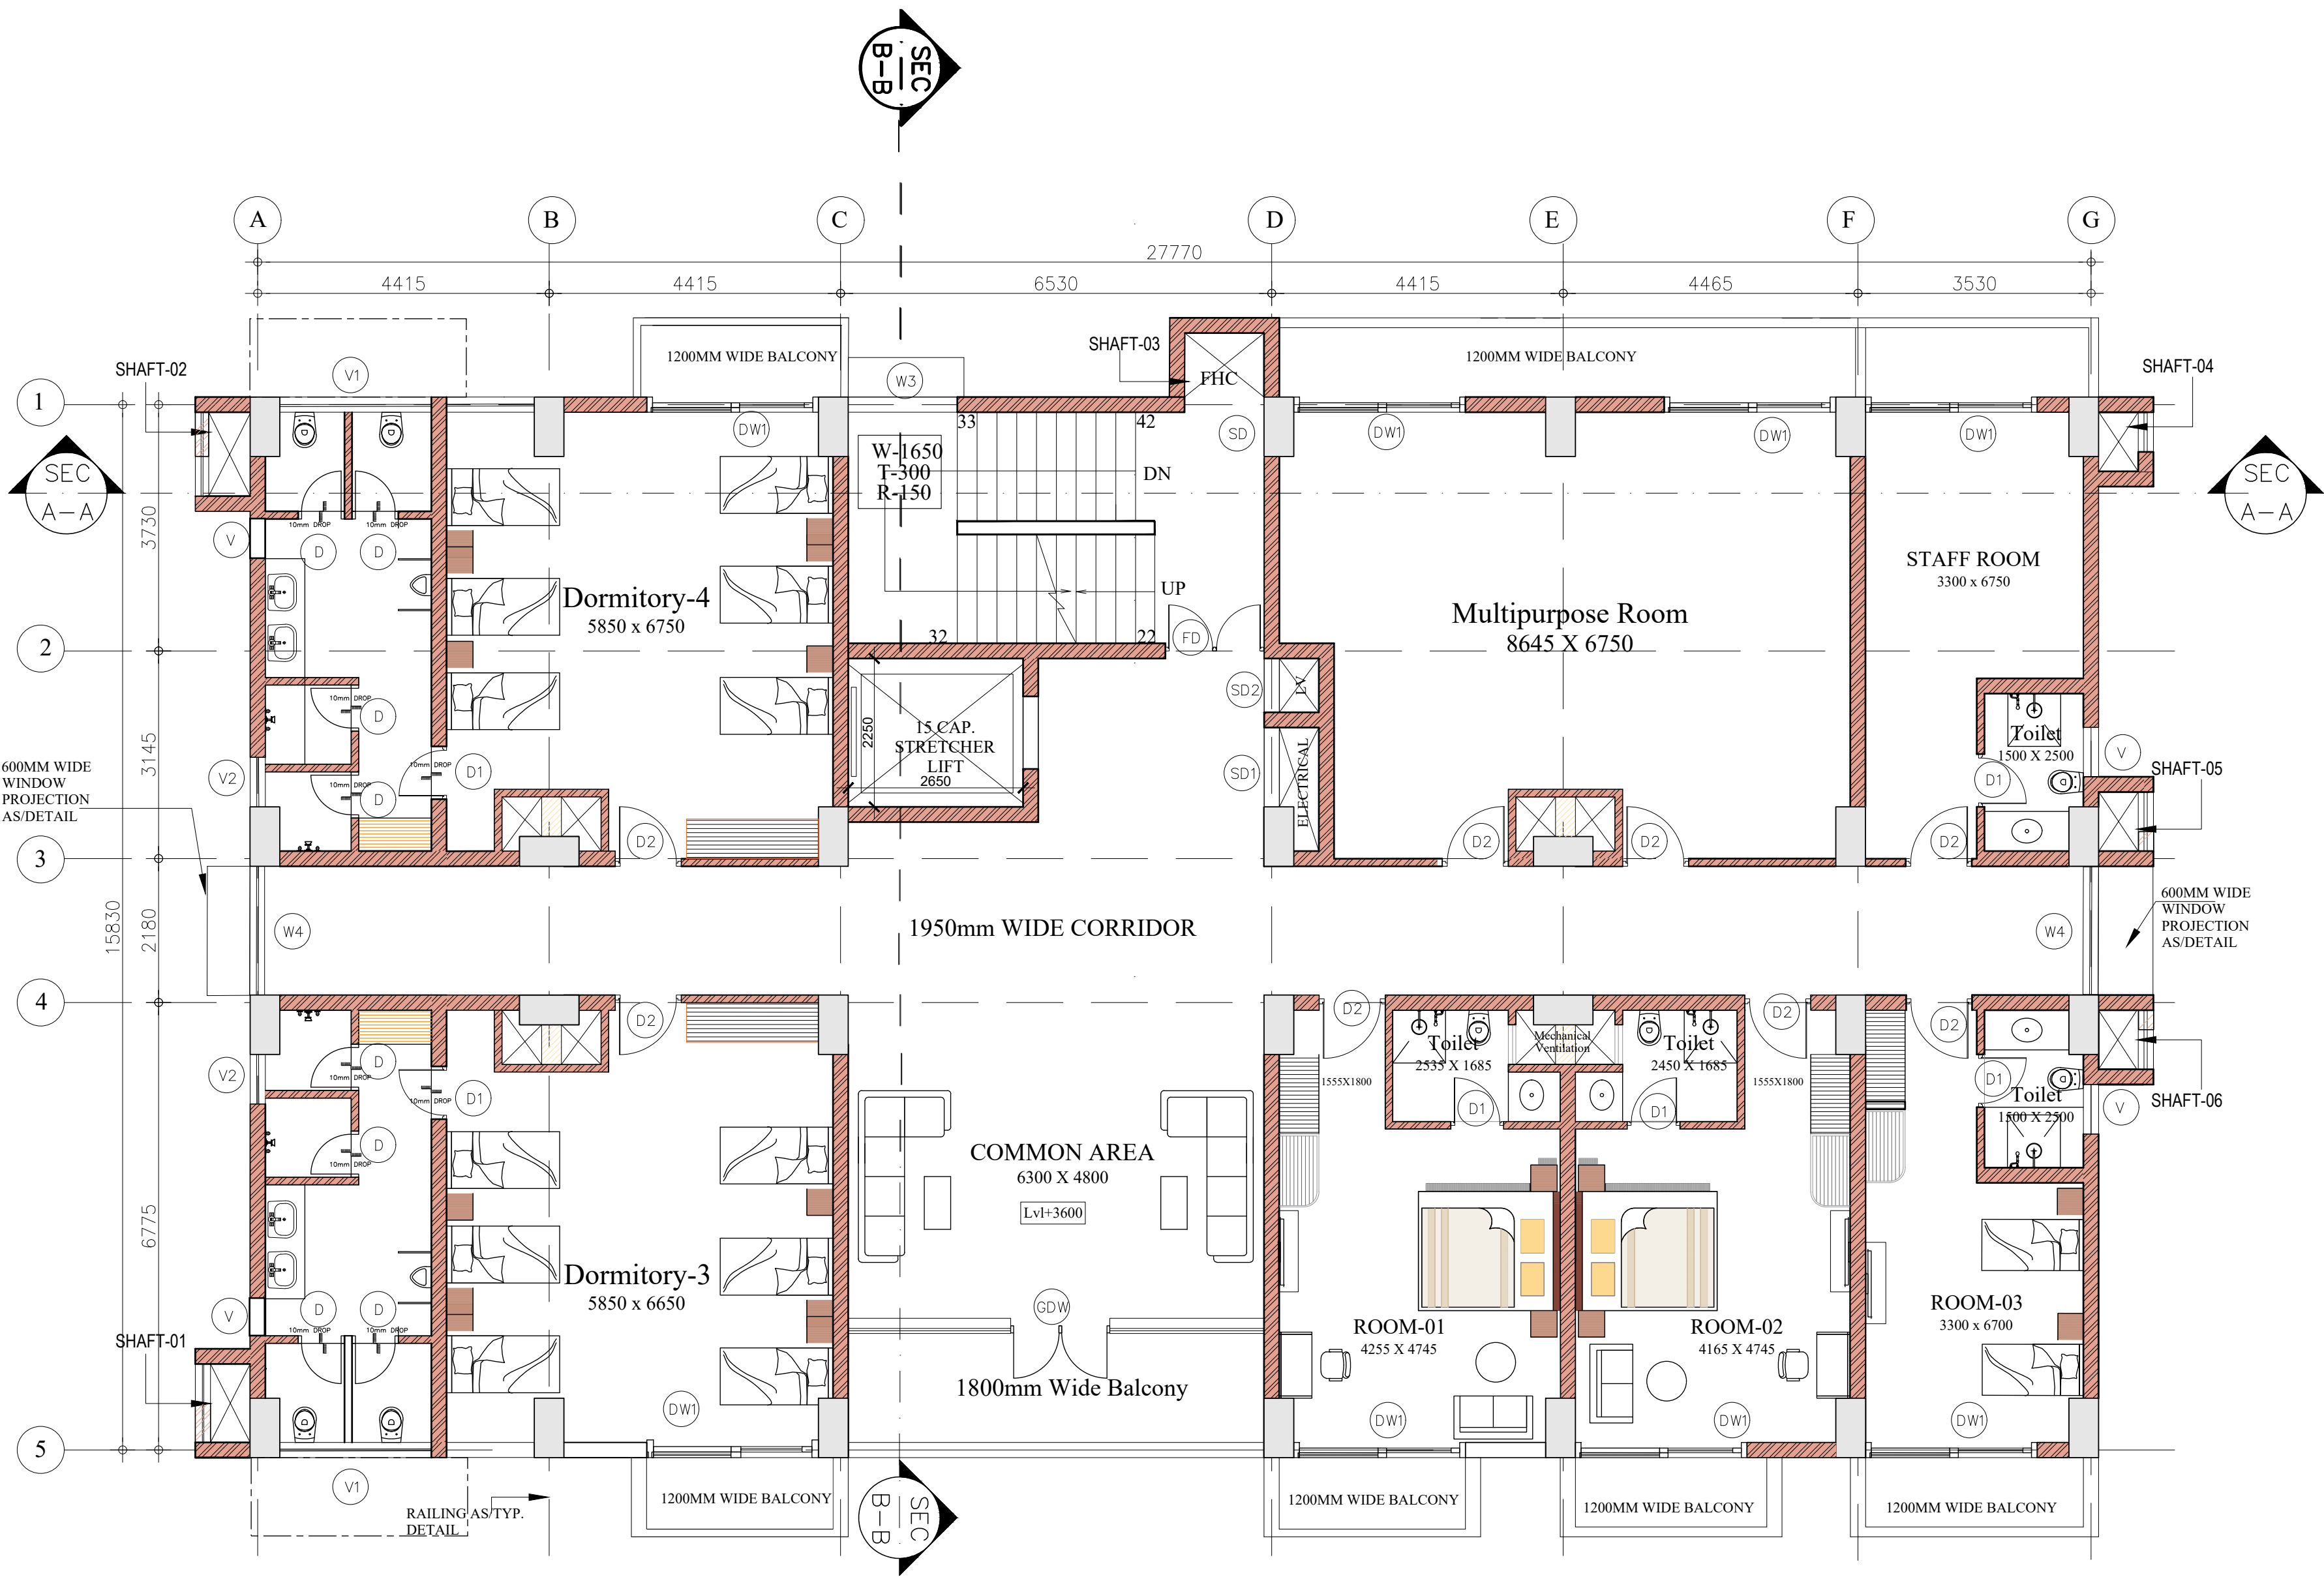


SCHEDULE OF DOORS - (Ground floor to Terrace floor)							
SL. NO	TYPE	NOS.	WIDTH	HEIGHT	CILL (from FFL)	LINTEL (from FFL)	REMARKS
1.	D	---	750	2100	00	2100	WC AND BATH
2.	D1	---	900	2100	00	2100	TOILETS
3.	D2	---	1000	2100	00	2100	ROOMS
4.	D3	---	1050	2100	00	2100	PWD TOILET
5.	D4	---	1500	2100	00	2100	SERVICE ENTRY
6.	DW1	---	2600	2100	00	2100	ROOM BALCONY
7.	GDW	---	6300	2400	00	2400	ENTRY
8.	GDW1	---	3230	2400	00	2400	BALCONY, DINING ENTRY
9.	FD	---	1500	2100	00	2100	STAIRCASE
10.	SD	---	900	2100	100	2100	FHC SHAFT
11.	SD1	---	900	2100	100	2100	ELE. SHAFT
12.	SD2	---	600	2100	100	2100	LV. SHAFT

SCHEDULE OF WINDOWS - (Ground floor to Terrace floor)						
SL. NO	TYPE	NOS.	WIDTH	HEIGHT	SILL (from FFL)	LINTEL (from FFL)
1.	W1	---	3100	1200	900	2100
2.	W2	---	3100	875	1225	2100
3.	W3	---	1650	1100	1000	2100
4.	W4	---	1950	1200	900	2100

SCHEDULE OF VENTILATORS - (Ground floor to Terrace floor)						
SL. NO	TYPE	NOS.	WIDTH	HEIGHT	SILL (from FFL)	LINTEL (from FFL)
1.	V	---	600	875	1225	2100
2.	V1	---	2295	450	2100	AS/SITE
2.	V2	---	900	450	2100	AS/SITE

SCHEDULE OF SHAFT JALI - (Ground floor to Terrace floor)							
SL. NO	TYPE	NOS.	WIDTH	HEIGHT	SILL (from FFL)	LINTEL (from FFL)	REMARKS
1.	JL	---	600	2550	+00	BEAM BOTTOM/AS PER STR.	ALUMINUM OPENABLE LOUVERED PANEL

KEY PLAN

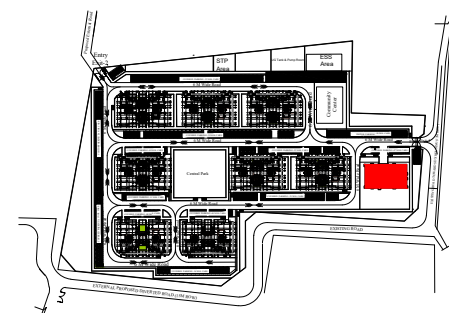


NOTES

- ALL DIMENSIONS ARE IN MM; UNLESS NOTED OTHERWISE.
- WRITTEN DIMENSIONS ARE TO BE FOLLOWED. DRAWINGS ARE NOT TO BE SCALED.
- ANY DISCREPANCY IN THE DRAWING SHALL BE BROUGHT TO THE NOTICE OF THE ENGINEER.
- THIS DRAWING SHALL BE READ IN CONJUNCTION WITH OTHER RELEVANT DRAWINGS.
- MOVABLE EQUIPMENT AND FURNISHINGS SUCH AS BED, WARDROBE, GEYSERS, TV, TABLE CHAIRS, ETC. ARE SHOWN FOR ILLUSTRATIVE PURPOSES ONLY (FOR MEP DETAILING) AND ARE NOT TO BE PROVIDED. REFER TENDER DOCUMENT FOR DETAILS OF FUR./EQP. TO BE PROVIDED.
- STRUCTURE DRAWING TO BE FOLLOWED FOR COLUMN SIZES

Sn.No.	Description	Area (Sqm)
01	Ground Floor Area	465 sqm
02	First Floor Area	495 sqm
03	Second Floor Area	500 sqm
04	Third Floor Area	500 sqm
05	Mumty Area	30 sqm

TENDER DRAWING

CLIENT	 OIL INDIA LIMITED (A Govt. of India Enterprise)	
CONSULTANT	 RITES THE INFRASTRUCTURE PEOPLE (A Govt. of India Enterprise)	
PROJECT	BQ WORKMEN HOUSING	
BUILDING	GUEST HOUSE (G+3)	
DRAWING TITLE	FIRST FLOOR PLAN	
DRG. NO.	MITES/BLD/AR/TD/029	
NORTH	SCALE	DATE
	NTS	JULY 2025

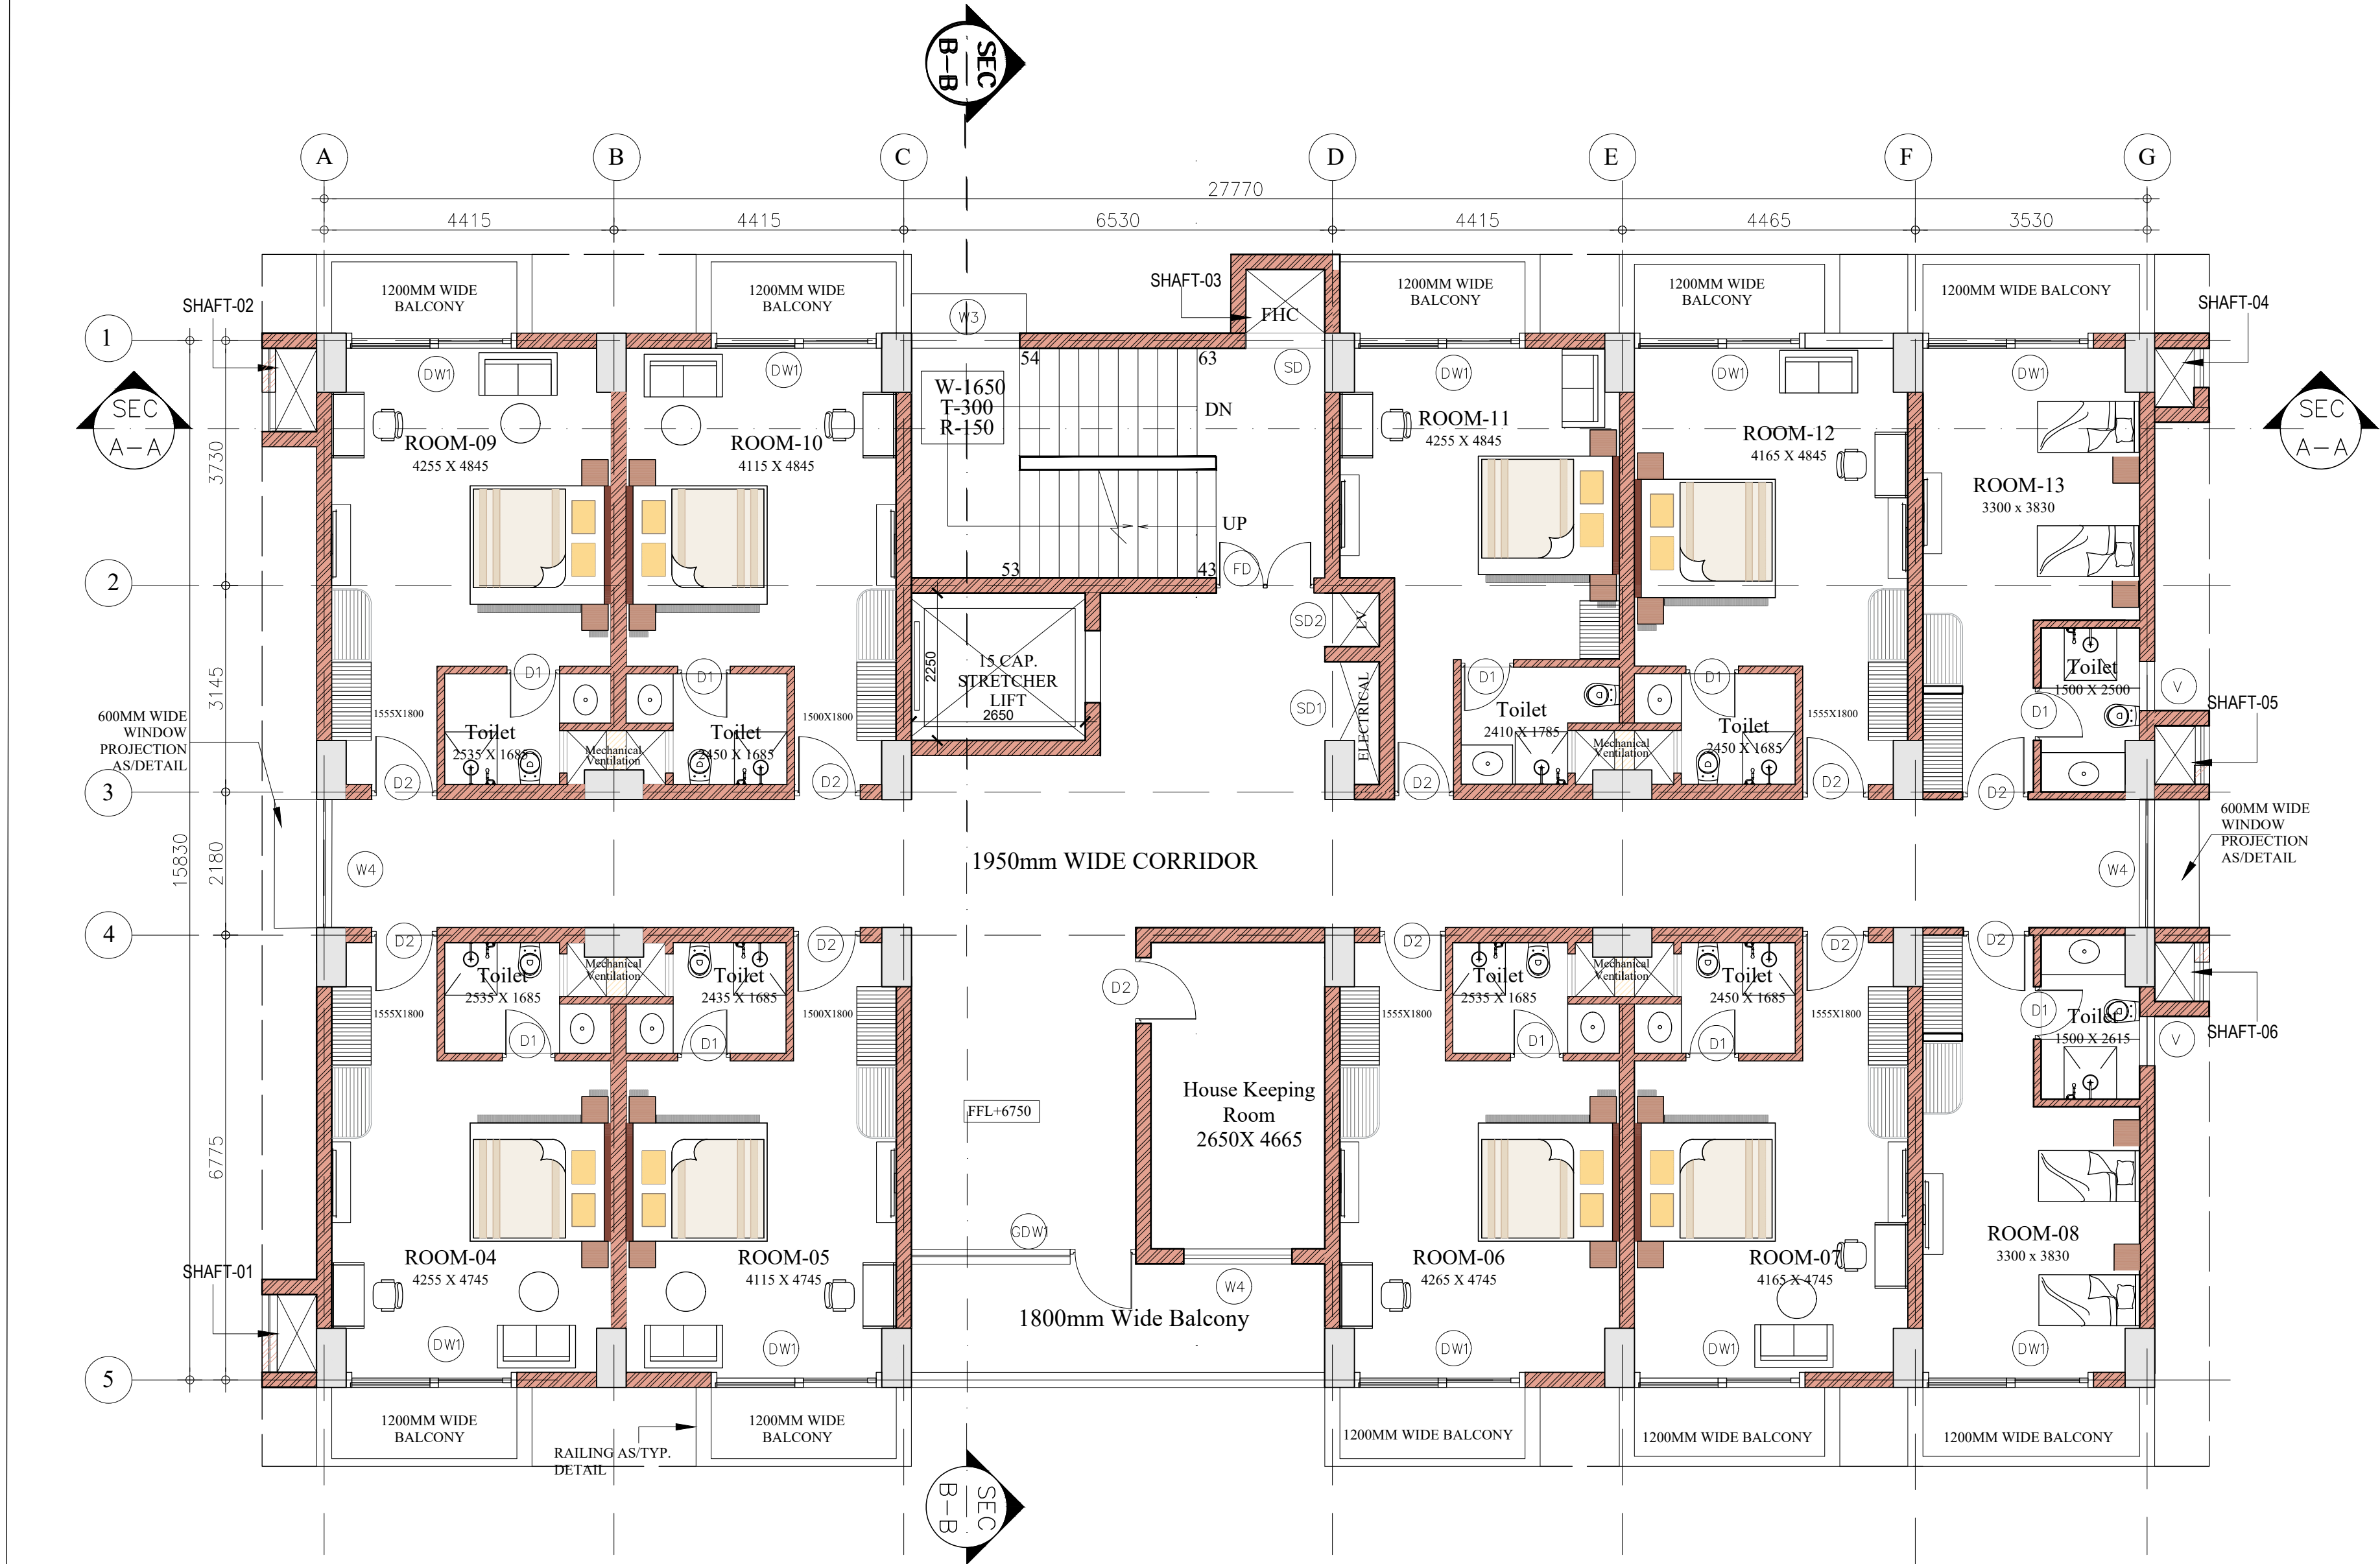

SCHEDULE OF DOORS - (Ground floor to Terrace floor)									
SL. NO	TYPE	NOS.	WIDTH	HEIGHT (from FFL)	CILL (from FFL)	LINTEL (from FFL)	LOCATION	REMARKS	
SCHEDULE OF DOORS									
1.	D	---	750	2100	00	2100	WC AND BATH	WPC DOOR PANEL WITH FRAME AS/DRAWING	
2.	D1	---	900	2100	00	2100	TOILETS	WPC DOOR PANEL WITH FRAME AS/DRAWING	
3.	D2	---	1000	2100	00	2100	ROOMS	SINGLE LEAF TEAK WOOD FRAME, FLUSH DOOR AS/DRAWING	
4.	D3	---	1050	2100	00	2100	PWD TOILET	WPC DOOR PANEL WITH FRAME AS/DRAWING	
5.	D4	---	1500	2100	00	2100	SERVICE ENTRY	DOUBLE LEAF TEAK WOOD FRAME, FLUSH DOOR AS/DRAWING	
6.	DW1	---	2600	2100	00	2100	ROOM BALCONY	UPVC THREE TRACK THREE PANELS SLIDING DOOR WITH TWO GLAZED & ONE WIRE MESH PANELS AS/DRAWING/SPECS.	
7.	GDW	---	6300	2400	00	2400	ENTRY	PIVOT FRAMELESS GLASS SWING DOOR (PAIR) WITH FRAMELESS FIXED GLASS PART. AS/DRAWING/SPECS WITH FROSTED FILM	
8.	GDW1	---	3230	2400	00	2400	BALCONY, DINING ENTRY	PIVOT FRAMELESS GLASS SWING DOOR (PAIR) WITH FRAMELESS FIXED GLASS PART. AS/DRAWING/SPECS WITH FROSTED FILM	
9.	FD	---	1500	2100	00	2100	STAIRCASE	2HR FIRE RATED METAL FIRE DOOR	
10.	SD	---	900	2100	100	2100	FHC SHAFT	M.S SINGLE LEAF DOOR WITH GLASS (FHC Shaft Door as per NBC & latest CPWD Guideline)	
11.	SD1	---	900	2100	100	2100	ELE. SHAFT	M.S SINGLE LEAF DOOR WITH VENTILATION AT TOP (Electrical Shaft Door as per NBC & latest CPWD Guideline)	
12.	SD2	---	600	2100	100	2100	LV. SHAFT	M.S SINGLE LEAF DOOR WITH VENTILATION AT TOP	

SCHEDULE OF WINDOWS - (Ground floor to Terrace floor)							
SL. NO	TYPE	NOS.	WIDTH	HEIGHT	SILL (from FFL)	LINTEL (from FFL)	REMARKS
1.	W1	---	3100	1200	900	2100	POWDER COATED ALUMINUM FRAMED SLIDING WINDOW - THREE TRACK SYSTEM WITH WIRE MESH AS/DRAWING
2.	W2	---	3100	875	1225	2100	POWDER COATED ALUMINUM FRAMED SLIDING WINDOW - THREE TRACK SYSTEM WITH WIRE MESH AS/DRAWING
3.	W3	---	1650	1100	1000	2100	POWDER COATED ALUMINUM FRAMED SLIDING WINDOW - TWO TRACK SYSTEM AS/DRAWING/SPECS
4.	W4	---	1950	1200	900	2100	POWDER COATED ALUMINUM FRAMED SLIDING WINDOW - THREE TRACK SYSTEM AS/DRAWING/SPECS
SCHEDULE OF VENTILATORS - (Ground floor to Terrace floor)							
SL. NO	TYPE	NOS.	WIDTH	HEIGHT	SILL (from FFL)	LINTEL (from FFL)	REMARKS
1.	V	---	600	875	1225	2100	POWDER-COATED ALUMINUM FRAME VENTILATOR WITH FIXED FROSTED GLASS PANELS AND INTEGRATED EXHAUST FAN AS/DRAWING/SPECS.
2.	V1	---	2295	450	2100	AS/SITE	POWDER-COATED ALUMINUM FRAME VENTILATOR WITH FIXED FROSTED GLASS PANELS AND INTEGRATED EXHAUST FAN AS/DRAWING/SPECS.
2.	V2	---	900	450	2100	AS/SITE	POWDER-COATED ALUMINUM FRAME VENTILATOR WITH FIXED FROSTED GLASS PANELS AND INTEGRATED EXHAUST FAN AS/DRAWING/SPECS.

SCHEDULE OF SHAFT JALI - (Ground floor to Terrace floor)							
SL. NO	TYPE	NOS.	WIDTH	HEIGHT	SILL (from FFL)	LINTEL (from FFL)	REMARKS
1.	JL	---	600	2550	+00	BEAM BOTTOM/AS PER STR.	ALUMINUM OPENABLE LOUVERED PANEL

KEY PLAN

NOTES

- ALL DIMENSIONS ARE IN MM, UNLESS NOTED OTHERWISE.
- WRITTEN DIMENSIONS ARE TO BE FOLLOWED. DRAWINGS ARE NOT TO BE SCALED.
- ANY DISCREPANCY IN THE DRAWING SHALL BE BROUGHT TO THE NOTICE OF THE ENGINEER.
- THIS DRAWING SHALL BE READ IN CONJUNCTION WITH OTHER RELEVANT DRAWINGS.
- MOVABLE EQUIPMENT AND FURNISHINGS SUCH AS BED, WARDROBE, GEYSERS, TV, TABLE CHAIRS, ETC. ARE SHOWN FOR ILLUSTRATIVE PURPOSES ONLY (FOR MEP DETAILING) AND ARE NOT TO BE PROVIDED. REFER TENDER DOCUMENT FOR DETAILS OF FUR./EQP. TO BE PROVIDED.
- STRUCTURE DRAWING TO BE FOLLOWED FOR COLUMN SIZES

Sn.No.	Description	Area (Sqm)
01	Ground Floor Area	465 sqm
02	First Floor Area	495 sqm
03	Second Floor Area	500 sqm
04	Third Floor Area	500 sqm
05	Mumty Area	30 sqm

TENDER DRAWING

CLIENTOIL INDIA LIMITED
(A Govt. of India Enterprise)

CONSULTANTRITES
THE INFRASTRUCTURE PEOPLE
(A Govt. of India Enterprise)

PROJECT
BQ WORKMEN HOUSING

BUILDING
GUEST HOUSE (G+3)


DRAWING TITLE
SECOND FLOOR PLAN

DRG. NO.
RITES/BLD/AR/TD/030

NORTH

SCALE
NTS

DATE
JULY 2025

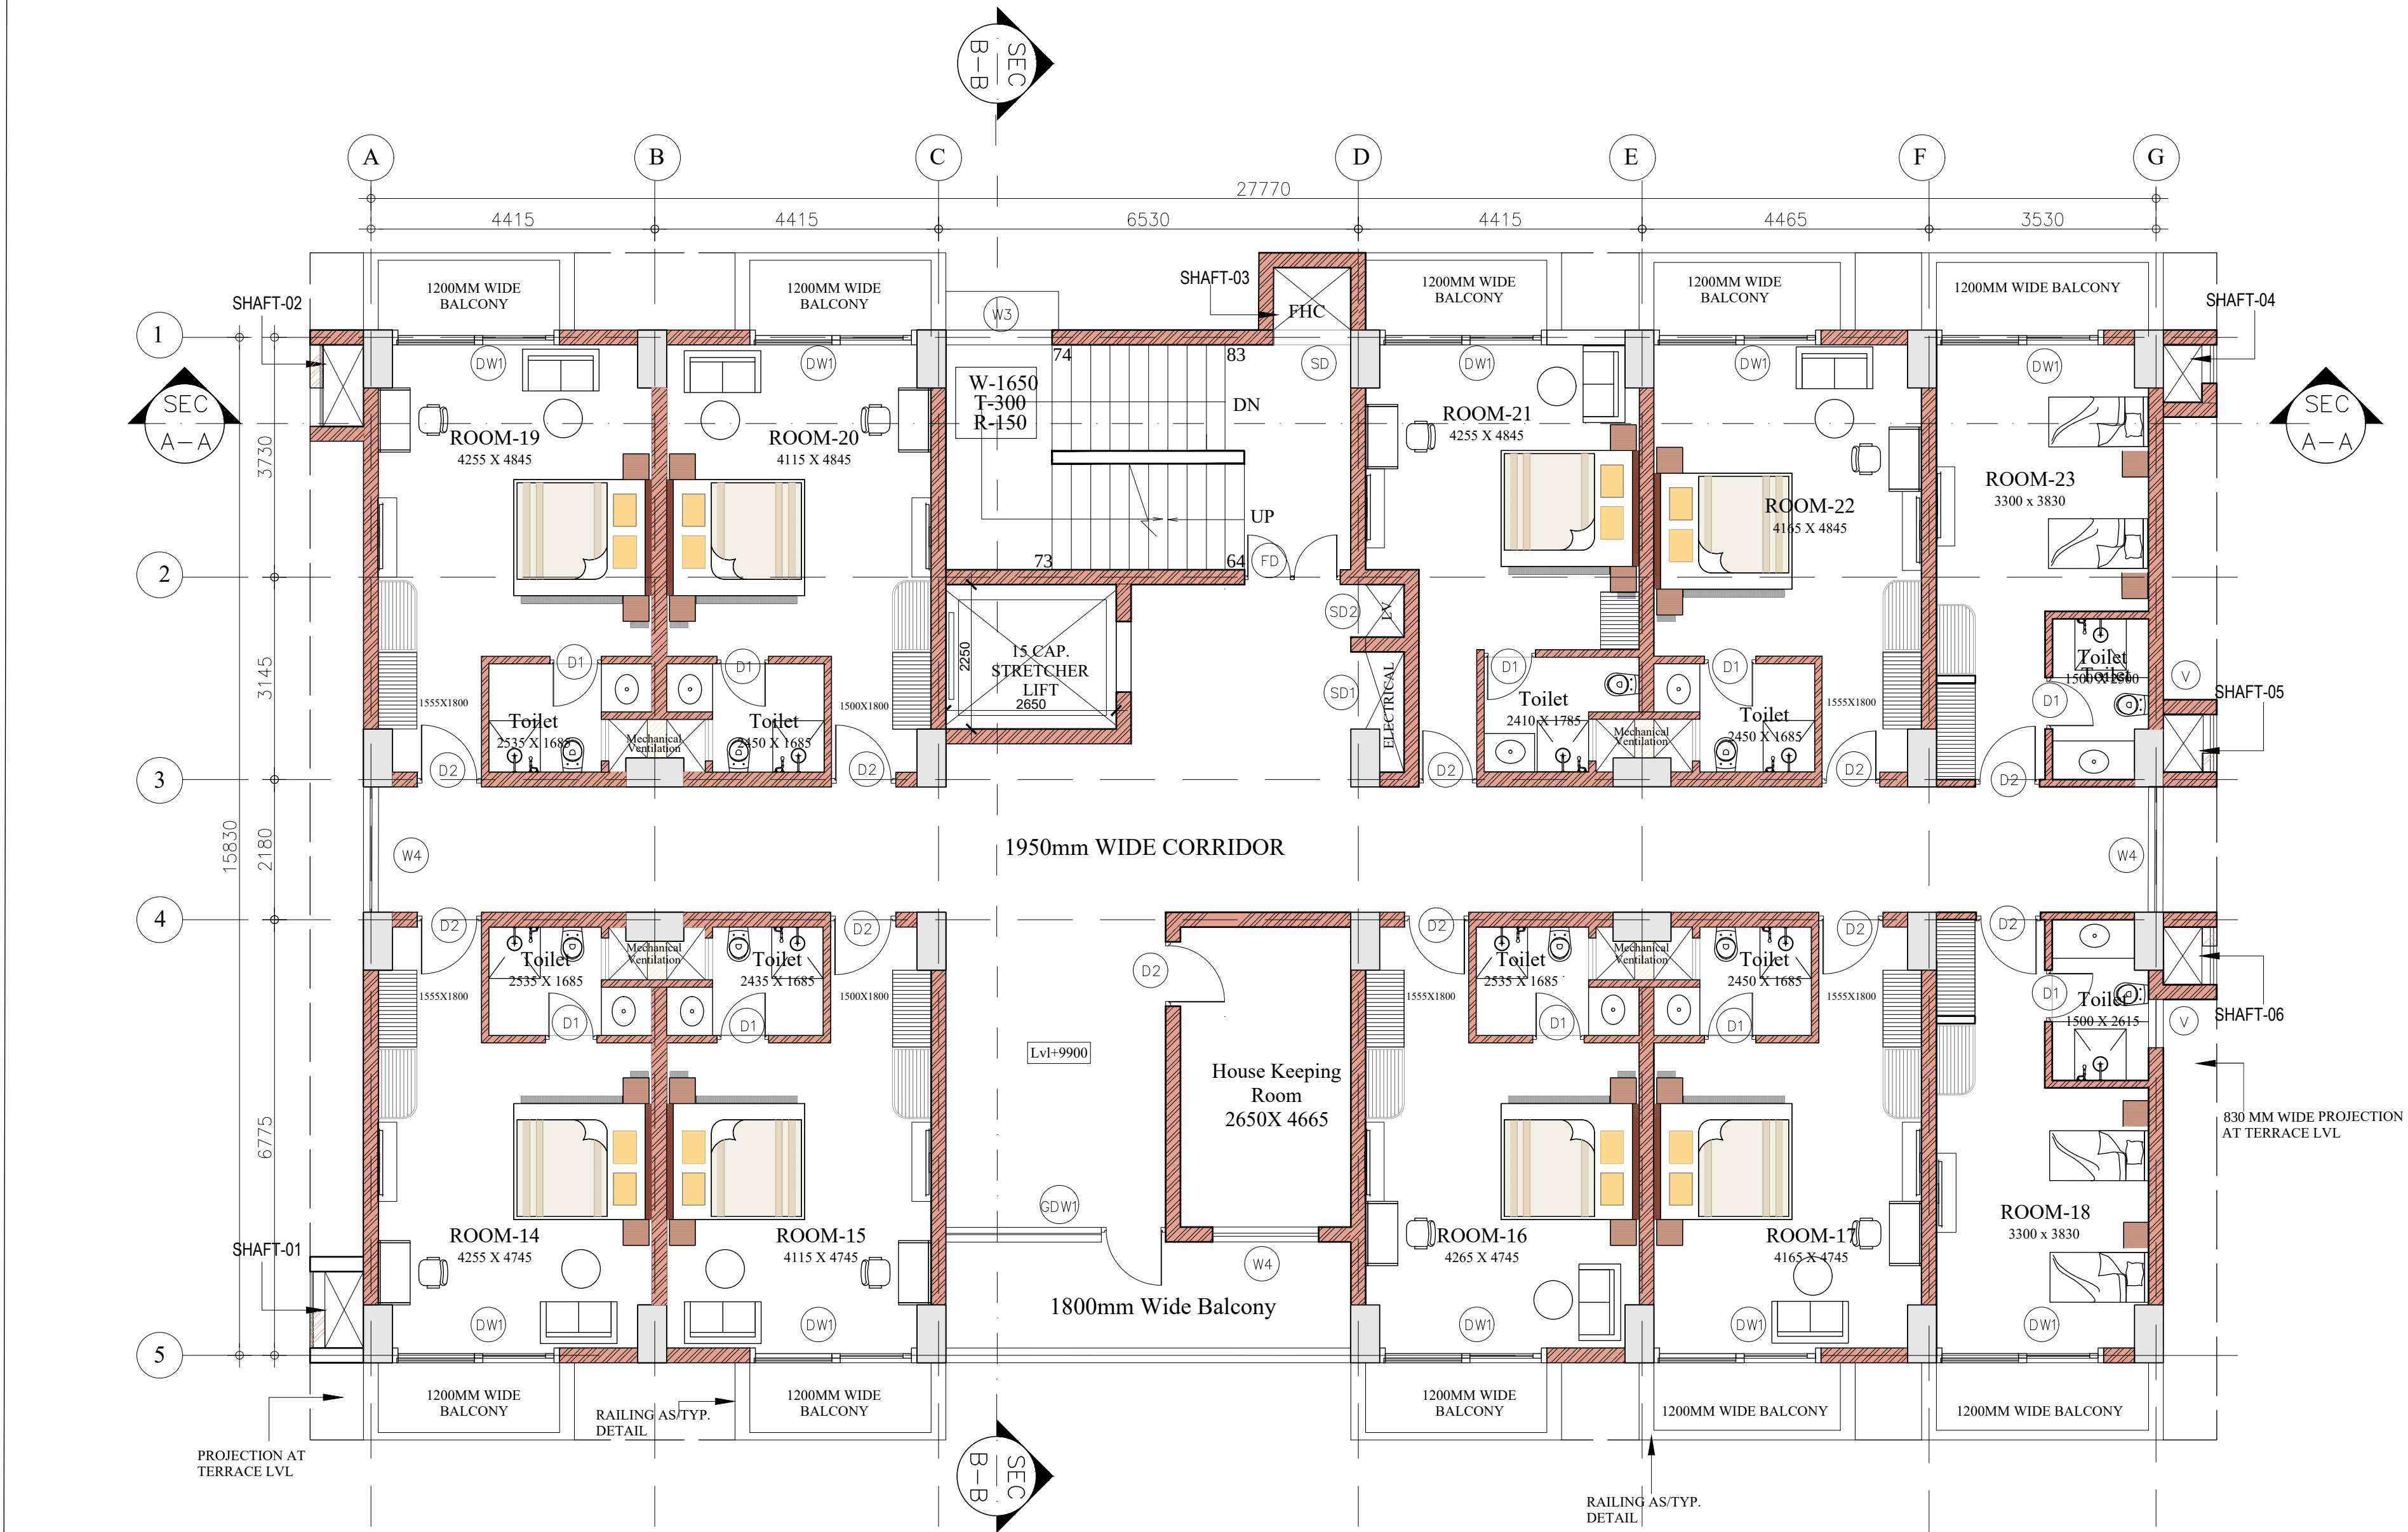


SCHEDULE OF DOORS - (Ground floor to Terrace floor)							
SL. NO	TYPE	NOS.	WIDTH	HEIGHT	CILL (from FFL)	LINTEL (from FFL)	REMARKS
1.	D	---	750	2100	00	2100	WC AND BATH
2.	D1	---	900	2100	00	2100	TOILETS
3.	D2	---	1000	2100	00	2100	ROOMS
4.	D3	---	1050	2100	00	2100	PWD TOILET
5.	D4	---	1500	2100	00	2100	SERVICE ENTRY
6.	DW1	---	2600	2100	00	2100	ROOM BALCONY
7.	GDW	---	6300	2400	00	2400	ENTRY
8.	GDW1	---	3230	2400	00	2400	BALCONY, DINING ENTRY
9.	FD	---	1500	2100	00	2100	STAIRCASE
10.	SD	---	900	2100	100	2100	FHC SHAFT
11.	SD1	---	900	2100	100	2100	ELE. SHAFT
12.	SD2	---	600	2100	100	2100	LV. SHAFT

SCHEDULE OF WINDOWS - (Ground floor to Terrace floor)							
SL. NO	TYPE	NOS.	WIDTH	HEIGHT	SILL (from FFL)	LINTEL (from FFL)	REMARKS
1.	W1	---	3100	1200	900	2100	POWDER COATED ALUMINUM FRAMED SLIDING WINDOW - THREE TRACK SYSTEM WITH WIRE MESH AS/DRAWING
2.	W2	---	3100	875	1225	2100	POWDER COATED ALUMINUM FRAMED SLIDING WINDOW - THREE TRACK SYSTEM WITH WIRE MESH AS/DRAWING
3.	W3	---	1650	1100	1000	2100	POWDER COATED ALUMINUM FRAMED SLIDING WINDOW - TWO TRACK SYSTEM AS/DRAWING/SPECS
4.	W4	---	1950	1200	900	2100	POWDER COATED ALUMINUM FRAMED SLIDING WINDOW - THREE TRACK SYSTEM AS/DRAWING/SPECS

SCHEDULE OF VENTILATORS - (Ground floor to Terrace floor)							
SL. NO	TYPE	NOS.	WIDTH	HEIGHT	SILL (from FFL)	LINTEL (from FFL)	REMARKS
1.	V	---	600	875	1225	2100	POWDER-COATED ALUMINUM FRAME VENTILATOR WITH FIXED FROSTED GLASS PANELS AND INTEGRATED EXHAUST FAN AS/DRAWING/SPECS
2.	V1	---	2295	450	2100	AS/SITE	POWDER-COATED ALUMINUM FRAME VENTILATOR WITH FIXED FROSTED GLASS PANELS AND INTEGRATED EXHAUST FAN AS/DRAWING/SPECS
2.	V2	---	900	450	2100	AS/SITE	POWDER-COATED ALUMINUM FRAME VENTILATOR WITH FIXED FROSTED GLASS PANELS AND INTEGRATED EXHAUST FAN AS/DRAWING/SPECS

SCHEDULE OF SHAFT JALI - (Ground floor to Terrace floor)							
SL. NO	TYPE	NOS.	WIDTH	HEIGHT	SILL (from FFL)	LINTEL (from FFL)	REMARKS
1.	JL	---	600	2550	+00	BEAM BOTTOM/AS PER STR.	ALUMINUM OPENABLE LOUVERED PANEL

KEY PLAN

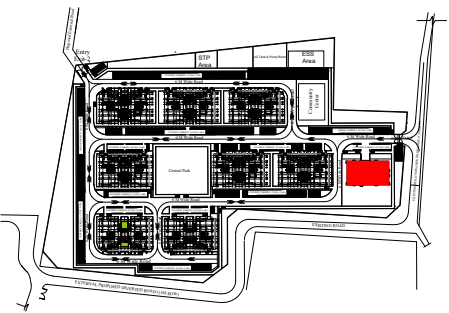

NOTES

- ALL DIMENSIONS ARE IN MM, UNLESS NOTED OTHERWISE.
- WRITTEN DIMENSIONS ARE TO BE FOLLOWED. DRAWINGS ARE NOT TO BE SCALED.
- ANY DISCREPANCY IN THE DRAWING SHALL BE BROUGHT TO THE NOTICE OF THE ENGINEER.
- THIS DRAWING SHALL BE READ IN CONJUNCTION WITH OTHER RELEVANT DRAWINGS.
- MOVABLE EQUIPMENT AND FURNISHINGS SUCH AS BED, WARDROBE, GEYSERS, TV, TABLE CHAIRS, ETC. ARE SHOWN FOR ILLUSTRATIVE PURPOSES ONLY (FOR MEP DETAILING) AND ARE NOT TO BE PROVIDED. REFER TENDER DOCUMENT FOR DETAILS OF FUR./EQP. TO BE PROVIDED.
- STRUCTURE DRAWING TO BE FOLLOWED FOR COLUMN SIZES

Sn.No.	Description	Area (Sqm)
01	Ground Floor Area	465 sqm
02	First Floor Area	495 sqm
03	Second Floor Area	500 sqm
04	Third Floor Area	500 sqm
05	Mumty Area	30 sqm

TENDER DRAWING

CLIENT OIL INDIA LIMITED
(A Govt. of India Enterprise)

CONSULTANT RITES
THE INFRASTRUCTURE PEOPLE
(A Govt. of India Enterprise)


PROJECT BQ WORKMEN HOUSING

BUILDING GUEST HOUSE (G+3)

DRAWING TITLE THIRD FLOOR PLAN

DRG. NO. RITES/BLD/AR/TD/031

NORTH SCALE NTS DATE JULY 2025

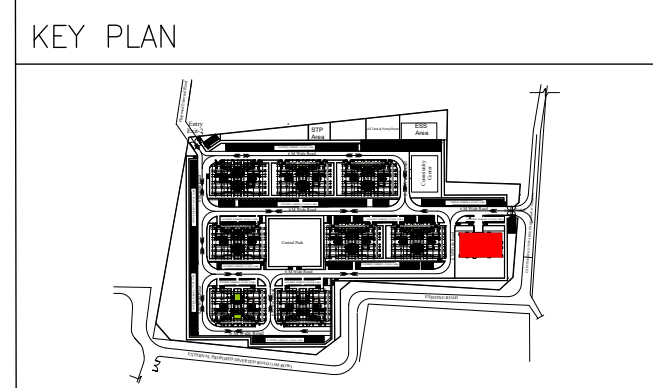

NOTES	
1.	ALL DIMENSIONS ARE IN MM; UNLESS NOTED OTHERWISE.
2.	WRITTEN DIMENSIONS ARE TO BE FOLLOWED. DRAWINGS ARE NOT TO BE SCALED.
3.	ANY DISCREPANCY IN THE DRAWING SHALL BE BROUGHT TO THE NOTICE OF THE ENGINEER.
4.	THIS DRAWING SHALL BE READ IN CONJUNCTION WITH OTHER RELEVANT DRAWINGS.

Sn.No.	Description	Area (Sq.m)
01	Ground Floor Area	465 sqm
02	First Floor Area	495 sqm
03	Second Floor Area	500 sqm
04	Third Floor Area	500 sqm
05	Mumty Area	30 sqm

TENDER DRAWING

CLIENT  **OIL INDIA LIMITED**
(A Govt. of India Enterprise)

CONSULTANT

IRITES
THE INFRASTRUCTURE PEOPLE
(A Govt. of India Enterprise)

PROJECT

BQ WORKMEN HOUSING

BUILDING	GUEST HOUSE (G+3)
----------	--------------------------

DRAWING TITLE

TERRACE FLOOR PLAN

DRG. NO.	RITES/BLD/AR/TD/032
----------	---


NORTH 	SCALE NTS	DATE JULY 2025
--	-------------------------	------------------------------

SCHEDULE OF DOORS - (Ground floor to Terrace floor)									
SL. NO	TYPE	NOS.	WIDTH	HEIGHT (from FFL)	CILL (from FFL)	LINTEL (from FFL)	LOCATION	REMARKS	
SCHEDULE OF DOORS									
1.	D	---	750	2100	00	2100	WC AND BATH	WPC DOOR PANEL WITH FRAME AS/DRAWING/SPECS	
2.	D1	---	900	2100	00	2100	TOILETS	WPC DOOR PANEL WITH FRAME AS/DRAWING/SPECS	
3.	D2	---	1000	2100	00	2100	ROOMS	SINGLE LEAF TEAK WOOD FRAME, FLUSH DOOR AS/DRAWING/SPECS	
4.	D3	---	1050	2100	00	2100	PWD TOILET	WPC DOOR PANEL WITH FRAME AS/DRAWING/SPECS	
5.	D4	---	1500	2100	00	2100	SERVICE ENTRY	DOUBLE LEAF TEAK WOOD FRAME, FLUSH DOOR AS/DRAWING/SPECS	
6.	GDW1	---	2600	2100	00	2100	ROOM BALCONY	UPVC THREE LEAF THREE PANELS SLIDING DOOR WITH TWO GLAZED & ONE WIRE MESH PANEL AS/DRAWING/SPECS	
7.	GDW	---	6300	2400	00	2400	ENTRY	PIVOT FRAMELESS GLASS SWING DOOR (PAIR) WITH FRAMELESS FIXED GLASS PART. AS/DRAWING/SPECS	
8.	GDW1	---	3230	2400	00	2400	BALCONY, DINING ENTRY	PIVOT FRAMELESS GLASS SWING DOOR (PAIR) WITH FRAMELESS FIXED GLASS PART. AS/DRAWING/SPECS	
9.	FD	---	1500	2100	00	2100	STAIRCASE	2HR FIRE RATED METAL FIRE DOOR AS/DRAWING/SPECS	
10.	SD	---	900	2100	100	2100	FHC SHAFT	M.S SINGLE LEAF DOOR WITH GLASS (FHC Shaft Door) as per NBC & latest CPWD Guideline)	
11.	SD1	---	900	2100	100	2100	ELE. SHAFT	M.S SINGLE LEAF DOOR WITH VENTILATION AT TOP (Electrical Shaft Door) as per NBC & latest CPWD Guideline)	
12.	SD2	---	600	2100	100	2100	L.V. SHAFT	M.S SINGLE LEAF DOOR WITH VENTILATION AT TOP AS/DRAWING/SPECS	

SCHEDULE OF WINDOWS - (Ground floor to Terrace floor)							REMARKS
SL. NO	TYPE	NOS.	WIDTH	HEIGHT	SILL (from FFL)	LINTEL (from FFL)	
1.	W1	---	3100	1200	900	2100	POWDER COATED ALUMINUM FRAMED SLIDING WINDOW - THREE TRACK SYSTEM WITH WIRE MESH AS/DRAWING
2.	W2	---	3100	875	1225	2100	POWDER COATED ALUMINUM FRAMED SLIDING WINDOW - THREE TRACK SYSTEM WITH WIRE MESH AS/DRAWING
3.	W3	---	1650	1100	1000	2100	POWDER COATED ALUMINUM FRAMED SLIDING WINDOW - TWO TRACK SYSTEM AS/DRAWING/SPECS
4.	W4	---	1950	1200	900	2100	POWDER COATED ALUMINUM FRAMED SLIDING WINDOW - THREE TRACK SYSTEM WITH WIRE MESH AS/DRAWING

SCHEDULE OF VENTILATORS - (Ground floor to Terrace floor)							
SL. NO	TYPE	NOS.	WIDTH	HEIGHT	SILL (from FFL)	LINTEL (from FFL)	REMARKS
1.	V	---	600	875	1225	2100	POWDER-COATED ALUMINUM FRAME VENTILATOR WITH FIXED FROSTED GLASS PANELS AND INTEGRATED EXHAUST FAN AS/DRAWING/SPCS
2.	V1	---	2295	450	2100	AS/SITE	POWDER-COATED ALUMINUM FRAME VENTILATOR WITH FIXED FROSTED GLASS PANELS
2.	V2	---	900	450	2100	AS/SITE	POWDER-COATED ALUMINUM FRAME VENTILATOR WITH FIXED FROSTED GLASS PANELS AS/DRAWING/SPCS

SL. NO	TYPE	NOS.	WIDTH	HEIGHT	SILL (from FFL)	LINTEL (from FFL)	REMARKS
1.	JL	---	600	2550	+00	BEAM BOTTOM/AS PER STR.	ALUMINUM OPENABLE LOUVERED PANEL

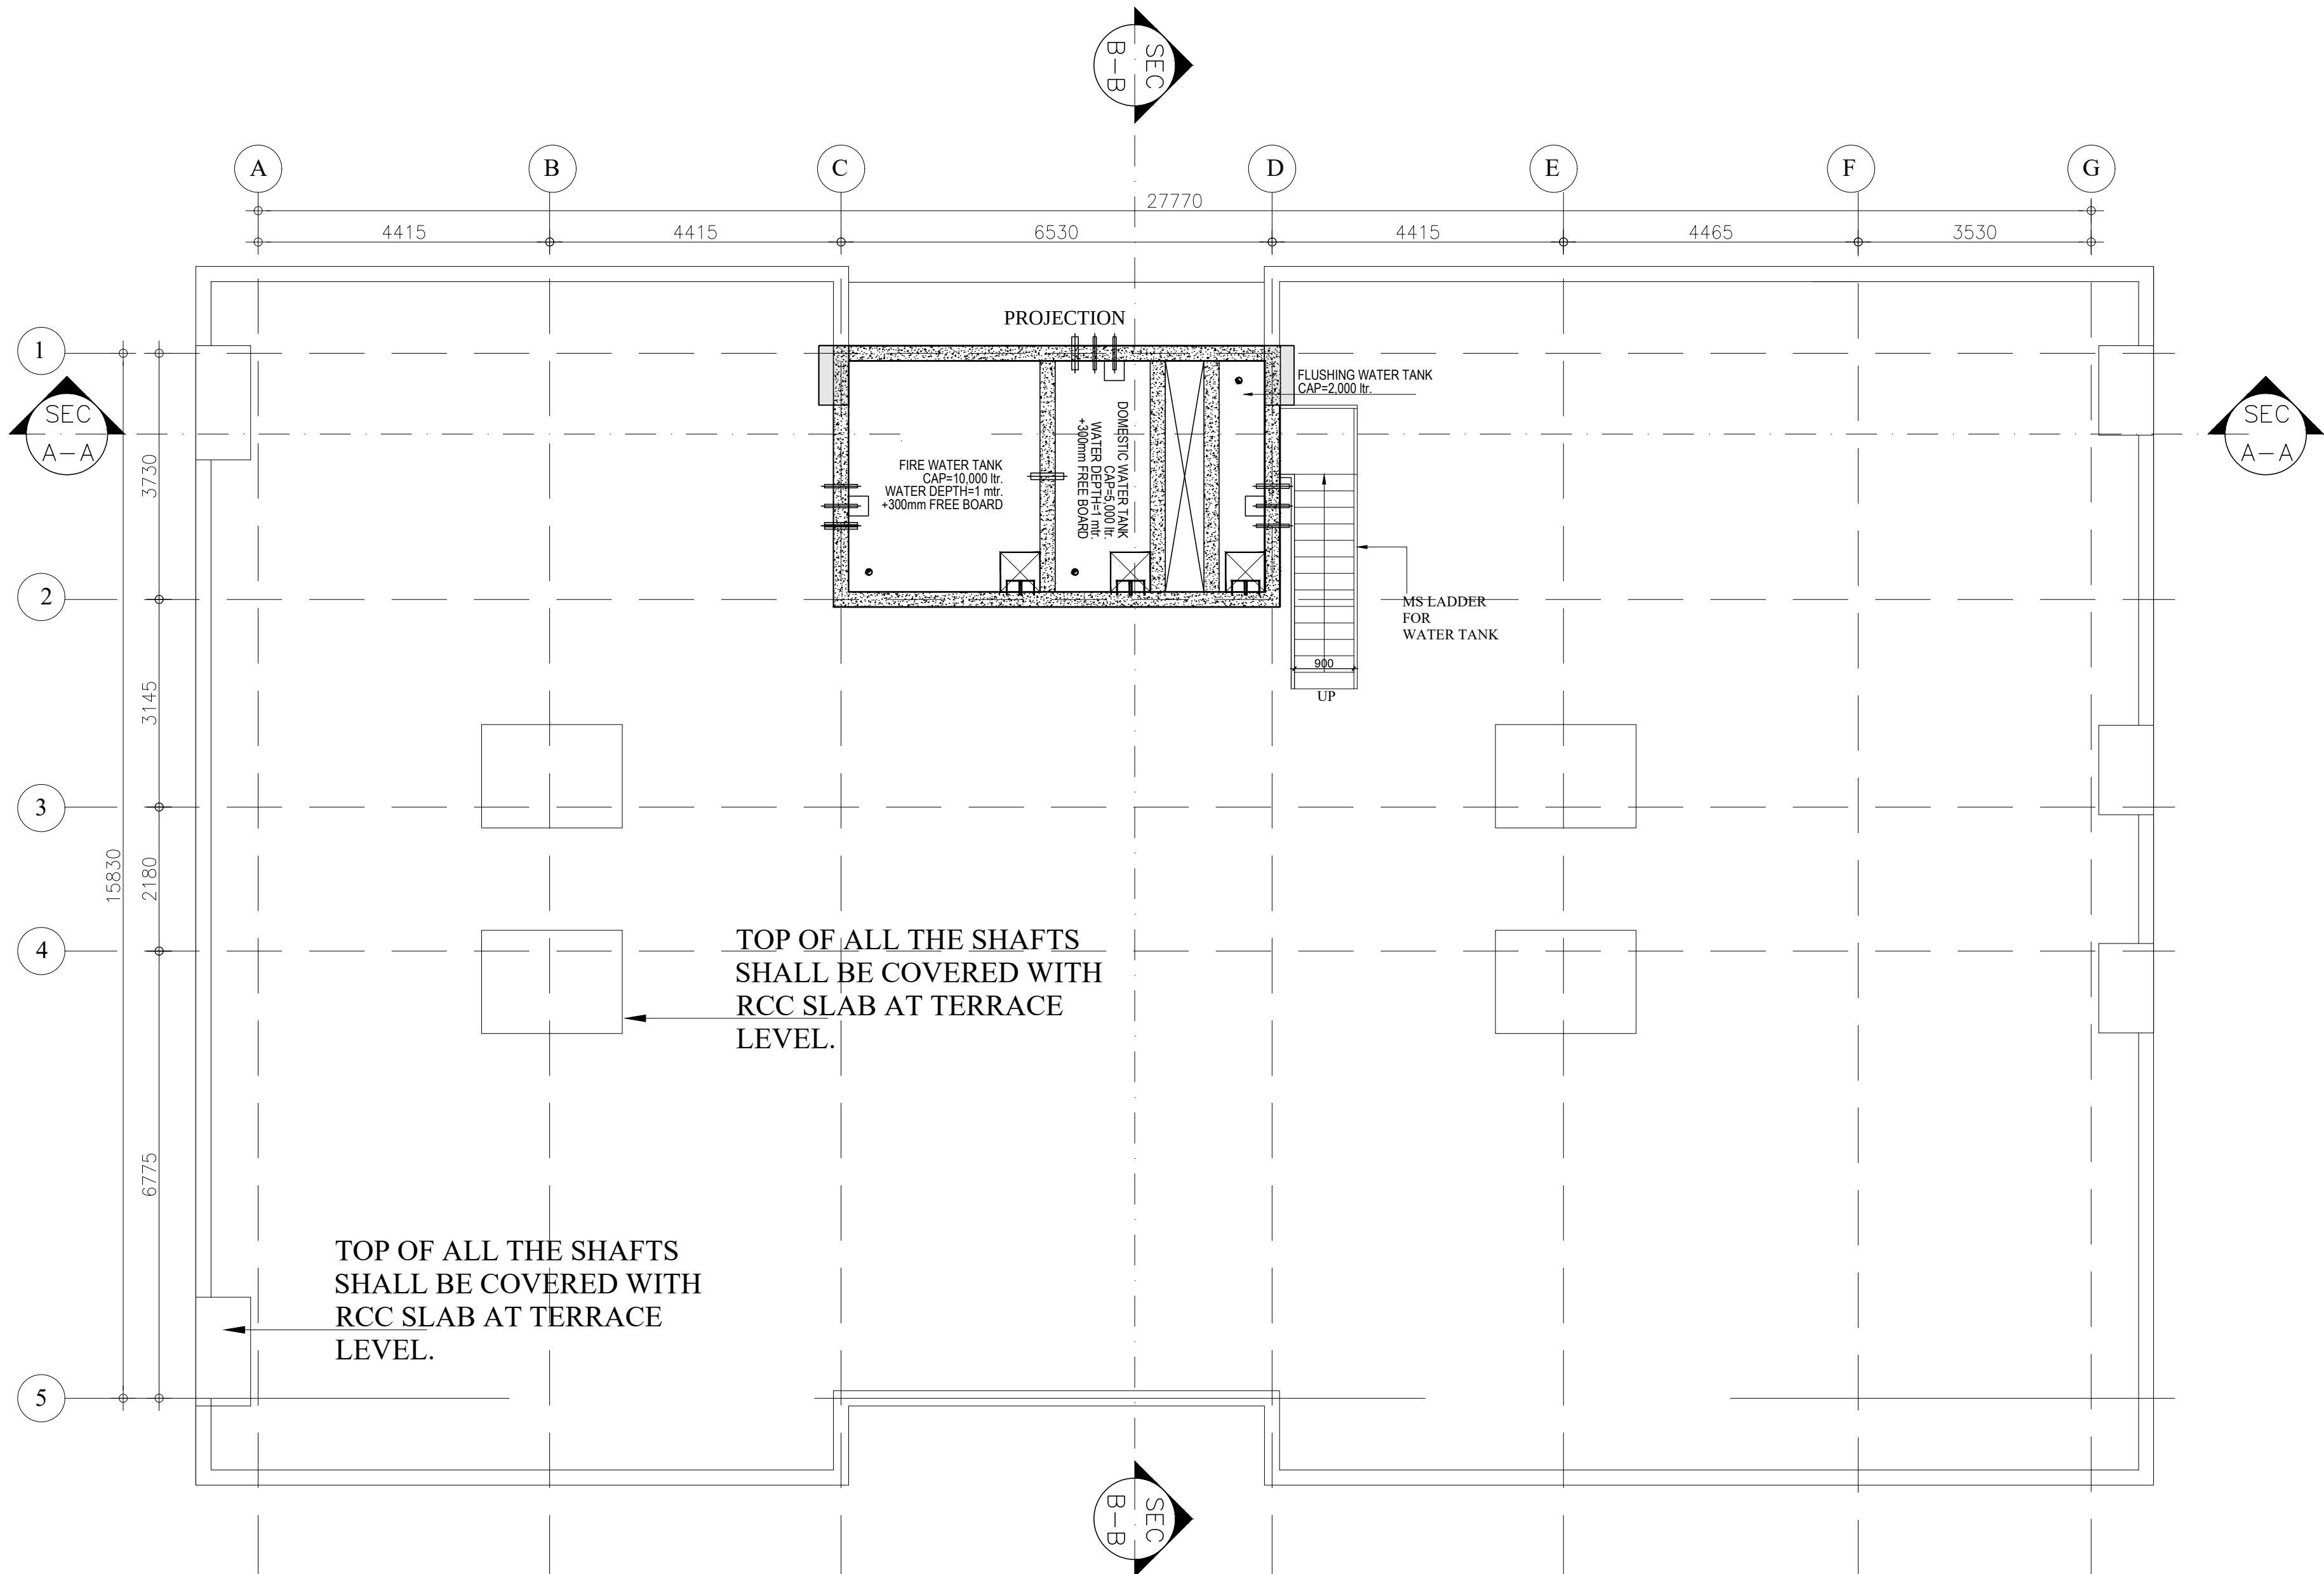

KEY PLAN

NOTES

- ALL DIMENSIONS ARE IN MM; UNLESS NOTED OTHERWISE.
- WRITTEN DIMENSIONS ARE TO BE FOLLOWED. DRAWINGS ARE NOT TO BE SCALED.
- ANY DISCREPANCY IN THE DRAWING SHALL BE BROUGHT TO THE NOTICE OF THE ENGINEER.
- THIS DRAWING SHALL BE READ IN CONJUNCTION WITH OTHER RELEVANT DRAWINGS.

Sn.No.	Description	Area (Sqm)
01	Ground Floor Area	465 sqm
02	First Floor Area	495 sqm
03	Second Floor Area	500 sqm
04	Third Floor Area	500 sqm
05	Mumty Area	30 sqm

TENDER DRAWING

CLIENT

OIL INDIA LIMITED
(A Govt. of India Enterprise)

CONSULTANT

RITES
THE INFRASTRUCTURE PEOPLE
(A Govt. of India Enterprise)

PROJECT

BQ WORKMEN HOUSING

BUILDING

GUEST HOUSE (G+3)

DRAWING TITLE

MUMTY ROOF PLAN

DRG. NO.

RITES/BLD/AR/TD/033

NORTH

SCALE


NTS

DATE

JULY 2025




FRONT ELEVATION (A)

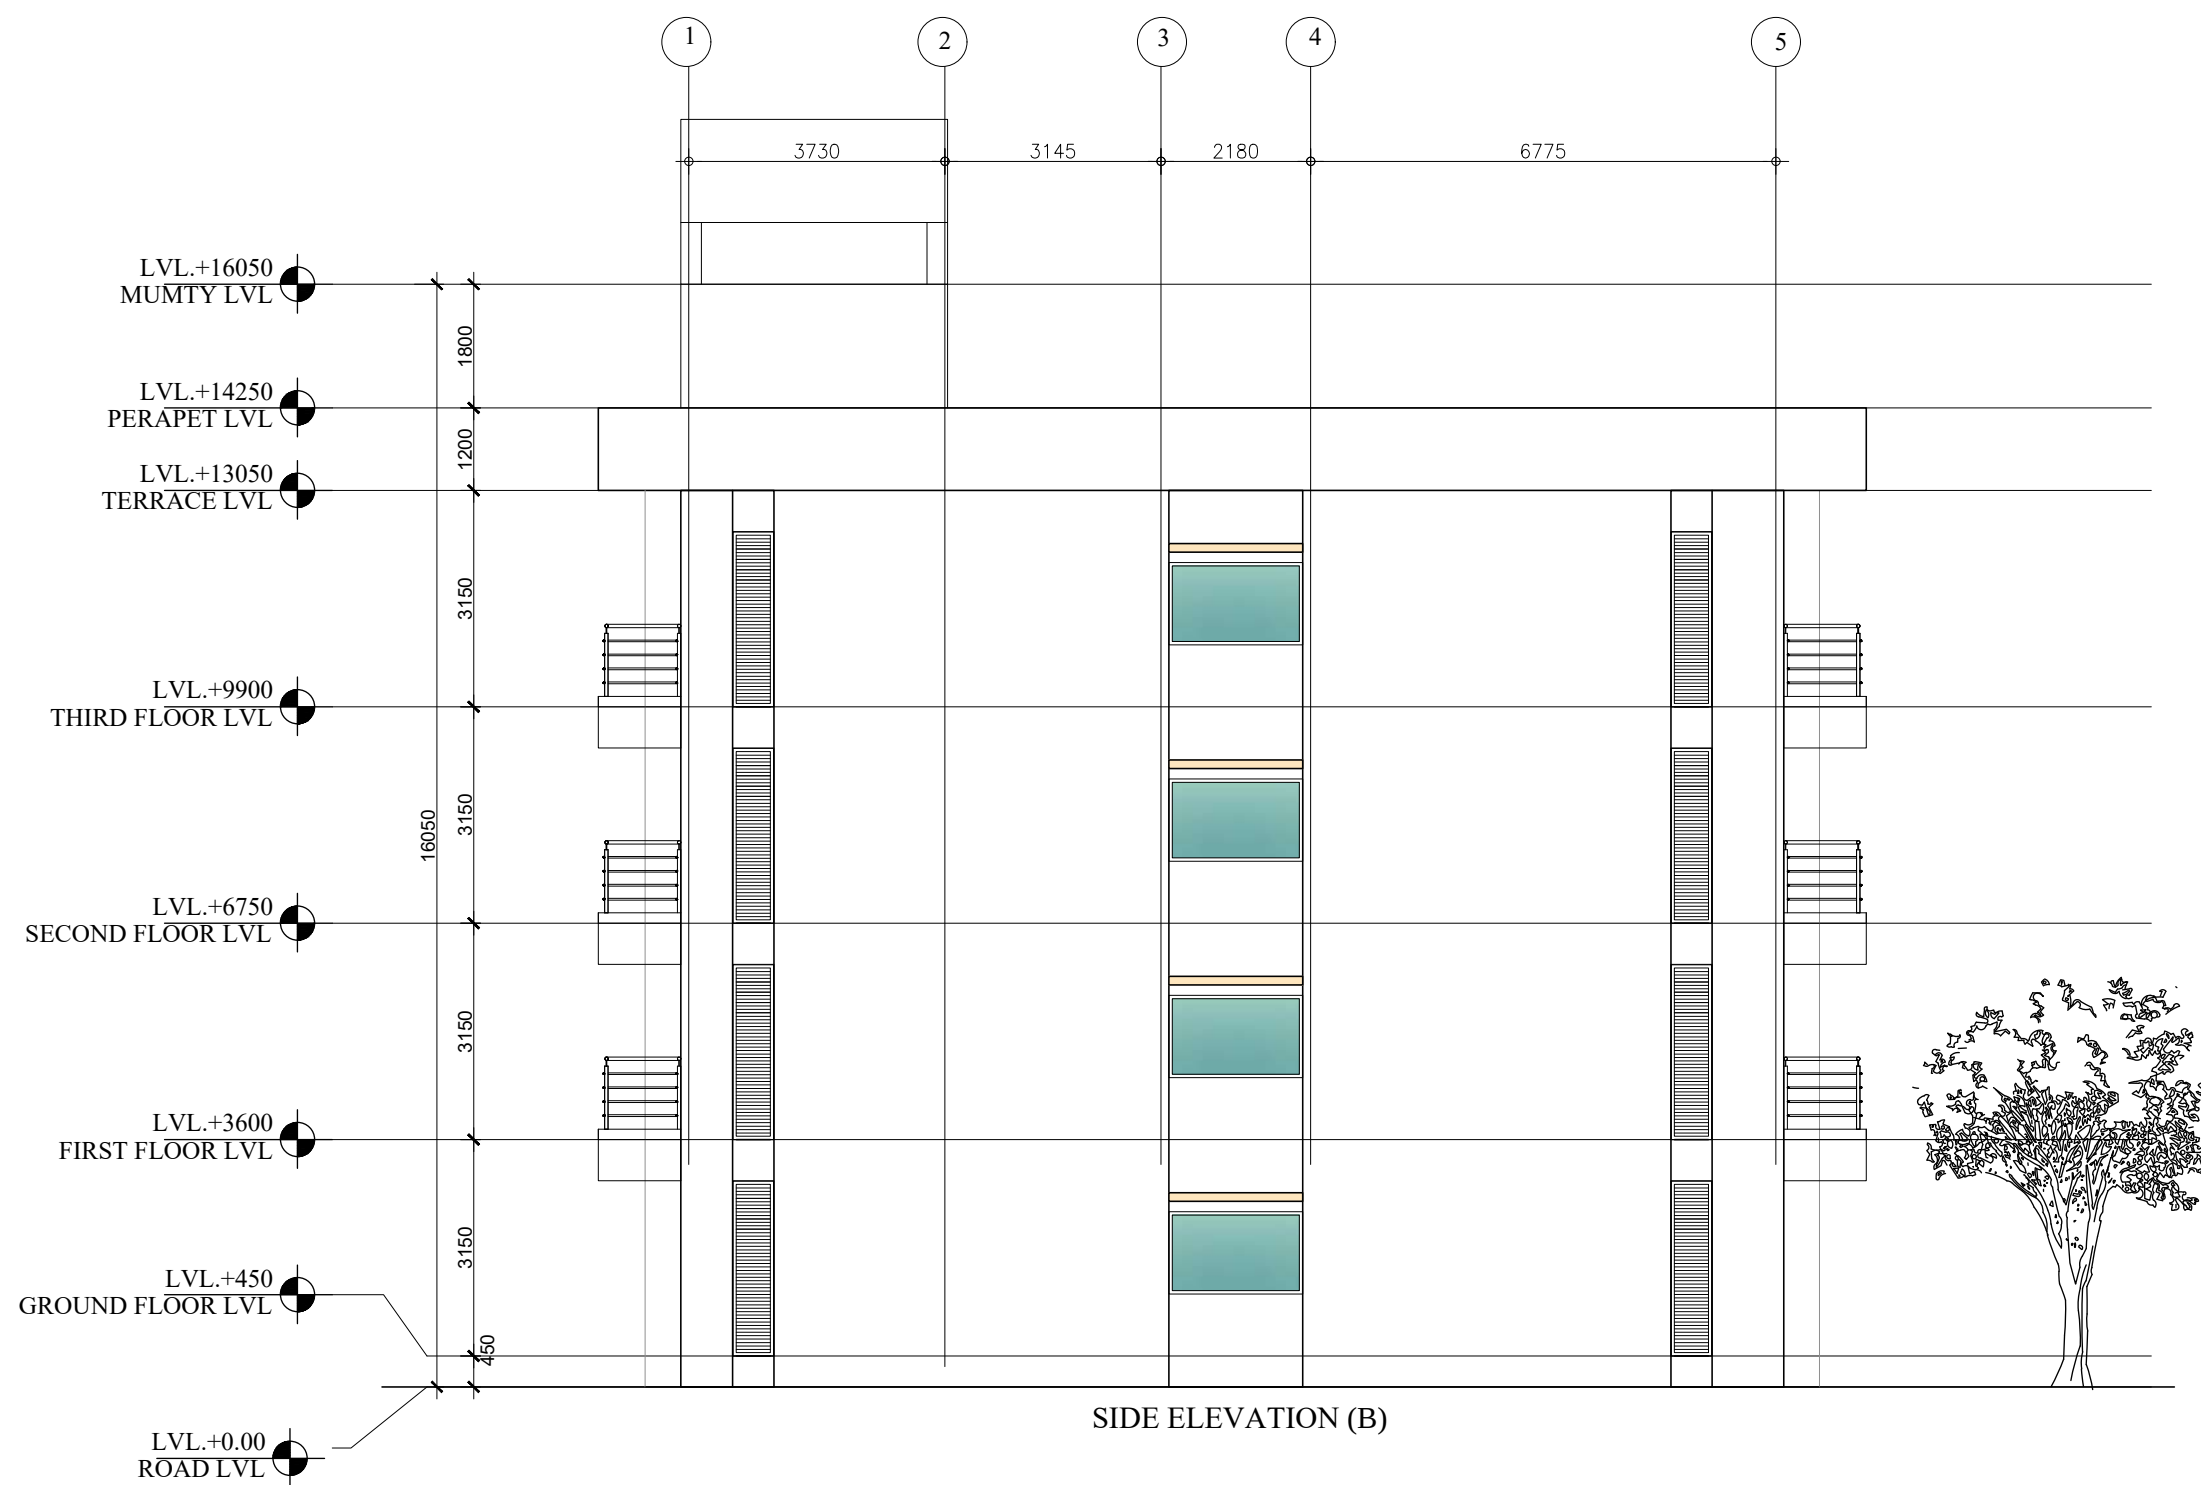

SIDE ELEVATION (B)

KEY PLAN

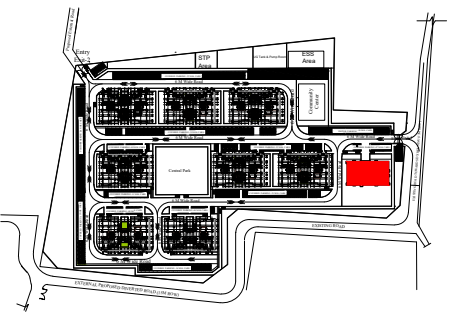


NOTES

1. ALL DIMENSIONS ARE IN MM; UNLESS NOTED OTHERWISE.
2. WRITTEN DIMENSIONS ARE TO BE FOLLOWED. DRAWINGS ARE NOT TO BE SCALED.
3. ANY DISCREPANCY IN THE DRAWING SHALL BE BROUGHT TO THE NOTICE OF THE ENGINEER.
4. THIS DRAWING SHALL BE READ IN CONJUNCTION WITH OTHER RELEVANT DRAWINGS.

Sn.No.	Description	Area (Sqm)
01	Ground Floor Area	465 sqm
02	First Floor Area	495 sqm
03	Second Floor Area	500 sqm
04	Third Floor Area	500 sqm
05	Mumty Area	30 sqm


TENDER DRAWING

CLIENT	 OIL INDIA LIMITED (A Govt. of India Enterprise)	
CONSULTANT	 IRITES THE INFRASTRUCTURE PEOPLE (A Govt. of India Enterprise)	
PROJECT	BQ WORKMEN HOUSING	
BUILDING	GUEST HOUSE (G+3)	
DRAWING TITLE	ELEVATION	
DRG. NO.	MITES/BLD/AR/TD/034	
NORTH	SCALE	DATE
	NTS	JULY 2025

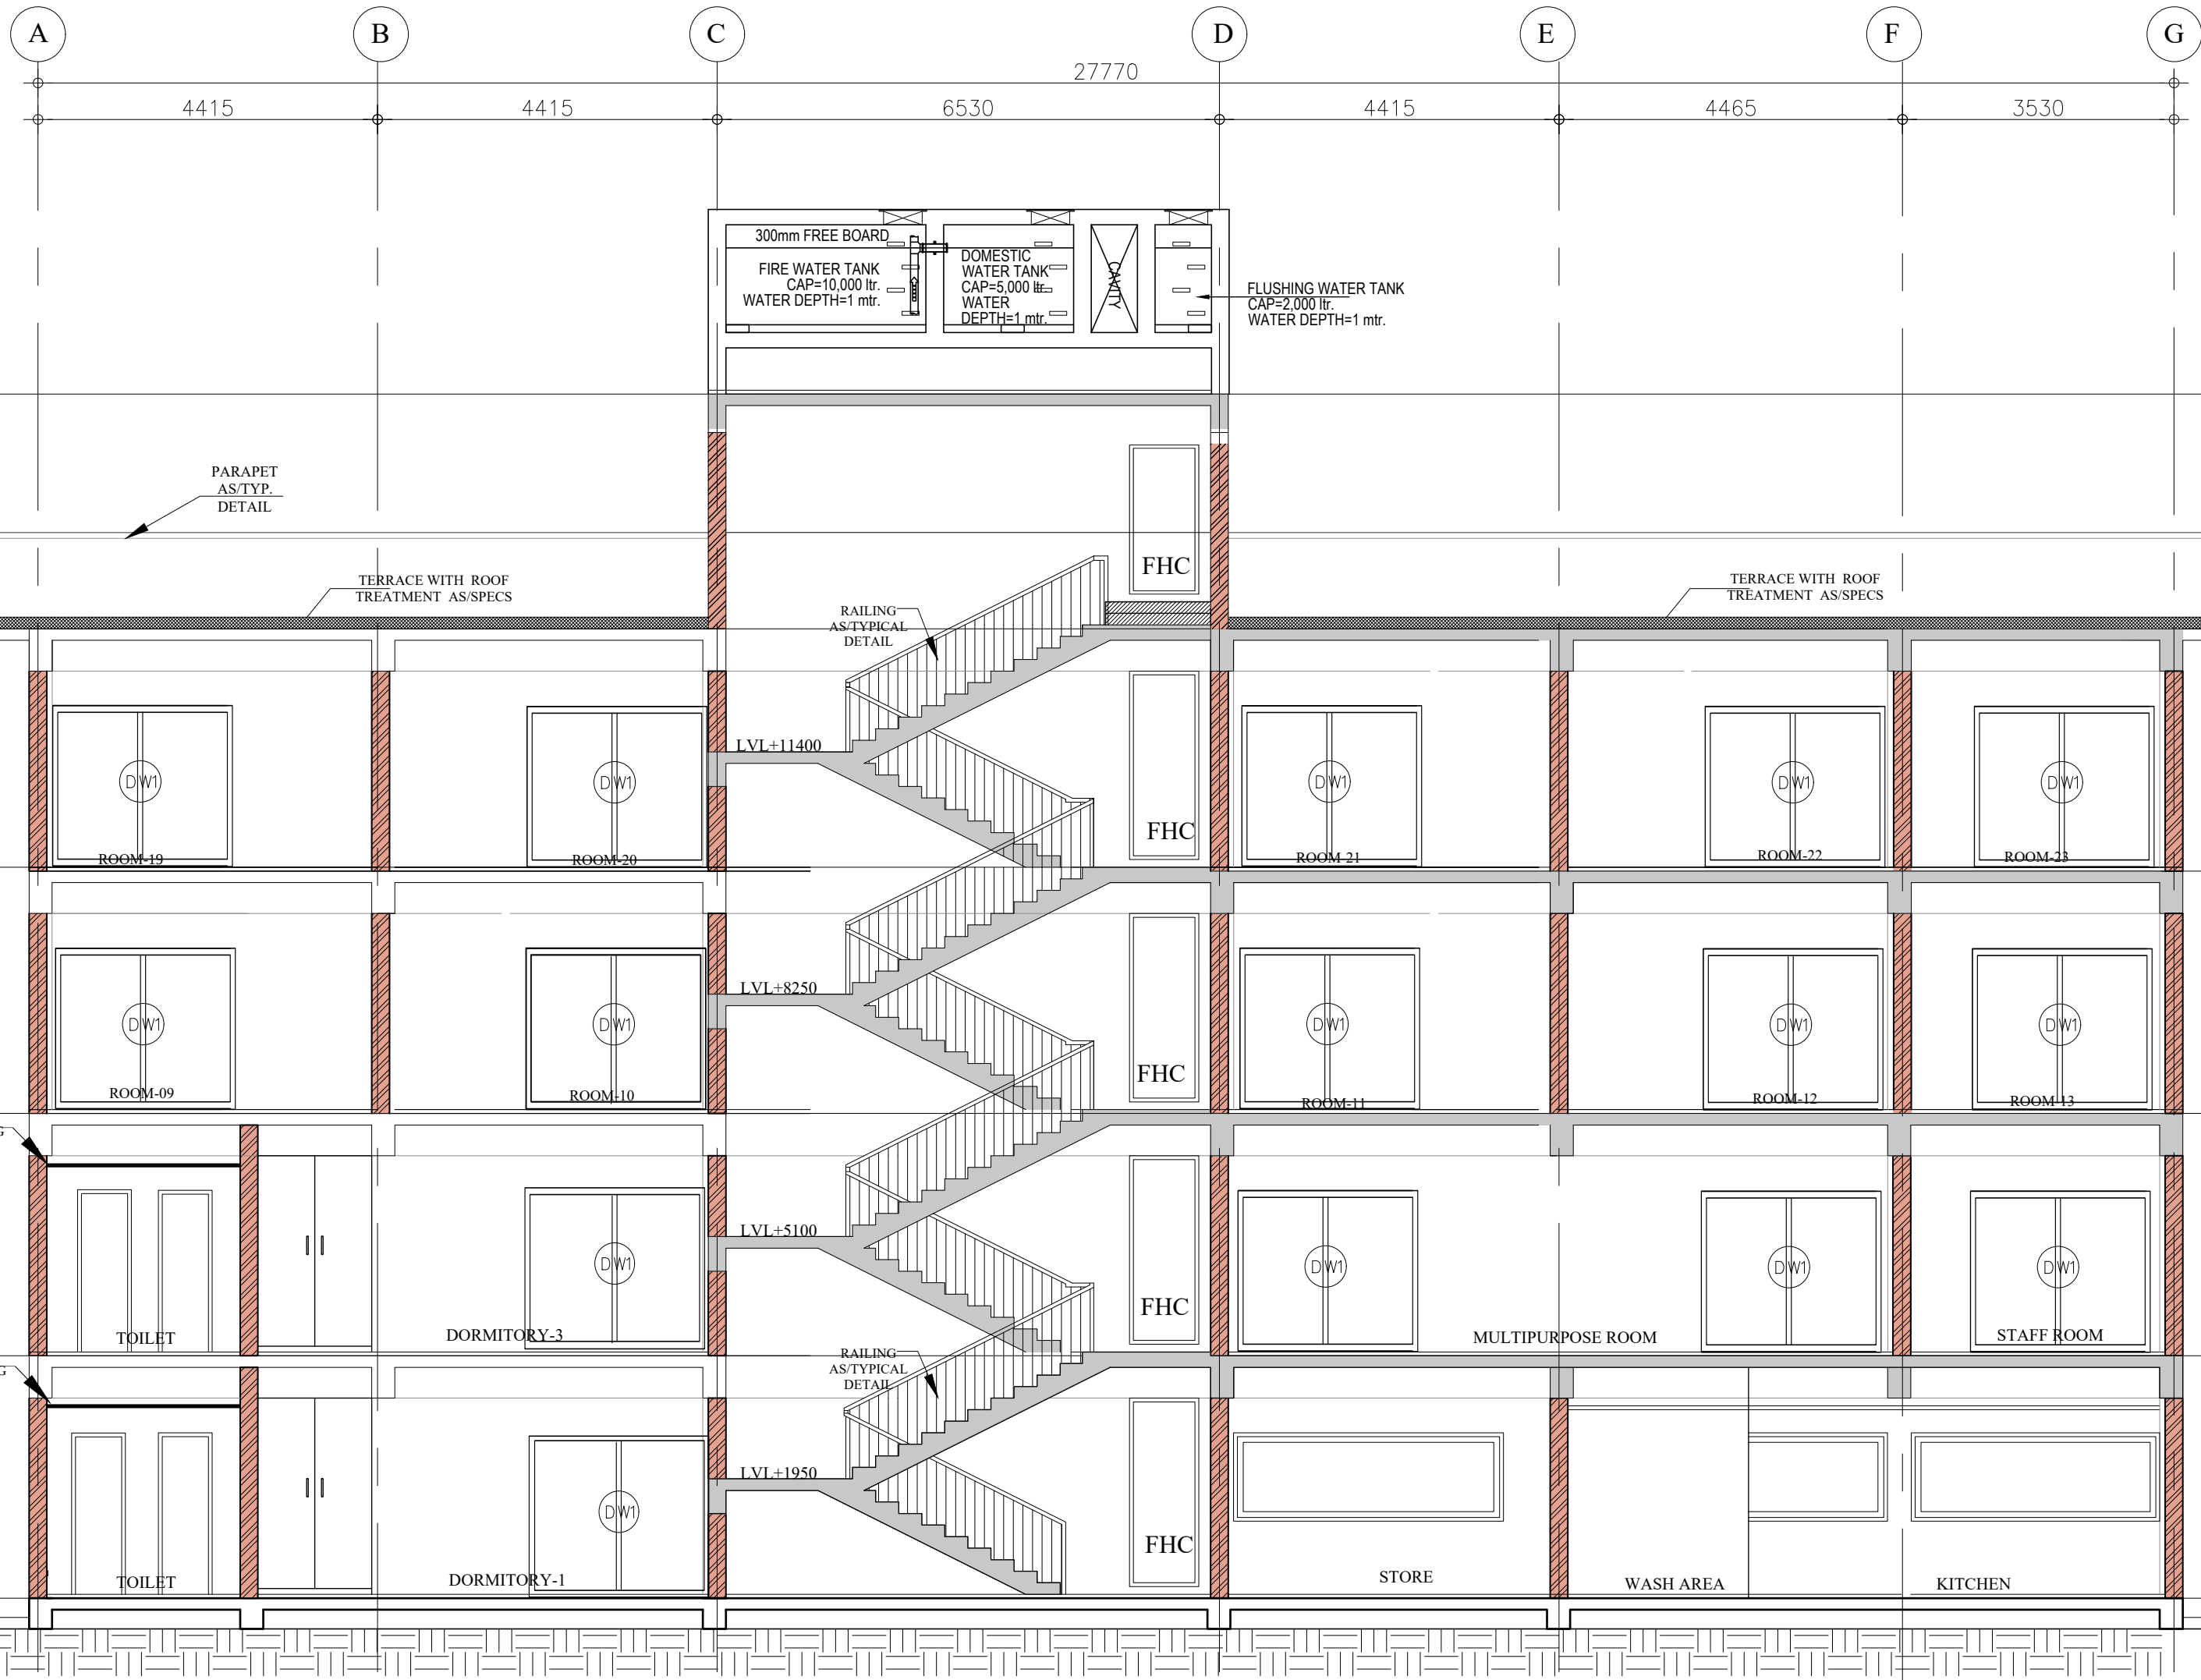

SECTION-AA

KEY PLAN

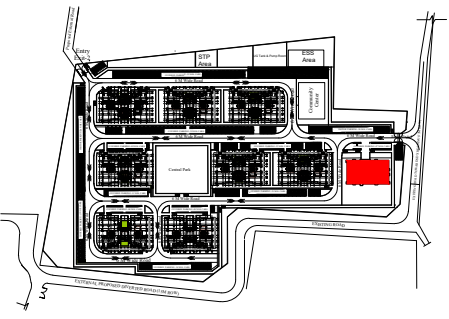


NOTES

1. ALL DIMENSIONS ARE IN MM; UNLESS NOTED OTHERWISE.
2. WRITTEN DIMENSIONS ARE TO BE FOLLOWED. DRAWINGS ARE NOT TO BE SCALED.
3. ANY DISCREPANCY IN THE DRAWING SHALL BE BROUGHT TO THE NOTICE OF THE ENGINEER.
4. THIS DRAWING SHALL BE READ IN CONJUNCTION WITH OTHER RELEVANT DRAWINGS.
5. THE FINISHED FLOOR LEVEL (FFL) SHALL BE MAINTAINED CONSIDERING RACEWAY, AS PER APPLICABLE CODES/ SPECIFICATIONS/ SITE REQUIREMENTS ABOVE THE STRUCTURAL SLAB LEVEL OF ALL BUILDINGS. REFER TENDER DOCUMENT FOR DETAILS.

TENDER DRAWING


CLIENT	 OIL INDIA LIMITED (A Govt. of India Enterprise)	
CONSULTANT	 MITES THE INFRASTRUCTURE PEOPLE (A Govt. of India Enterprise)	
PROJECT	BQ WORKMEN HOUSING	
BUILDING	GUEST HOUSE (G+3)	
DRAWING TITLE	SECTION A-A'	
DRG. NO.	MITES/BLD/AR/TD/035	
NORTH	SCALE	DATE
	NTS	JULY 2025

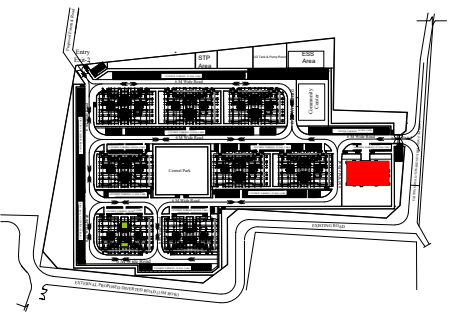

1. ALL DIMENSIONS ARE IN MM; UNLESS NOTED OTHERWISE.
2. WRITTEN DIMENSIONS ARE TO BE FOLLOWED. DRAWINGS ARE NOT TO BE SCALED.
3. ANY DISCREPANCY IN THE DRAWING SHALL BE BROUGHT TO THE NOTICE OF THE ENGINEER.
4. THIS DRAWING SHALL BE READ IN CONJUNCTION WITH OTHER RELEVANT DRAWINGS.
5. THE FINISHED FLOOR LEVEL (FFL) SHALL BE MAINTAINED CONSIDERING RACEWAY, AS PER APPLICABLE CODES/ SPECIFICATIONS/ SITE REQUIREMENTS ABOVE THE STRUCTURAL SLAB LEVEL OF ALL BUILDINGS.
REFER TENDER DOCUMENT FOR DETAILS.
6. RAILING SHOULD COMPLY WITH NBC NORMS.


NORTH 	SCALE NTS	DATE JULY 2025
--	------------------	-----------------------

DOOR-D

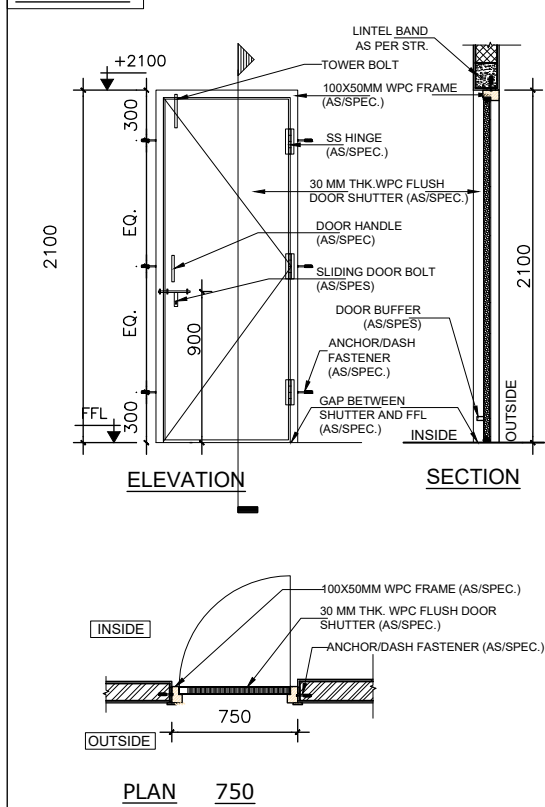


TYPE : WPC FRAME AND WPC FLUSH SHUTTER
SIZE : 750MMX2100MM

DOOR-D1

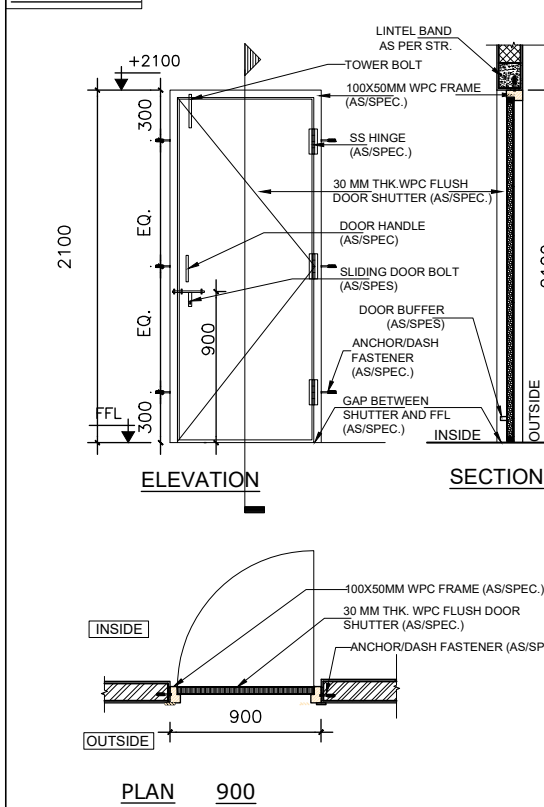


TYPE : WPC FRAME AND WPC FLUSH SHUTTER
SIZE : 900MMX2100MM

DOOR-D2

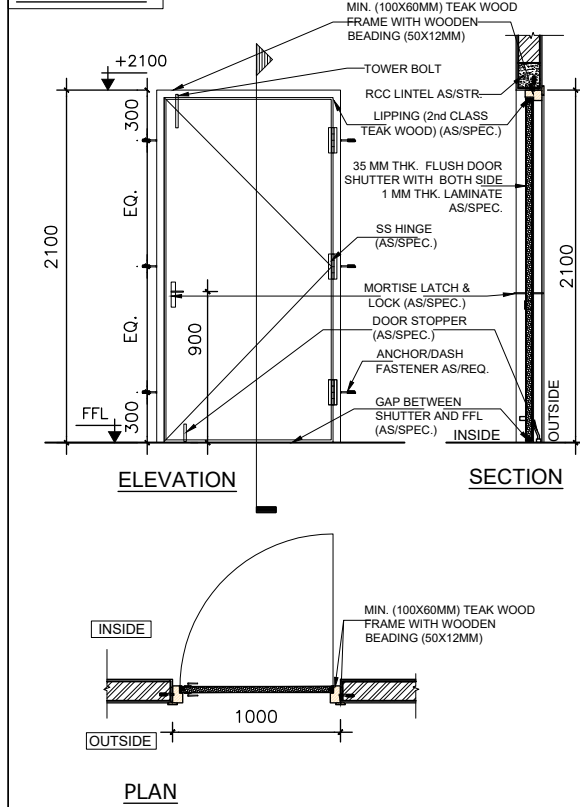


TYPE : SINGLE LEAF TEAK WOOD FRAME, FLUSH DOOR
SIZE : 1000MMX2100MM

DOOR-D3

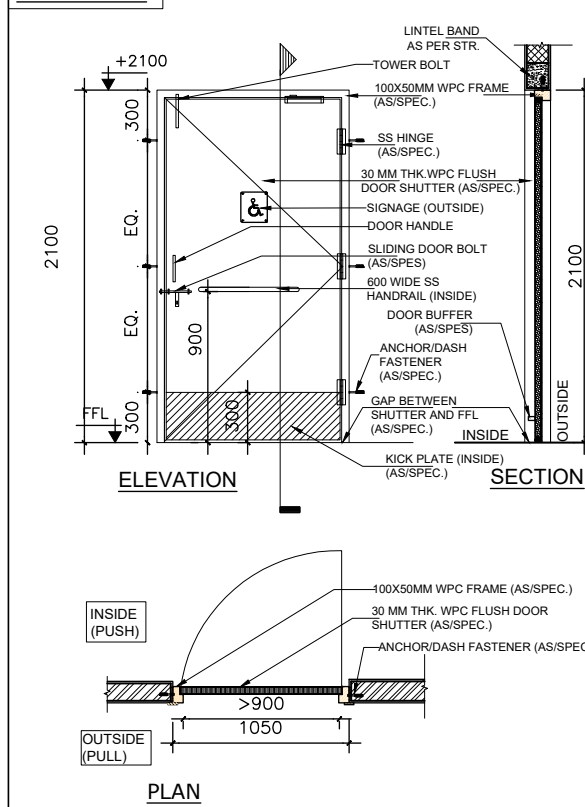


TYPE : WPC FRAME AND WPC FLUSH SHUTTER
SIZE : 1050MMX2100MM

DOOR-D4

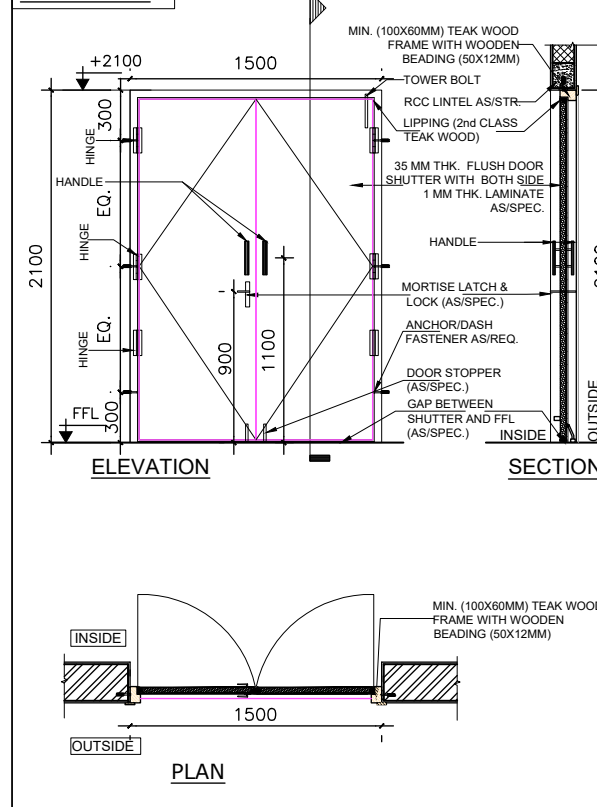


TYPE : TEAK WOOD FRAME DOUBLE LEAF FLUSH DOOR
SIZE : 1500MMX2100MM

DOOR-GDW

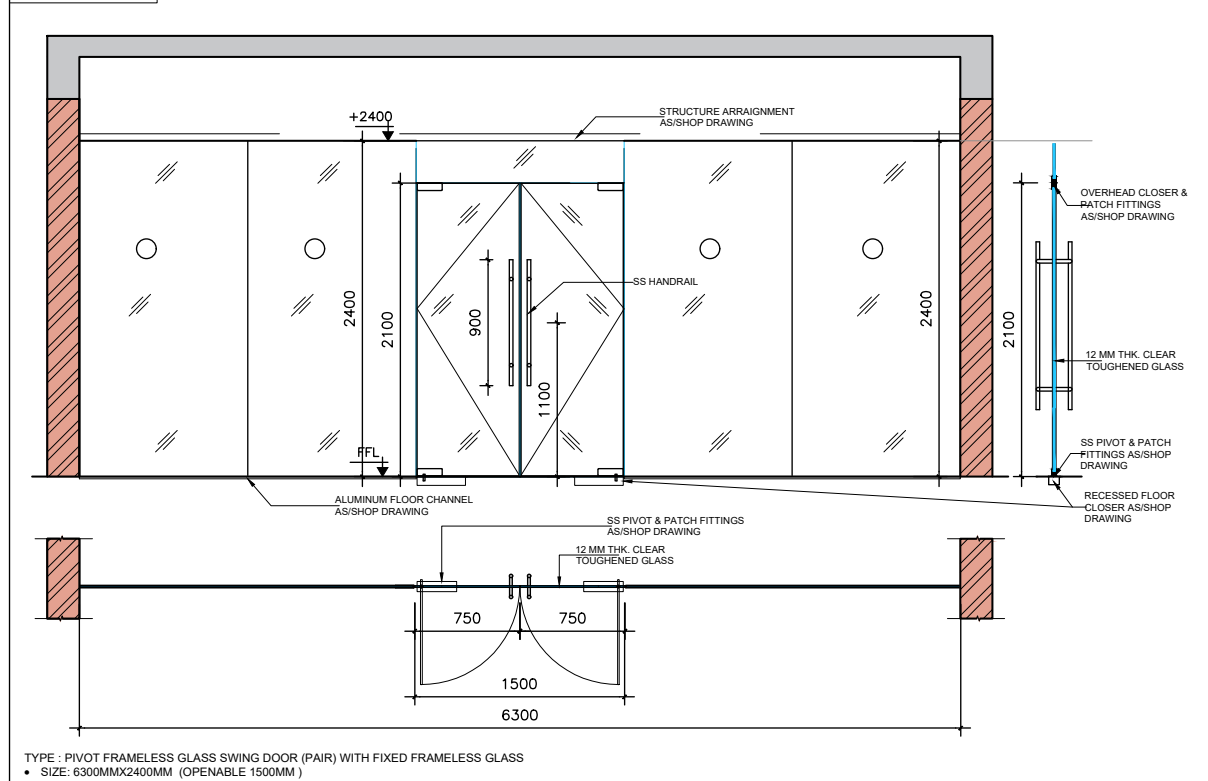


TYPE : PIVOT FRAMELESS GLASS SWING DOOR (PAIR) WITH FIXED FRAMELESS GLASS
• SIZE : 6300MMX2400MM (OPENABLE 1500MM)

DOOR-GDW1

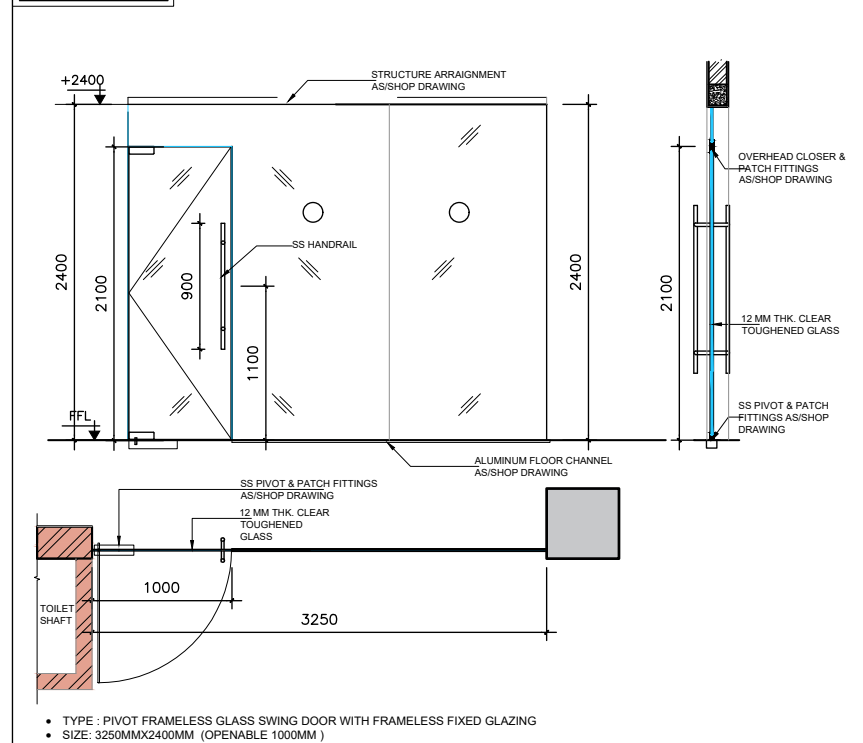


• TYPE : PIVOT FRAMELESS GLASS SWING DOOR WITH FRAMELESS FIXED GLAZING
• SIZE : 3250MMX2400MM (OPENABLE 1000MM)

DOOR-DW1

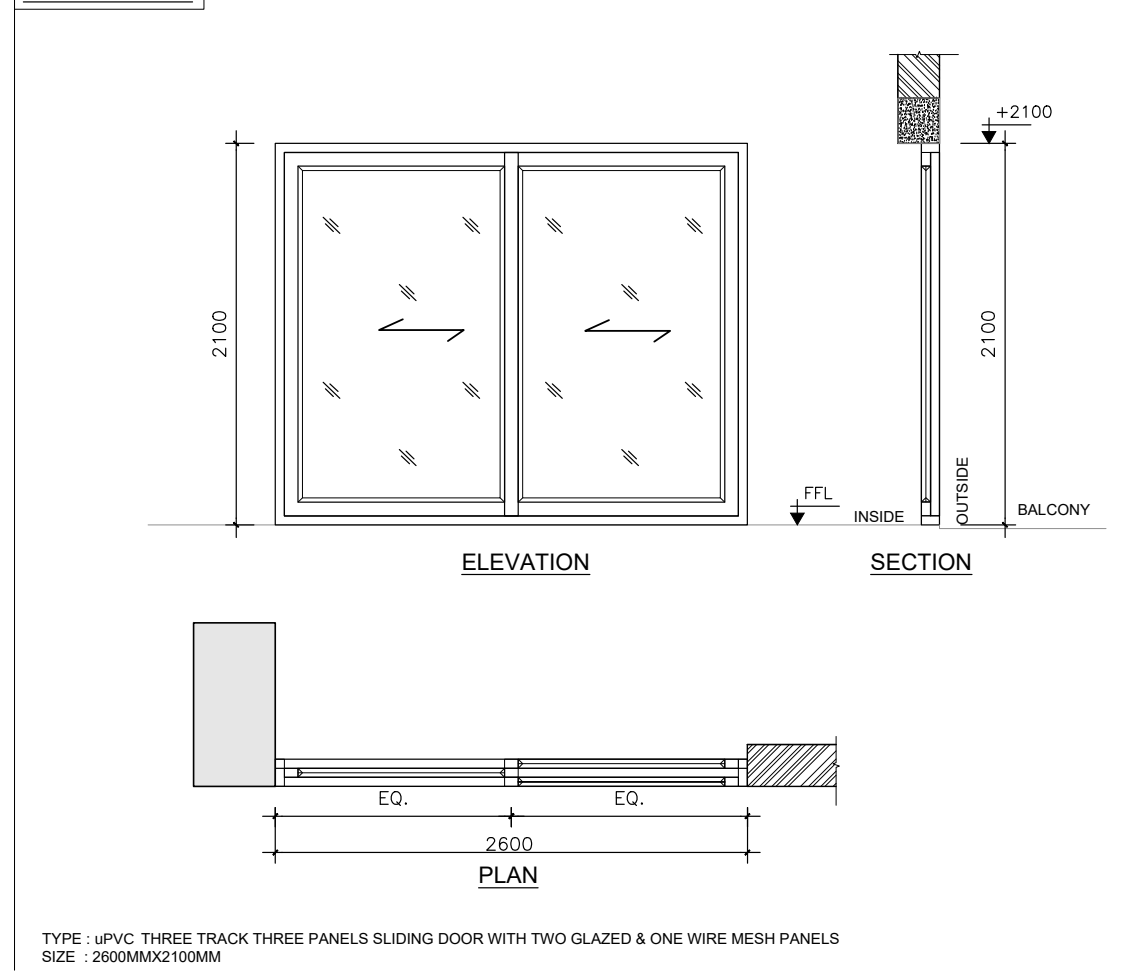


TYPE : uPVC THREE TRACK THREE PANELS SLIDING DOOR WITH TWO GLAZED & ONE WIRE MESH PANELS
SIZE : 2600MMX2100MM

DOOR-FD

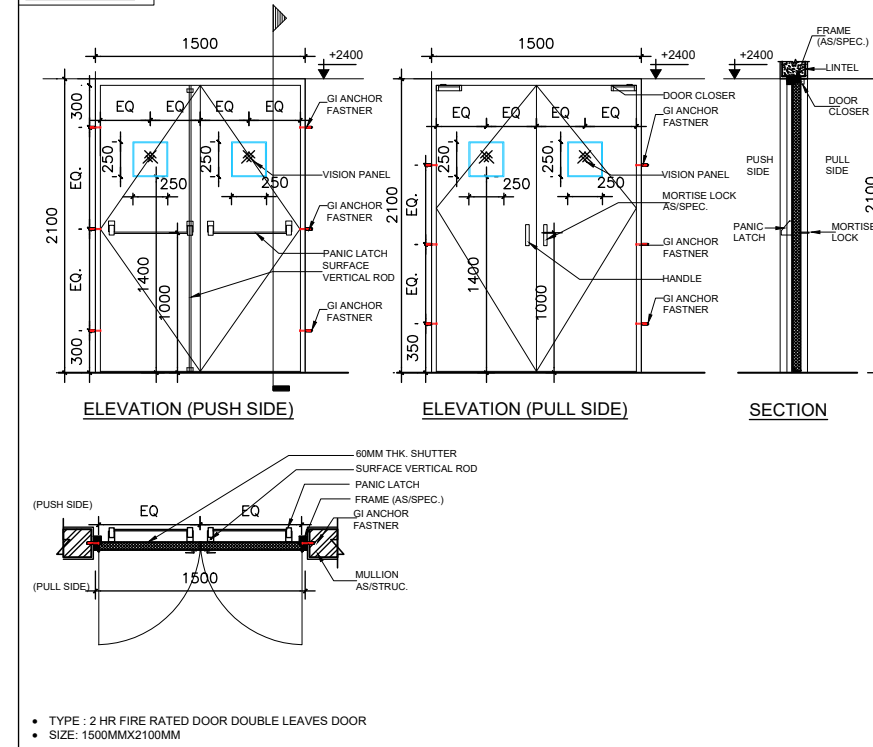

• TYPE : 2 HR FIRE RATED DOOR DOUBLE LEAVES DOOR
• SIZE : 1500MMX2100MM

KEY PLAN

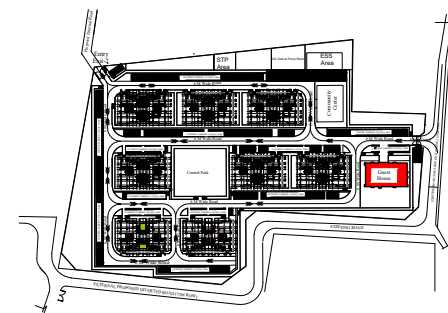

NOTES

1. ALL DIMENSIONS ARE IN MM. UNLESS NOTED OTHERWISE.
2. WRITTEN DIMENSIONS ARE TO BE FOLLOWED. DRAWINGS ARE NOT TO BE SCALED.
3. ANY DISCREPANCY IN THE DRAWING SHALL BE BROUGHT TO THE NOTICE OF THE ENGINEER.
4. THIS DRAWING SHALL BE READ IN CONJUNCTION WITH OTHER RELEVANT DRAWINGS.
5. THE DRAWING IS INDICATIVE ONLY.
6. SHOP DRAWING TO BE PREPARED FOR APPROVAL.
7. REFER SPECIFICATION AND SCHEDULE OF FINISH.

TENDER DRAWING

CLIENT



CONSULTANT



PROJECT

BQ WORKMEN HOUSING

BUILDING

GUEST HOUSE (G+3)

DRAWING TITLE

DOOR WINDOW-1

DRG. NO.

RITES/BLD/AR/TD/037

NORTH



SCALE

NTS


DATE

JULY 2025

SCHEDULE OF DOORS - (Ground floor to Terrace floor)


SL. NO	TYPE	NOS.	WIDTH	HEIGHT (from FFL.)	CILL (from FFL.)	LINTEL (from FFL.)	LOCATION	REMARKS
SCHEDULE OF DOORS								
1.	D	---	750	2100	00	2100	WC AND BATH	WPC DOOR PANEL WITH FRAME AS/DRAWING
2.	D1	---	900	2100	00	2100	TOILETS	WPC DOOR PANEL WITH FRAME AS/DRAWING
3.	D2	---	1000	2100	00	2100	ROOMS	SINGLE LEAF TEAK WOOD FRAME, FLUSH DOOR AS/DRAWING
4.	D3	---	1050	2100	00	2100	PWD TOILET	WPC DOOR PANEL WITH FRAME AS/DRAWING
5.	D4	---	1500	2100	00	2100	SERVICE ENTRY	DOUBLE LEAF TEAK WOOD FRAME, FLUSH DOOR AS/DRAWING
6.	DW1	---	2600	2100	00	2100	ROOM BALCONY	THREE TRACK THREE PANELS SLIDING DOOR WITH TWO GLAZED & ONE WIRE MESH PANELS
7.	GDW	---	6300	2400	00	2400	ENTRY	PIVOT FRAMELESS GLASS SWING DOOR (PAIR) WITH FRAMELESS FIXED GLASS AS/DRAWING
8.	GDW1	---	3230	2400	00	2400	BALCONY, DINING ENTRY	PIVOT FRAMELESS GLASS SWING DOOR (PAIR) WITH FRAMELESS FIXED GLASS AS/DRAWING
9.	FD	---	1500	2100	00	2100	STAIRCASE	2HR FIRE RATED METAL FIRE DOOR
10.	SD	---	900	2100	100	2100	FHC SHAFT	M.S.SINGLE LEAF DOOR WITH GLASS (FHC Shaft Door as per NBC & latest CPWD Guideline)
11.	SD1	---	900	2100	100	2100	ELE. SHAFT	M.S.SINGLE LEAF DOOR WITH VENTILATION AT TOP (Electrical Shaft Door as per NBC & latest CPWD Guideline)
12.	SD2	---	600	2100	100	2100	LV. SHAFT	M.S.SINGLE LEAF DOOR WITH VENTILATION AT TOP

TYPICAL WINDOW -W1

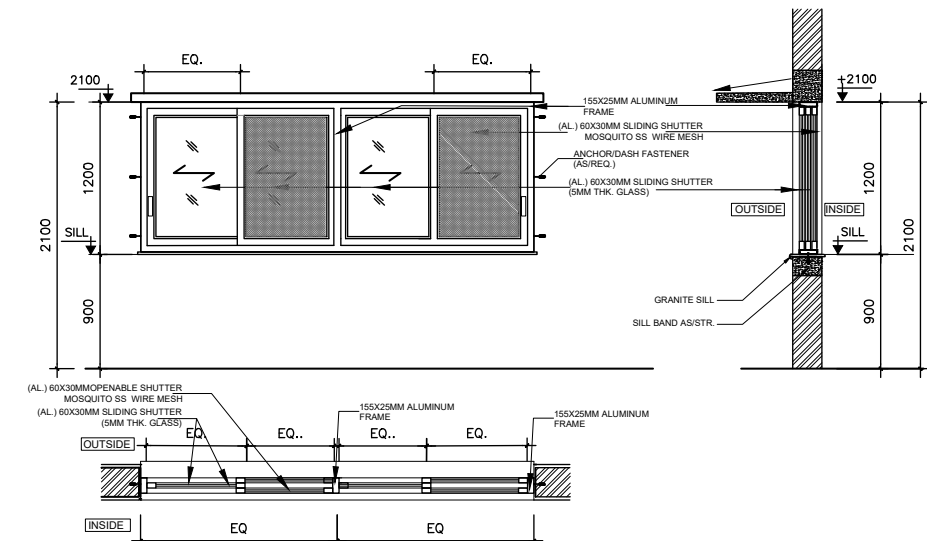


- TYPE : ALUMINUM FRAMED SLIDING WINDOW – THREE TRACK SYSTEM WITH WIRE MESH AS/DRAWING
- SIZE : 3100 X 1200 MM

TYPICAL WINDOW -W2

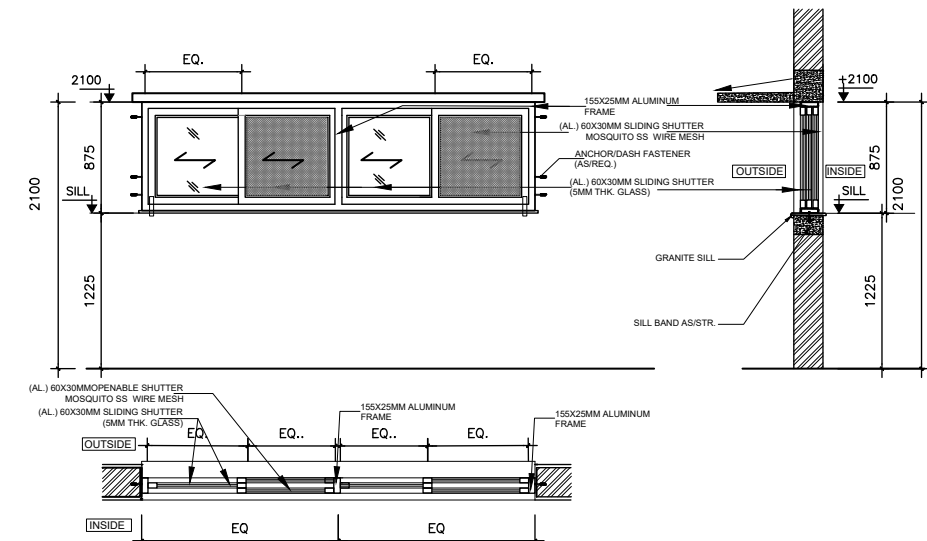


- TYPE : ALUMINUM FRAMED SLIDING WINDOW – THREE TRACK SYSTEM WITH WIRE MESH AS/DRAWING
- SIZE : 3100 X 875 MM

TYPICAL MS GRILL ALL AROUND WINDOW OPENING

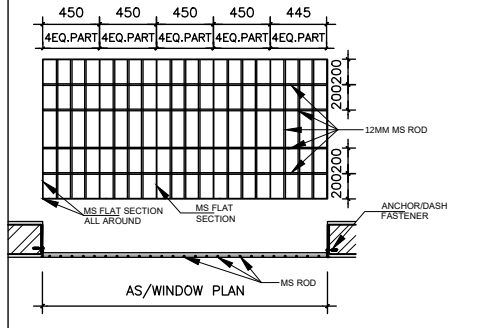


JL-TYPICAL ALUMINUM FRAME- OPENABLE LOUVERED PANEL

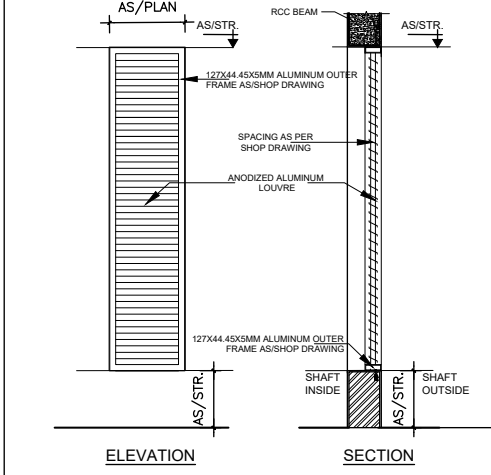


- TYPE : ALUMINUM FRAME- OPENABLE LOUVERED PANEL
- SIZE : 600 X 2550 MM

DOOR-SD2

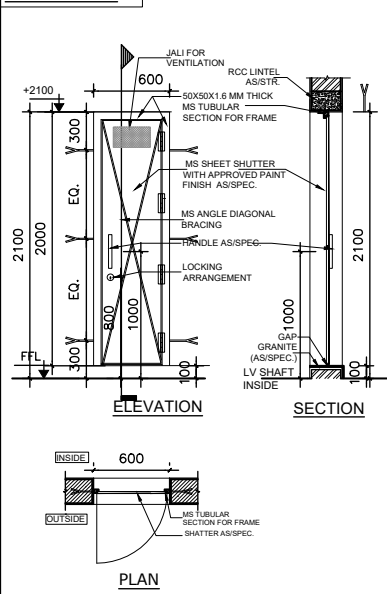


- TYPE : M.S. PAINTED SINGLE LEAF DOOR
- SIZE : 600MMX2100MM

TYPICAL WINDOW -W3

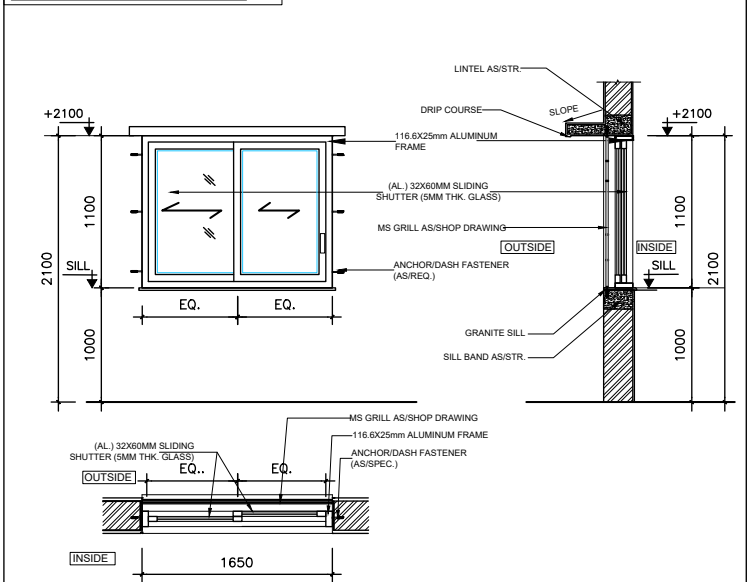


- TYPE : ALUMINUM 2 TRACK SLIDING WINDOW
- SIZE : 1650 X 1100 MM

TYPICAL WINDOW -W4

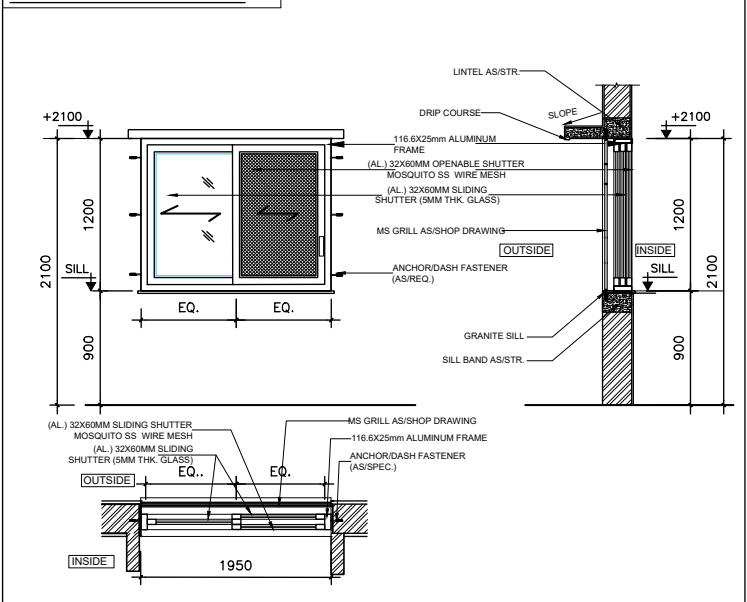


- TYPE : ALUMINUM 3 TRACK SLIDING WINDOW WITH SS WIRE MESH PANEL
- SIZE : 1950 X 1200 MM

TYPICAL TOILET VENTILATOR -V

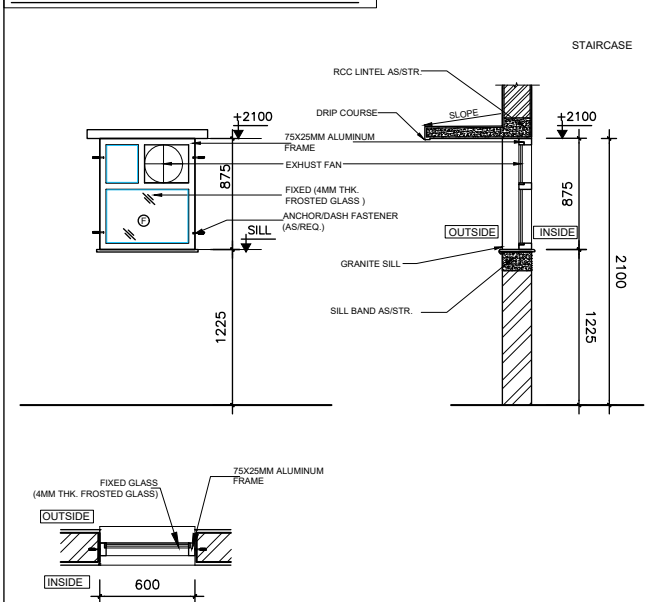


- TYPE : ALUMINUM FRAME FIXED PANELS FROSTED GLASS WITH EXHUST FAN
- SIZE : 600X875MM

TYPICAL TOILET VENTILATOR -V1

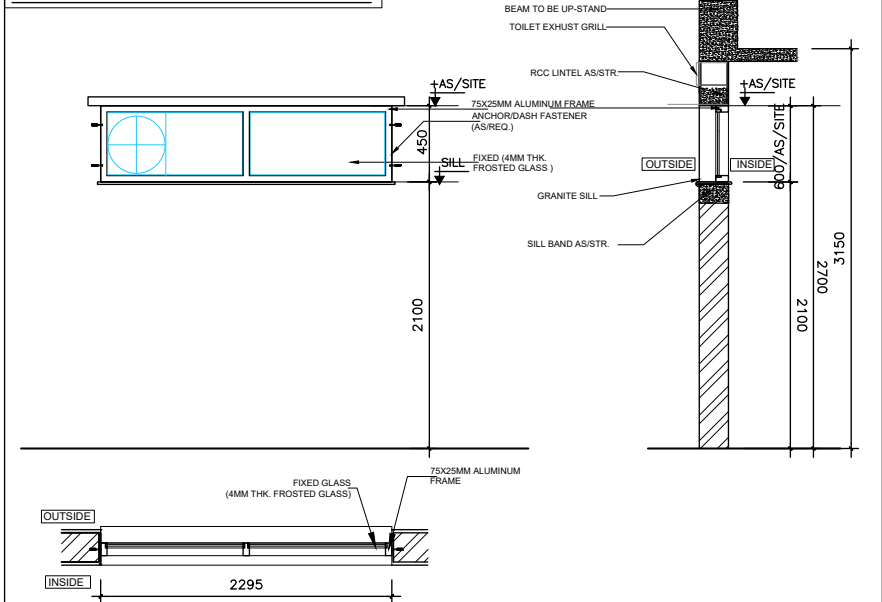


- TYPE : ALUMINUM FRAME FIXED PANELS FROSTED GLASS WITH EXHUST FAN
- SIZE : 2295X450 MM

TYPICAL TOILET VENTILATOR -V2

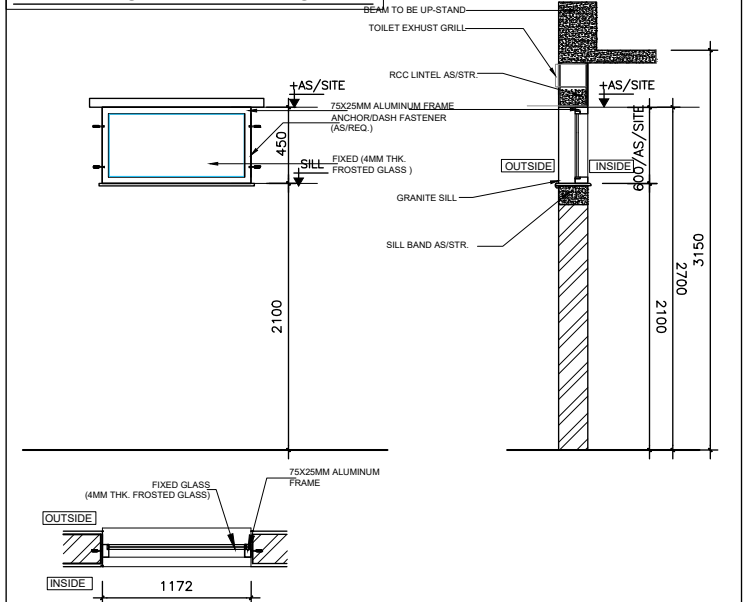

- TYPE : ALUMINUM FRAME FIXED PANELS FROSTED GLASS WITH EXHUST FAN
- SIZE : 1172X450 MM

KEY PLAN

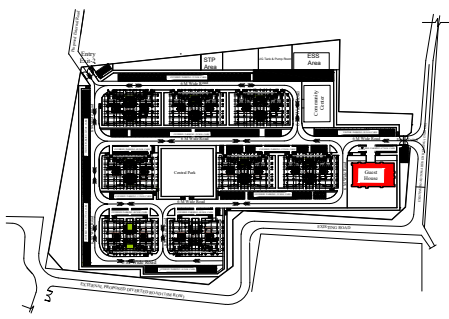

NOTES

1. ALL DIMENSIONS ARE IN MM. UNLESS NOTED OTHERWISE.
2. WRITTEN DIMENSIONS ARE TO BE FOLLOWED. DRAWINGS ARE NOT TO BE SCALED.
3. ANY DISCREPANCY IN THE DRAWING SHALL BE BROUGHT TO THE NOTICE OF THE ENGINEER.
4. THIS DRAWING SHALL BE READ IN CONJUNCTION WITH OTHER RELEVANT DRAWINGS.
5. THE DRAWING IS INDICATIVE ONLY.
6. SHOP DRAWING TO BE PREPARED FOR APPROVAL.
7. REFER SPECIFICATION AND SCHEDULE OF FINISH.

TENDER DRAWING

CLIENT
OIL INDIA LIMITED
(A Govt. of India Enterprise)

CONSULTANT
IRITES
THE INFRASTRUCTURE PEOPLE
(A Govt. of India Enterprise)

PROJECT
BQ WORKMEN HOUSING

BUILDING
GUEST HOUSE (G+3)

DRAWING TITLE
DOOR WINDOW-2

DRG. NO.
BITES/BLD/AR/TD/038

NORTH

SCALE
NTS
DATE
JULY 2025

SCHEDULE OF WINDOWS - (Ground floor to Terrace floor)


SL. NO	TYPE	NOS.	WIDTH	HEIGHT	SILL (from FFL)	LINTEL (from FFL)	REMARKS
1.	W1	---	3100	1200	900	2100	POWDER COATED ALUMINUM FRAMED SLIDING WINDOW – THREE TRACK SYSTEM WITH WIRE MESH AS/DRAWING
2.	W2	---	3100	875	1225	2100	POWDER COATED ALUMINUM FRAMED SLIDING WINDOW – THREE TRACK SYSTEM WITH WIRE MESH AS/DRAWING
3.	W3	---	1650	1100	1000	2100	POWDER COATED ALUMINUM FRAMED SLIDING WINDOW – TWO TRACK SYSTEM AS/DRAWING/SPECS
4.	W4	---	1950	1200	900	2100	POWDER COATED ALUMINUM FRAMED SLIDING WINDOW – THREE TRACK SYSTEM AS/DRAWING/SPECS

SCHEDULE OF VENTILATORS - (Ground floor to Terrace floor)


SL. NO	TYPE	NOS.	WIDTH	HEIGHT	SILL (from FFL)	LINTEL (from FFL)	REMARKS
1.	V	---	600	875	1225	2100	POWDER-COATED ALUMINUM FRAME VENTILATOR WITH FIXED FRO.GLASS PANELS AND INTEGRATED EXHAUST FAN
2.	V1	---	2295	450	2100	AS/SITE	POWDER-COATED ALUMINUM FRAME VENTILATOR WITH FIXED FROSTED GLASS PANELS AS/SPECS
2.	V2	---	900	450	2100	AS/SITE	POWDER-COATED ALUMINUM FRAME VENTILATOR WITH FIXED FROSTED GLASS PANELS AS/SPECS

SCHEDULE OF SHAFT JALI - (Ground floor to Terrace floor)


SL. NO	TYPE	NOS.	WIDTH	HEIGHT	SILL (from FFL)	LINTEL (from FFL)	REMARKS
1.	JL	---	600	2550	+00	BEAM BOTTOM/AS PER STR.	ALUMINUM OPENABLE LOUVERED PANEL

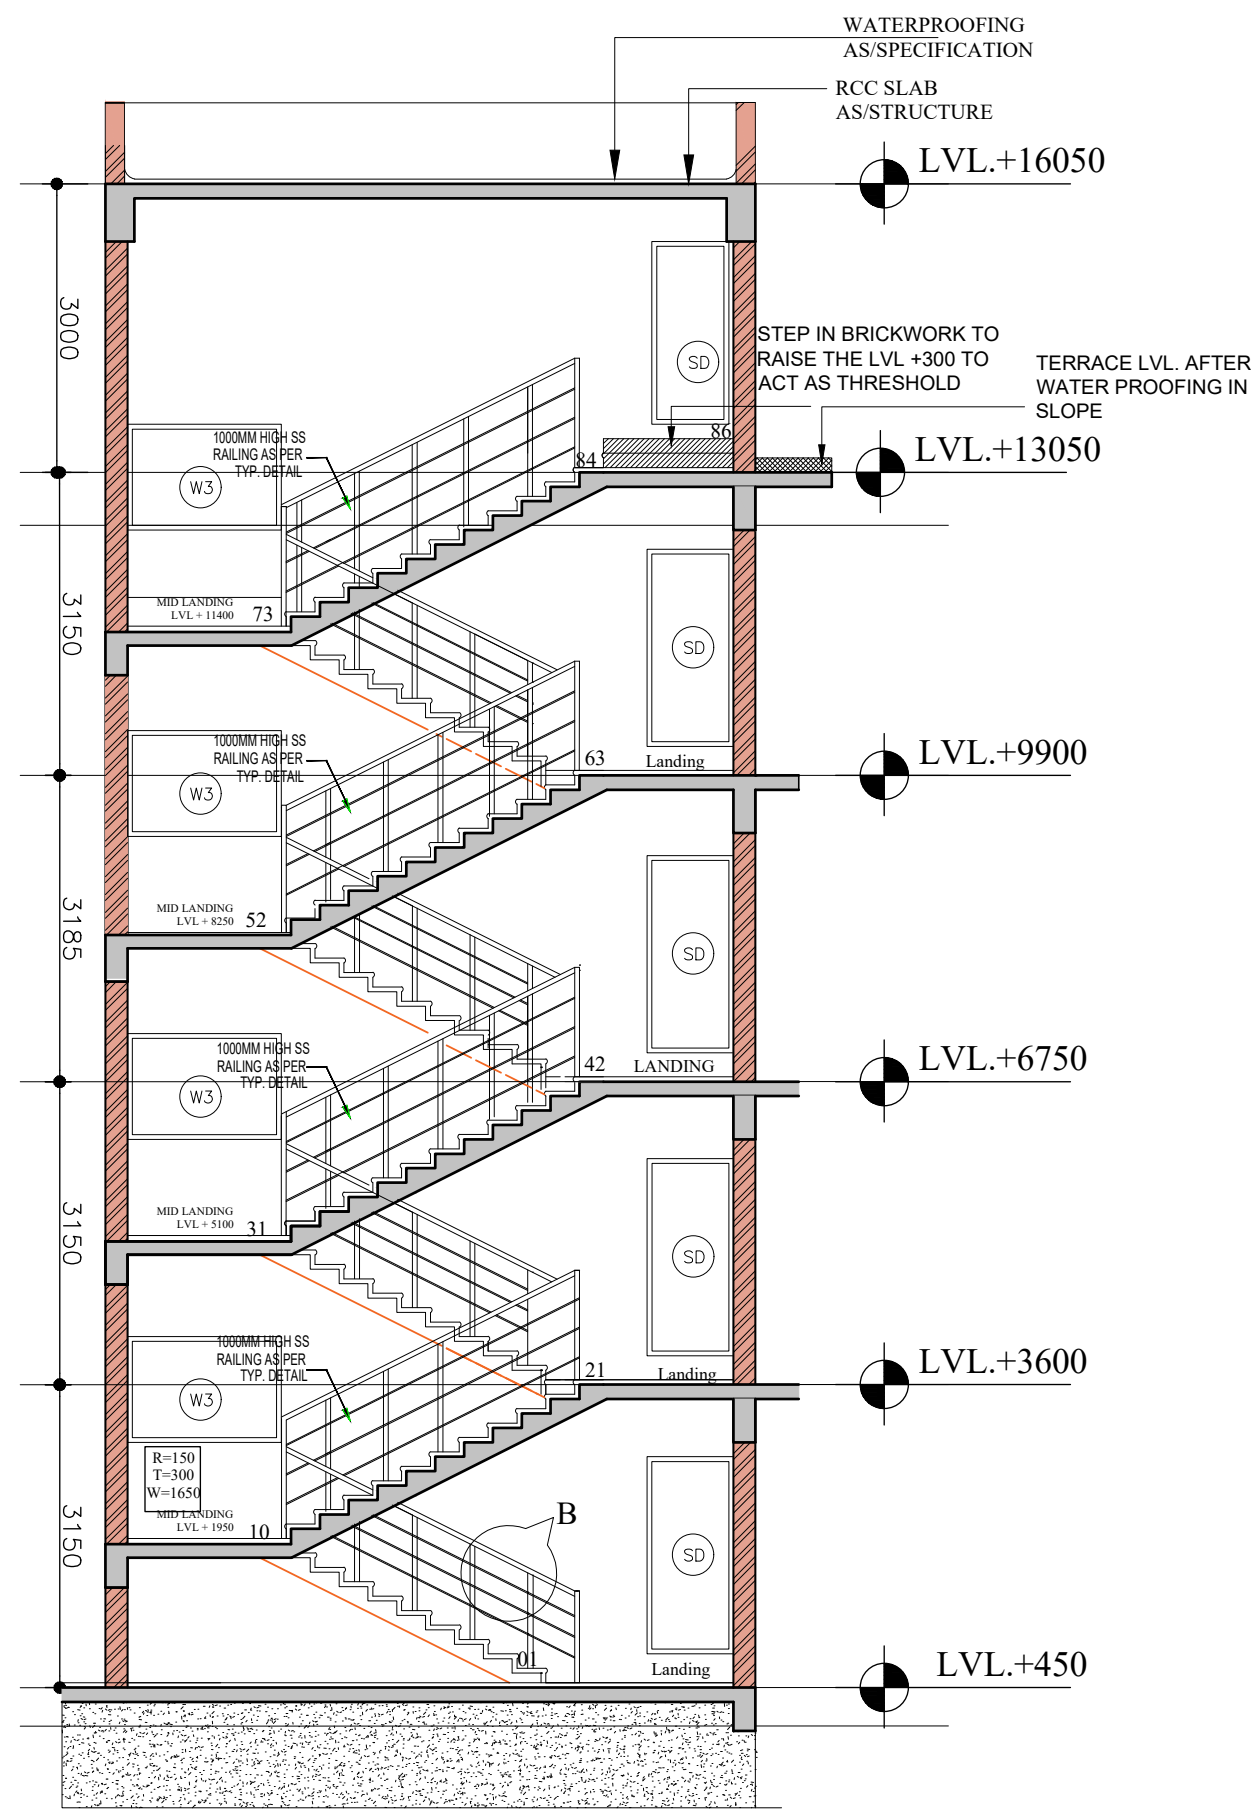


SECTION YY

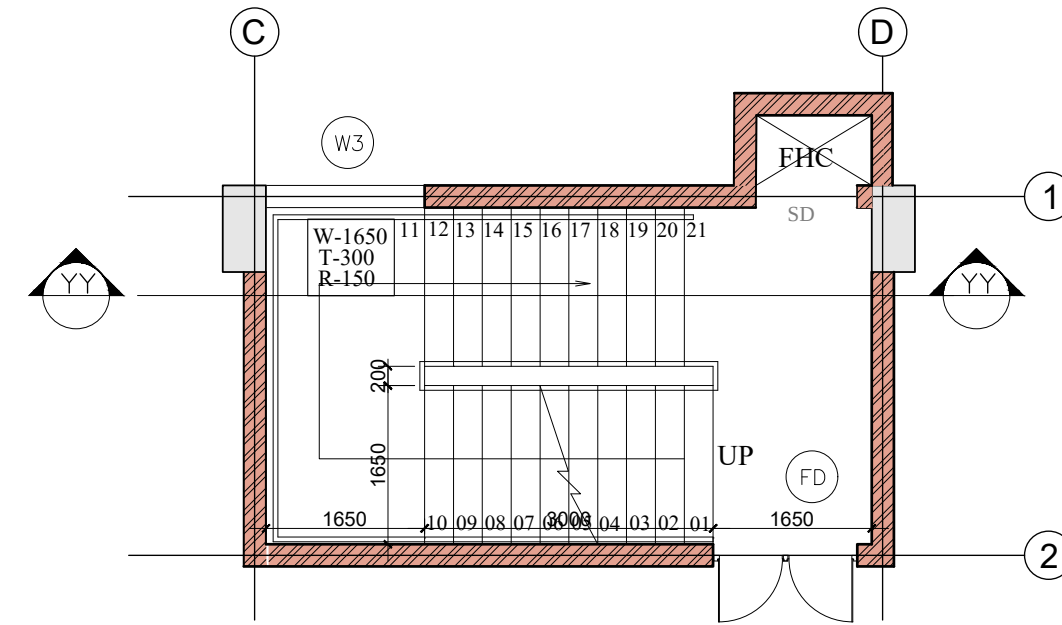


TYPICAL STAIRCASE PLAN AT GROUND FLOOR

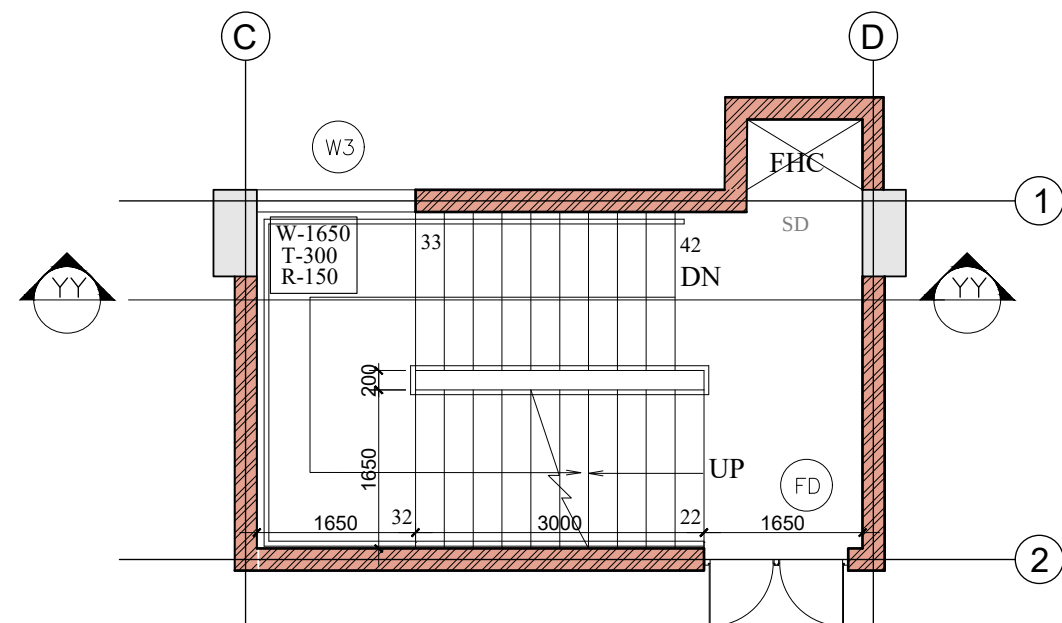


TYPICAL STAIRCASE PLAN AT FIRST FLOOR

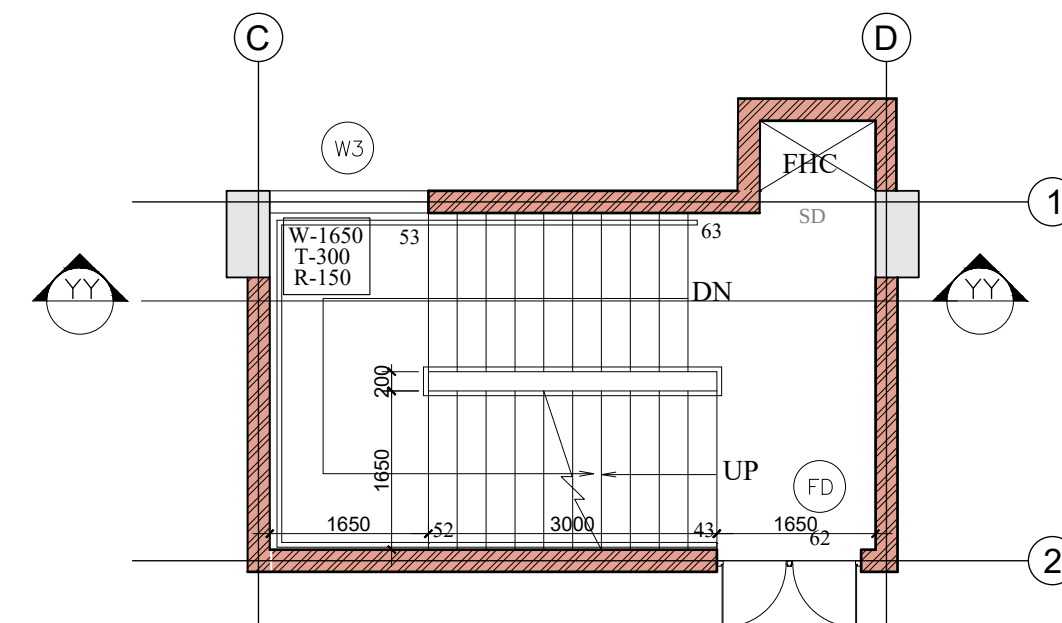


TYPICAL STAIRCASE PLAN AT SECOND FLOOR

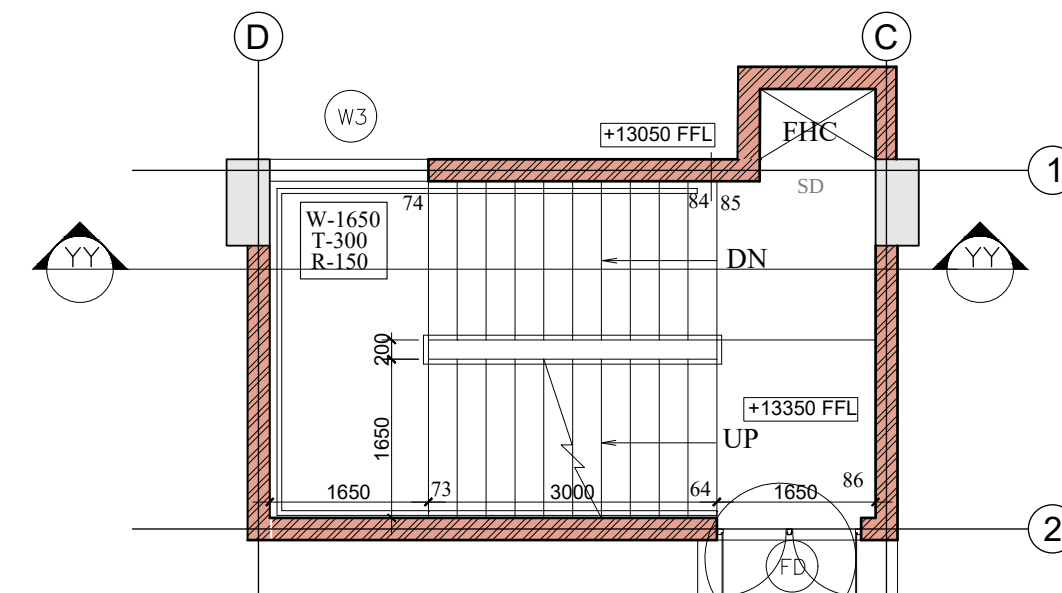


TYPICAL STAIRCASE PLAN AT THIRD FLOOR

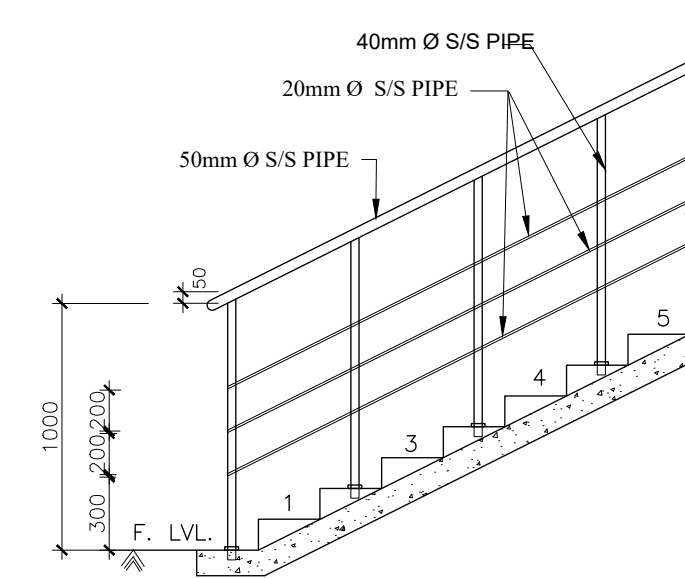


STAIRCASE RAILING DETAIL
DETAIL B

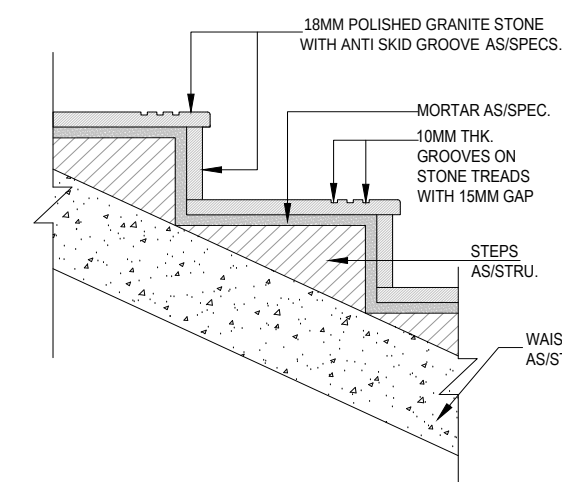

STEPS DETAIL

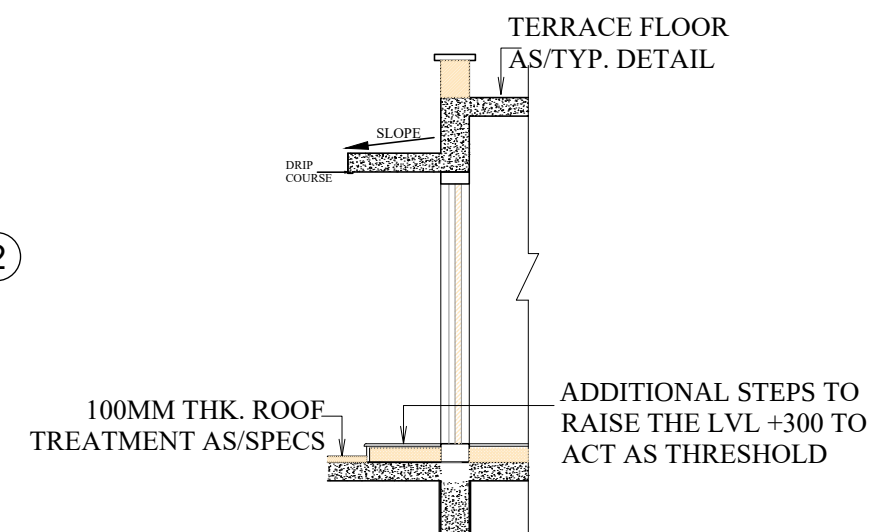

DETAIL D

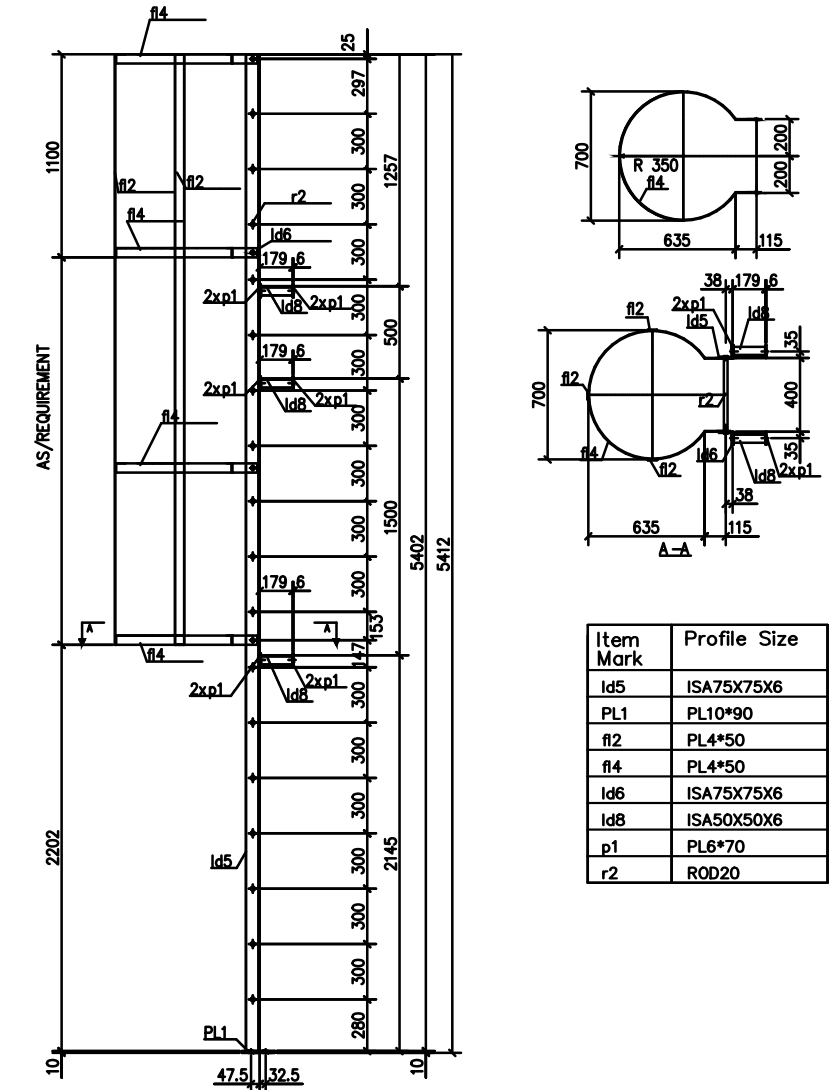

TYPICAL MS LADDER DETAIL

NOTES

- ALL DIMENSIONS ARE IN MM; UNLESS NOTED OTHERWISE.
- WRITTEN DIMENSIONS ARE TO BE FOLLOWED. DRAWINGS ARE NOT TO BE SCALED.
- ANY DISCREPANCY IN THE DRAWING SHALL BE BROUGHT TO THE NOTICE OF THE ENGINEER.
- THIS DRAWING SHALL BE READ IN CONJUNCTION WITH OTHER RELEVANT DRAWINGS.

TENDER DRAWING

CLIENT
OIL INDIA LIMITED
(A Govt. of India Enterprise)

CONSULTANT
IRITES
THE INFRASTRUCTURE PEOPLE
(A Govt. of India Enterprise)


PROJECT
BQ WORKMEN HOUSING

BUILDING
GUEST HOUSE (G+3)


DRAWING TITLE
STAIRCASE & MS LADDER DETAIL

DRG. NO.
MITES/BLD/AR/TD/039


NORTH	SCALE	DATE
	NTS	JULY 2025

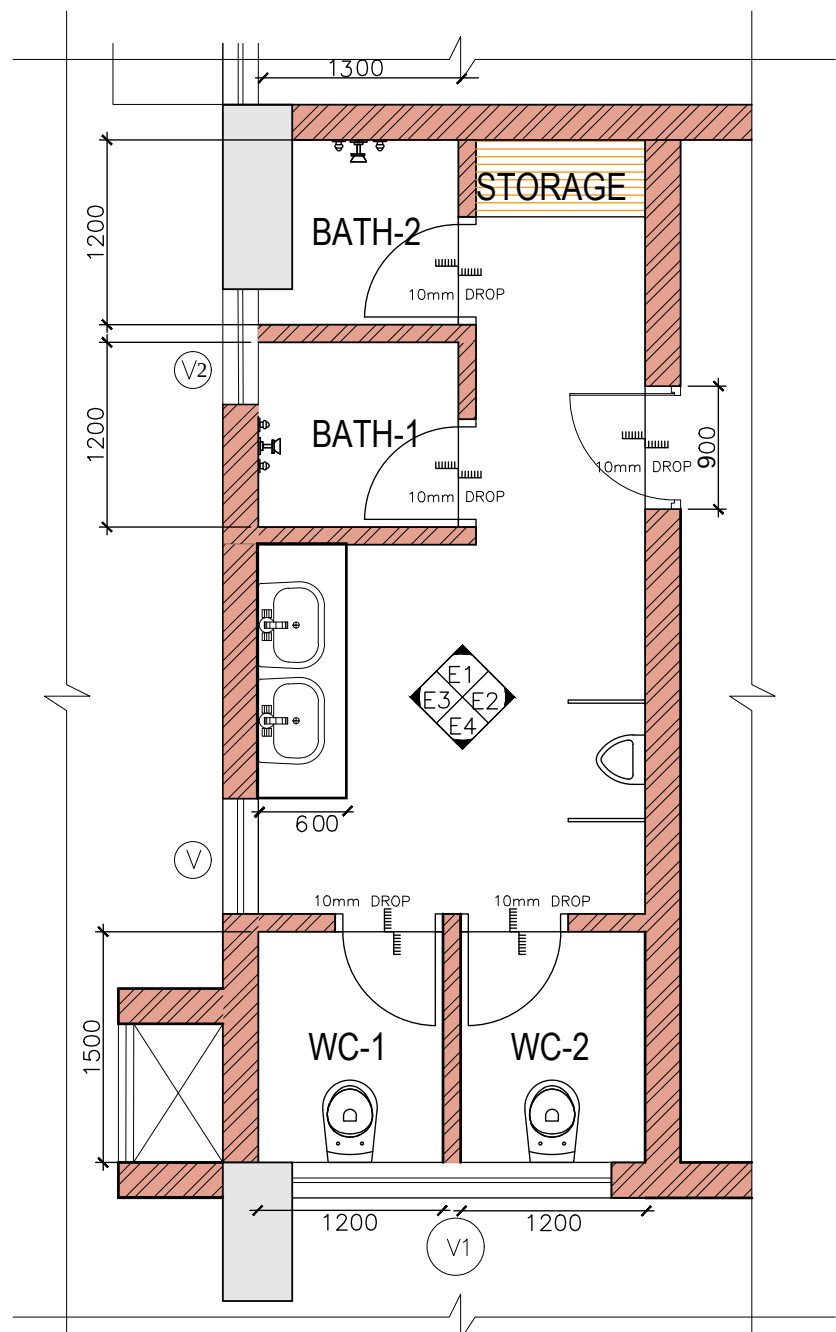


01 PLAN

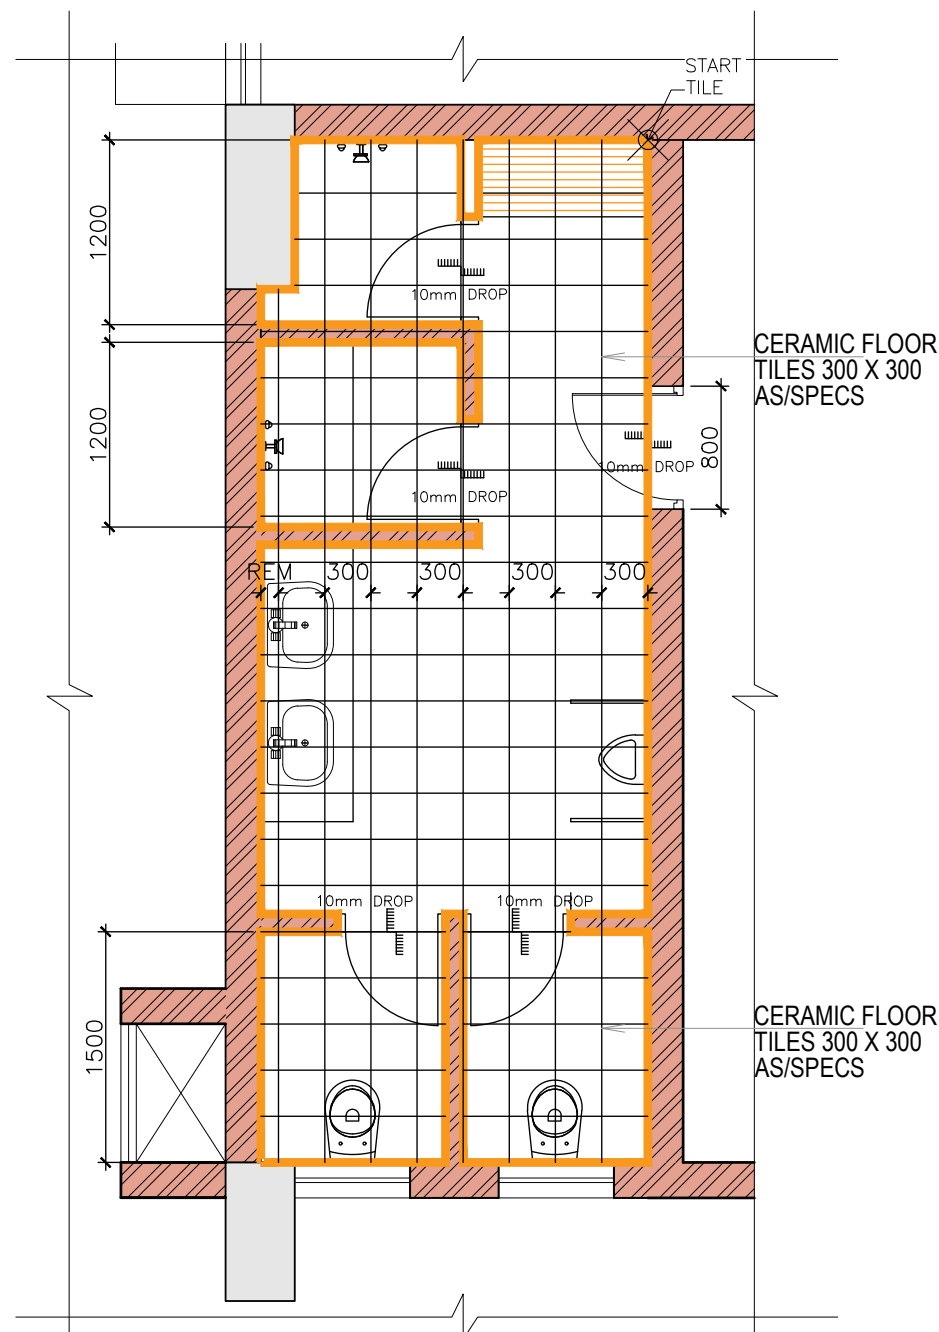


02 PLAN_FLOORING

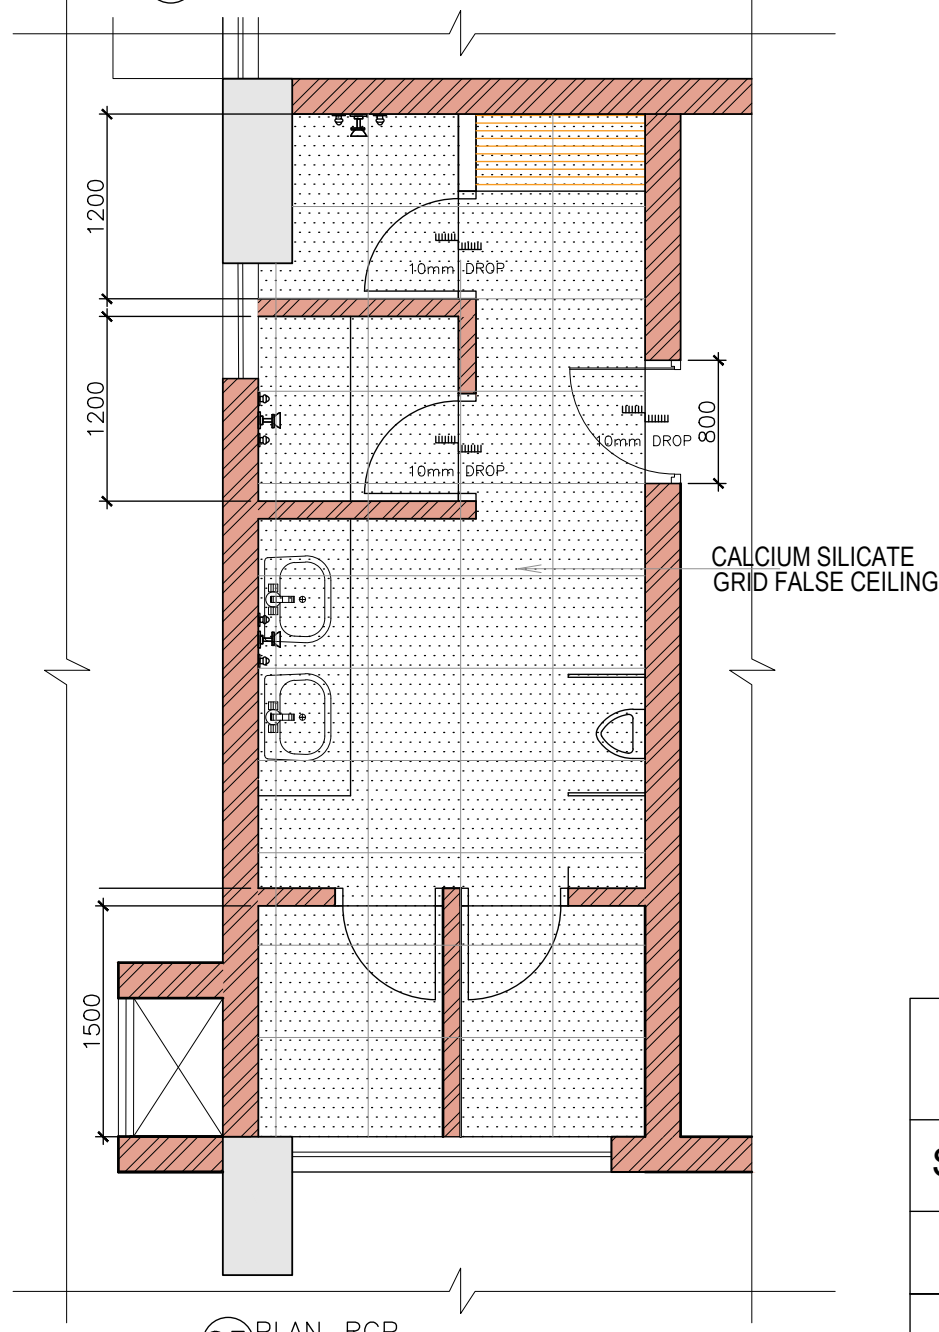


03 PLAN_RCP

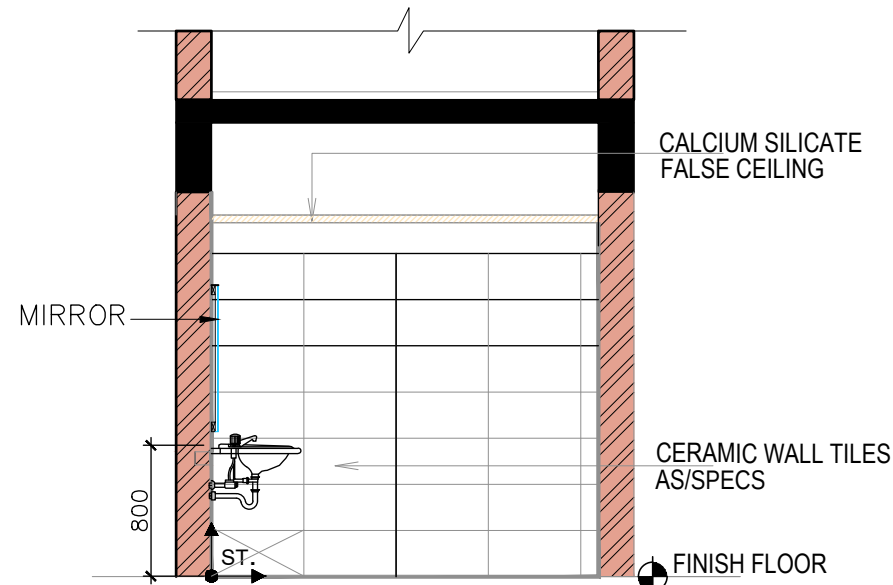


E1 ELEVATION

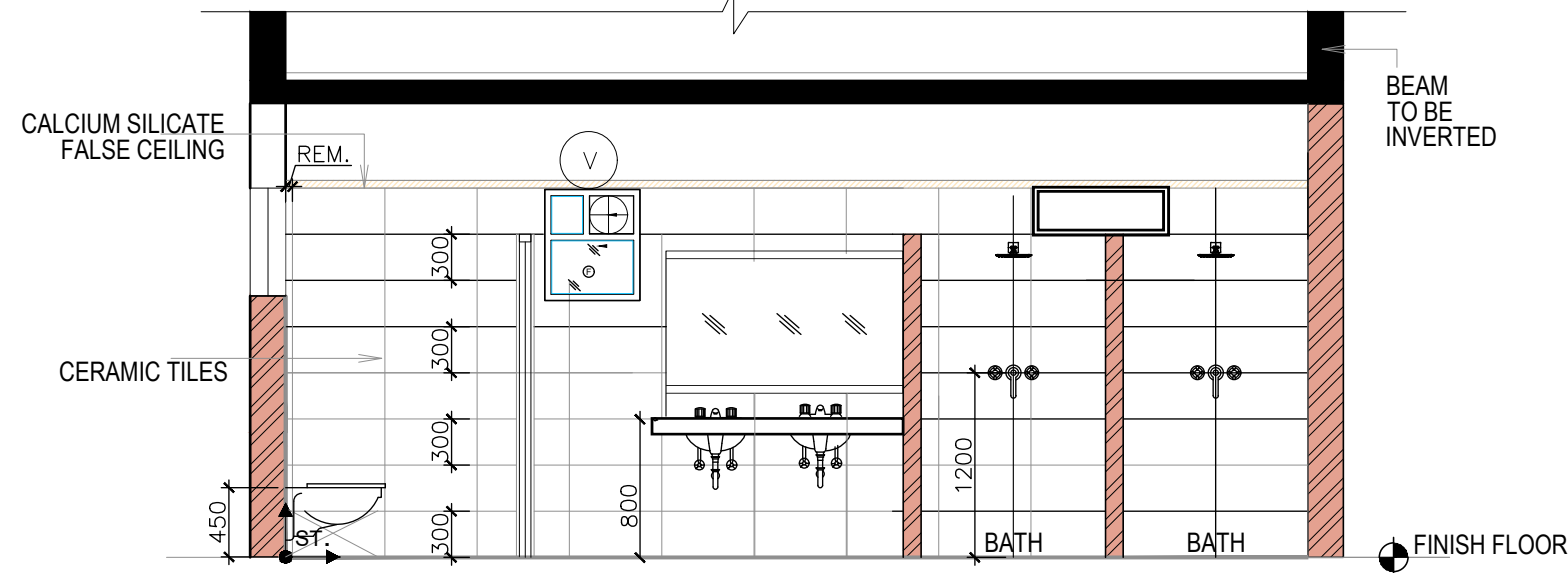

E3 ELEVATION

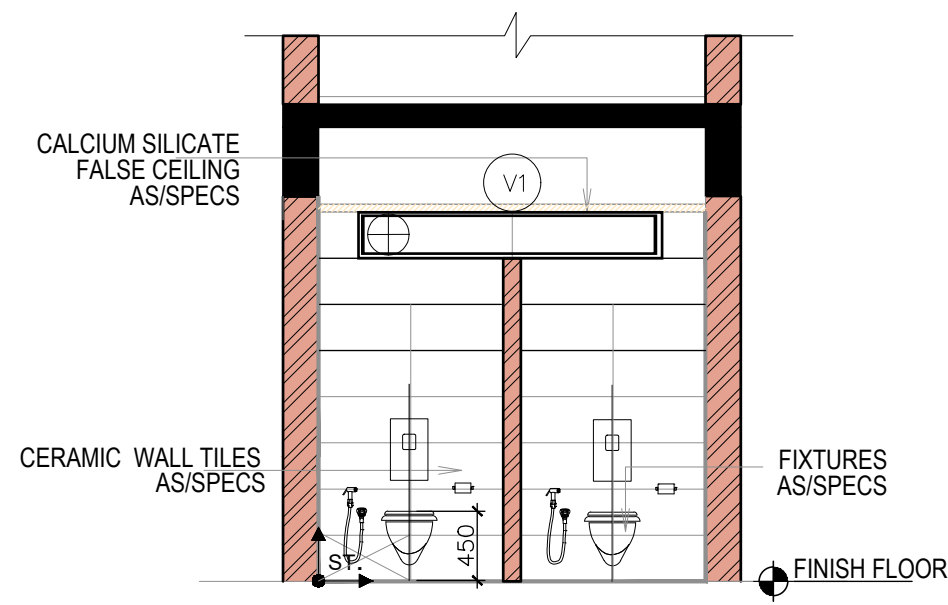

E4 ELEVATION

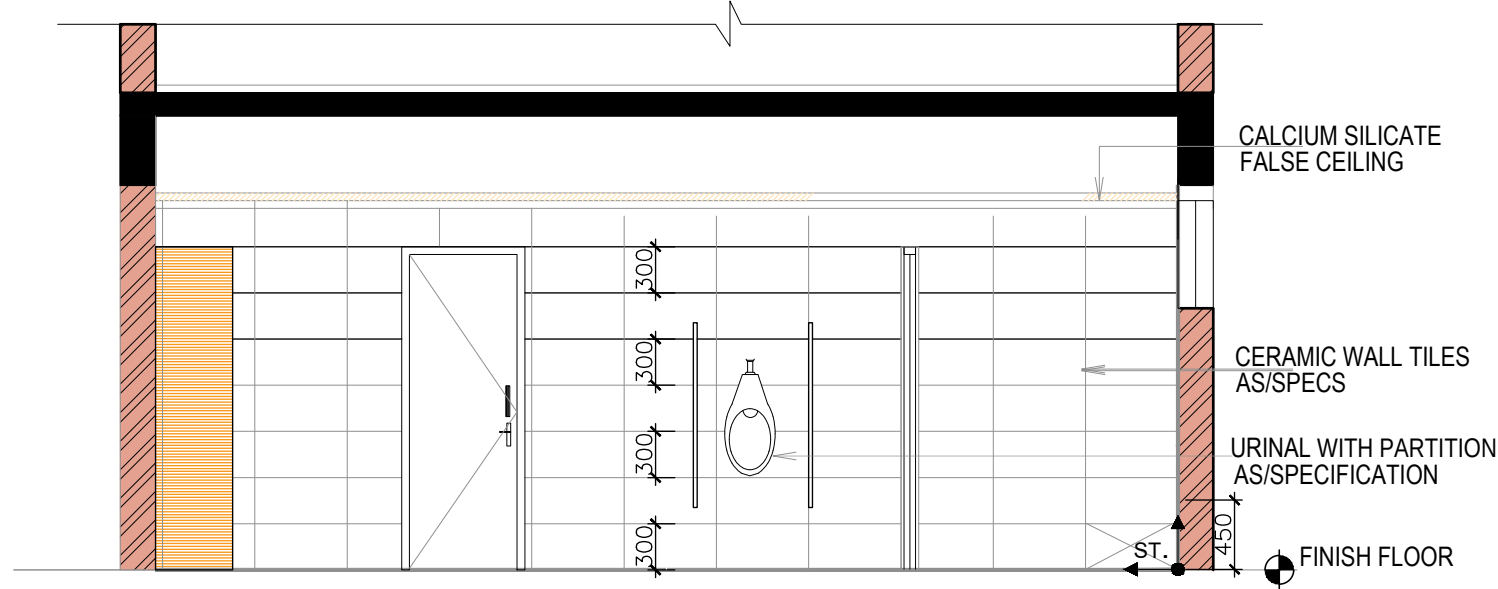


E2 ELEVATION

LEGEND FOR CLADDING/FLOORING

S. NO.	MATERIAL	HEIGHT FROM FFL
01	CERAMIC WALL TILES AS/SPECS	UPTO CEILING HT.
02	RECTIFIED ANTI SKID CERAMIC TILES (300 X 300)	FLOORING

KEY PLAN

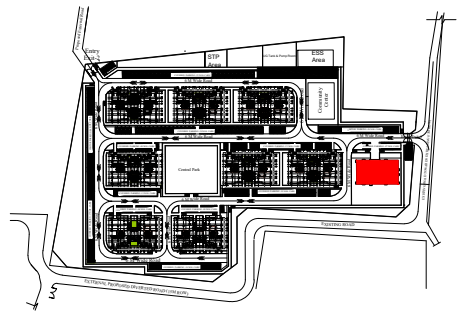

NOTES

- ALL DIMENSIONS ARE IN MM; UNLESS NOTED OTHERWISE.
- WRITTEN DIMENSIONS ARE TO BE FOLLOWED. DRAWINGS ARE NOT TO BE SCALED.
- ANY DISCREPANCY IN THE DRAWING SHALL BE BROUGHT TO THE NOTICE OF THE ENGINEER.
- THIS DRAWING SHALL BE READ IN CONJUNCTION WITH OTHER RELEVANT DRAWINGS.

Sn.No.	Description	Area (Sqm)
01	Ground Floor Area	465 sqm
02	First Floor Area	495 sqm
03	Second Floor Area	500 sqm
04	Third Floor Area	500 sqm
05	Mumty Area	30 sqm

TENDER DRAWING

CLIENT
OIL INDIA LIMITED
(A Govt. of India Enterprise)

CONSULTANT
IRITES
THE INFRASTRUCTURE PEOPLE
(A Govt. of India Enterprise)

PROJECT
BQ WORKMEN HOUSING


BUILDING
GUEST HOUSE (G+3)

DRAWING TITLE
TYPICAL TOILET DETAIL (DORMITORY)

DRG. NO.
BITES/BLD/AR/TD/040

NORTH


SCALE
NTS
DATE
JULY 2025

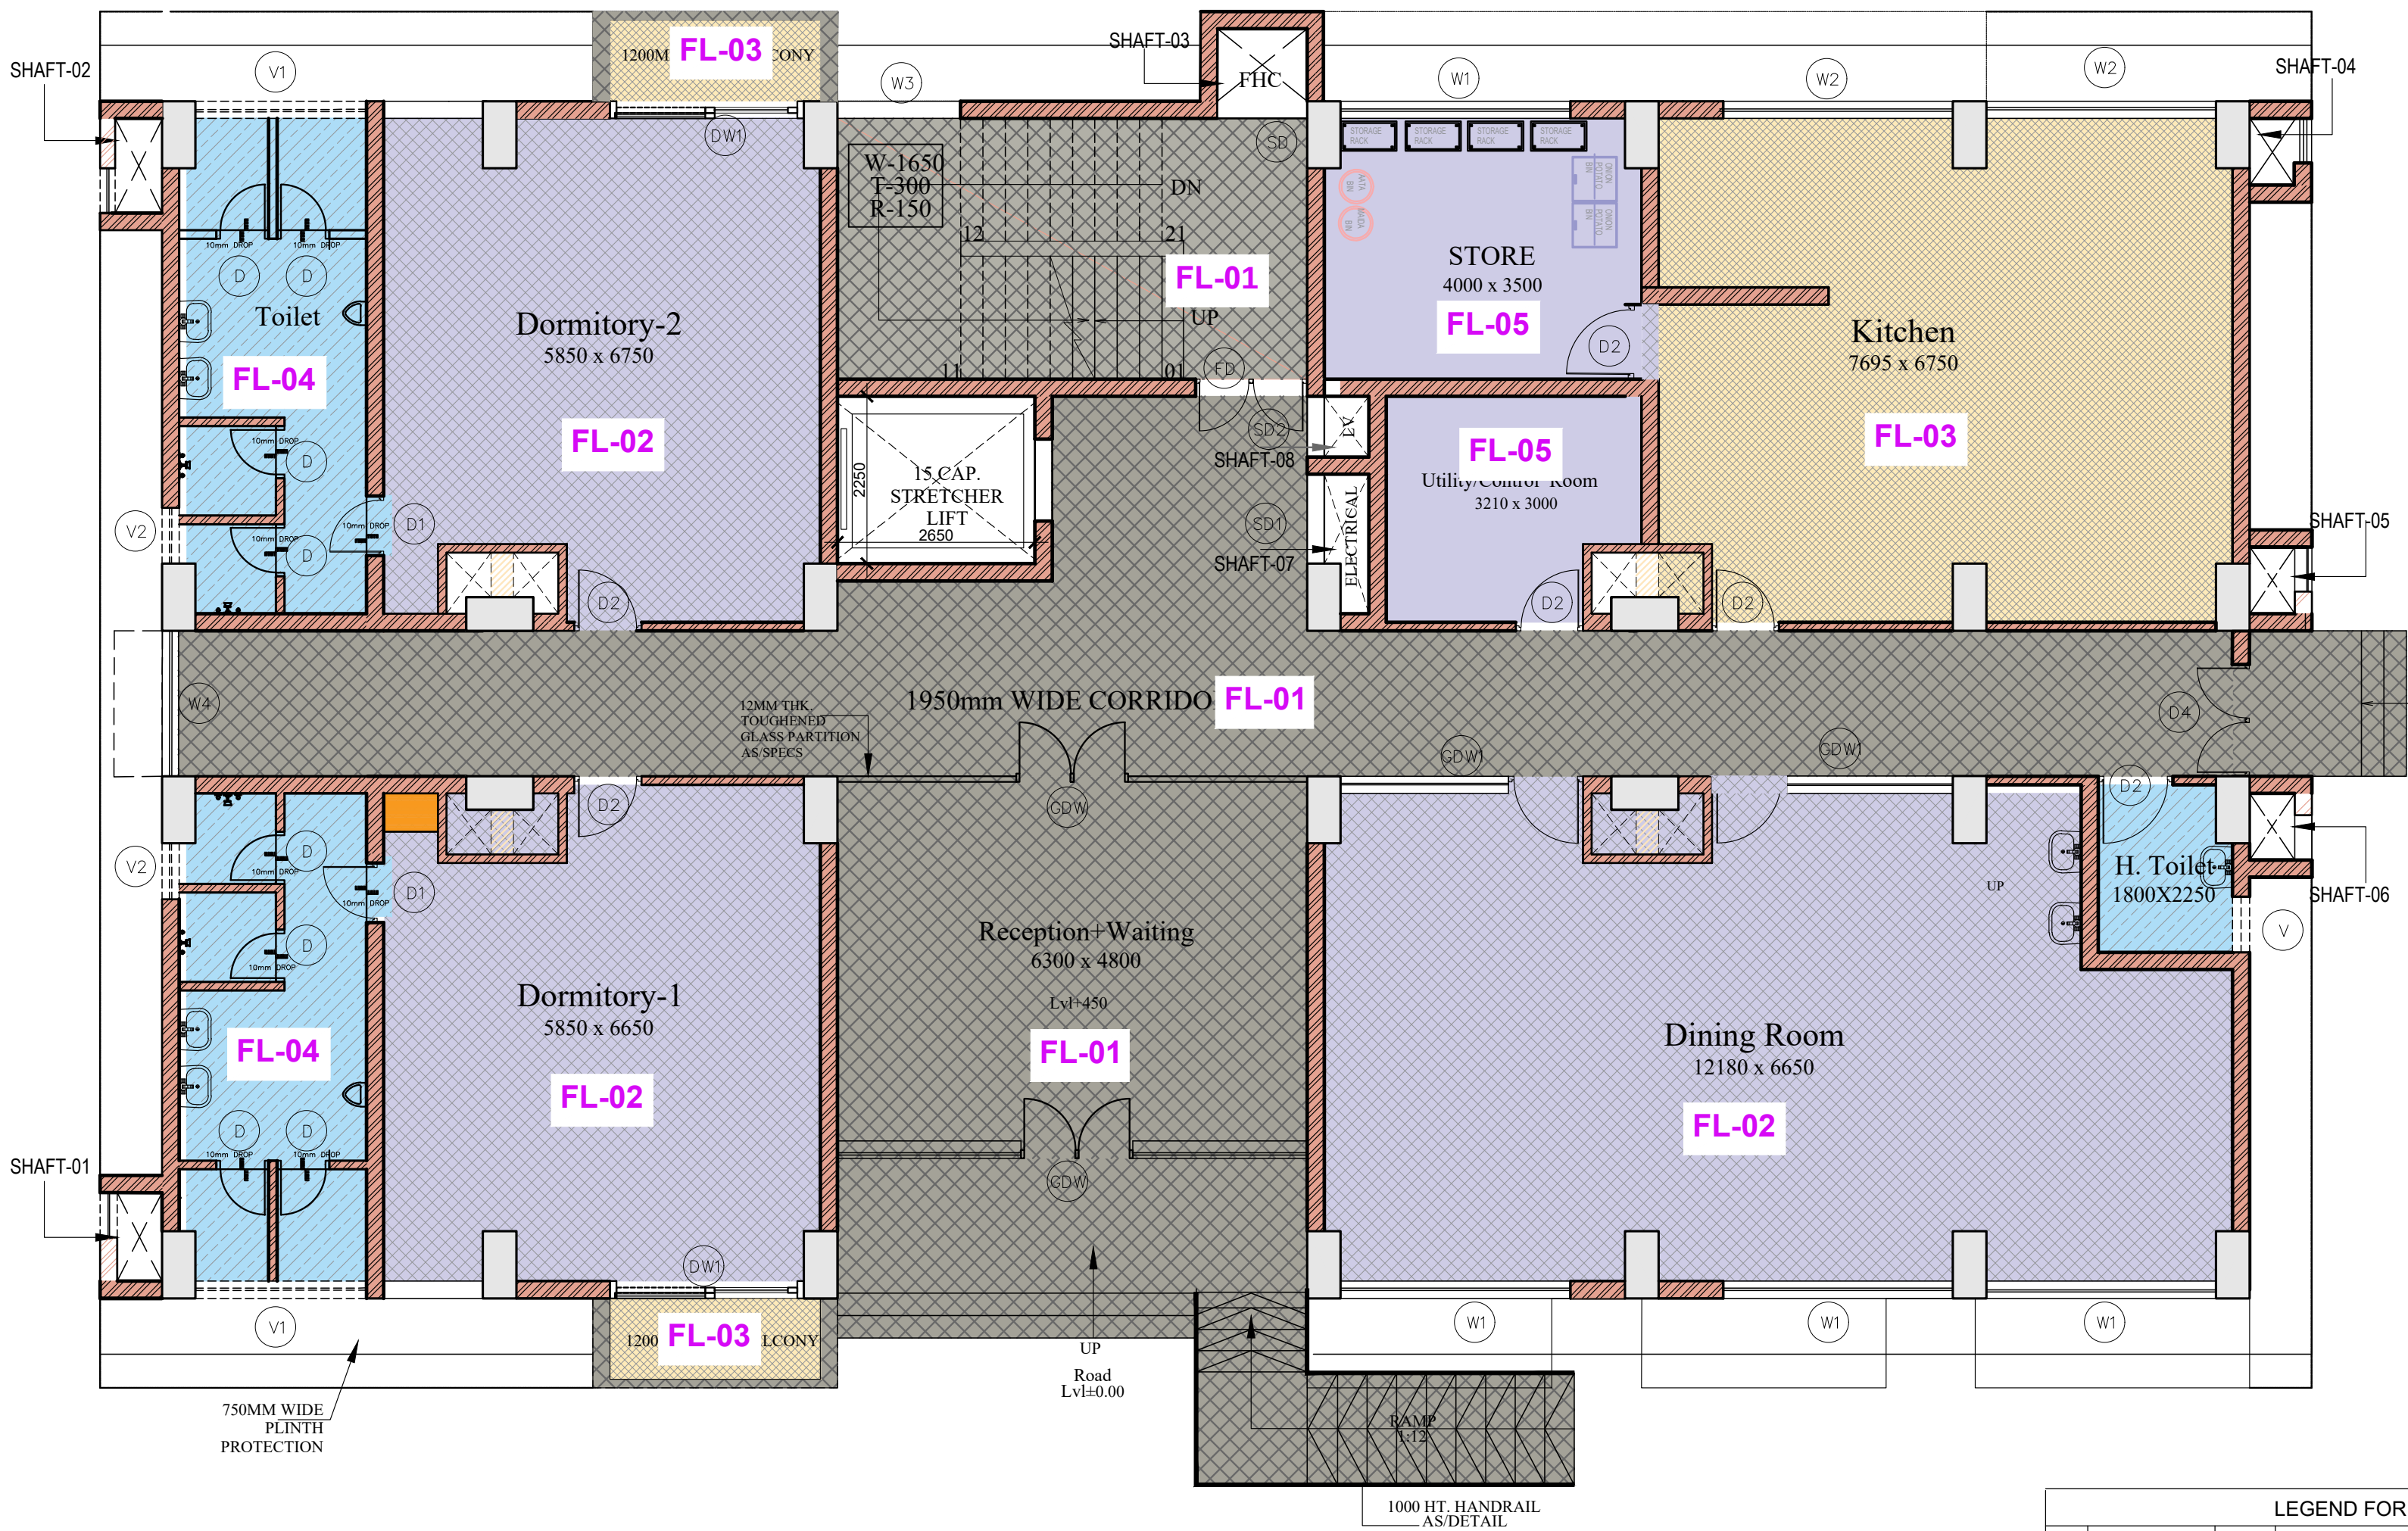

GROUND FLOOR PLAN

LEGEND FOR FLOORING				
S.NO.	HATCH SYMBOL	ICON	MATERIAL	AREA OF APPLICATION
01		FL-01	18MM THK POLISHED GRANITE FLOORING PER SPECS	• LIFT LOBBY AND ENTRANCE, PORCH • RECEPTION & WAITING • CORRIDORS • BALCONY RAILING SILL
02		FL-02	POLISHED GLAZED VITRIFIED TILE (800 X 800)	• DORMITORY • DINING ROOM
03		FL-03	MATT/ANTISKID GLAZED VITRIFIED TILE (800 X 800)	• KITCHEN • BALCONY
04		FL-04	RECTIFIED ANTI SKID CERAMIC TILES (300 X 300)	• TOILETS
05		FL-05	25MM THK. KOTA STONE	• STORE • UTILITY/CONTROL ROOM
06		FL-01	18MM THK POLISHED GRANITE FLOORING ANTI SKID GROOVE AS PER SPECS	• STAIRCASE
07		FL-07	LIQUID RUBBER WATER PROOFING, LAYING CC 1:2:4 CONCRETE FOR ROOF GRADING, HEAT RESISTANT SRI TILES AS PER SPECIFICATIONS.	---
08	SKIRTING 100 MM HIGH, MATCHING THE FLOOR FINISH; DADO IN TOILETS UP TO FALSE CEILING LEVEL AND IN KITCHENS UP TO 2100 MM HEIGHT, ALL AS PER SPECIFICATIONS			

KEY PLAN

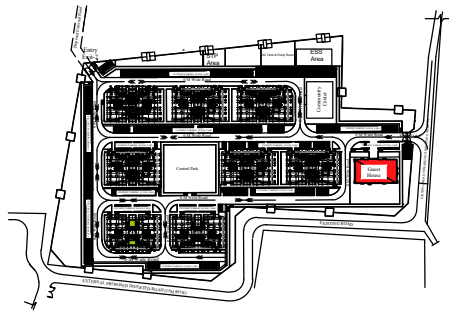

NOTES

1. ALL DIMENSIONS ARE IN MM; UNLESS NOTED OTHERWISE.
2. WRITTEN DIMENSIONS ARE TO BE FOLLOWED. DRAWINGS ARE NOT TO BE SCALED.
3. ANY DISCREPANCY IN THE DRAWING SHALL BE BROUGHT TO THE NOTICE OF THE ENGINEER.
4. THIS DRAWING SHALL BE READ IN CONJUNCTION WITH OTHER RELEVANT DRAWINGS.
5. THE FINISHED FLOOR LEVEL (FFL) SHALL BE MAINTAINED CONSIDERING RACEWAY, AS PER APPLICABLE CODES/ SPECIFICATIONS/ SITE REQUIREMENTS ABOVE THE STRUCTURAL SLAB LEVEL OF ALL BUILDINGS. REFER TENDER DOCUMENT FOR DETAILS.

TENDER DRAWING

CLIENT
 OIL INDIA LIMITED
(A Govt. of India Enterprise)

CONSULTANT
 RITES
THE INFRASTRUCTURE PEOPLE
(A Govt. of India Enterprise)


PROJECT
BQ WORKMEN HOUSING

BUILDING
GUEST HOUSE (G+3)

DRAWING TITLE
FLOORING DETAIL

DRG. NO.
RITES/BLD/AR/TD/041


NORTH 	SCALE NTS	DATE JULY 2025
-----------	--------------	-------------------

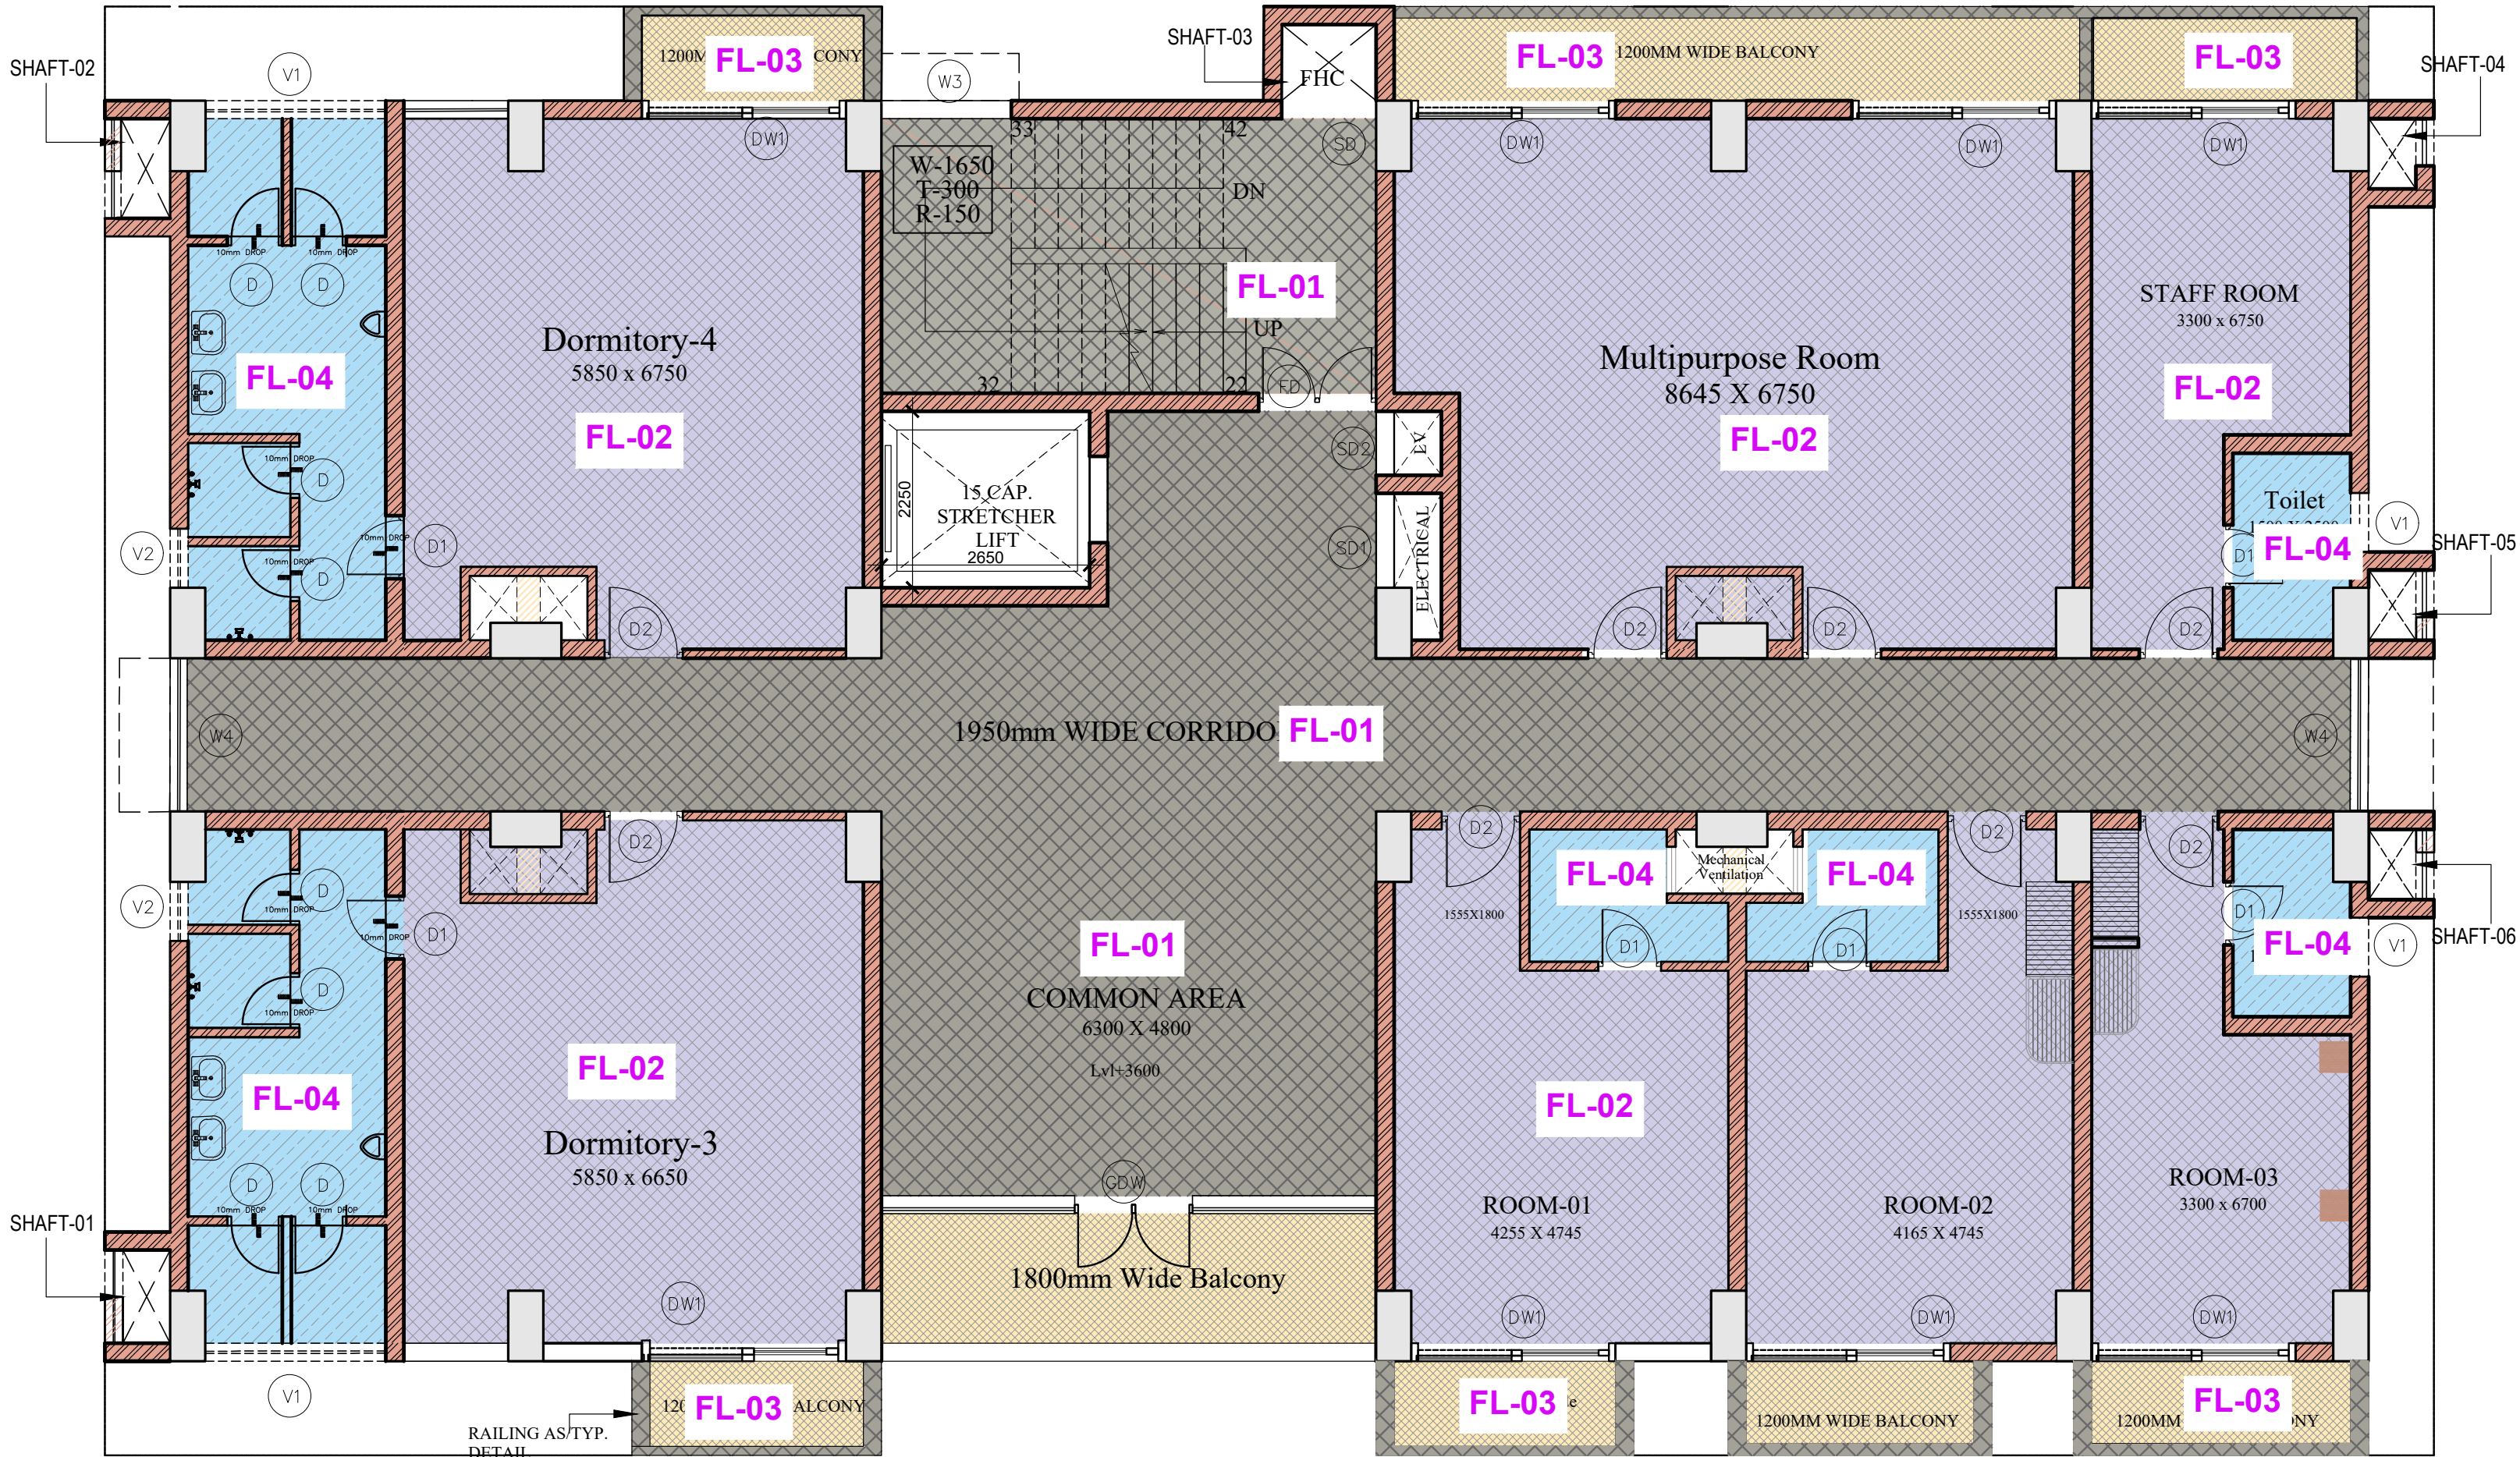

FIRST FLOOR PLAN

LEGEND FOR FLOORING				
S.NO.	HATCH SYMBOL	ICON	MATERIAL	AREA OF APPLICATION
01		FL-01	18MM THK POLISHED GRANITE FLOORING PER SPECS	- LIFT LOBBY - COMMON AREA - CORRIDORS - BALCONY RAILING SILL
02		FL-02	POLISHED GLAZED VITRIFIED TILE (800 X 800)	- DORMITORY - ROOMS - MULTIPURPOSE ROOM - STAFF ROOM
03		FL-03	ANTISKID GLAZED VITRIFIED TILE (800 X 800)	BALCONY
04		FL-04	RECTIFIED ANTI SKID CERAMIC TILES (300 X 300)	TOILETS
05		FL-05	25MM THK. KOTA STONE	---
06		FL-01	18MM THK POLISHE GRANITE FLOORING ANTI SKID GROOVE AS PER SPECS	STAIRCASE
07		FL-07	LIQUID RUBBER WATER PROOFING, LAYING CC 1:2:4 CONCRETE FOR ROOF GRADING, HEAT RESISTANT SRI TILES AS PER SPECIFICATIONS.	---
08	SKIRTING 100 MM HIGH, MATCHING THE FLOOR FINISH; DADO IN TOILETS UP TO FALSE CEILING LEVEL ALL AS PER SPECIFICATIONS			

KEY PLAN

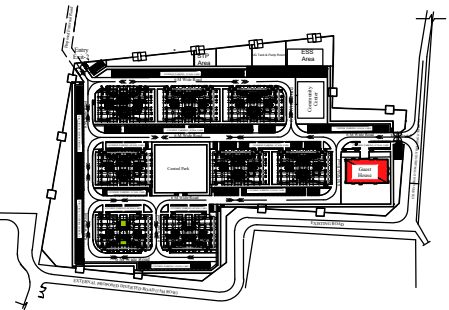

NOTES

- ALL DIMENSIONS ARE IN MM; UNLESS NOTED OTHERWISE.
- WRITTEN DIMENSIONS ARE TO BE FOLLOWED. DRAWINGS ARE NOT TO BE SCALED.
- ANY DISCREPANCY IN THE DRAWING SHALL BE BROUGHT TO THE NOTICE OF THE ENGINEER.
- THIS DRAWING SHALL BE READ IN CONJUNCTION WITH OTHER RELEVANT DRAWINGS.
- THE FINISHED FLOOR LEVEL (FFL) SHALL BE MAINTAINED CONSIDERING RACEWAY, AS PER APPLICABLE CODES/ SPECIFICATIONS/ SITE REQUIREMENTS ABOVE THE STRUCTURAL SLAB LEVEL OF ALL BUILDINGS. REFER TENDER DOCUMENT FOR DETAILS.

TENDER DRAWING


CLIENT	OIL INDIA LIMITED (A Govt. of India Enterprise)		
CONSULTANT	MITES THE INFRASTRUCTURE PEOPLE (A Govt. of India Enterprise)		
PROJECT	BQ WORKMEN HOUSING		
BUILDING	GUEST HOUSE (G+3)		
DRAWING TITLE	FLOORING DETAIL		
DRG. NO.	MITES/BLD/AR/TD/042		
NORTH	SCALE	DATE	
	NTS	JULY 2025	



SECOND FLOOR PLAN

LEGEND FOR FLOORING				
S.NO.	HATCH SYMBOL	ICON	MATERIAL	AREA OF APPLICATION
01		FL-01	18MM THK POLISHED GRANITE FLOORING PER SPECS	• LIFT LOBBY • COMMON AREA • CORRIDORS • BALCONY RAILING SILL
02		FL-02	POLISHED GLAZED VITRIFIED TILE (800 X 800)	• ROOMS • STAFF ROOM
03		FL-03	MATT/ANTISKID GLAZED VITRIFIED TILE (800 X 800)	• BALCONY • HOUSEKEEPING ROOM
04		FL-04	RECTIFIED ANTI SKID CERAMIC TILES (300 X 300)	• TOILETS
05		FL-05	25MM THK. KOTA STONE	---
06		FL-01	18MM THK POLISHE GRANITE FLOORING ANTI SKID GROOVE AS PER SPECS	• STAIRCASE
07		FL-07	LIQUID RUBBER WATER PROOFING, LAYING CC 1:2:4 CONCRETE FOR ROOF GRADING, HEAT RESISTANT SRI TILES AS PER SPECIFICATIONS.	---
08	SKIRTING 100 MM HIGH, MATCHING THE FLOOR FINISH; DADO IN TOILETS UP TO FALSE CEILING LEVEL A ALL AS PER SPECIFICATIONS			

KEY PLAN

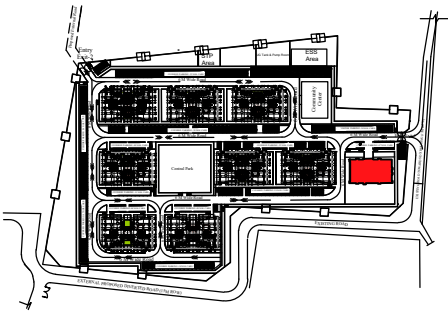

NOTES

1. ALL DIMENSIONS ARE IN MM; UNLESS NOTED OTHERWISE.
2. WRITTEN DIMENSIONS ARE TO BE FOLLOWED. DRAWINGS ARE NOT TO BE SCALED.
3. ANY DISCREPANCY IN THE DRAWING SHALL BE BROUGHT TO THE NOTICE OF THE ENGINEER.
4. THIS DRAWING SHALL BE READ IN CONJUNCTION WITH OTHER RELEVANT DRAWINGS.
5. THE FINISHED FLOOR LEVEL (FFL) SHALL BE MAINTAINED CONSIDERING RACEWAY, AS PER APPLICABLE CODES/ SPECIFICATIONS/ SITE REQUIREMENTS ABOVE THE STRUCTURAL SLAB LEVEL OF ALL BUILDINGS. REFER TENDER DOCUMENT FOR DETAILS.

TENDER DRAWING


CLIENT	 OIL INDIA LIMITED (A Govt. of India Enterprise)		
CONSULTANT	 THE INFRASTRUCTURE PEOPLE (A Govt. of India Enterprise)		
PROJECT	BQ WORKMEN HOUSING		
BUILDING	GUEST HOUSE (G+3)		
DRAWING TITLE	FLOORING DETAIL		
DRG. NO.	MITES/BLD/AR/TD/043		
NORTH	SCALE	DATE	
	NTS	JULY 2025	



THIRD FLOOR PLAN

LEGEND FOR FLOORING				
S.NO.	HATCH SYMBOL	ICON	MATERIAL	AREA OF APPLICATION
01		FL-01	18MM THK POLISHED GRANITE FLOORING PER SPECS	- LIFT LOBBY - COMMON AREA - CORRIDORS - BALCONY RAILING SILL
02		FL-02	POLISHED GLAZED VITRIFIED TILE (800 X 800)	- ROOMS - STAFF ROOM
03		FL-03	MATT/ANTISKID GLAZED VITRIFIED TILE (800 X 800)	- BALCONY - HOUSE KEEPING ROOM
04		FL-04	RECTIFIED ANTI SKID CERAMIC TILES (300 X 300)	TOILETS
05		FL-05	25MM THK. KOTA STONE	---
06		FL-01	18MM THK POLISHE GRANITE FLOORING ANTI SKID GROOVE AS PER SPECS	STAIRCASE
07		FL-07	LIQUID RUBBER WATER PROOFING, LAYING CC 1:2:4 CONCRETE FOR ROOF GRADING, HEAT RESISTANT SRI TILES AS PER SPECIFICATIONS.	---
08	SKIRTING 100 MM HIGH, MATCHING THE FLOOR FINISH; DADO IN TOILETS UP TO FALSE CEILING LEVEL A ALL AS PER SPECIFICATIONS			

KEY PLAN

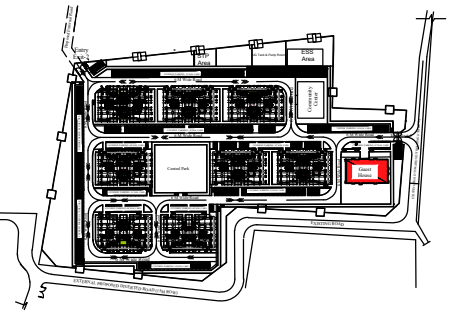

NOTES

- ALL DIMENSIONS ARE IN MM; UNLESS NOTED OTHERWISE.
- WRITTEN DIMENSIONS ARE TO BE FOLLOWED. DRAWINGS ARE NOT TO BE SCALED.
- ANY DISCREPANCY IN THE DRAWING SHALL BE BROUGHT TO THE NOTICE OF THE ENGINEER.
- THIS DRAWING SHALL BE READ IN CONJUNCTION WITH OTHER RELEVANT DRAWINGS.
- THE FINISHED FLOOR LEVEL (FFL) SHALL BE MAINTAINED CONSIDERING RACEWAY, AS PER APPLICABLE CODES/ SPECIFICATIONS/ SITE REQUIREMENTS ABOVE THE STRUCTURAL SLAB LEVEL OF ALL BUILDINGS. REFER TENDER DOCUMENT FOR DETAILS.

TENDER DRAWING

CLIENT OIL INDIA LIMITED
(A Govt. of India Enterprise)

CONSULTANT RITES
THE INFRASTRUCTURE PEOPLE
(A Govt. of India Enterprise)


PROJECT **BQ WORKMEN HOUSING**

BUILDING **GUEST HOUSE (G+3)**

DRAWING TITLE **FLOORING DETAIL**

DRG. NO. **MITES/BLD/AR/TD/044**

NORTH	SCALE NTS	DATE JULY 2025
-------	---------------------	--------------------------

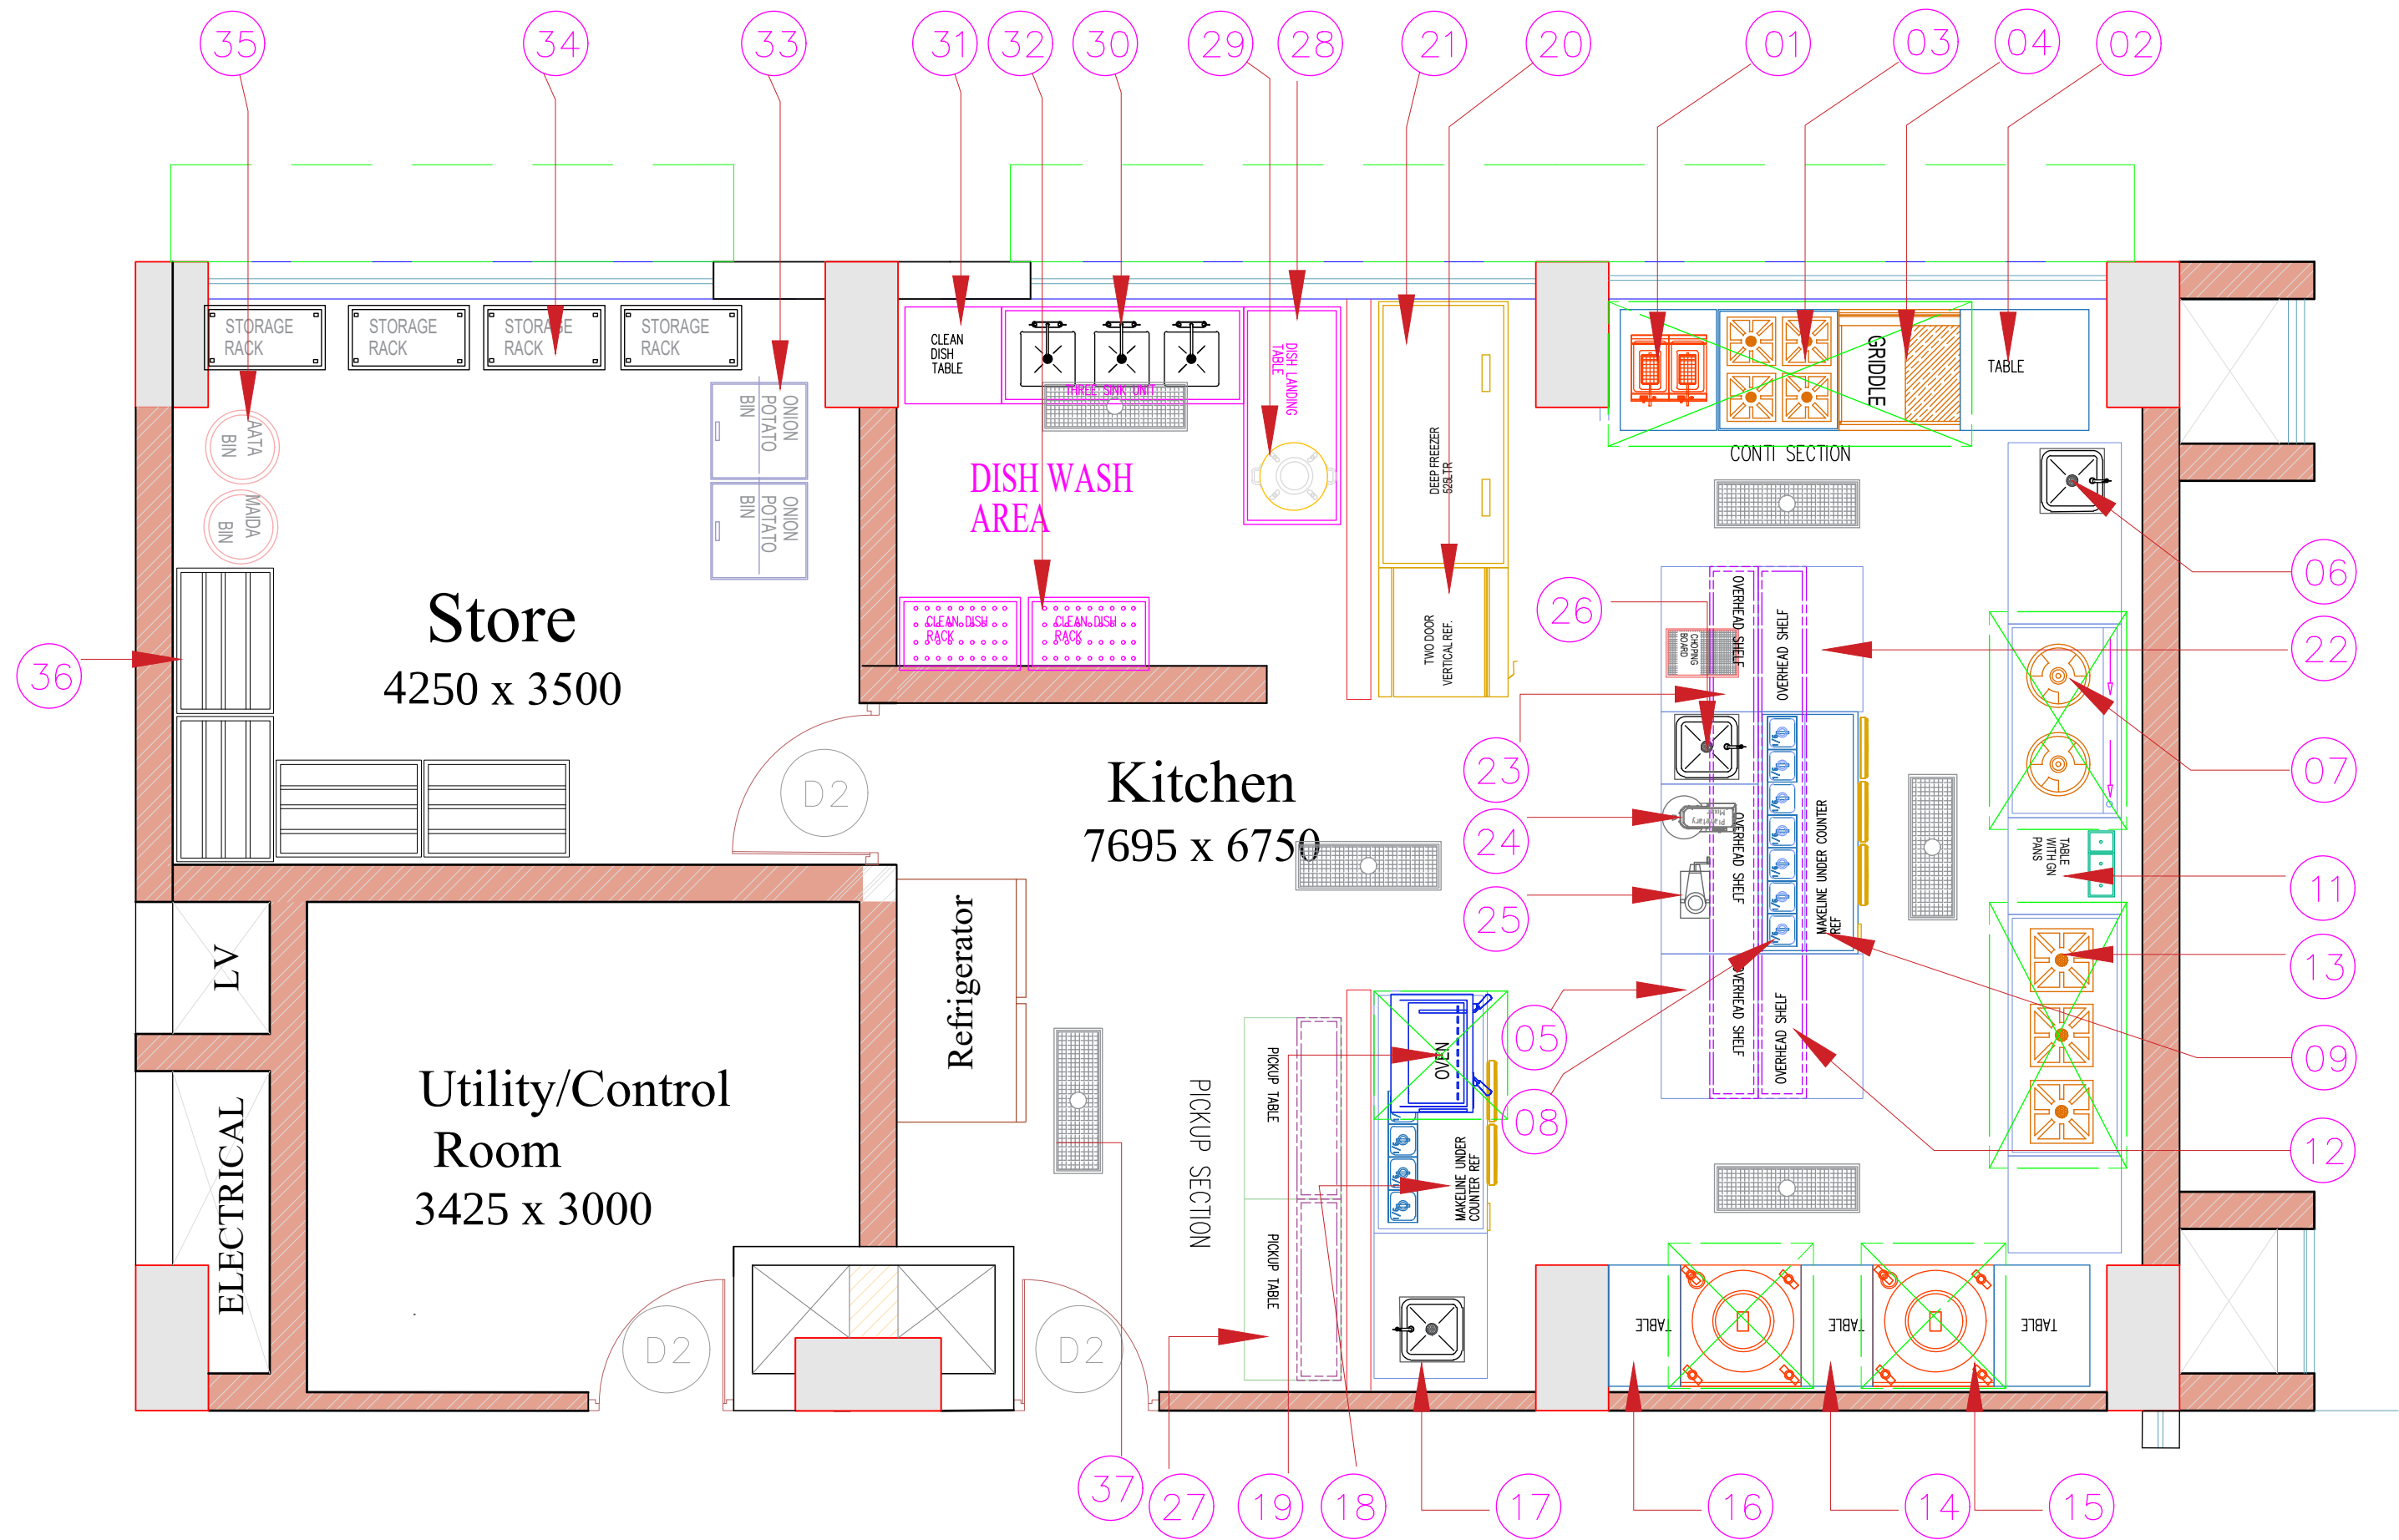

S.No.	ITEM DESCRIPTION	QTY TO BE PROVIDED		
01	DOUBLE DEEP FAT FRYER	1	21	DEEP FREEZER MAKE - WESTERN
02	TABLE FOR FRYER	1	22	PREPARATION TABLE
03	FOUR BURNER RANGE	1	23	OVERHEAD SHELF
04	GRIDDLE PLATE	1	24	PLANTERY MIXER
05	WORK TABLE	1	25	JTC BLENDER
06	WORK TABLE WITH SINK	1	26	SINGLE SINK
07	TWO BURNER CHINESE RANGE	1	27	PICKUP TABLE WITH OHS
08	MIZZA TABLE	1		DISH WASH AREA
10	OVERHEAD HEATING ELEMENT	1	28	DISH LANDING TABLE
11	WORK TABLE	1	29	GARBAGE BIN
12	OVERHEAD SHELF	1	30	THREE SINK UNIT
13	THREE BURNER RANGE	1	31	CLEAN DISH TABLE
14	WORK TABLE	1	32	RACK
15	SS TANDOOR	2		STORE ROOM
16	WORK TABLE	2	33	POTATO ONION BIN MS
17	TABLE WITH SINK	1	34	MS STORAGE RACK
18	UNDER COUNTER REF.	1	35	AATA /MAIDA DRUM
19	WALL MOUNTED DECK OVEN	1	36	PLASTIC PALLET
20	TWO DOOR VERTICAL REF.	1	37	EXHAUST HOOD
			38	EXHAUST HOOD
			39	EXHAUST HOOD
			40	EXHAUST HOOD
			41	EXHAUST HOOD

NOTES

1. ALL DIMENSIONS ARE IN MM; UNLESS NOTED OTHERWISE.
2. WRITTEN DIMENSIONS ARE TO BE FOLLOWED. DRAWINGS ARE NOT TO BE SCALED.
3. ANY DISCREPANCY IN THE DRAWING SHALL BE BROUGHT TO THE NOTICE OF THE ENGINEER.
4. THIS DRAWING SHALL BE READ IN CONJUNCTION WITH OTHER RELEVANT DRAWINGS.
5. THE DRAWING IS INDICATIVE ONLY.
6. SHOP DRAWING FOR KITCHEN TO BE PREPARED FOR APPROVAL.
7. REFER RELEVANT SPECIFICATION.

TENDER DRAWING

CLIENT



OIL INDIA LIMITED
(A Govt. of India Enterprise)

CONSULTANT



PROJECT

BQ WORKMEN HOUSING

BUILDING

GUEST HOUSE(G+3)

DRAWING TITLE

COMMERCIAL KITCHEN DETAIL

DRG. NO.

MITES/BLD/AR/TD/046

NORTH



SCALE

NTS

DATE

JULY 2025