


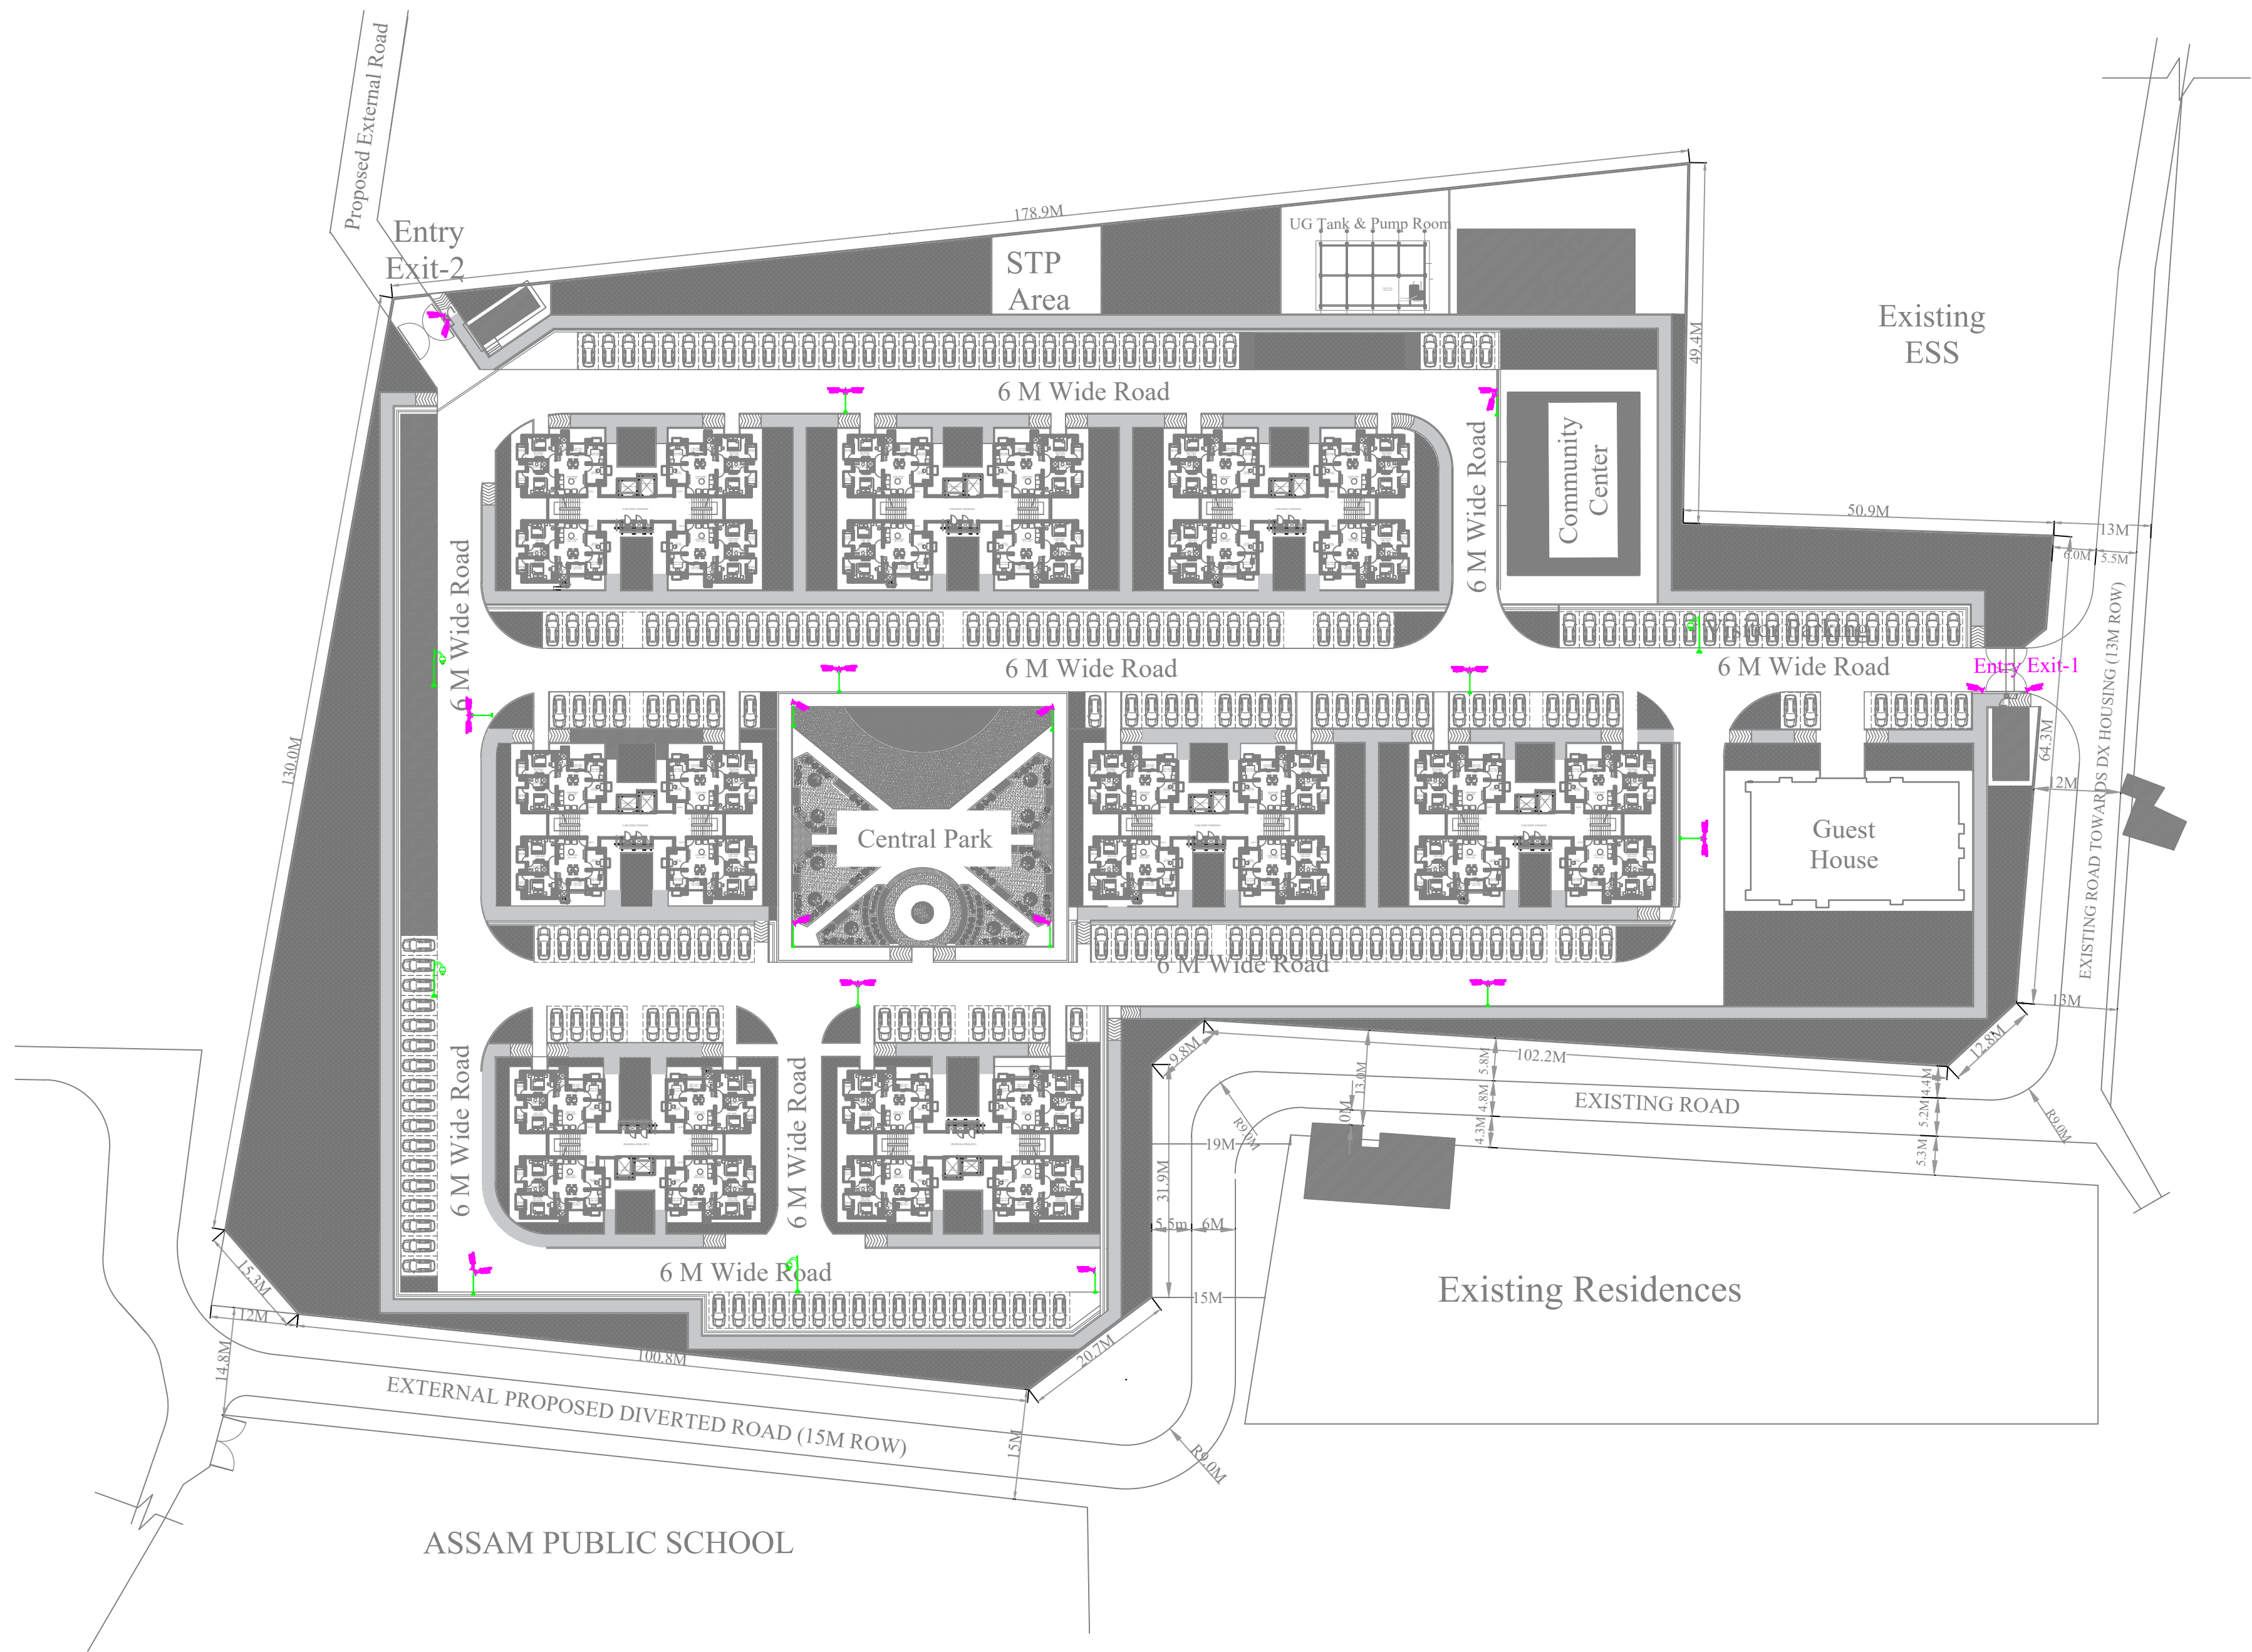

SITE LAYOUT

THESE ARE THE MINIMUM REQUIREMENT, IN CASE ANY
ADDITIONAL REQUIREMENT EPC CONTRACTOR HAS TO
CONSIDER WITHOUT ANY EXTRA COST

LEGENDS:-

Sr.NO.	DESCRIPTION	SYMBOL.	QTY.
1.	5MP PTZ CAMERA		04
2.	5MP BULLET CAMERA		27

CONSULTANT :



MEP CONSULTANT



PKV Consulting Engineers (P) Ltd.
C-815, DDA Flats, Loni Road, Delhi - 110093
E-mail - pramod@pkv.co.in, info@pkv.co.in
TELEFAX - 011-22816297

REVISION DATE DESCRIPTIONS

PROJECT:
BQ WORKMEN GROUP HOUSING
COMPLEX AT DULIAJAN ASSAM.

CLIENT:-




OIL INDIA LIMITED
(A Govt. of India Enterprise)

DRAWING TITLE :

EXTERNAL CCTV LAYOUT PLAN


SCALE	DATE:	DRAWING NUMBER
NTS	JULY 2025	MITES/BLD/EL/TEN/210

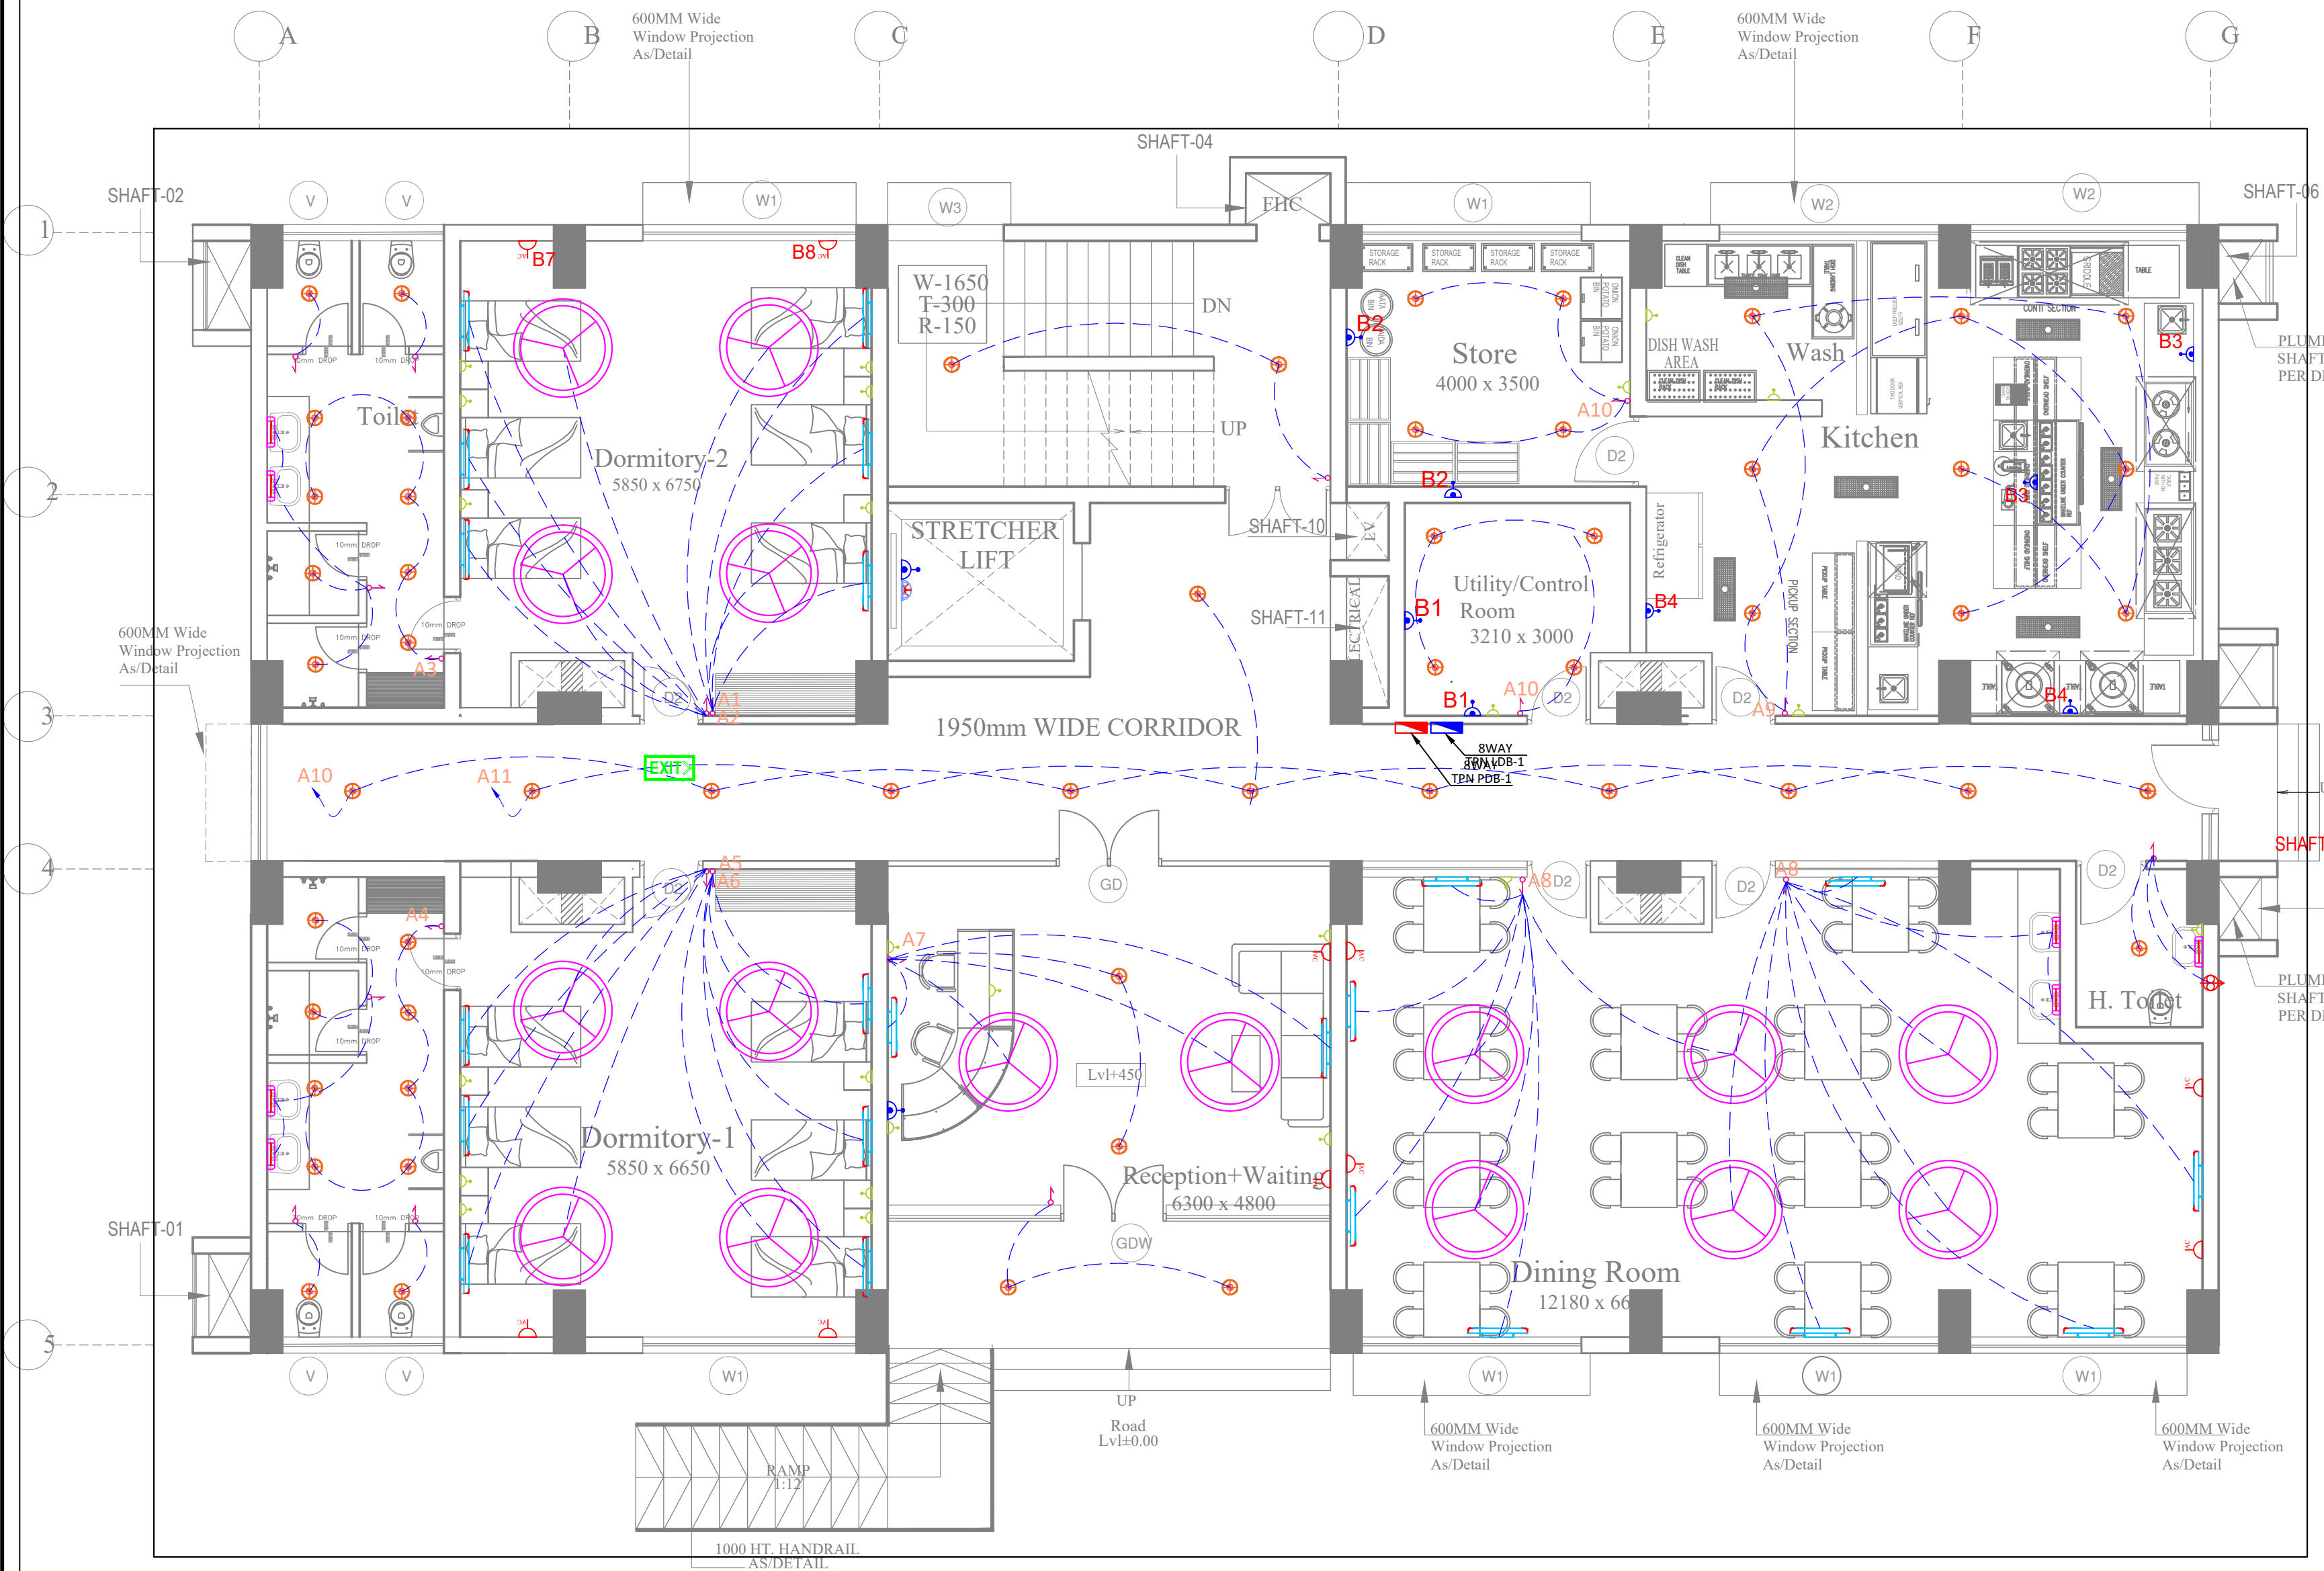

LEGEND :-			
S. No.	SYMBOL	DESCRIPTION	POSITION HEIGHT
1.		6A ONE WAY SWITCH BOARD	AS PER CPWD
2.		1400 MMØ CEILING FAN	CEILING
3.		36W WALL MOUNTED LIGHT	AS PER CPWD
4.		12W LED CEILING LIGHT	CEILING
5.		10W LED MIRROR LIGHT	AS PER CPWD
6.		6A SWITCH SOCKET OUTLET	AS PER CPWD
7.		EXHAUST FAN	AS PER CPWD
8.		16A SWITCH SOCKET OUTLET	AS PER CPWD
9.		25A SOCKET FOR AC	AS PER CPWD
10.		TV POINT	AS PER CPWD
11.		LOOPING	AS PER CPWD
12.		12W BULK HEAD LIGHT	AS PER CPWD
13.		36 W LED SURFACE MOUNTED TUBE LIGHT	AS PER CPWD
14.		DISTRIBUTION BOARD POWER	AS PER CPWD
15.		DISTRIBUTION BOARD LIGHT	AS PER CPWD

NOTES:-	
1.	ALL DIMENSIONS ARE IN MM; UNLESS NOTED OTHERWISE.
2.	WRITTEN DIMENSIONS ARE TO BE FOLLOWED. DRAWINGS ARE NOT TO BE SCALED.
3.	ANY DISCREPANCY IN THE DRAWING SHALL BE BROUGHT TO THE NOTICE OF THE ENGINEER-IN-CHARGE.
4.	THIS DRAWING SHALL BE READ IN CONJUNCTION WITH OTHER RELEVANT DRAWINGS.
5.	ALL ELECTRICAL WORKS SHALL BE COMPLETED AS PER CPWD SPECIFICATIONS, RELEVANT IS CODE & REGULATION OF THE ELECTRICAL AUTHORITIES' ETC. AS REQUIRED.
6.	EPC CONTRACTOR TO SUBMIT SHOP DRAWINGS FOR APPROVAL BEFORE EXECUTION OF WORK.
7.	DISCREPANCY, IF ANY SHALL BE BROUGHT TO THE NOTICE OF ENGINEER-IN-CHARGE AND CLARIFICATION OBTAINED IN WRITING PRIOR TO EXECUTION OF THE WORK.


TENDER DRAWING		
CLIENT	OIL INDIA LIMITED (A Govt. of India Enterprise)	
CONSULTANT	RITES THE INFRASTRUCTURE PEOPLE (A Govt. of India Enterprise)	
MEP CONSULTANT	PKV CONSULTING ENGINEERS (P) LTD. 815 - C DDA FLATS EAST OF LONI ROAD DELHI - 110093 email:-info@pkv.co.in	
JOB TITLE	BQ WORKMEN GROUP HOUSING COMPLEX AT DULIAJAN ASSAM.	
DRAWING TITLE	GUEST HOUSE, GROUND FLOOR LIGHTING & POWER LAYOUT	
SCALE	DATE	DRG. NO.
NTS	JULY 2025	MITES/BLD/EL/TEN/211

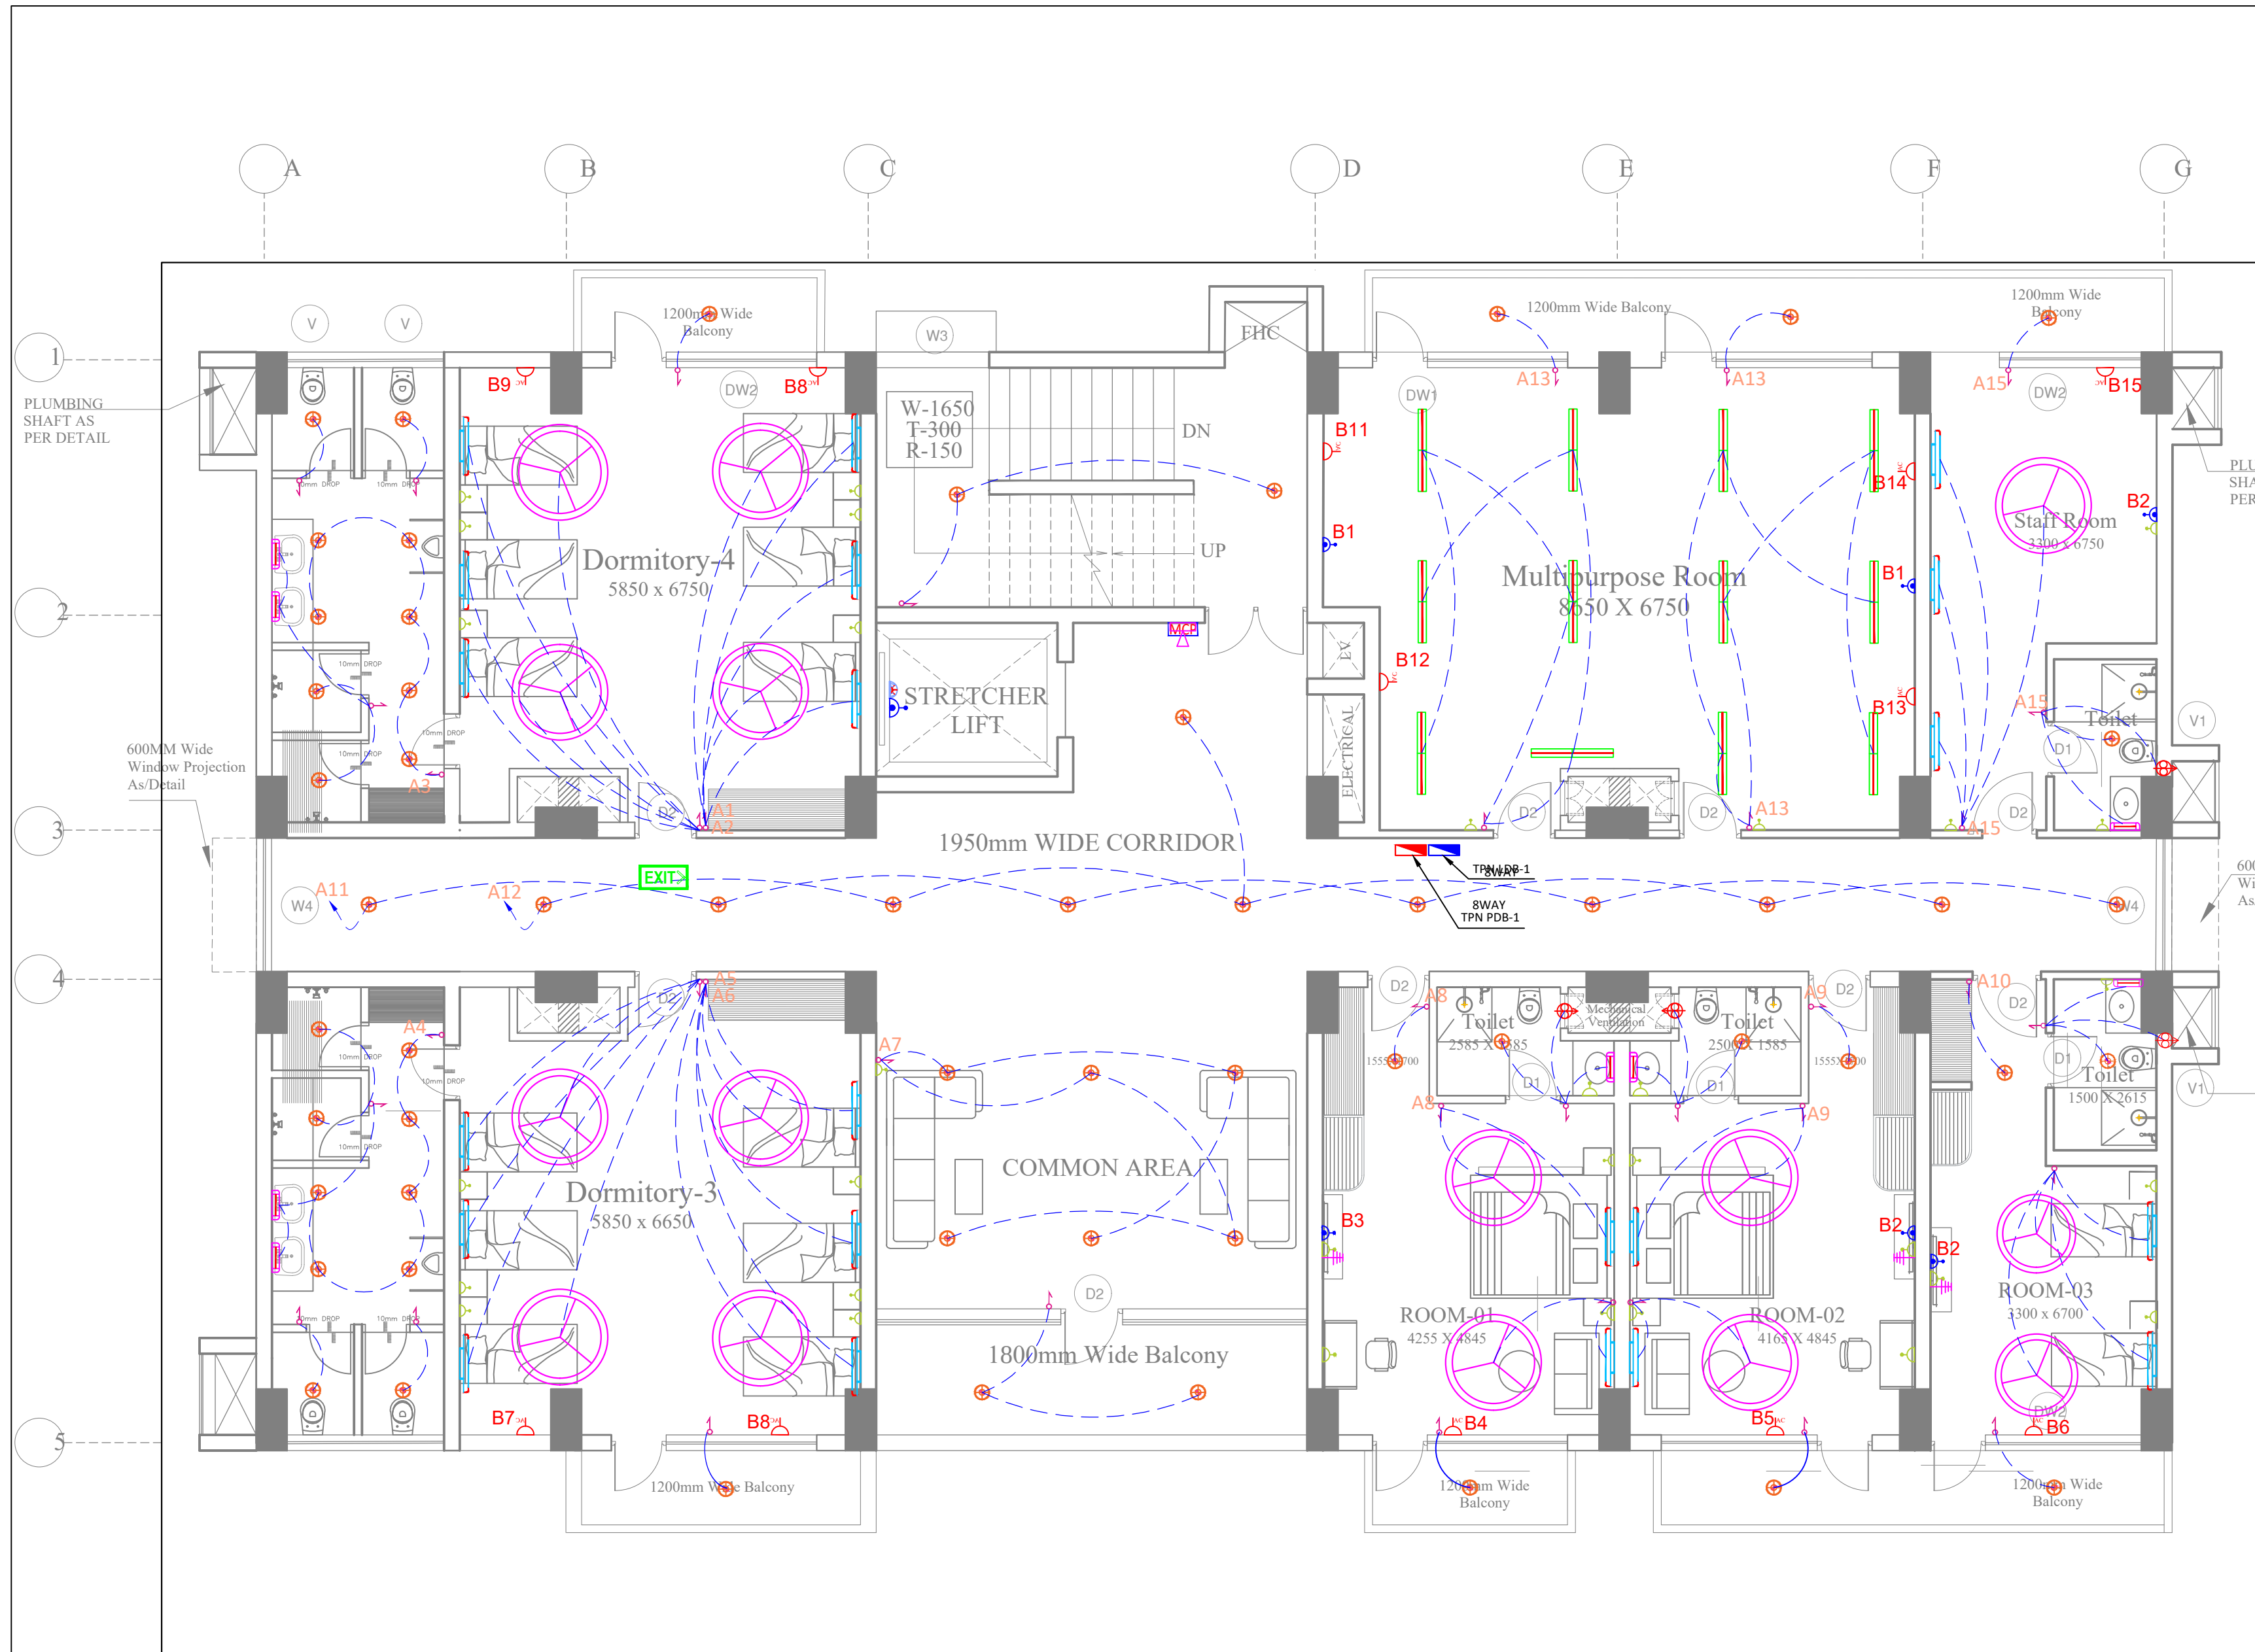

LEGEND :-			
S. No.	SYMBOL	DESCRIPTION	POSITION HEIGHT
1.		6A ONE WAY SWITCH BOARD	AS PER CPWD
2.		1400 MMØ CEILING FAN	CEILING
3.		36W WALL MOUNTED LIGHT	AS PER CPWD
4.		12W LED CEILING LIGHT	CEILING
5.		10W LED MIRROR LIGHT	AS PER CPWD
6.		6A SWITCH SOCKET OUTLET	AS PER CPWD
7.		EXHAUST FAN	AS PER CPWD
8.		16A SWITCH SOCKET OUTLET	AS PER CPWD
9.		25A SOCKET FOR AC	AS PER CPWD
10.		TV POINT	AS PER CPWD
11.		LOOPING	AS PER CPWD
12.		12W BULK HEAD LIGHT	AS PER CPWD
13.		36 W LED SURFACE MOUNTED TUBE LIGHT	AS PER CPWD
14.		DISTRIBUTION BOARD POWER	AS PER CPWD
15.		DISTRIBUTION BOARD LIGHT	AS PER CPWD

- NOTES:-
1. ALL DIMENSIONS ARE IN MM; UNLESS NOTED OTHERWISE.
 2. WRITTEN DIMENSIONS ARE TO BE FOLLOWED. DRAWINGS ARE NOT TO BE SCALED.
 3. ANY DISCREPANCY IN THE DRAWING SHALL BE BROUGHT TO THE NOTICE OF THE ENGINEER-IN-CHARGE.
 4. THIS DRAWING SHALL BE READ IN CONJUNCTION WITH OTHER RELEVANT DRAWINGS.
 5. ALL ELECTRICAL WORKS SHALL BE COMPLETED AS PER CPWD SPECIFICATIONS, RELEVANT IS CODE & REGULATION OF THE ELECTRICAL AUTHORITIES' ETC. AS REQUIRED.
 6. EPC CONTRACTOR TO SUBMIT SHOP DRAWINGS FOR APPROVAL BEFORE EXECUTION OF WORK.
 7. DISCREPANCY, IF ANY SHALL BE BROUGHT TO THE NOTICE OF ENGINEER-IN-CHARGE, AND CLARIFICATION OBTAINED IN WRITING PRIOR TO EXECUTION OF THE WORK.

TENDER DRAWING		
CLIENT		
OIL INDIA LIMITED (A Govt. of India Enterprise)		
CONSULTANT		
RITES THE INFRASTRUCTURE PEOPLE (A Govt. of India Enterprise)		
MEP CONSULTANT		
PKV CONSULTING ENGINEERS (P) LTD.		
815 - C DDA FLATS EAST OF LONI ROAD DELHI - 110093 email:-info@pkv.co.in		
JOB TITLE		
BQ WORKMEN GROUP HOUSING COMPLEX AT DULIAJAN ASSAM.		
DRAWING TITLE		
GUEST HOUSE, FIRST FLOOR LIGHTING & POWER LAYOUT		
SCALE DATE DRG. NO.		
NTS	JULY 2025	MITES/BLD/EL/TEN/212

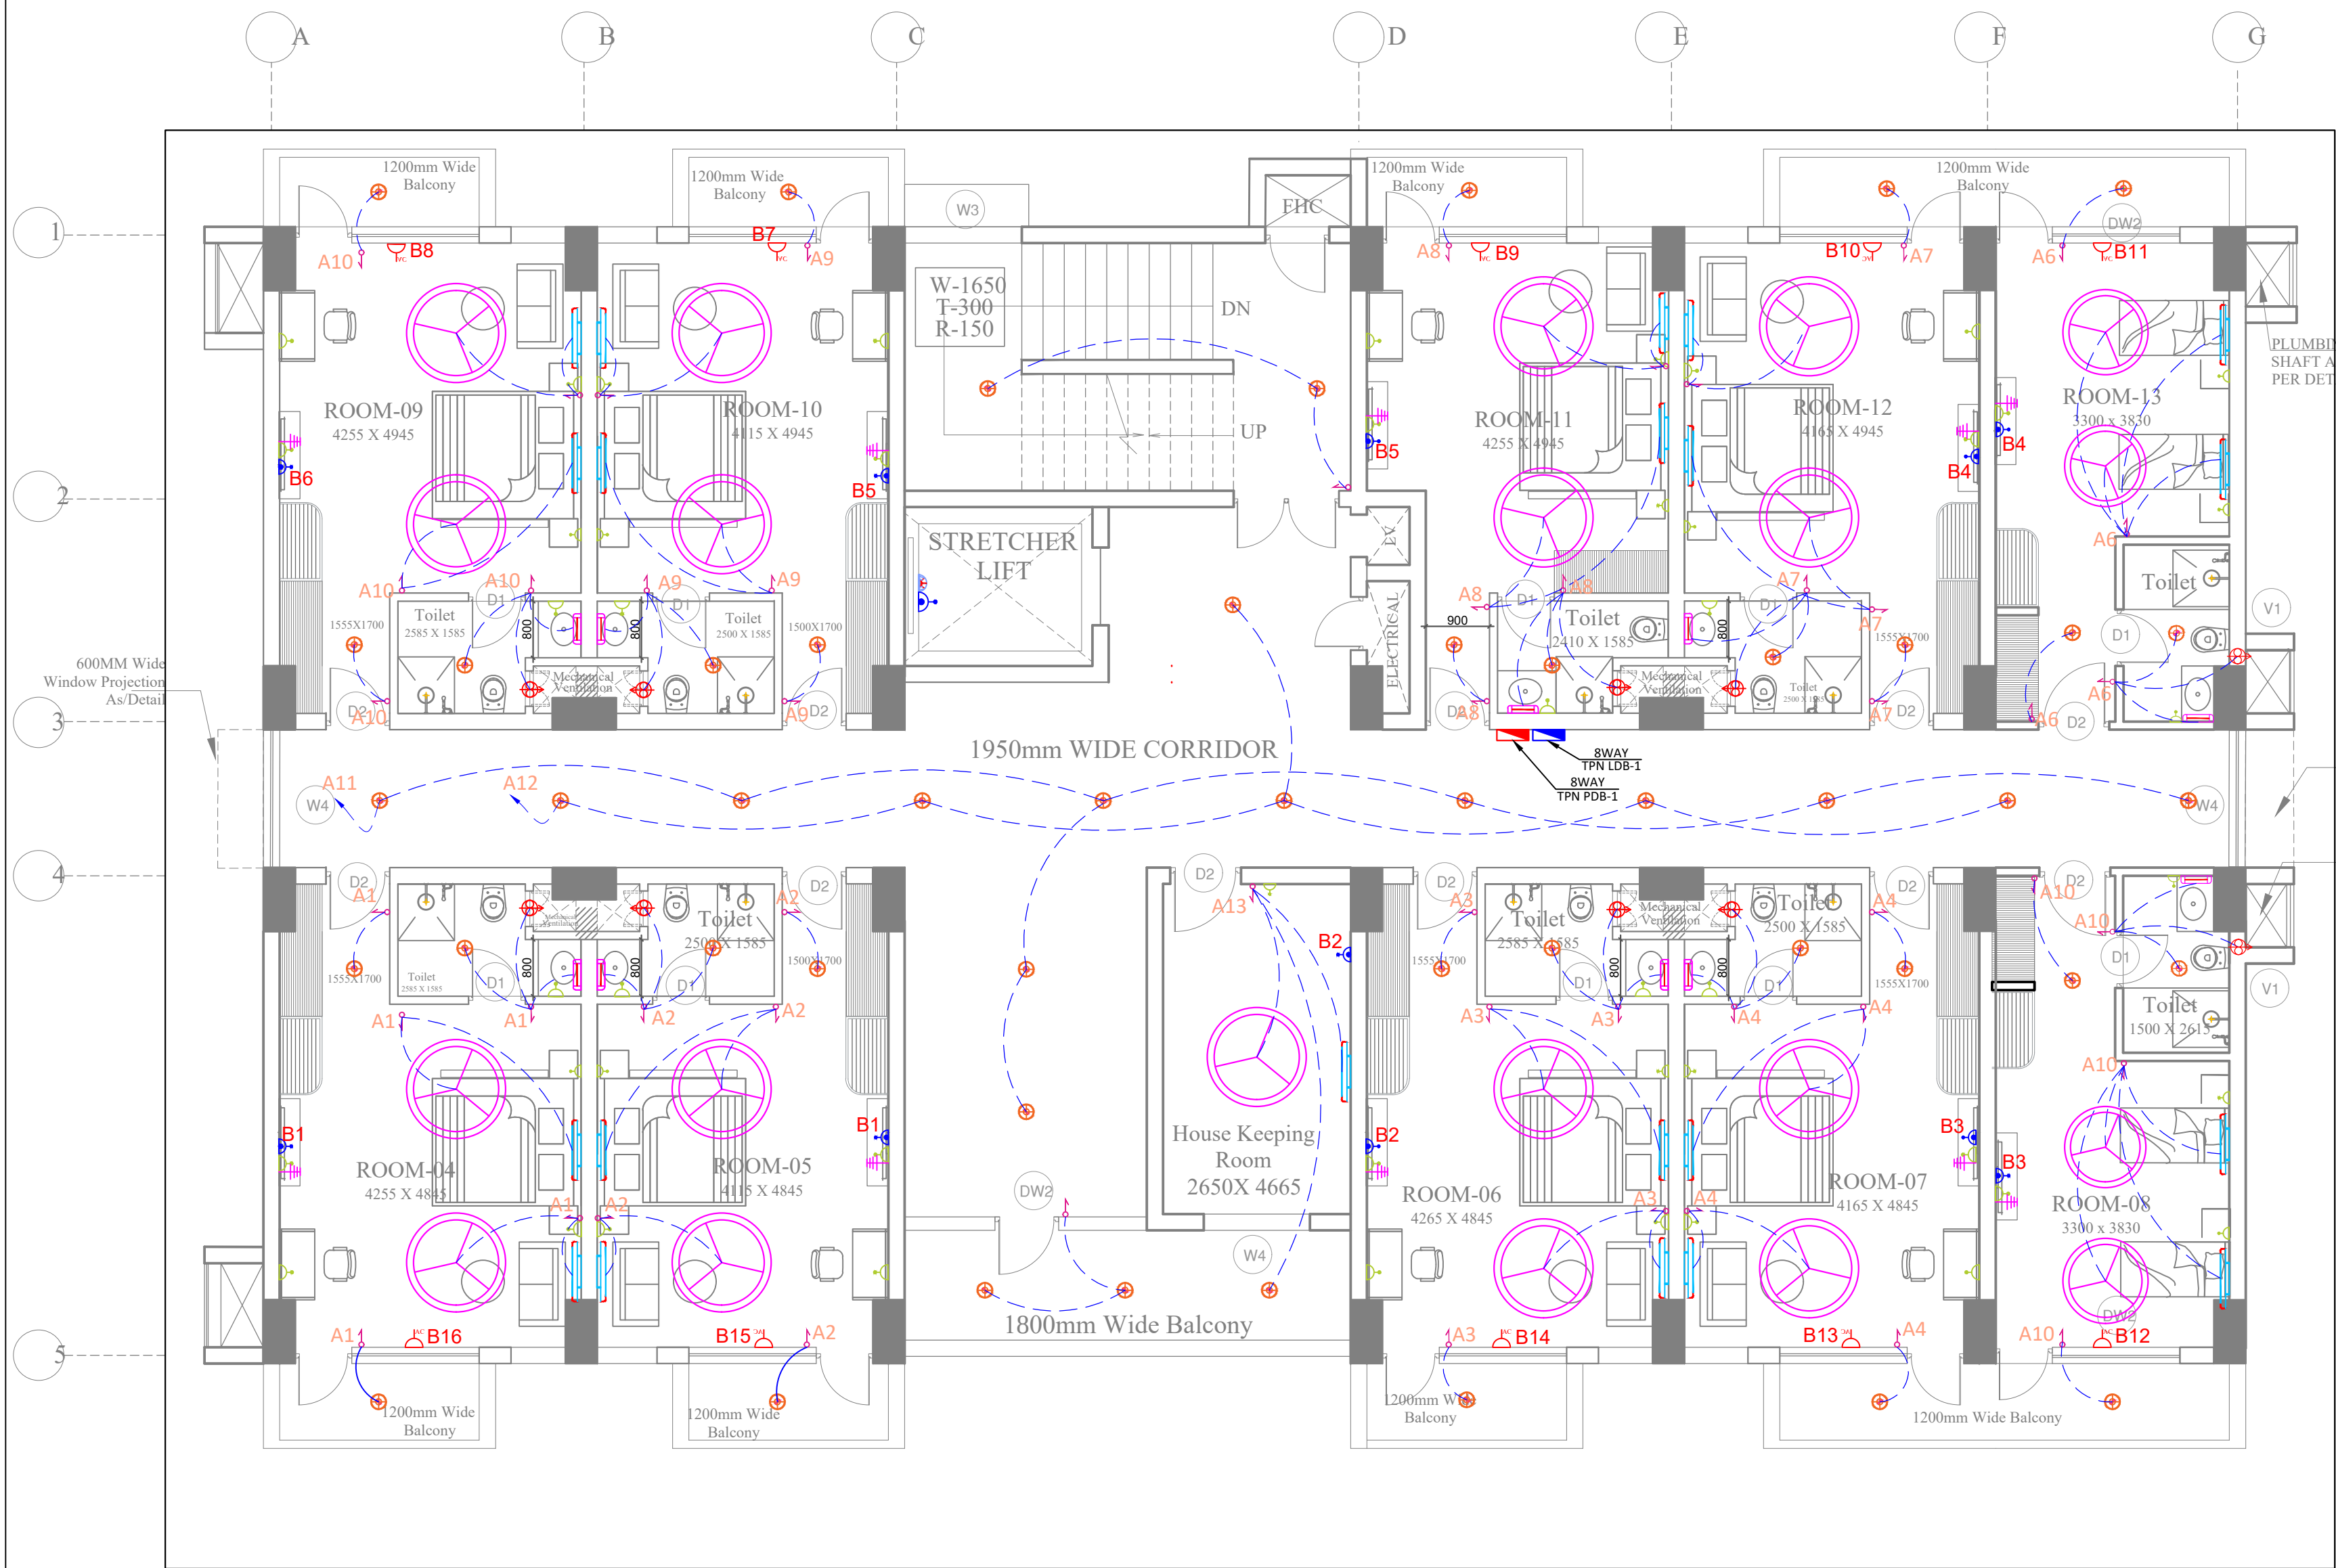

LEGEND :-			
S No.	SYMBOL	DESCRIPTION	POSITION HEIGHT
1.		6A ONE WAY SWITCH BOARD	AS PER CPWD
2.		1400 MMØ CEILING FAN	CEILING
3.		36W WALL MOUNTED LIGHT	AS PER CPWD
4.		12W LED CEILING LIGHT	CEILING
5.		10W LED MIRROR LIGHT	AS PER CPWD
6.		6A SWITCH SOCKET OUTLET	AS PER CPWD
7.		EXHAUST FAN	AS PER CPWD
8.		16A SWITCH SOCKET OUTLET	AS PER CPWD
9.		25A SOCKET FOR AC	AS PER CPWD
10.		TV POINT	AS PER CPWD
11.		LOOPING	AS PER CPWD
12.		12W BULK HEAD LIGHT	AS PER CPWD
13.		36 W LED SURFACE MOUNTED TUBE LIGHT	AS PER CPWD
14.		DISTRIBUTION BOARD POWER	AS PER CPWD
15.		DISTRIBUTION BOARD LIGHT	AS PER CPWD

- NOTES:-
1. ALL DIMENSIONS ARE IN MM; UNLESS NOTED OTHERWISE.
 2. WRITTEN DIMENSIONS ARE TO BE FOLLOWED. DRAWINGS ARE NOT TO BE SCALED.
 3. ANY DISCREPANCY IN THE DRAWING SHALL BE BROUGHT TO THE NOTICE OF THE ENGINEER-IN-CHARGE.
 4. THIS DRAWING SHALL BE READ IN CONJUNCTION WITH OTHER RELEVANT DRAWINGS.
 5. ALL ELECTRICAL WORKS SHALL BE COMPLETED AS PER CPWD SPECIFICATIONS, RELEVANT IS CODE & REGULATION OF THE ELECTRICAL AUTHORITIES' ETC. AS REQUIRED.
 6. EPC CONTRACTOR TO SUBMIT SHOP DRAWINGS FOR APPROVAL BEFORE EXECUTION OF WORK.
 7. DISCREPANCY, IF ANY SHALL BE BROUGHT TO THE NOTICE OF ENGINEER-IN-CHARGE, AND CLARIFICATION OBTAINED IN WRITING PRIOR TO EXECUTION OF THE WORK.

TENDER DRAWING

CLIENT

OIL INDIA LIMITED
(A Govt. of India Enterprise)

CONSULTANT

MITES
THE INFRASTRUCTURE PEOPLE
(A Govt. of India Enterprise)

MEP CONSULTANT

PKV CONSULTING ENGINEERS (P) LTD.

815 - C DDA FLATS
EAST OF LONI ROAD DELHI - 110093
email:-info@pkv.co.in

JOB TITLE

**BQ WORKMEN GROUP HOUSING
COMPLEX AT DULIAJAN ASSAM.**

DRAWING TITLE

**GUEST HOUSE, SECOND AND THIRD
FLOOR LIGHTING & POWER LAYOUT**

SCALE


DATE

DRG. NO.

NTS

JULY 2025


MITES/BLD/EL/TEN/213

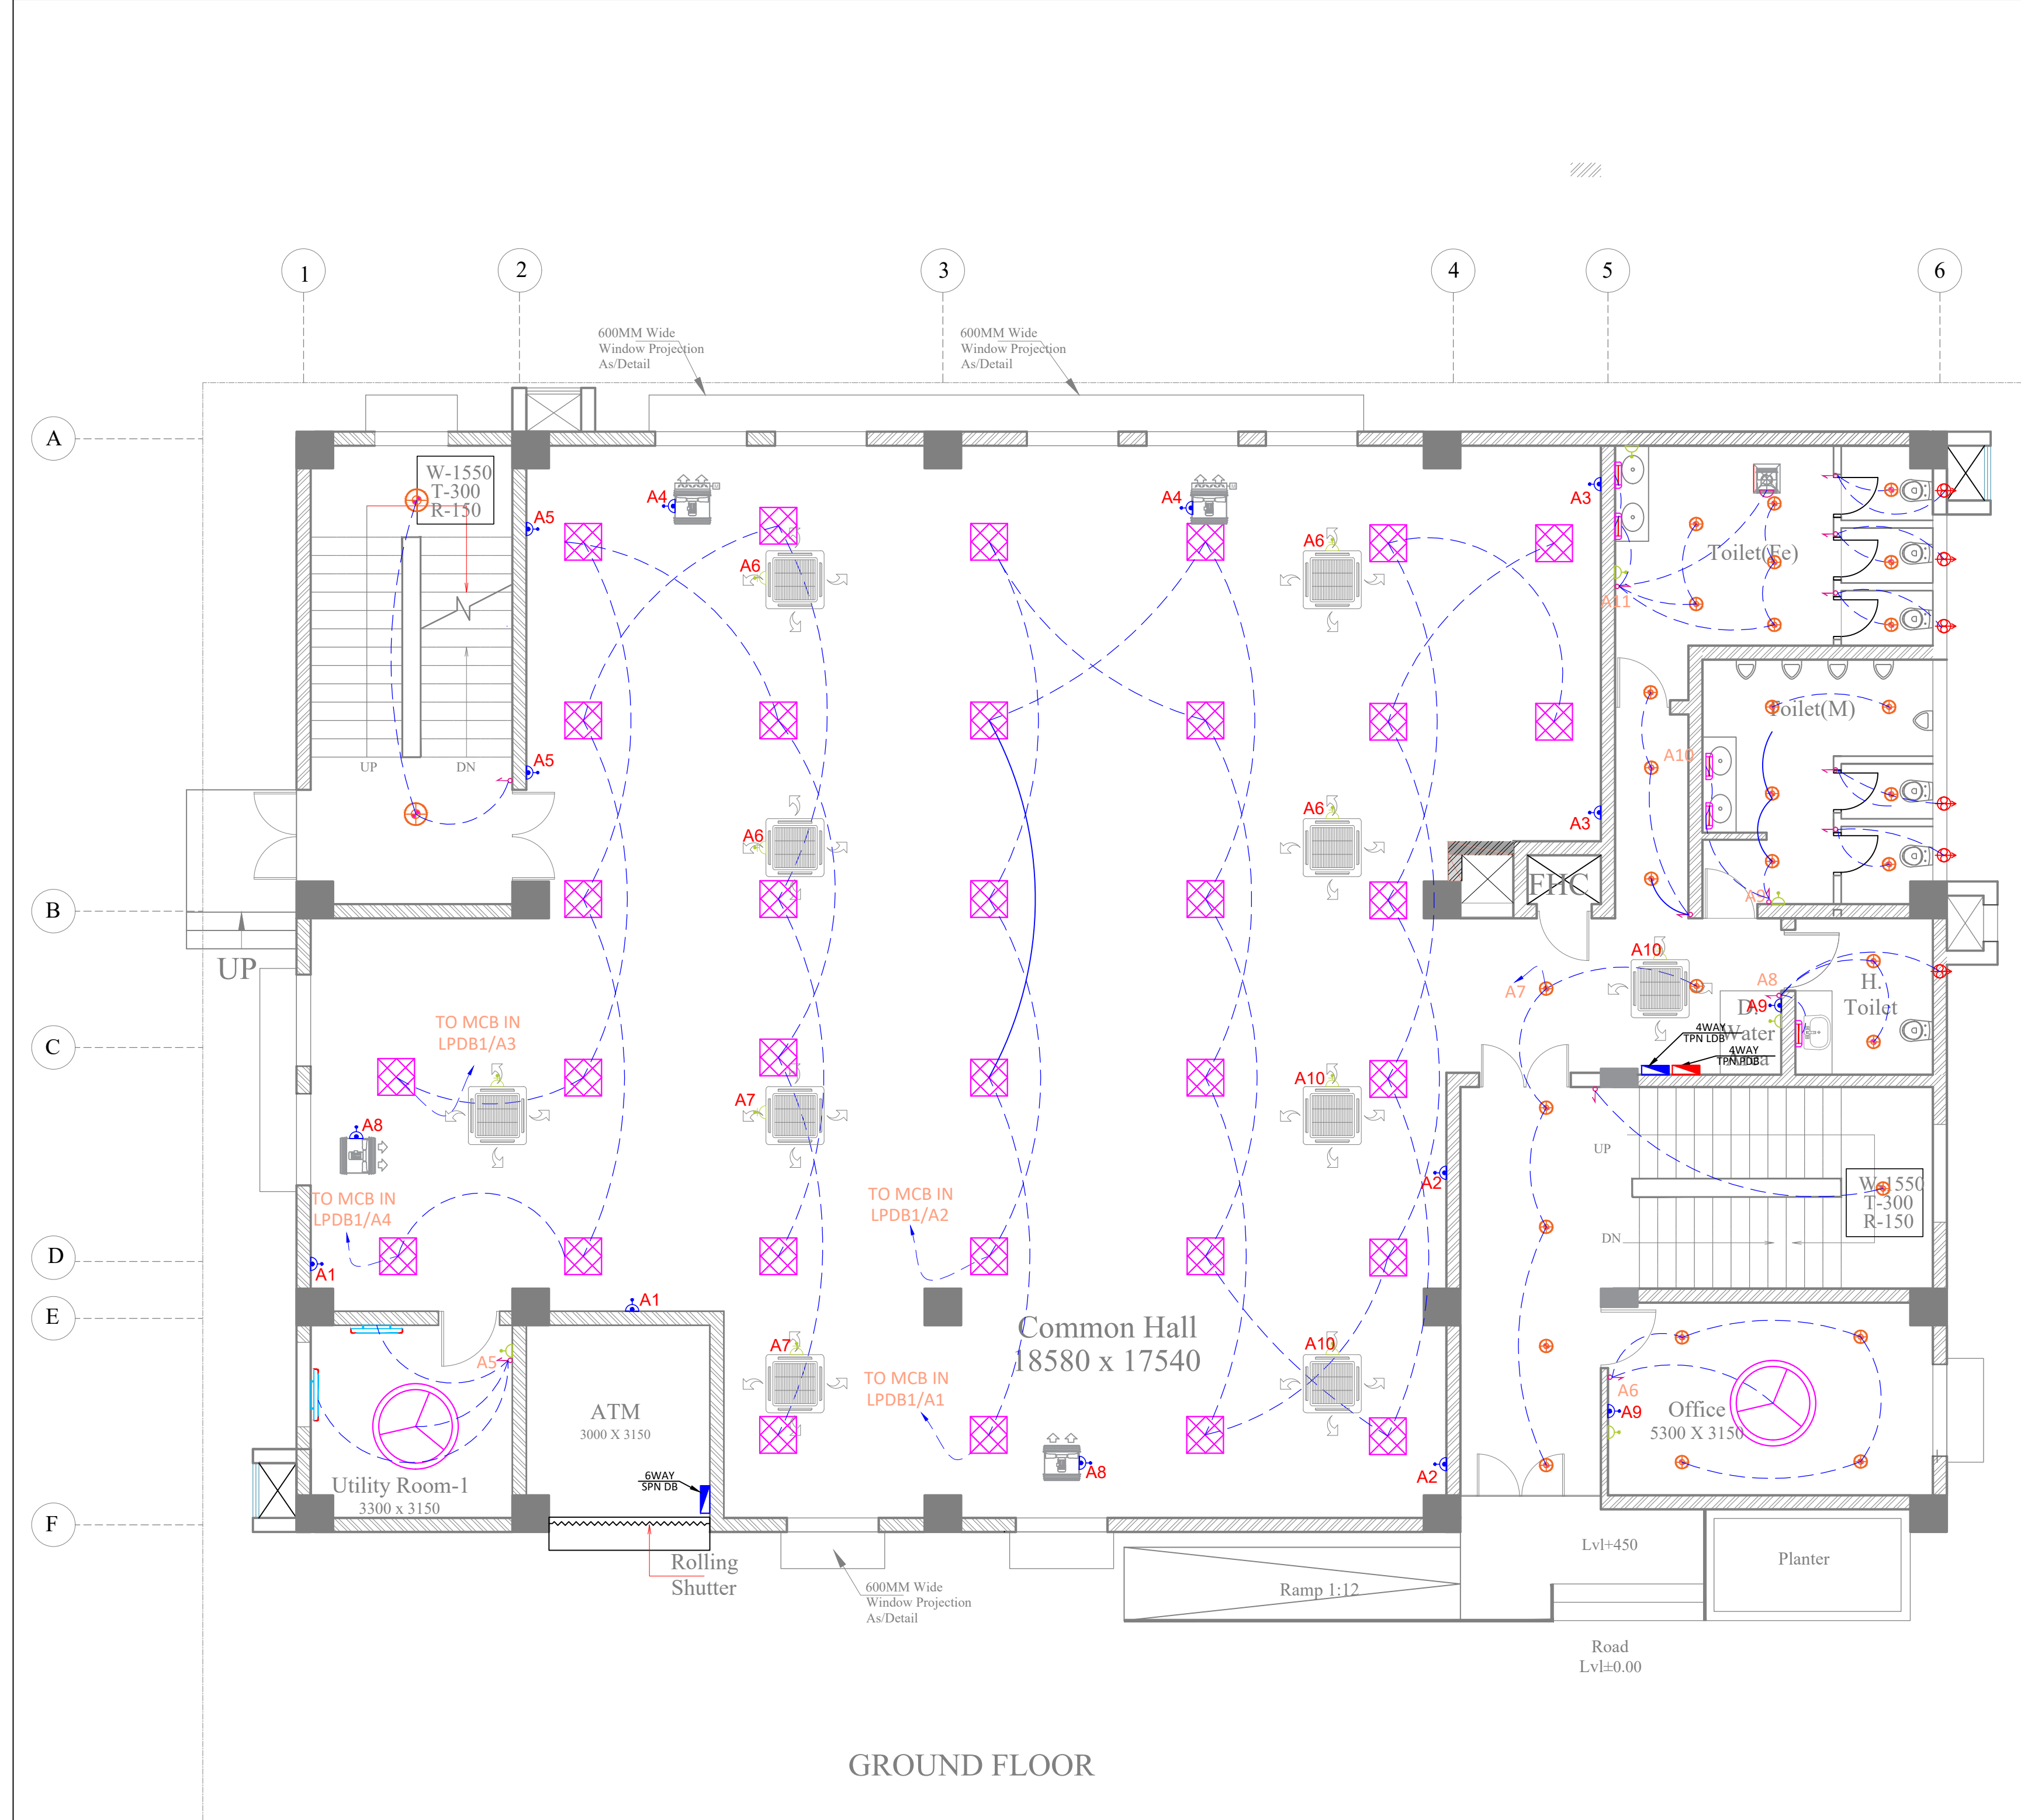

LEGEND :-			
S. No.	SYMBOL	DESCRIPTION	POSITION HEIGHT
1.		6A ONE WAY SWITCH BOARD	AS PER CPWD
2.		1400 MMØ CEILING FAN	CEILING
3.		36W WALL MOUNTED LIGHT	AS PER CPWD
4.		12W WALL BRACKET LIGHT	AS PER CPWD
5.		12W LED CEILING LIGHT	CEILING
6.		10W LED MIRROR LIGHT	AS PER CPWD
7.		BELL PUSH	AS PER CPWD
8.		BELL BUZZER	AS PER CPWD
9.		6A SWITCH SOCKET OUTLET	AS PER CPWD
10.		6A EXHAUST SOCKET CEILING ROSE	CEILING
11.		EXHAUST FAN	AS PER CPWD
12.		16A SWITCH SOCKET OUTLET	AS PER CPWD
13.		25A SOCKET FOR AC	AS PER CPWD
14.		LOOPING	AS PER CPWD
15.		12W BULK HEAD LIGHT	AS PER CPWD
16.		36 W LED SURFACE MOUNTED TUBE LIGHT	AS PER CPWD
17.		36 W LED SURFACE CEILING TUBE LIGHT	AS PER CPWD
18.		DISTRIBUTION BOARD LIGHT	AS PER CPWD
19.		2NO 6A SWITCH & SOCKET	AS PER CPWD

- NOTES:-
1. ALL DIMENSIONS ARE IN MM; UNLESS NOTED OTHERWISE.
 2. WRITTEN DIMENSIONS ARE TO BE FOLLOWED. DRAWINGS ARE NOT TO BE SCALED.
 3. ANY DISCREPANCY IN THE DRAWING SHALL BE BROUGHT TO THE NOTICE OF THE ENGINEER-IN-CHARGE.
 4. THIS DRAWING SHALL BE READ IN CONJUNCTION WITH OTHER RELEVANT DRAWINGS.
 5. ALL ELECTRICAL WORKS SHALL BE COMPLETED AS PER CPWD SPECIFICATIONS, RELEVANT IS CODE & REGULATION OF THE ELECTRICAL AUTHORITIES ETC. AS REQUIRED.
 6. EPC CONTRACTOR TO SUBMIT SHOP DRAWINGS FOR APPROVAL BEFORE EXECUTION OF WORK.
 7. DISCREPANCY, IF ANY SHALL BE BROUGHT TO THE NOTICE OF ENGINEER-IN-CHARGE AND CLARIFICATION OBTAINED IN WRITING PRIOR TO EXECUTION OF THE WORK.

TENDER DRAWING		
CLIENT		
OIL INDIA LIMITED (A Govt. of India Enterprise)		
CONSULTANT		
RITES THE INFRASTRUCTURE PEOPLE (A Govt. of India Enterprise)		
MEP CONSULTANT		
PKV CONSULTING ENGINEERS (P) LTD.		
815 - C DDA FLATS EAST OF LONI ROAD DELHI - 110093 email: -info@pkv.co.in		
JOB TITLE		
BQ WORKMEN GROUP HOUSING COMPLEX AT DULIAJAN ASSAM.		
DRAWING TITLE		
COMMUNITY CENTRE GROUND FLOOR LIGHTING & POWER LAYOUT		
SCALE	DATE	DRG. NO.
NTS	JULY 2025	RITES/BLD/EL/TEN/214

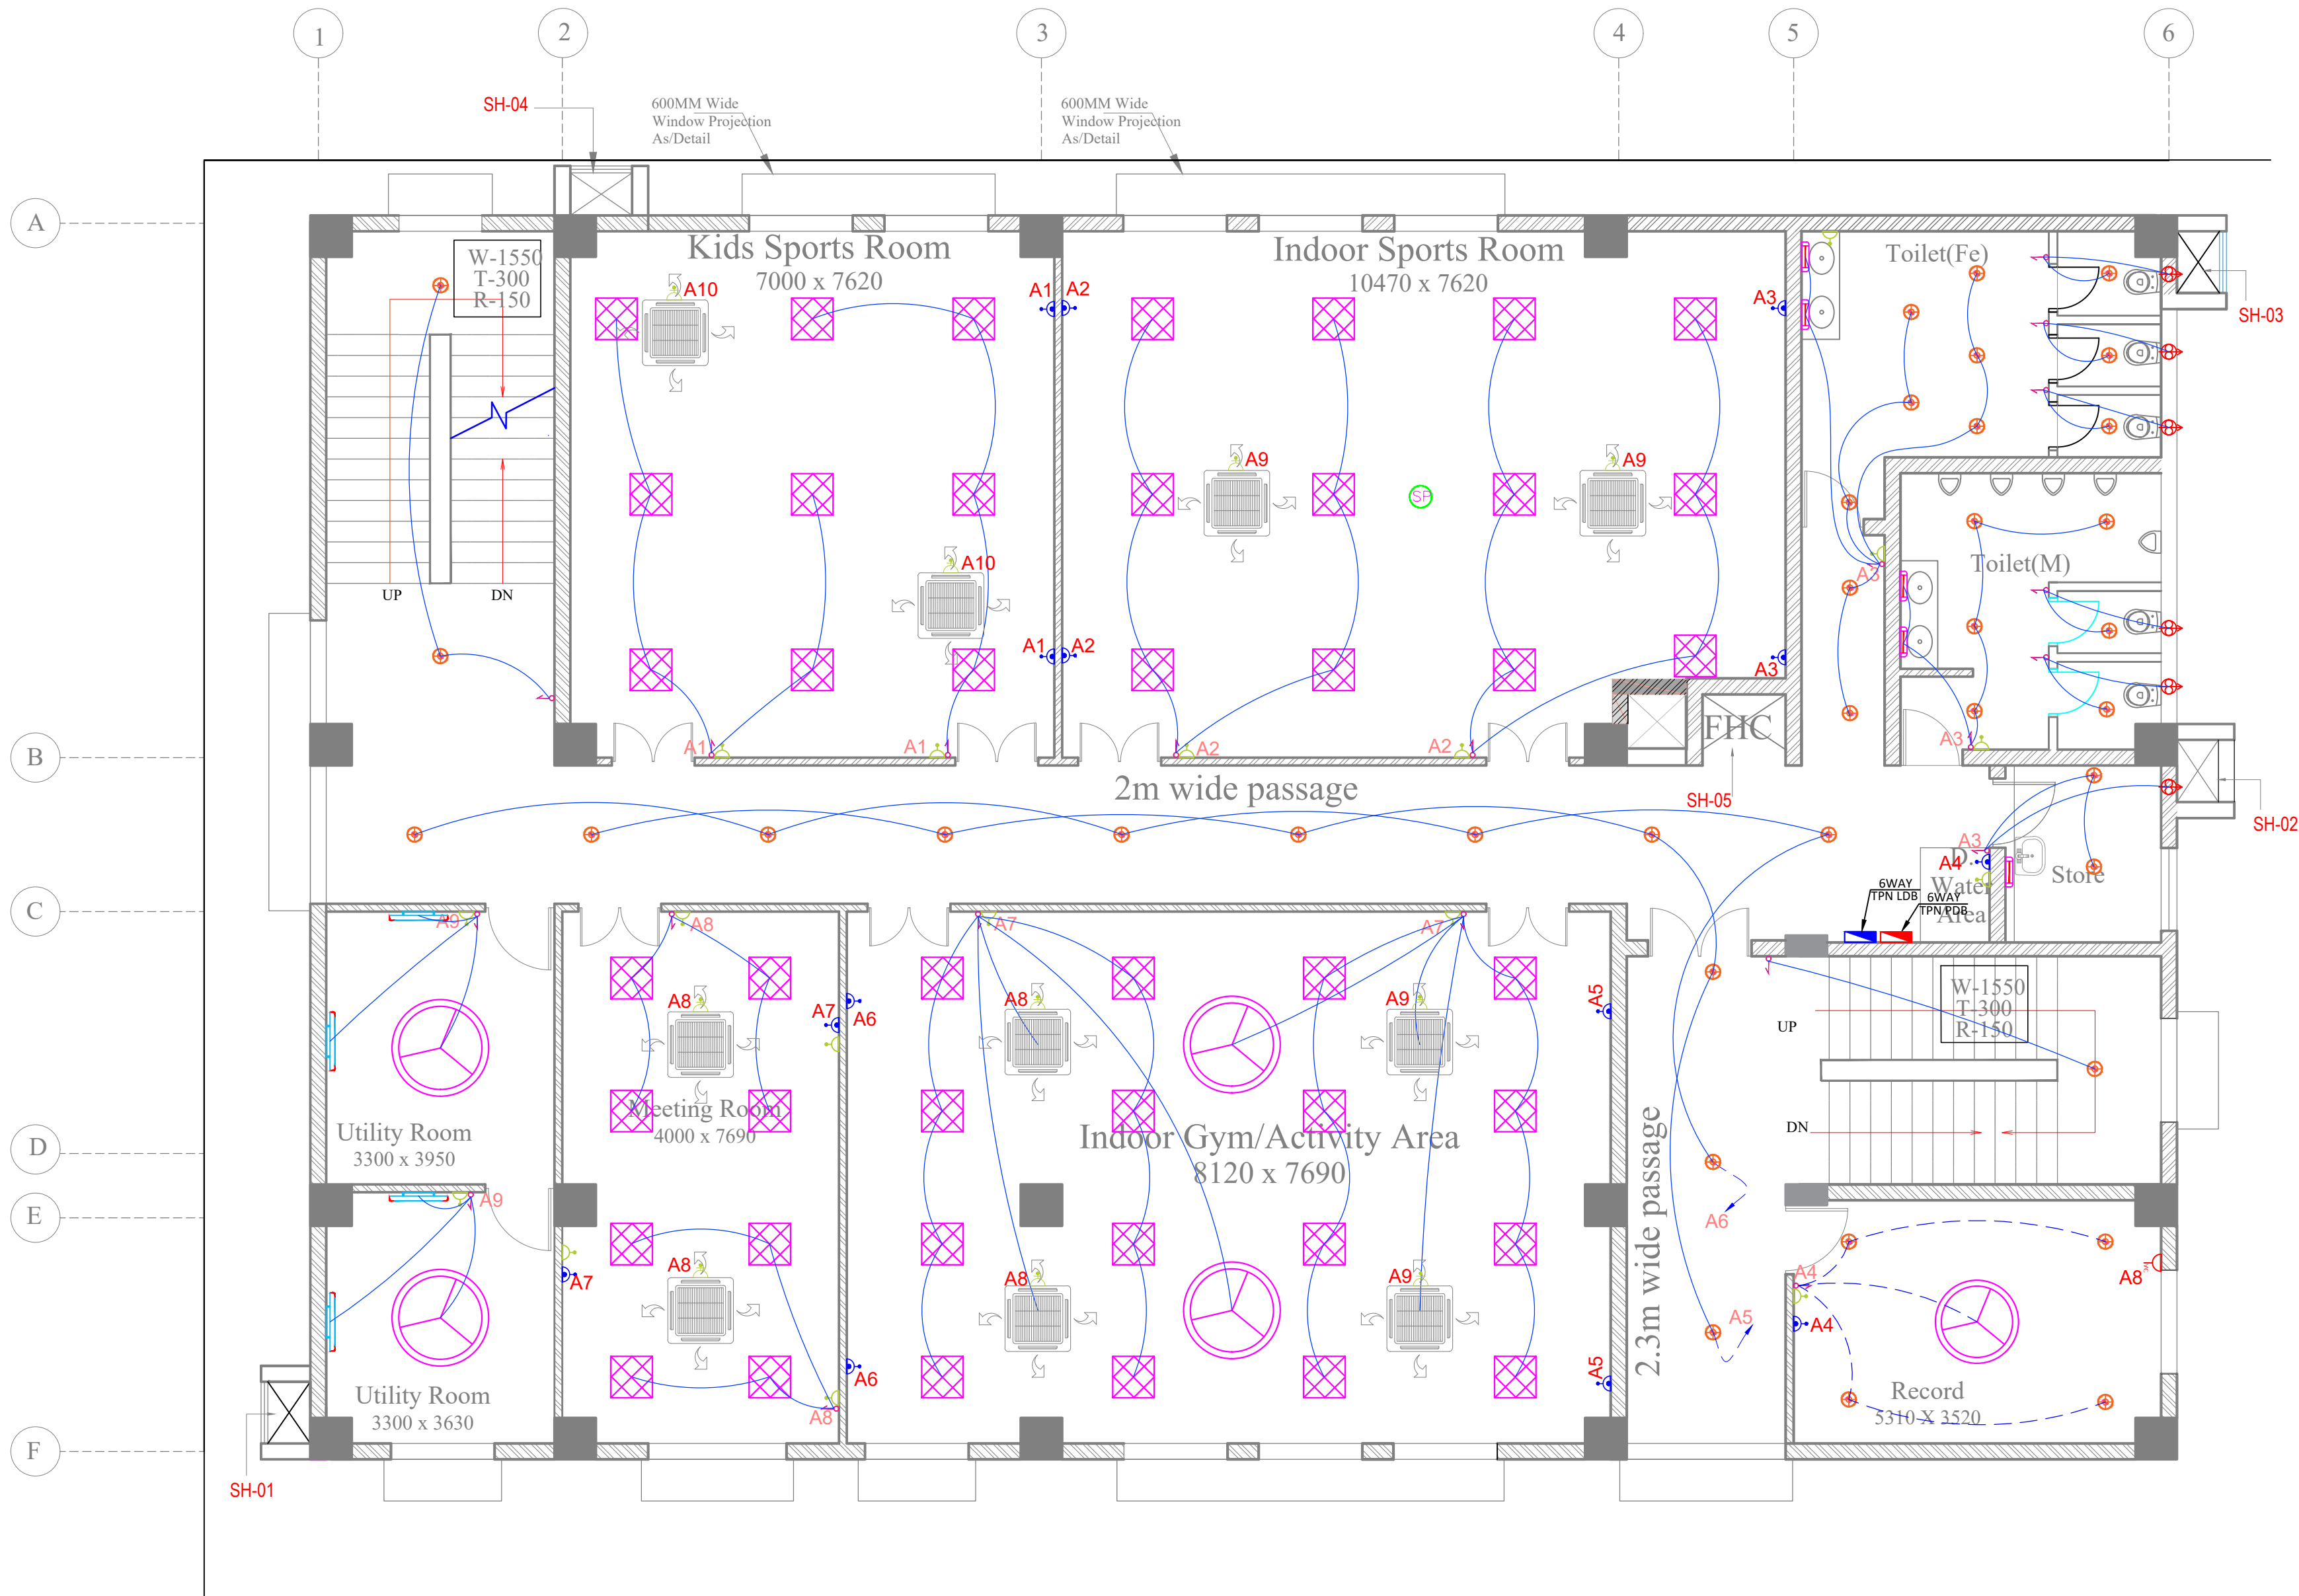

FIRST FLOOR

LEGEND :-			
S. No.	SYMBOL	DESCRIPTION	POSITION HEIGHT
1.		6A ONE WAY SWITCH BOARD	AS PER CPWD
2.		1400 MMØ CEILING FAN	CEILING
3.		36W WALL MOUNTED LIGHT	AS PER CPWD
4.		12W WALL BRACKET LIGHT	AS PER CPWD
5.		12W LED CEILING LIGHT	CEILING
6.		10W LED MIRROR LIGHT	AS PER CPWD
7.		BELL PUSH	AS PER CPWD
8.		BELL BUZZER	AS PER CPWD
9.		6A SWITCH SOCKET OUTLET	AS PER CPWD
10.		6A EXHAUST SOCKET CEILING ROSE	CEILING
11.		EXHAUST FAN	AS PER CPWD
12.		16A SWITCH SOCKET OUTLET	AS PER CPWD
13.		25A SOCKET FOR AC	AS PER CPWD
14.		LOOPING	AS PER CPWD
15.		12W BULK HEAD LIGHT	AS PER CPWD
16.		36 W LED SURFACE MOUNTED TUBE LIGHT	AS PER CPWD
17.		36 W LED SURFACE CEILING TUBE LIGHT	AS PER CPWD
18.		DISTRIBUTION BOARD LIGHT	AS PER CPWD
19.		2NO 6A SWITCH & SOCKET	AS PER CPWD

- NOTES:-
- ALL DIMENSIONS ARE IN MM; UNLESS NOTED OTHERWISE.
 - WRITTEN DIMENSIONS ARE TO BE FOLLOWED. DRAWINGS ARE NOT TO BE SCALED.
 - ANY DISCREPANCY IN THE DRAWING SHALL BE BROUGHT TO THE NOTICE OF THE ENGINEER-IN-CHARGE.
 - THIS DRAWING SHALL BE READ IN CONJUNCTION WITH OTHER RELEVANT DRAWINGS.
 - ALL ELECTRICAL WORKS SHALL BE COMPLETED AS PER CPWD SPECIFICATIONS, RELEVANT IS CODE & REGULATION OF THE ELECTRICAL AUTHORITIES ETC. AS REQUIRED.
 - EPC CONTRACTOR TO SUBMIT SHOP DRAWINGS FOR APPROVAL BEFORE EXECUTION OF WORK.
 - DISCREPANCY, IF ANY SHALL BE BROUGHT TO THE NOTICE OF ENGINEER-IN-CHARGE AND CLARIFICATION OBTAINED IN WRITING PRIOR TO EXECUTION OF THE WORK.

TENDER DRAWING		
CLIENT	 OIL INDIA LIMITED <i>(A Govt. of India Enterprise)</i>	
CONSULTANT	 RITES THE INFRASTRUCTURE PEOPLE <i>(A Govt. of India Enterprise)</i>	
MEP CONSULTANT	 PKV CONSULTING ENGINEERS (P) LTD. 815 - C DDA FLATS EAST OF LONI ROAD DELHI - 110093 email:-info@pkv.co.in	
JOB TITLE	BQ WORKMEN GROUP HOUSING COMPLEX AT DULIAJAN ASSAM.	
DRAWING TITLE	COMMUNITY CENTRE FIRST FLOOR LIGHTING & POWER LAYOUT	
SCALE	DATE	DRG. NO.
NTS	JULY 2025	RITES/BLD/EL/TEN/215

LEGENDS:-

	DATA OUTLET
	VOICE OUTLET
	DOME CAMERA
	PA CEILING SPEAKER
	MANUAL CALL POINT
	HOOTER
	CONTEROL MODULE
	TALK BACK JACK

LEGEND		
SL.NO	SYMBOL	DESCRIPTION
01		SMOKE DETECTOR
02		HEAT DETECTOR

NOTES:-

1. ALL DIMENSIONS ARE IN MM; UNLESS NOTED OTHERWISE.
2. WRITTEN DIMENSIONS ARE TO BE FOLLOWED. DRAWINGS ARE NOT TO BE SCALED.
3. ANY DISCREPANCY IN THE DRAWING SHALL BE BROUGHT TO THE NOTICE OF THE ENGINEER-IN-CHARGE.
4. THIS DRAWING SHALL BE READ IN CONJUNCTION WITH OTHER RELEVANT DRAWINGS.
5. ALL ELECTRICAL WORKS SHALL BE COMPLETED AS PER CPWD SPECIFICATIONS, RELEVANT IS CODE & REGULATION OF THE ELECTRICAL AUTHORITIES' ETC. AS REQUIRED.
6. EPC CONTRACTOR TO SUBMIT SHOP DRAWINGS FOR APPROVAL BEFORE EXECUTION OF WORK.
7. DISCREPANCY, IF ANY SHALL BE BROUGHT TO THE NOTICE OF ENGINEER-IN-CHARGE, AND CLARIFICATION OBTAINED IN WRITING PRIOR TO EXECUTION OF THE WORK.

TENDER DRAWING

CLIENT
 OIL INDIA LIMITED
(A Govt. of India Enterprise)


CONSULTANT
 RITES
THE INFRASTRUCTURE PEOPLE
(A Govt. of India Enterprise)

MEP CONSULTANT
PKV CONSULTING ENGINEERS (P) LTD.
 815 - C DDA FLATS
EAST OF LONI ROAD DELHI - 110093
email:-info@pkv.co.in

JOB TITLE
**BQ WORKMEN GROUP HOUSING
COMPLEX AT DULIAJAN ASSAM**

DRAWING TITLE
**GUEST HOUSE GROUND FLOOR CCTV
& PA SYSTEM FIRE ALARM LAYOUT**

SCALE	DATE	DRG. NO.
NTS	JULY 2025	RITES/BLD/EL/TEN/216

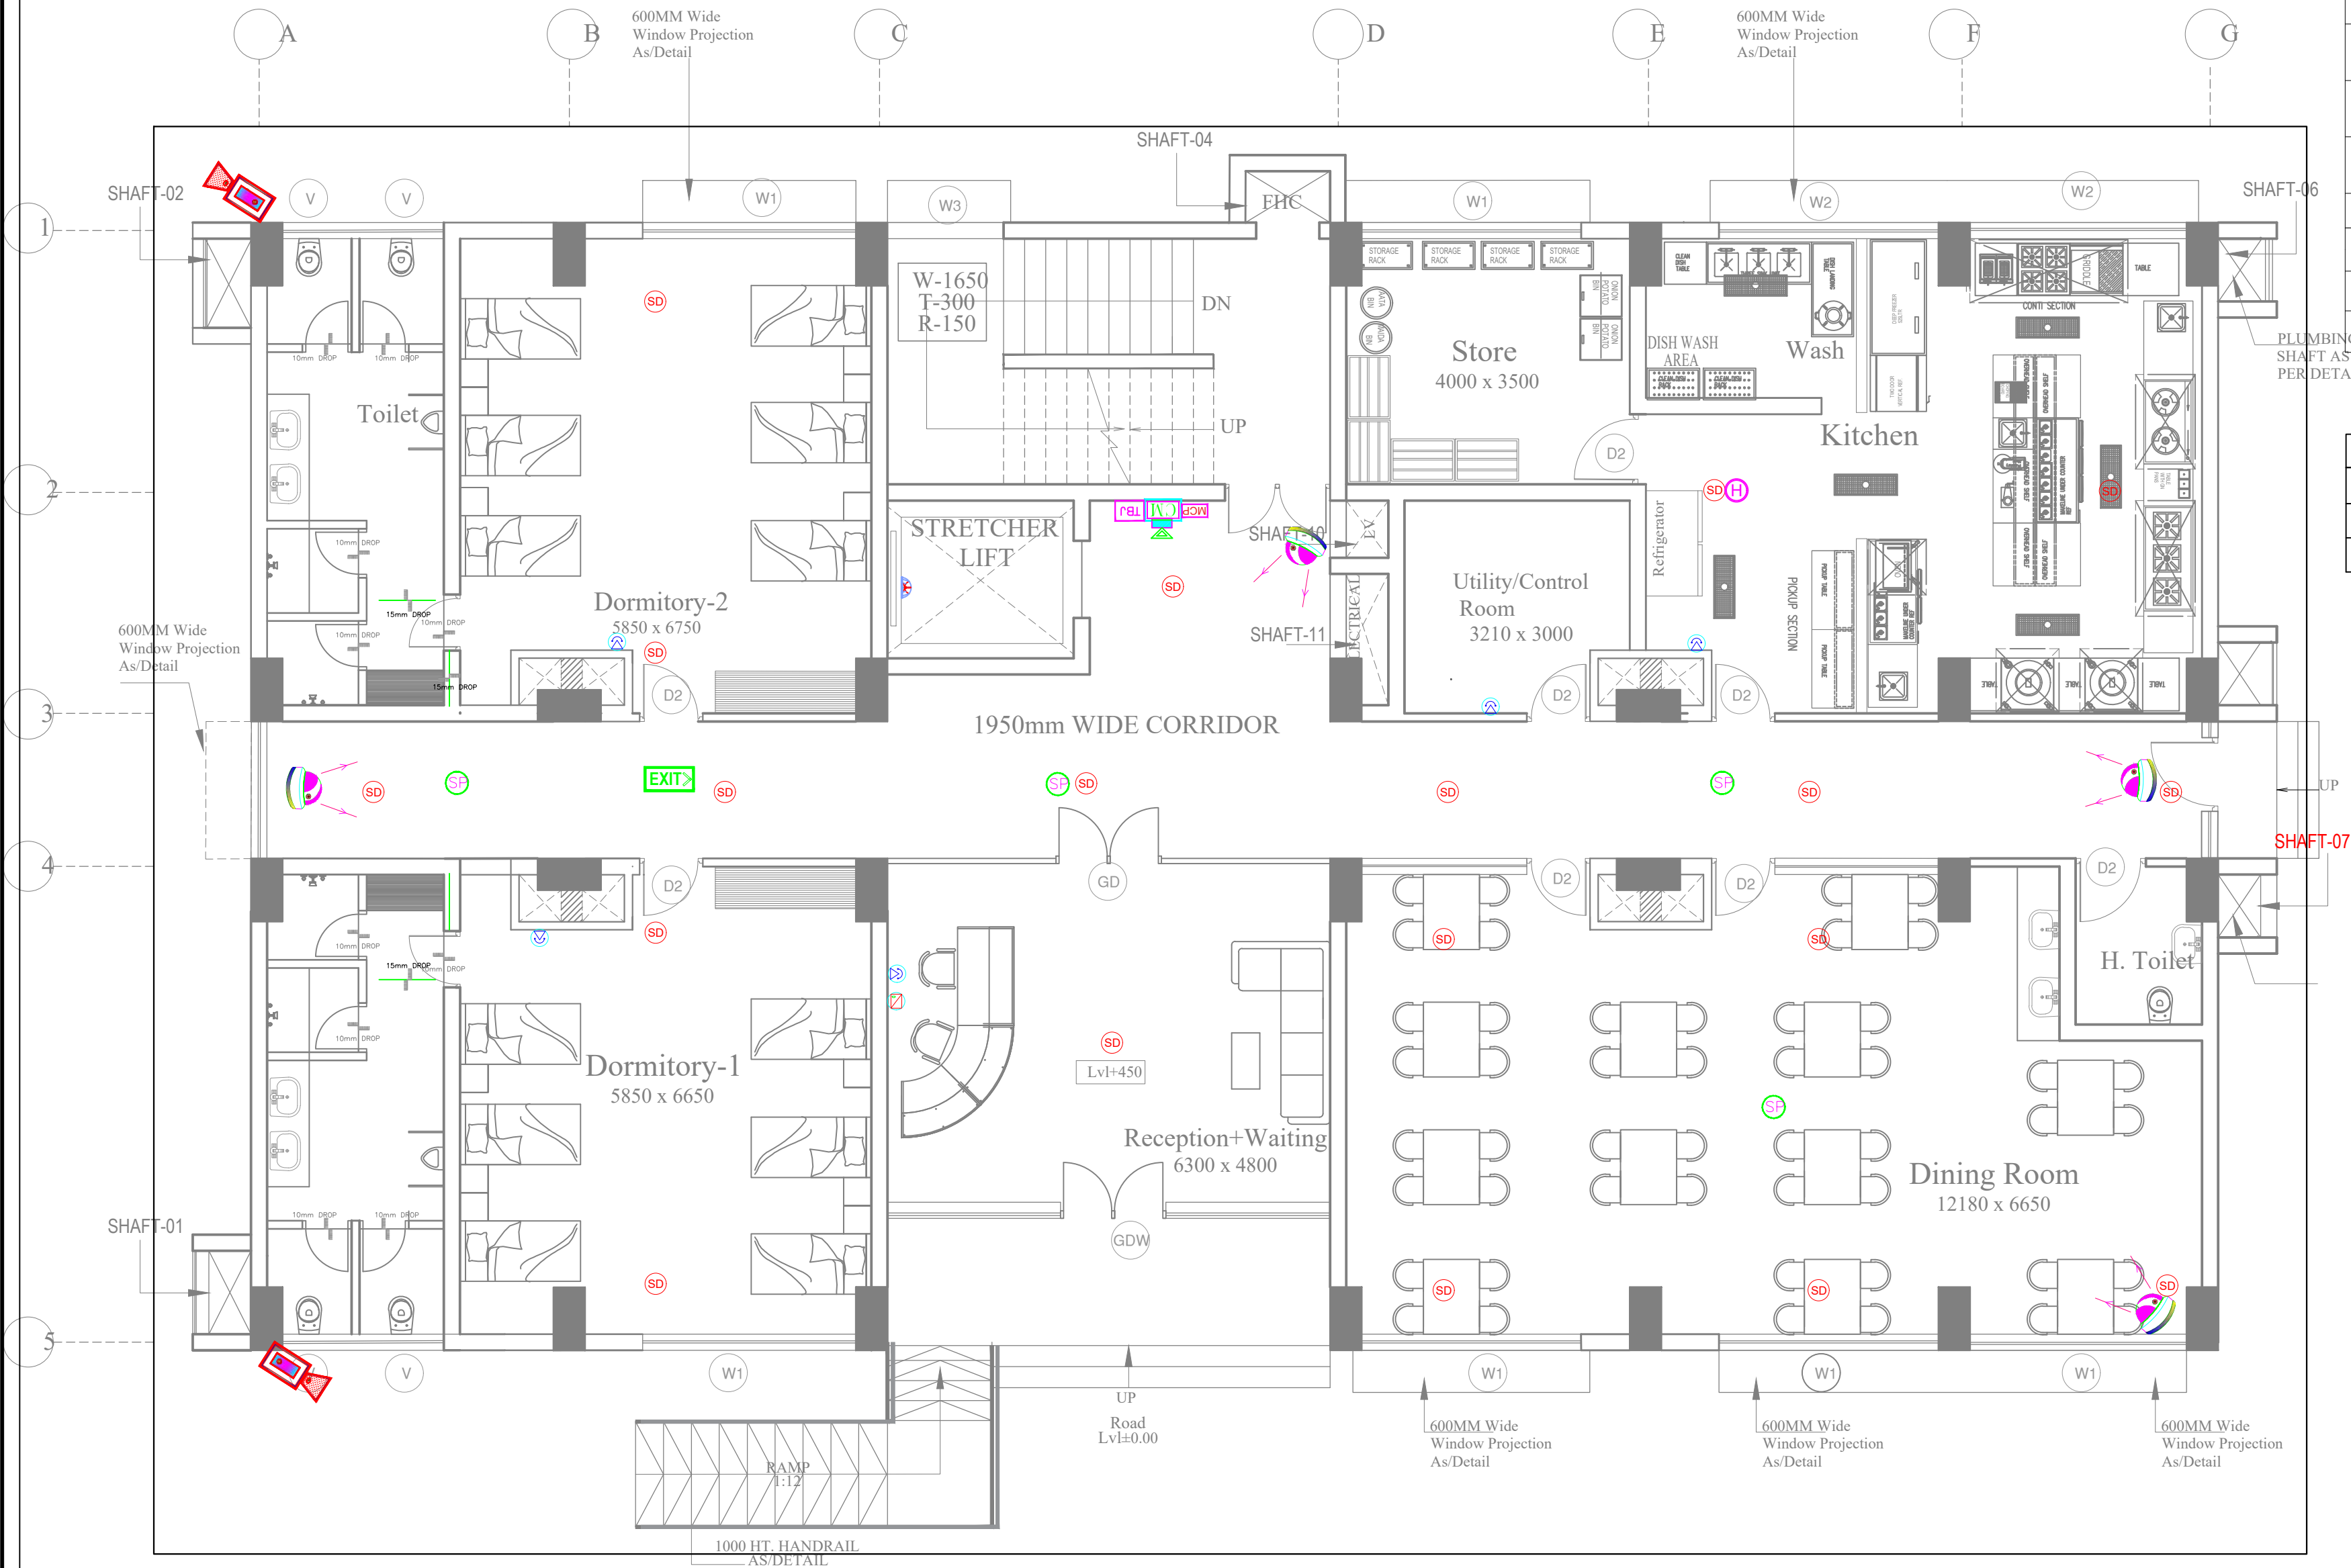

LEGENDS:-

	DATA OUTLET
	VOICE OUTLET
	DOME CAMERA
	PA CEILING SPEAKER
	MANUAL CALL POINT
	HOOTER
	CONTEROL MODULE
	TALK BACK JACK

LEGEND

SL.NO	SYMBOL	DESCRIPTION
01		SMOKE DETECTOR

NOTES:-

1. ALL DIMENSIONS ARE IN MM; UNLESS NOTED OTHERWISE.
2. WRITTEN DIMENSIONS ARE TO BE FOLLOWED. DRAWINGS ARE NOT TO BE SCALED.
3. ANY DISCREPANCY IN THE DRAWING SHALL BE BROUGHT TO THE NOTICE OF THE ENGINEER-IN-CHARGE.
4. THIS DRAWING SHALL BE READ IN CONJUNCTION WITH OTHER RELEVANT DRAWINGS.
5. ALL ELECTRICAL WORKS SHALL BE COMPLETED AS PER CPWD SPECIFICATIONS, RELEVANT IS CODE & REGULATION OF THE ELECTRICAL AUTHORITIES' ETC. AS REQUIRED.
6. EPC CONTRACTOR TO SUBMIT SHOP DRAWINGS FOR APPROVAL BEFORE EXECUTION OF WORK.
7. DISCREPANCY, IF ANY SHALL BE BROUGHT TO THE NOTICE OF ENGINEER-IN-CHARGE, AND CLARIFICATION OBTAINED IN WRITING PRIOR TO EXECUTION OF THE WORK.

TENDER DRAWING

CLIENT

OIL INDIA LIMITED
(A Govt. of India Enterprise)

CONSULTANT

RITES
THE INFRASTRUCTURE PEOPLE
(A Govt. of India Enterprise)

MEP CONSULTANT

PKV CONSULTING ENGINEERS (P) LTD.



815 - C DDA FLATS
EAST OF LONI ROAD DELHI - 110093
email:-info@pkv.co.in

JOB TITLE

**BQ WORKMEN GROUP HOUSING
COMPLEX AT DULIAJAN ASSAM**

DRAWING TITLE

**GUEST HOUSE, FIRST FLOOR CCTV &
PA SYSTEM FIRE ALARM LAYOUT**



SCALE	DATE	DRG. NO.
NTS	JULY 2025	RITES/BLD/EL/TEN/217

LEGENDS:-

	DATA OUTLET
	VOICE OUTLET
	DOME CAMERA
	PA CEILING SPEAKER
	MANUAL CALL POINT
	HOOTER
	CONTEROL MODULE
	TALK BACK JACK

LEGEND		
SL.NO	SYMBOL	DESCRIPTION
01		SMOKE DETECTOR

NOTES:-

1. ALL DIMENSIONS ARE IN MM; UNLESS NOTED OTHERWISE.
2. WRITTEN DIMENSIONS ARE TO BE FOLLOWED. DRAWINGS ARE NOT TO BE SCALED.
3. ANY DISCREPANCY IN THE DRAWING SHALL BE BROUGHT TO THE NOTICE OF THE ENGINEER-IN-CHARGE.
4. THIS DRAWING SHALL BE READ IN CONJUNCTION WITH OTHER RELEVANT DRAWINGS.
5. ALL ELECTRICAL WORKS SHALL BE COMPLETED AS PER CPWD SPECIFICATIONS, RELEVANT IS CODE & REGULATION OF THE ELECTRICAL AUTHORITIES ETC. AS REQUIRED.
6. EPC CONTRACTOR TO SUBMIT SHOP DRAWINGS FOR APPROVAL BEFORE EXECUTION OF WORK.
7. DISCREPANCY, IF ANY SHALL BE BROUGHT TO THE NOTICE OF ENGINEER-IN-CHARGE, AND CLARIFICATION OBTAINED IN WRITING PRIOR TO EXECUTION OF THE WORK.

TENDER DRAWING

CLIENT	 OIL INDIA LIMITED (A Govt. of India Enterprise)		
CONSULTANT	 MITES THE INFRASTRUCTURE PEOPLE (A Govt. of India Enterprise)		
MEP CONSULTANT	PKV CONSULTING ENGINEERS (P) LTD.  815 - C DDA FLATS EAST OF LONI ROAD DELHI - 110093 email:-info@pkv.co.in		
JOB TITLE	BQ WORKMEN GROUP HOUSING COMPLEX AT DULIAJAN ASSAM		
DRAWING TITLE	GUEST HOUSE, SECOND AND THIRD FLOOR CCTV & PA SYSTEM FIRE ALARM LAYOUT		
SCALE	DATE	DRG. NO.	
NTS	JULY 2025	MITES/BLD/EL/TEN/218	



LEGENDS:-

	DATA OUTLET
	VOICE OUTLET
	DOME CAMERA
	BULLET CAMERA
	MOUNTED SPEAKER
	PA CEILING SPEAKER
	MANUAL CALL POINT
	HOOTER
	CONTEROL MODULE
	TALK BACK JACK

NOTES:-

- ALL DIMENSIONS ARE IN MM; UNLESS NOTED OTHERWISE.
- WRITTEN DIMENSIONS ARE TO BE FOLLOWED. DRAWINGS ARE NOT TO BE SCALED.
- ANY DISCREPANCY IN THE DRAWING SHALL BE BROUGHT TO THE NOTICE OF THE ENGINEER-IN-CHARGE.
- THIS DRAWING SHALL BE READ IN CONJUNCTION WITH OTHER RELEVANT DRAWINGS.
- ALL ELECTRICAL WORKS SHALL BE COMPLETED AS PER CPWD SPECIFICATIONS, RELEVANT IS CODE & REGULATION OF THE ELECTRICAL AUTHORITIES ETC. AS REQUIRED.
- EPC CONTRACTOR TO SUBMIT SHOP DRAWINGS FOR APPROVAL BEFORE EXECUTION OF WORK.
- DISCREPANCY, IF ANY SHALL BE BROUGHT TO THE NOTICE OF ENGINEER-IN-CHARGE AND CLARIFICATION OBTAINED IN WRITING PRIOR TO EXECUTION OF THE WORK.

TENDER DRAWING

CLIENT



CONSULTANT



MEP CONSULTANT

PKV CONSULTING ENGINEERS (P) LTD.



815 - C DDA FLATS
EAST OF LONI ROAD DELHI - 110093
email: -info@pkv.co.in

JOB TITLE

BQ WORKMEN GROUP HOUSING
COMPLEX AT DULIAJAN ASSAM

DRAWING TITLE

COMMUNITY CENTRE, GROUND
FLOOR CCTV & PA SYSTEM LAYOUT



SCALE

NTS


DATE

JULY 2025

DRG. NO.

RITES/BLD/EL/TEN/219

GROUND FLOOR

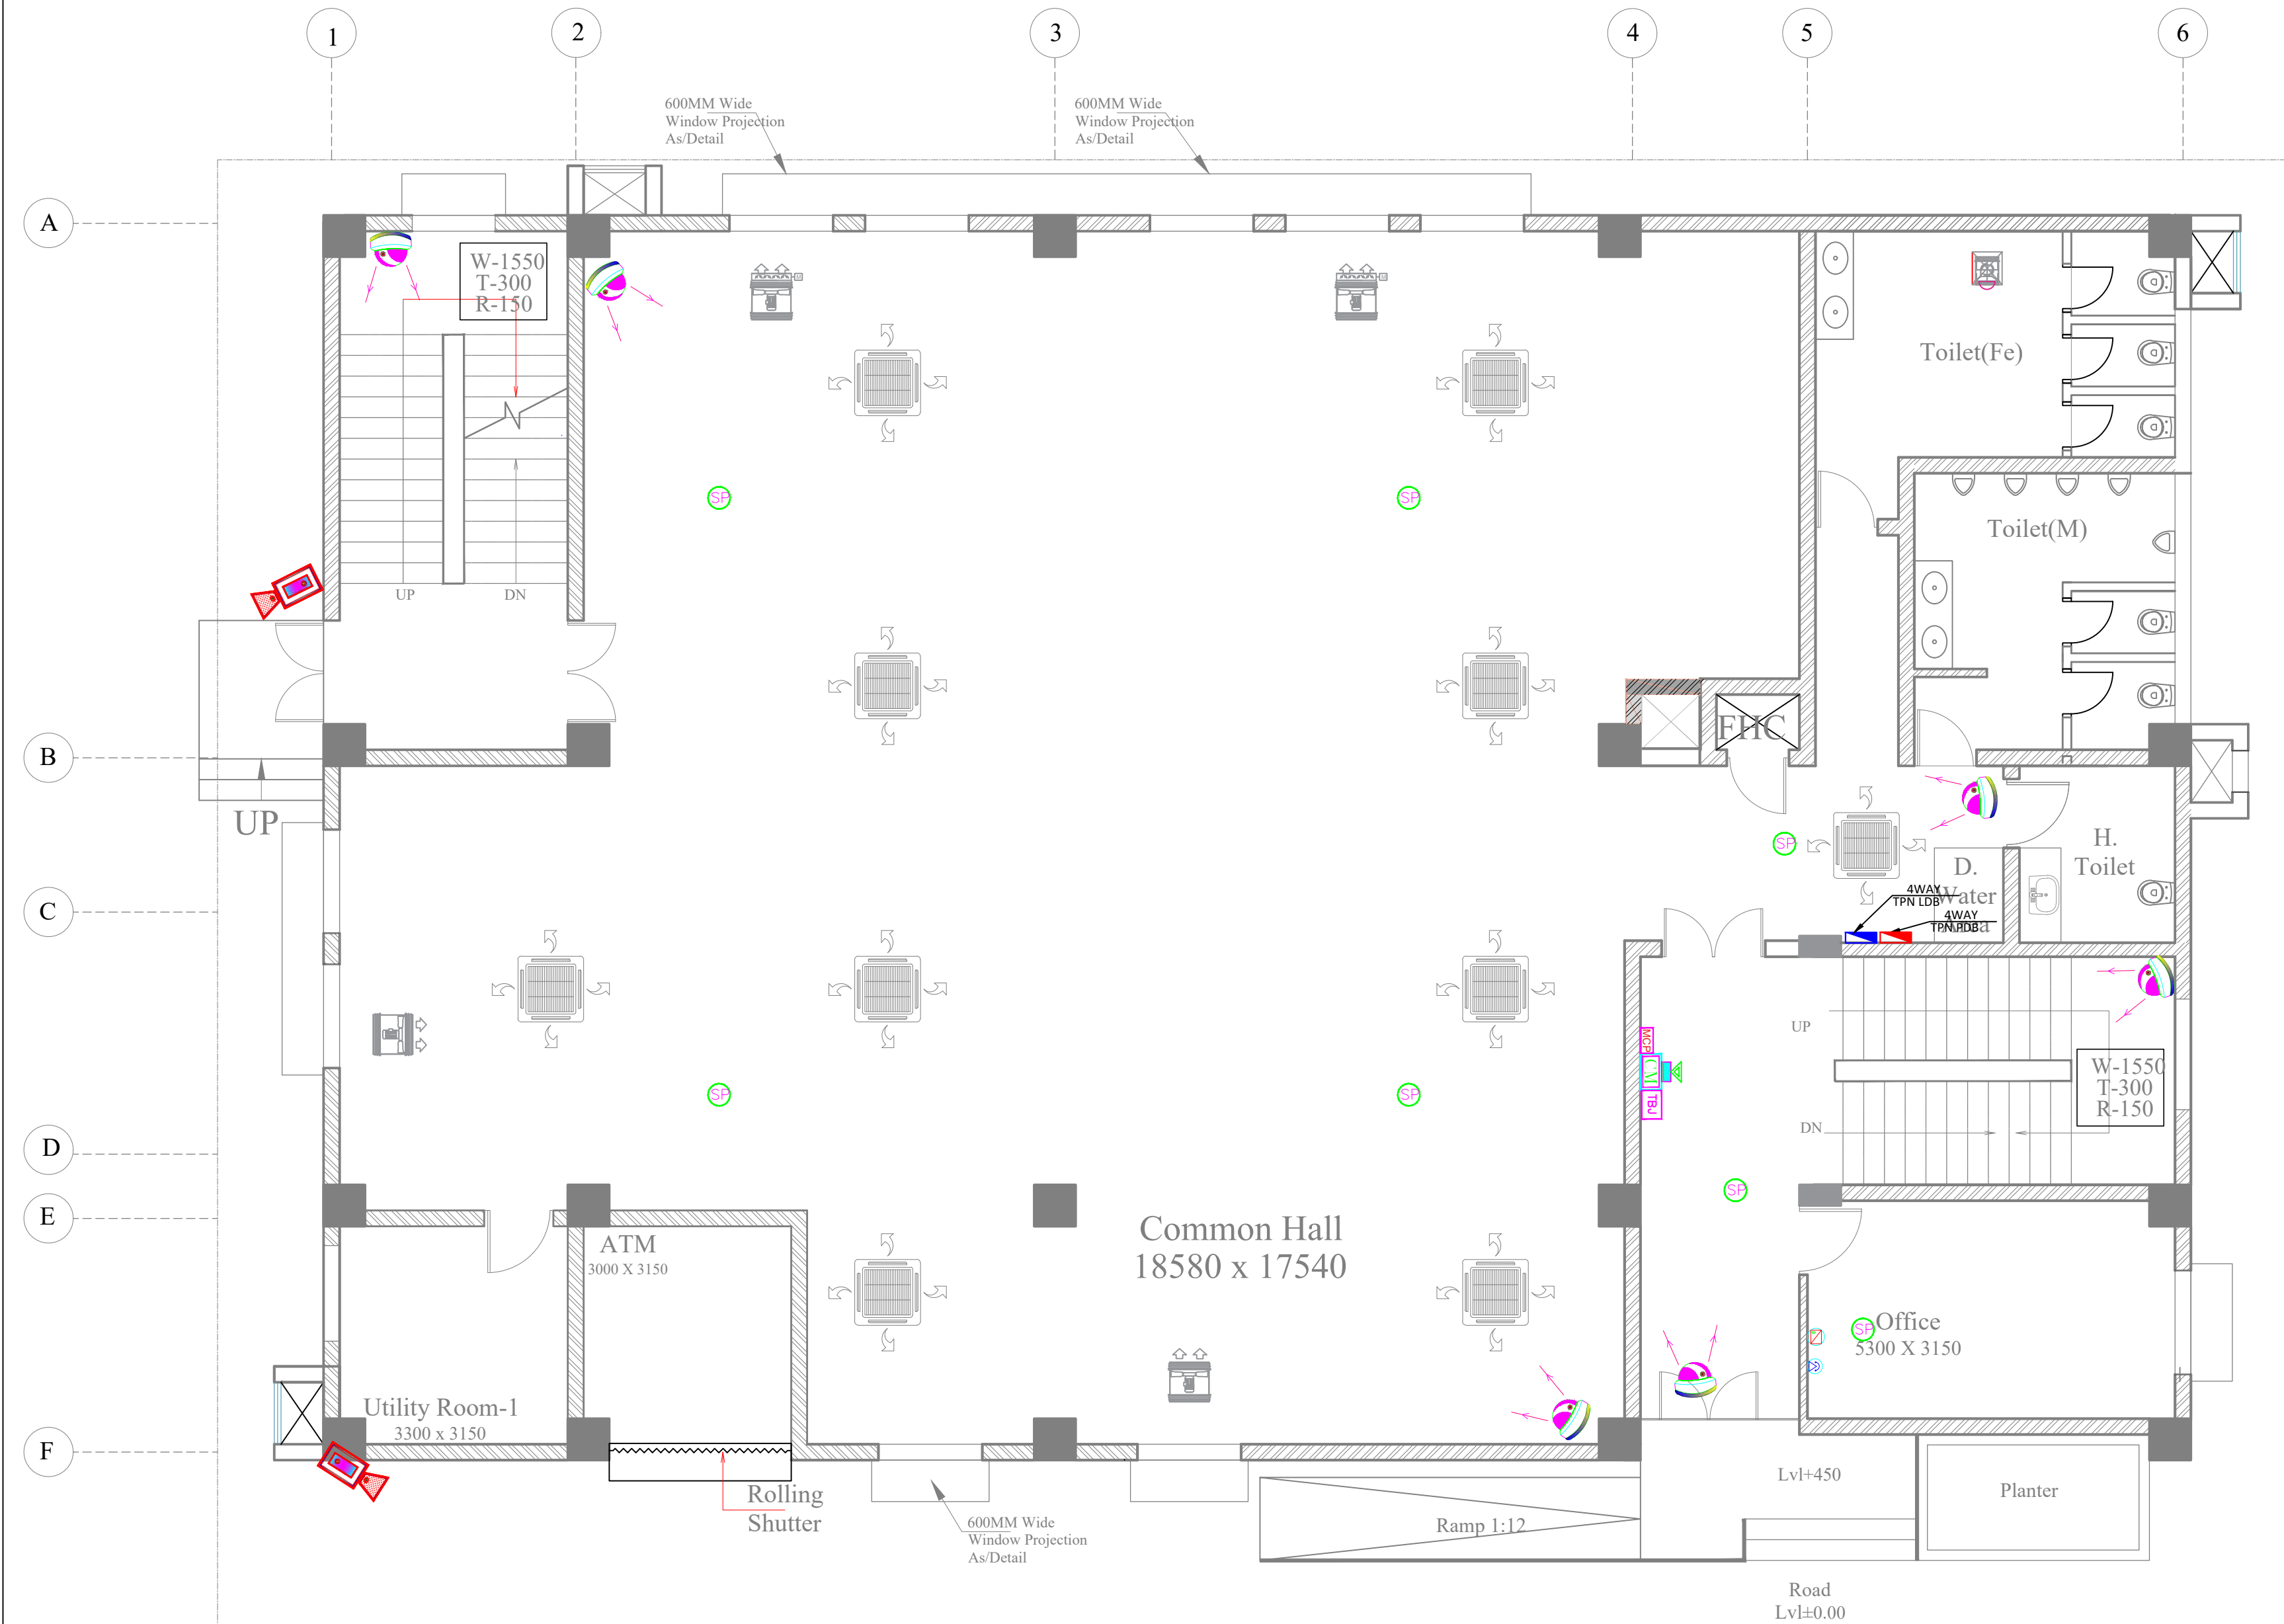

LEGENDS:-

	DOME CAMERA
	PA CEILING SPEAKER
	MANUAL CALL POINT
	HOOTER
	CONTEROL MODULE
	TALK BACK JACK

NOTES:-

- ALL DIMENSIONS ARE IN MM; UNLESS NOTED OTHERWISE.
- WRITTEN DIMENSIONS ARE TO BE FOLLOWED. DRAWINGS ARE NOT TO BE SCALED.
- ANY DISCREPANCY IN THE DRAWING SHALL BE BROUGHT TO THE NOTICE OF THE ENGINEER-IN-CHARGE.
- THIS DRAWING SHALL BE READ IN CONJUNCTION WITH OTHER RELEVANT DRAWINGS.
- ALL ELECTRICAL WORKS SHALL BE COMPLETED AS PER CPWD SPECIFICATIONS,RELEVANT IS CODE & REGULATION OF THE ELECTRICAL AUTHORITIES ETC. AS REQUIRED.
- EPC CONTRACTOR TO SUBMIT SHOP DRAWINGS FOR APPROVAL BEFORE EXECUTION OF WORK.
- DISCREPANCY, IF ANY SHALL BE BROUGHT TO THE NOTICE OF ENGINEER-IN-CHARGE AND CLARIFICATION OBTAINED IN WRITING PRIOR TO EXECUTION OF THE WORK.

TENDER DRAWING

CLIENT



CONSULTANT



MEP CONSULTANT

PKV CONSULTING ENGINEERS (P) LTD.



815 - C DDA FLATS
EAST OF LONI ROAD DELHI - 110093
email: -info@pkv.co.in

JOB TITLE

BQ WORKMEN GROUP HOUSING
COMPLEX AT DULIAJAN ASSAM

DRAWING TITLE

COMMUNITY CENTRE, FIRST FLOOR
CCTV & PA SYSTEM LAYOUT



SCALE

DATE


DRG. NO.


NTS

JULY 2025

RITES/BLD/EL/TEN/220

FIRST FLOOR

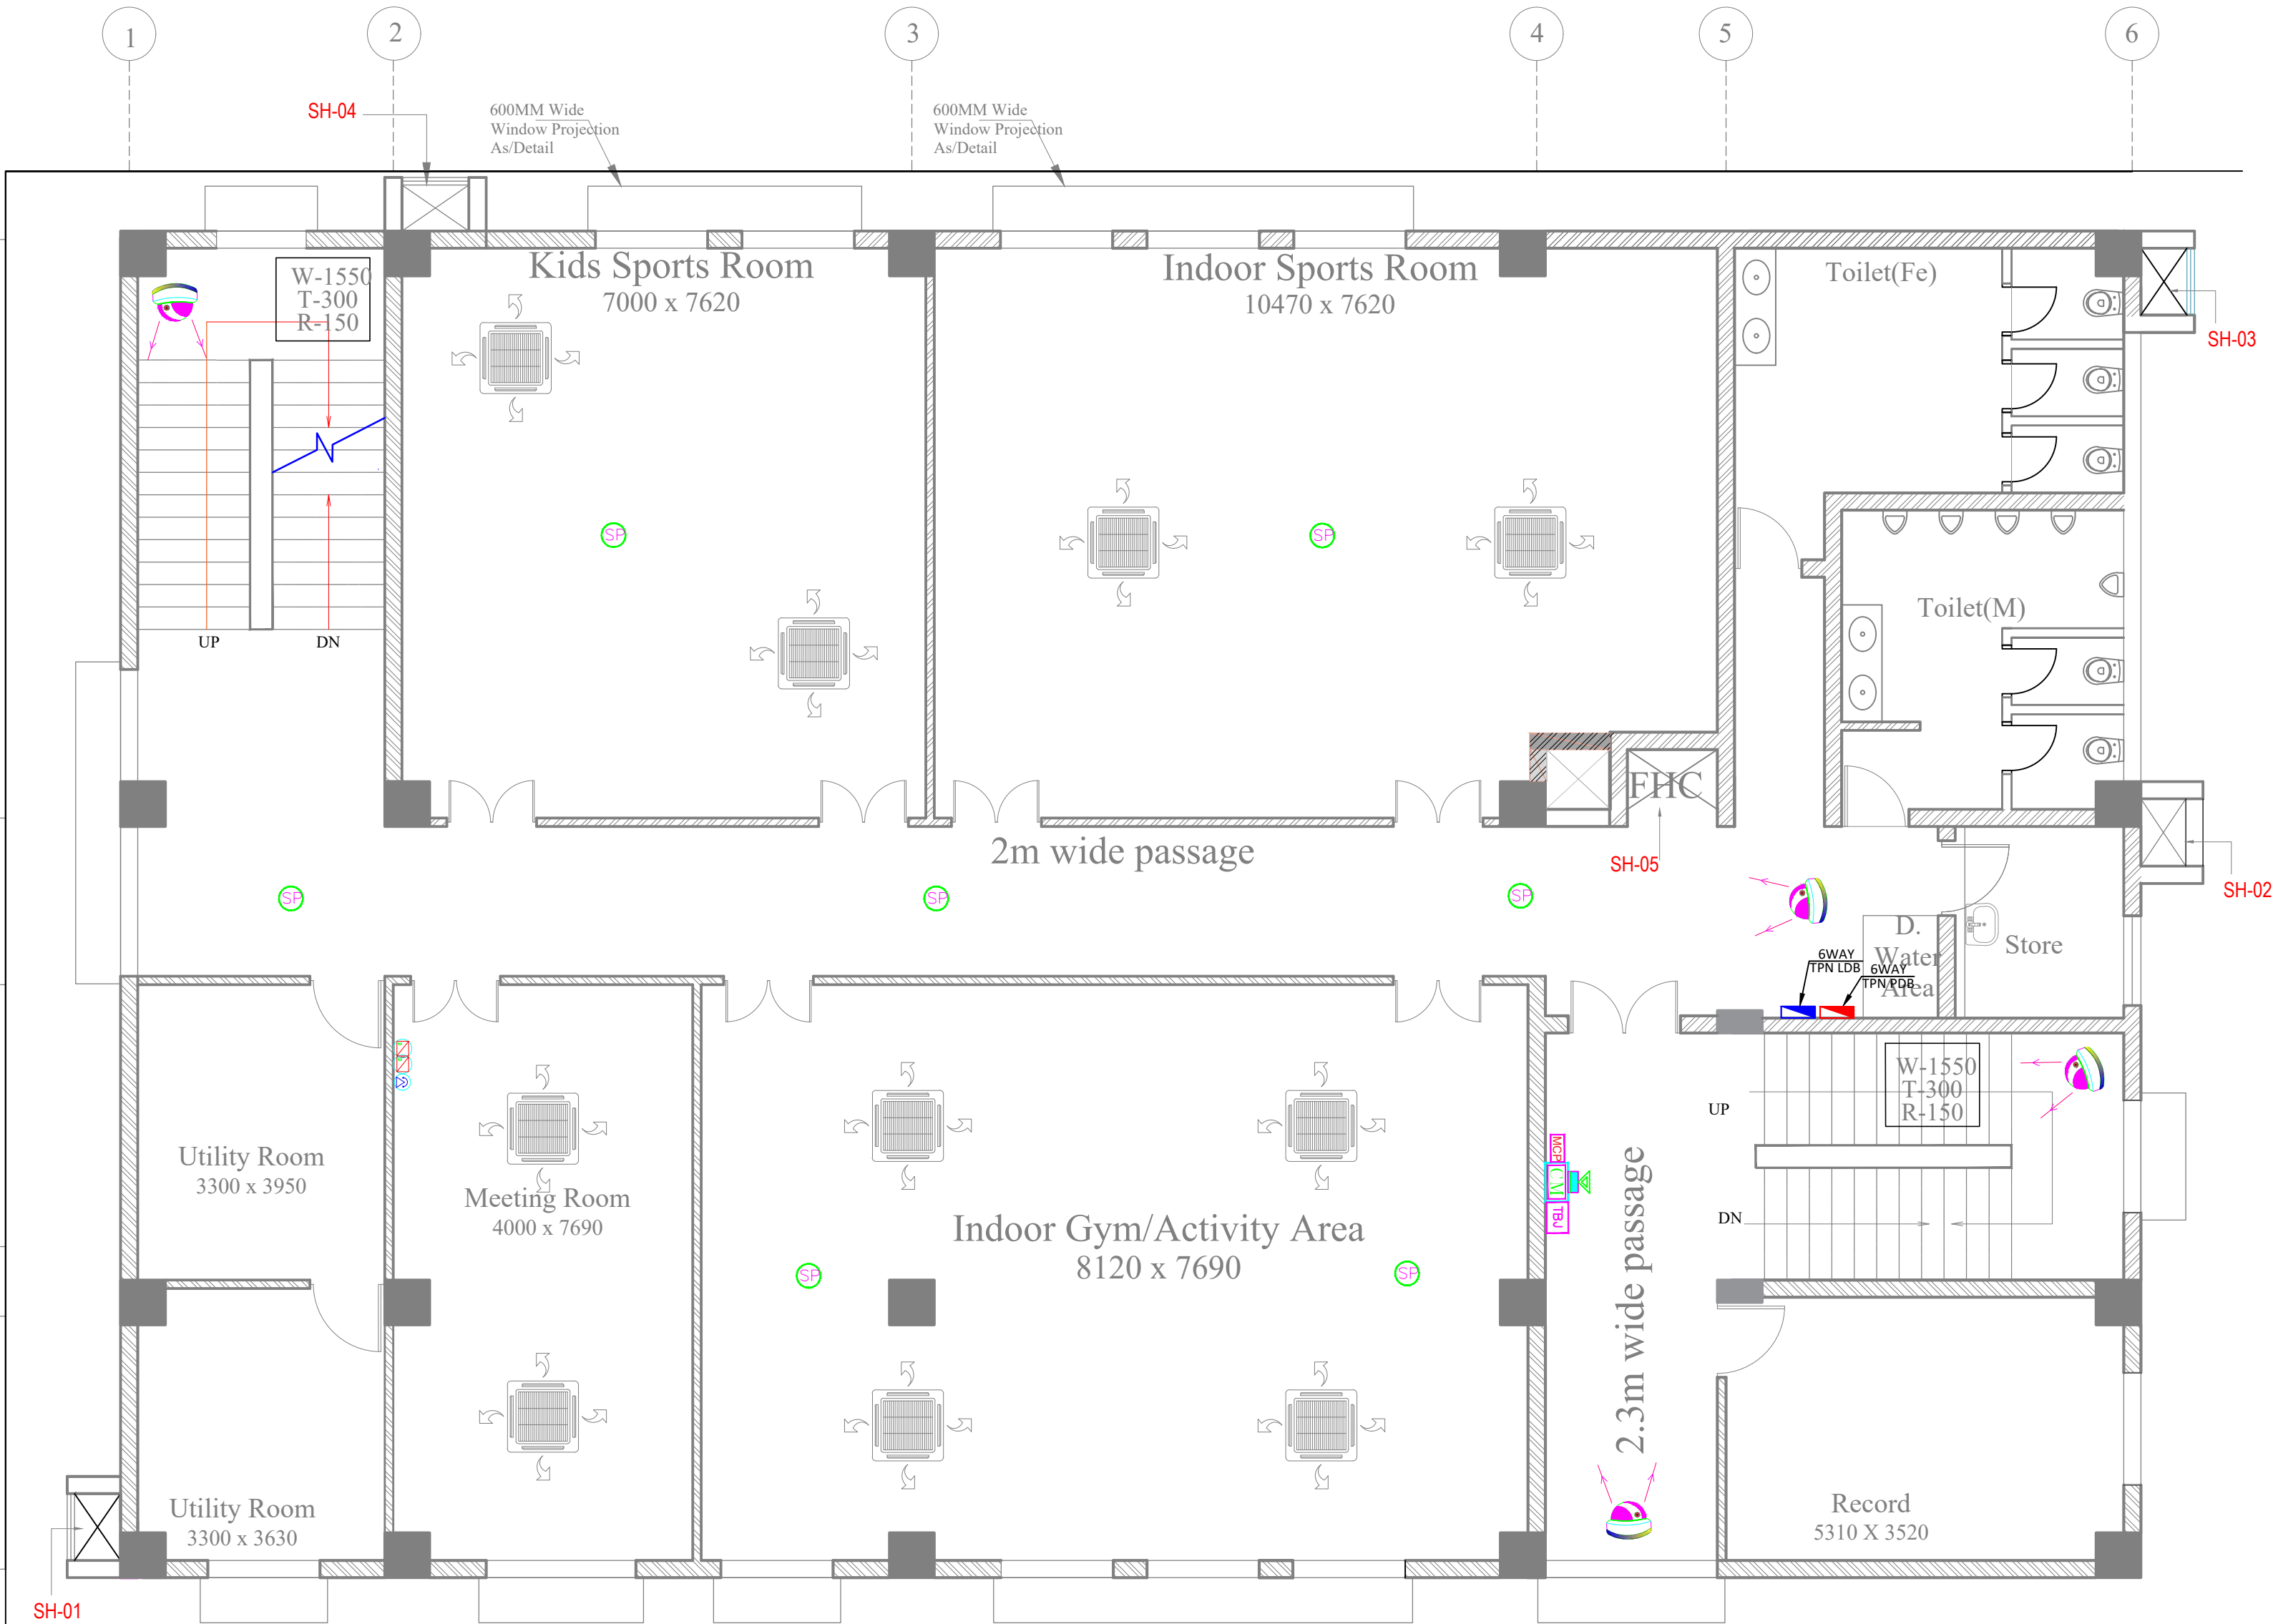

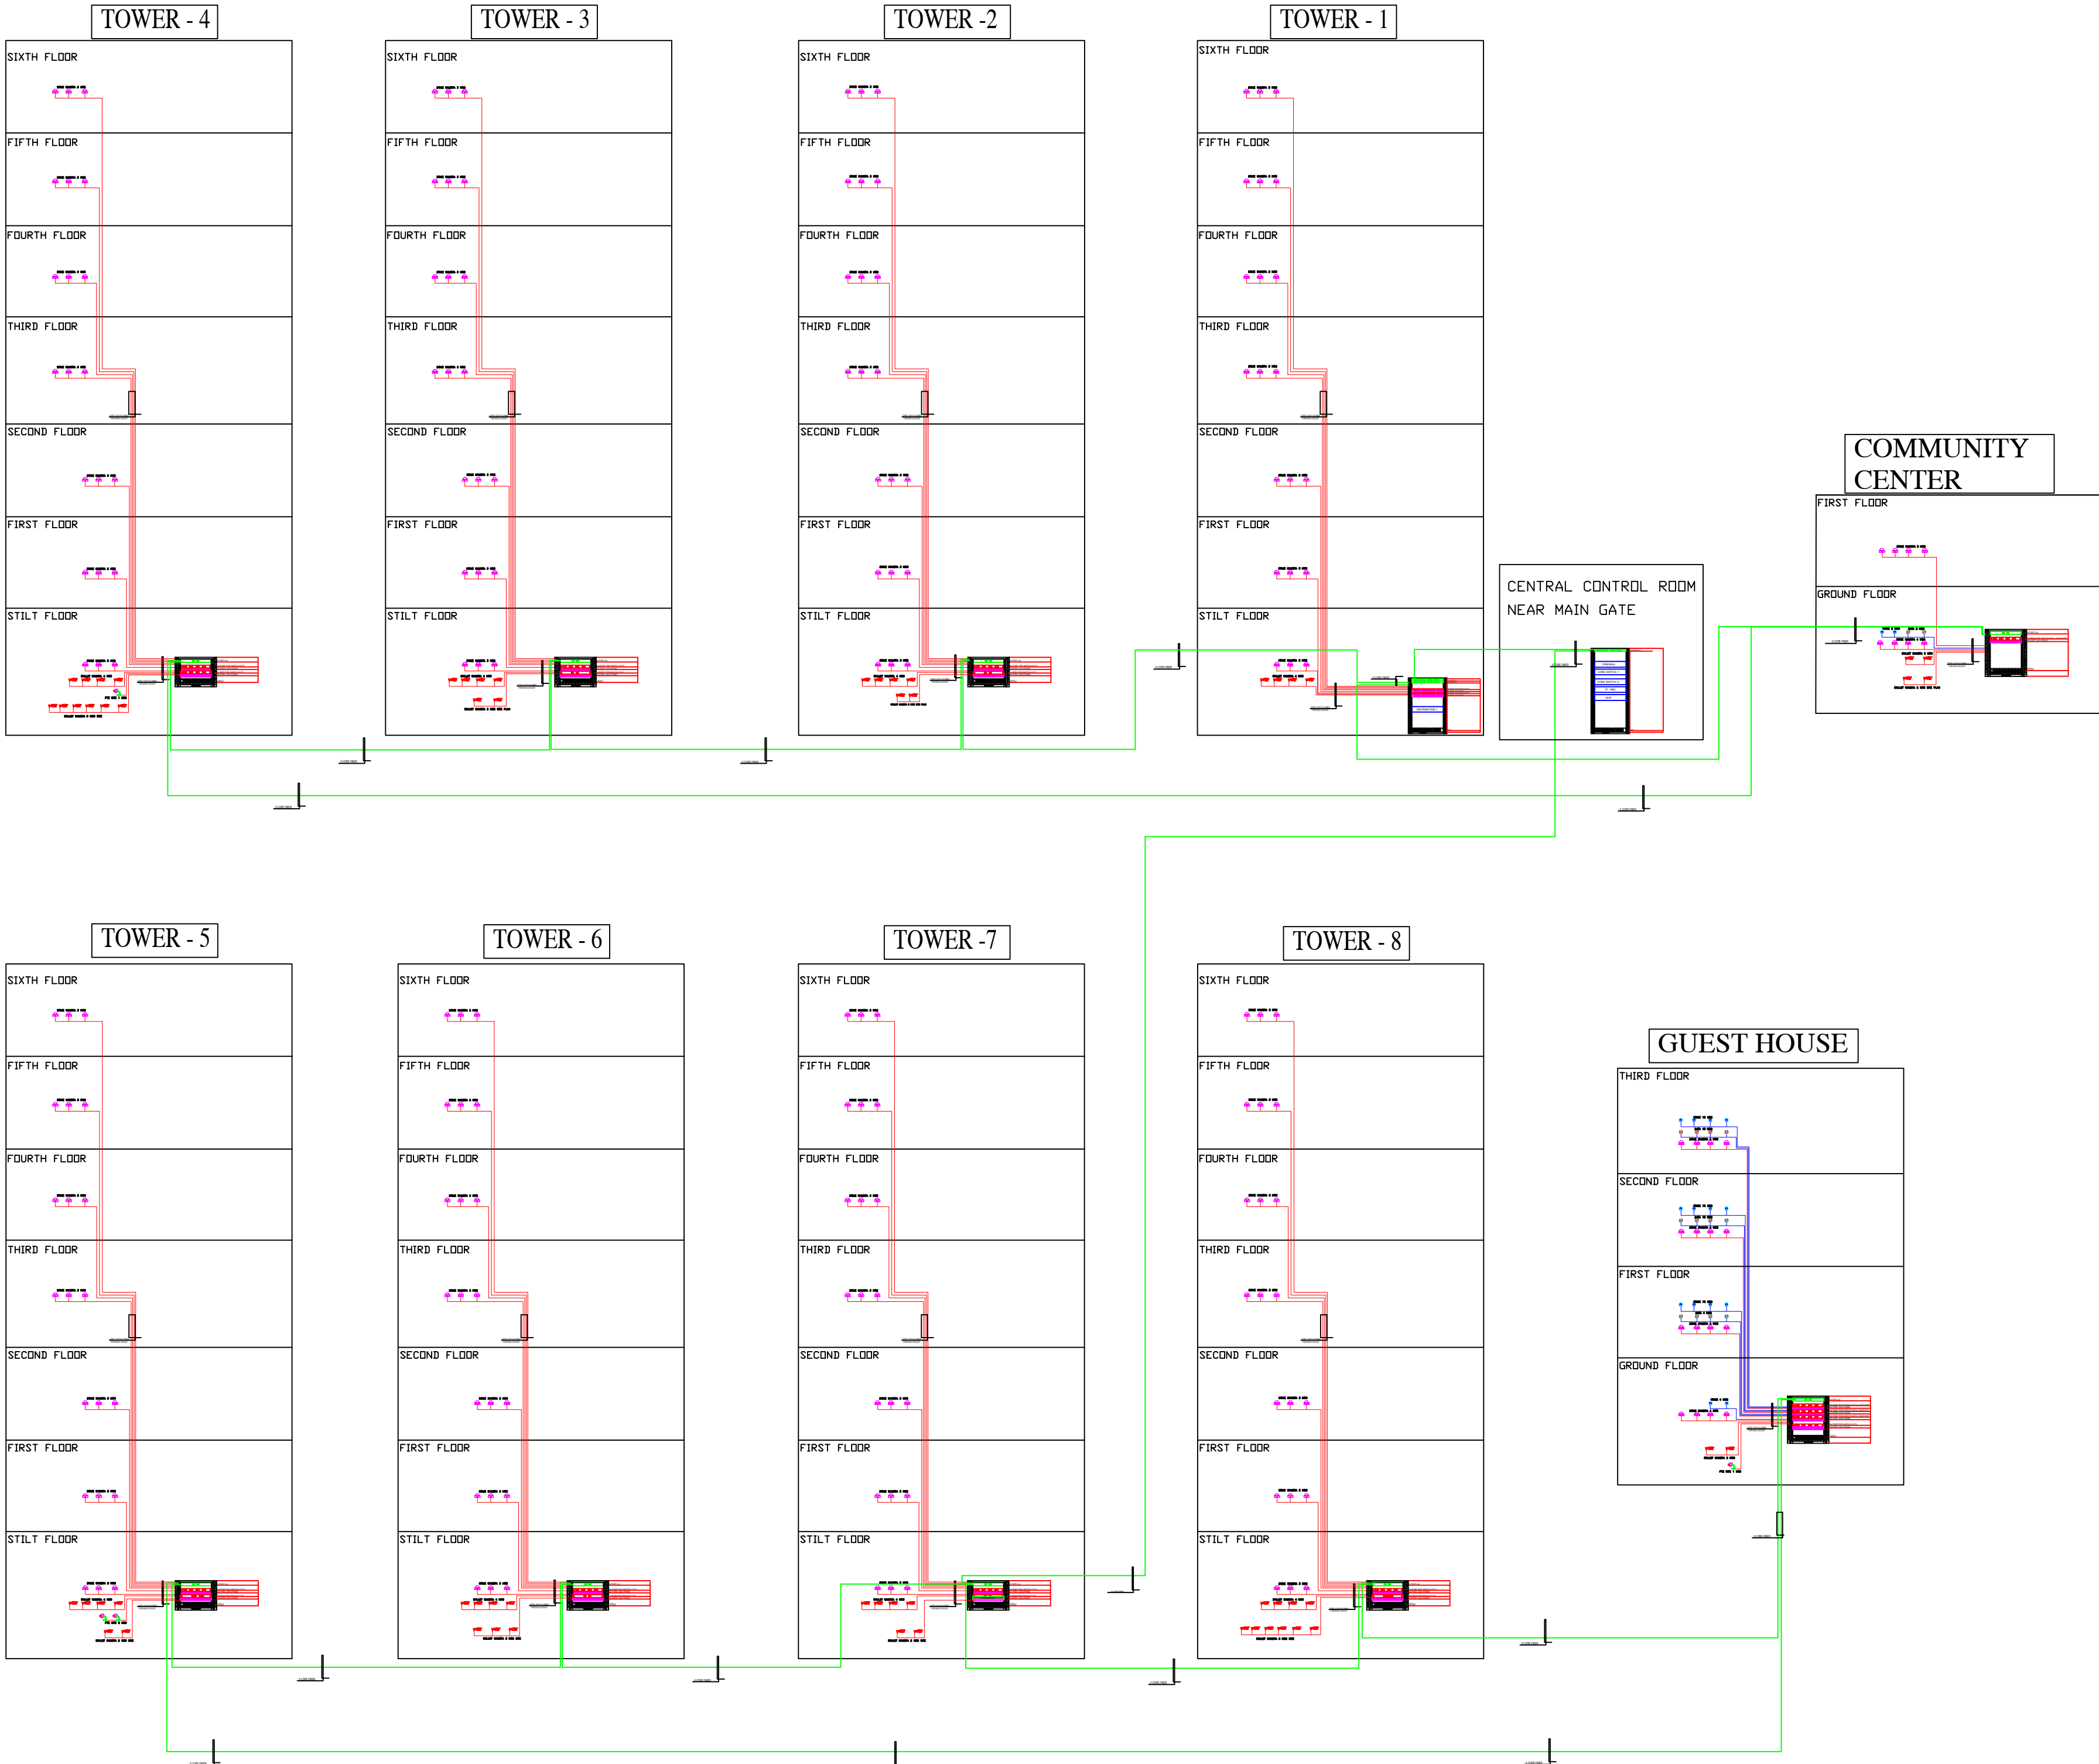

LEGENDS :-		
SYM.	DESCRIPTION	QTY.
	VOICE OUTLET	32
	LAN POINT	26
	DOME CAMERA	190
	BULLET CAMERA	63
	PTZ CAMERA	04
	CAT 6 CABLE	AS PER SITE REQ
	CAT 6A CABLE	AS PER SITE REQ
	6 CORE FIBER CABLE	AS PER SITE REQ

NOTE :
THESE ARE THE MINIMUM REQUIREMENT, IN CASE ANY ADDITIONAL REQUIREMENT EPC CONTRACTOR HAS TO CONSIDER WITHOUT ANY EXTRA COST

- NOTES:-
1. ALL DIMENSIONS ARE IN MM; UNLESS NOTED OTHERWISE.
 2. WRITTEN DIMENSIONS ARE TO BE FOLLOWED. DRAWINGS ARE NOT TO BE SCALED.
 3. ANY DISCREPANCY IN THE DRAWING SHALL BE BROUGHT TO THE NOTICE OF THE ENGINEER-IN-CHARGE.
 4. THIS DRAWING SHALL BE READ IN CONJUNCTION WITH OTHER RELEVANT DRAWINGS.
 5. ALL ELECTRICAL WORKS SHALL BE COMPLETED AS PER CPWD SPECIFICATIONS, RELEVANT IS CODE & REGULATION OF THE ELECTRICAL AUTHORITIES, ETC., AS REQUIRED.
 6. EPC CONTRACTOR TO SUBMIT SHOP DRAWINGS FOR APPROVAL BEFORE EXECUTION OF WORK.
 7. DISCREPANCY, IF ANY SHALL BE BROUGHT TO THE NOTICE OF ENGINEER-IN-CHARGE AND CLARIFICATION OBTAINED IN WRITING PRIOR TO EXECUTION OF THE WORK.

TENDER DRAWING		
CLIENT	 OIL INDIA LIMITED (A Govt. of India Enterprise)	
CONSULTANT	 RITES THE INFRASTRUCTURE PEOPLE (A Govt. of India Enterprise)	
MEP CONSULTANT	 PKV CONSULTING ENGINEERS (P) LTD 815 - C DDA FLATS EAST OF LONI ROAD DELHI - 110093 email:- info@pkv.co.in	
JOB TITLE	BQ WORKMEN GROUP HOUSING COMPLEX AT DULIAJAN ASSAM	
DRAWING TITLE		
SCHEMATIC DIAGRAM OF CCTV AND EPABX SYSTEM		
SCALE	DATE	
NTS	JULY 2025	RITES/BLD/EL/TEN/221



TYPICAL FLOOR PLAN

Note: Split AC units shown in the drawing are only for illustrative purposes only, not in the scope of EPC contract.

MECHANICAL LEGEND	
SYMBOL	DESCRIPTION
	SPLIT HI WALL UNIT
	SPLIT OUTDOOR UNIT
	REFRIGERANT GAS PIPE
	REFRIGERANT LIQUID PIPE
	DRAIN PIPE
	PROPELLER FAN

NOTES:-

- ALL DIMENSIONS ARE IN MM, UNLESS NOTED OTHERWISE.
- WRITTEN DIMENSIONS ARE TO BE FOLLOWED. DRAWINGS ARE NOT TO BE SCALED.
- ANY DISCREPANCY IN THE DRAWING SHALL BE BROUGHT TO THE NOTICE OF THE ENGINEER-IN-CHARGE.
- THIS DRAWING SHALL BE READ IN CONJUNCTION WITH OTHER RELEVANT DRAWINGS.
- ALL ELECTRICAL WORKS SHALL BE COMPLETED AS PER CPWD SPECIFICATIONS, RELEVANT IS CODE & REGULATION OF THE ELECTRICAL AUTHORITIES, ETC. AS REQUIRED.
- EPC CONTRACTOR TO SUBMIT SHOP DRAWINGS FOR APPROVAL BEFORE EXECUTION OF WORK.
- DISCREPANCY, IF ANY SHALL BE BROUGHT TO THE NOTICE OF ENGINEER-IN-CHARGE AND CLARIFICATION OBTAINED IN WRITING PRIOR TO EXECUTION OF THE WORK.

TENDER DRAWING

CLIENT	OIL INDIA LIMITED (A Govt. of India Enterprise)	
CONSULTANT	IRITES THE INFRASTRUCTURE PEOPLE (A Govt. of India Enterprise)	
MEP Consultants:	PKV CONSULTING ENGINEERS(P) LTD. C-815, DDA Flats, Loni Road, Delhi-110093 TELEFAX-011-22816297 E-mail:-info@pkv.co.in, pramod@pkv.co.in	
JOB TITLE	BQ WORKMEN GROUP HOUSING COMPLEX AT DULIAJAN ASSAM	
DRAWING TITLE	HOUSING BLOCK, TYPICAL FLOOR HVAC LAYOUT	
Scale	DATE	DRG. NO.
NTS	JULY 2025	IRITES/BLD/HVAC/TEN/301