



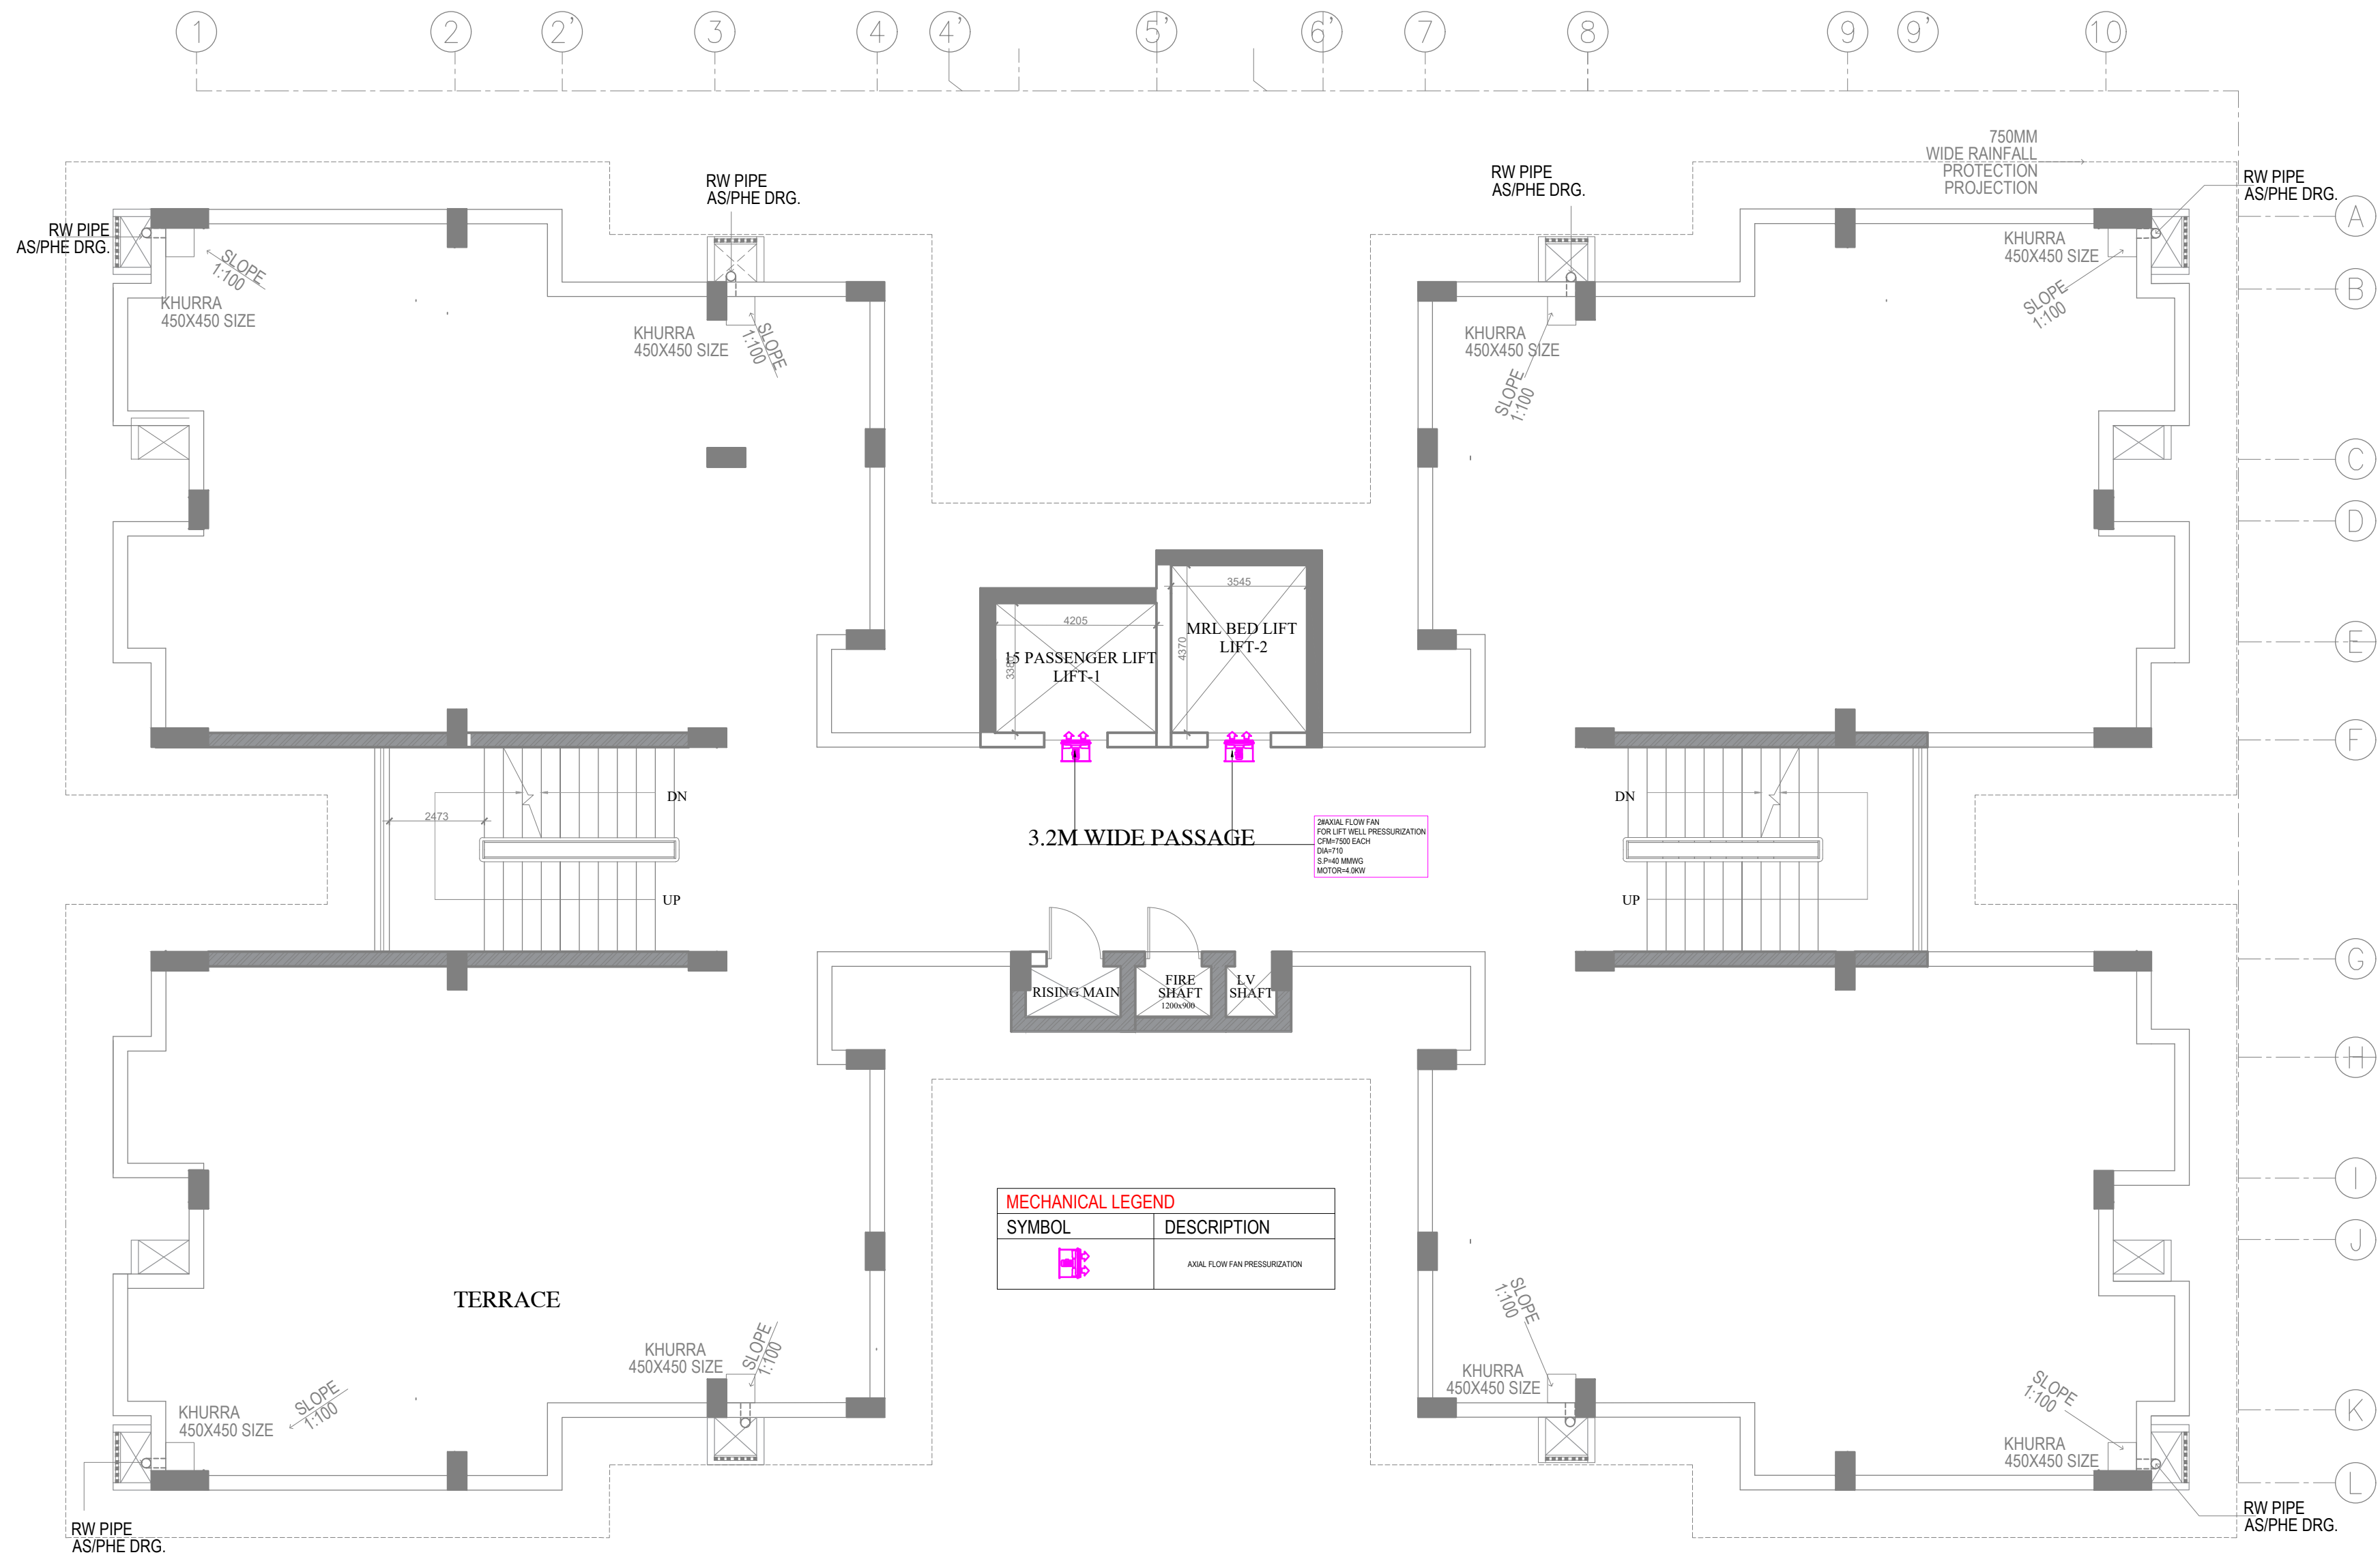

- NOTES:-**
1. ALL DIMENSIONS ARE IN MM; UNLESS NOTED OTHERWISE.
 2. WRITTEN DIMENSIONS ARE TO BE FOLLOWED. DRAWINGS ARE NOT TO BE SCALED.
 3. ANY DISCREPANCY IN THE DRAWING SHALL BE BROUGHT TO THE NOTICE OF THE ENGINEER-IN-CHARGE.
 4. THIS DRAWING SHALL BE READ IN CONJUNCTION WITH OTHER RELEVANT DRAWINGS.
 5. ALL ELECTRICAL WORKS SHALL BE COMPLETED AS PER CPWD SPECIFICATIONS, RELEVANT IS CODE & REGULATION OF THE ELECTRICAL AUTHORITIES ETC. AS REQUIRED.
 6. EPC CONTRACTOR TO SUBMIT SHOP DRAWINGS FOR APPROVAL BEFORE EXECUTION OF WORK.
 7. DISCREPANCY, IF ANY SHALL BE BROUGHT TO THE NOTICE OF ENGINEER-IN-CHARGE AND CLARIFICATION OBTAINED IN WRITING PRIOR TO EXECUTION OF THE WORK.

TENDER DRAWING		
REVISIONS		
CLIENT		
OIL INDIA LIMITED (A Govt. of India Enterprise)		
CONSULTANT		
RITES THE INFRASTRUCTURE PEOPLE (A Govt. of India Enterprise)		
MEP Consultants:		
PKV CONSULTING ENGINEERS(P) LTD. C-815, DDA Flats, Loni Road, Delhi-110093 TELEFAX-011-22816297 E-mail:-info@pkv.co.in, pramod@pkv.co.in		
JOB TITLE		
BQ WORKMEN GROUP HOUSING COMPLEX AT DULIAJAN ASSAM		
DRAWING TITLE		
HOUSING BLOCK, TERRACE FLOOR HVAC LAYOUT		
Scale	DATE	DRG. NO.
NTS	JULY 2025	RITES/BLD/HVAC/TEN/302

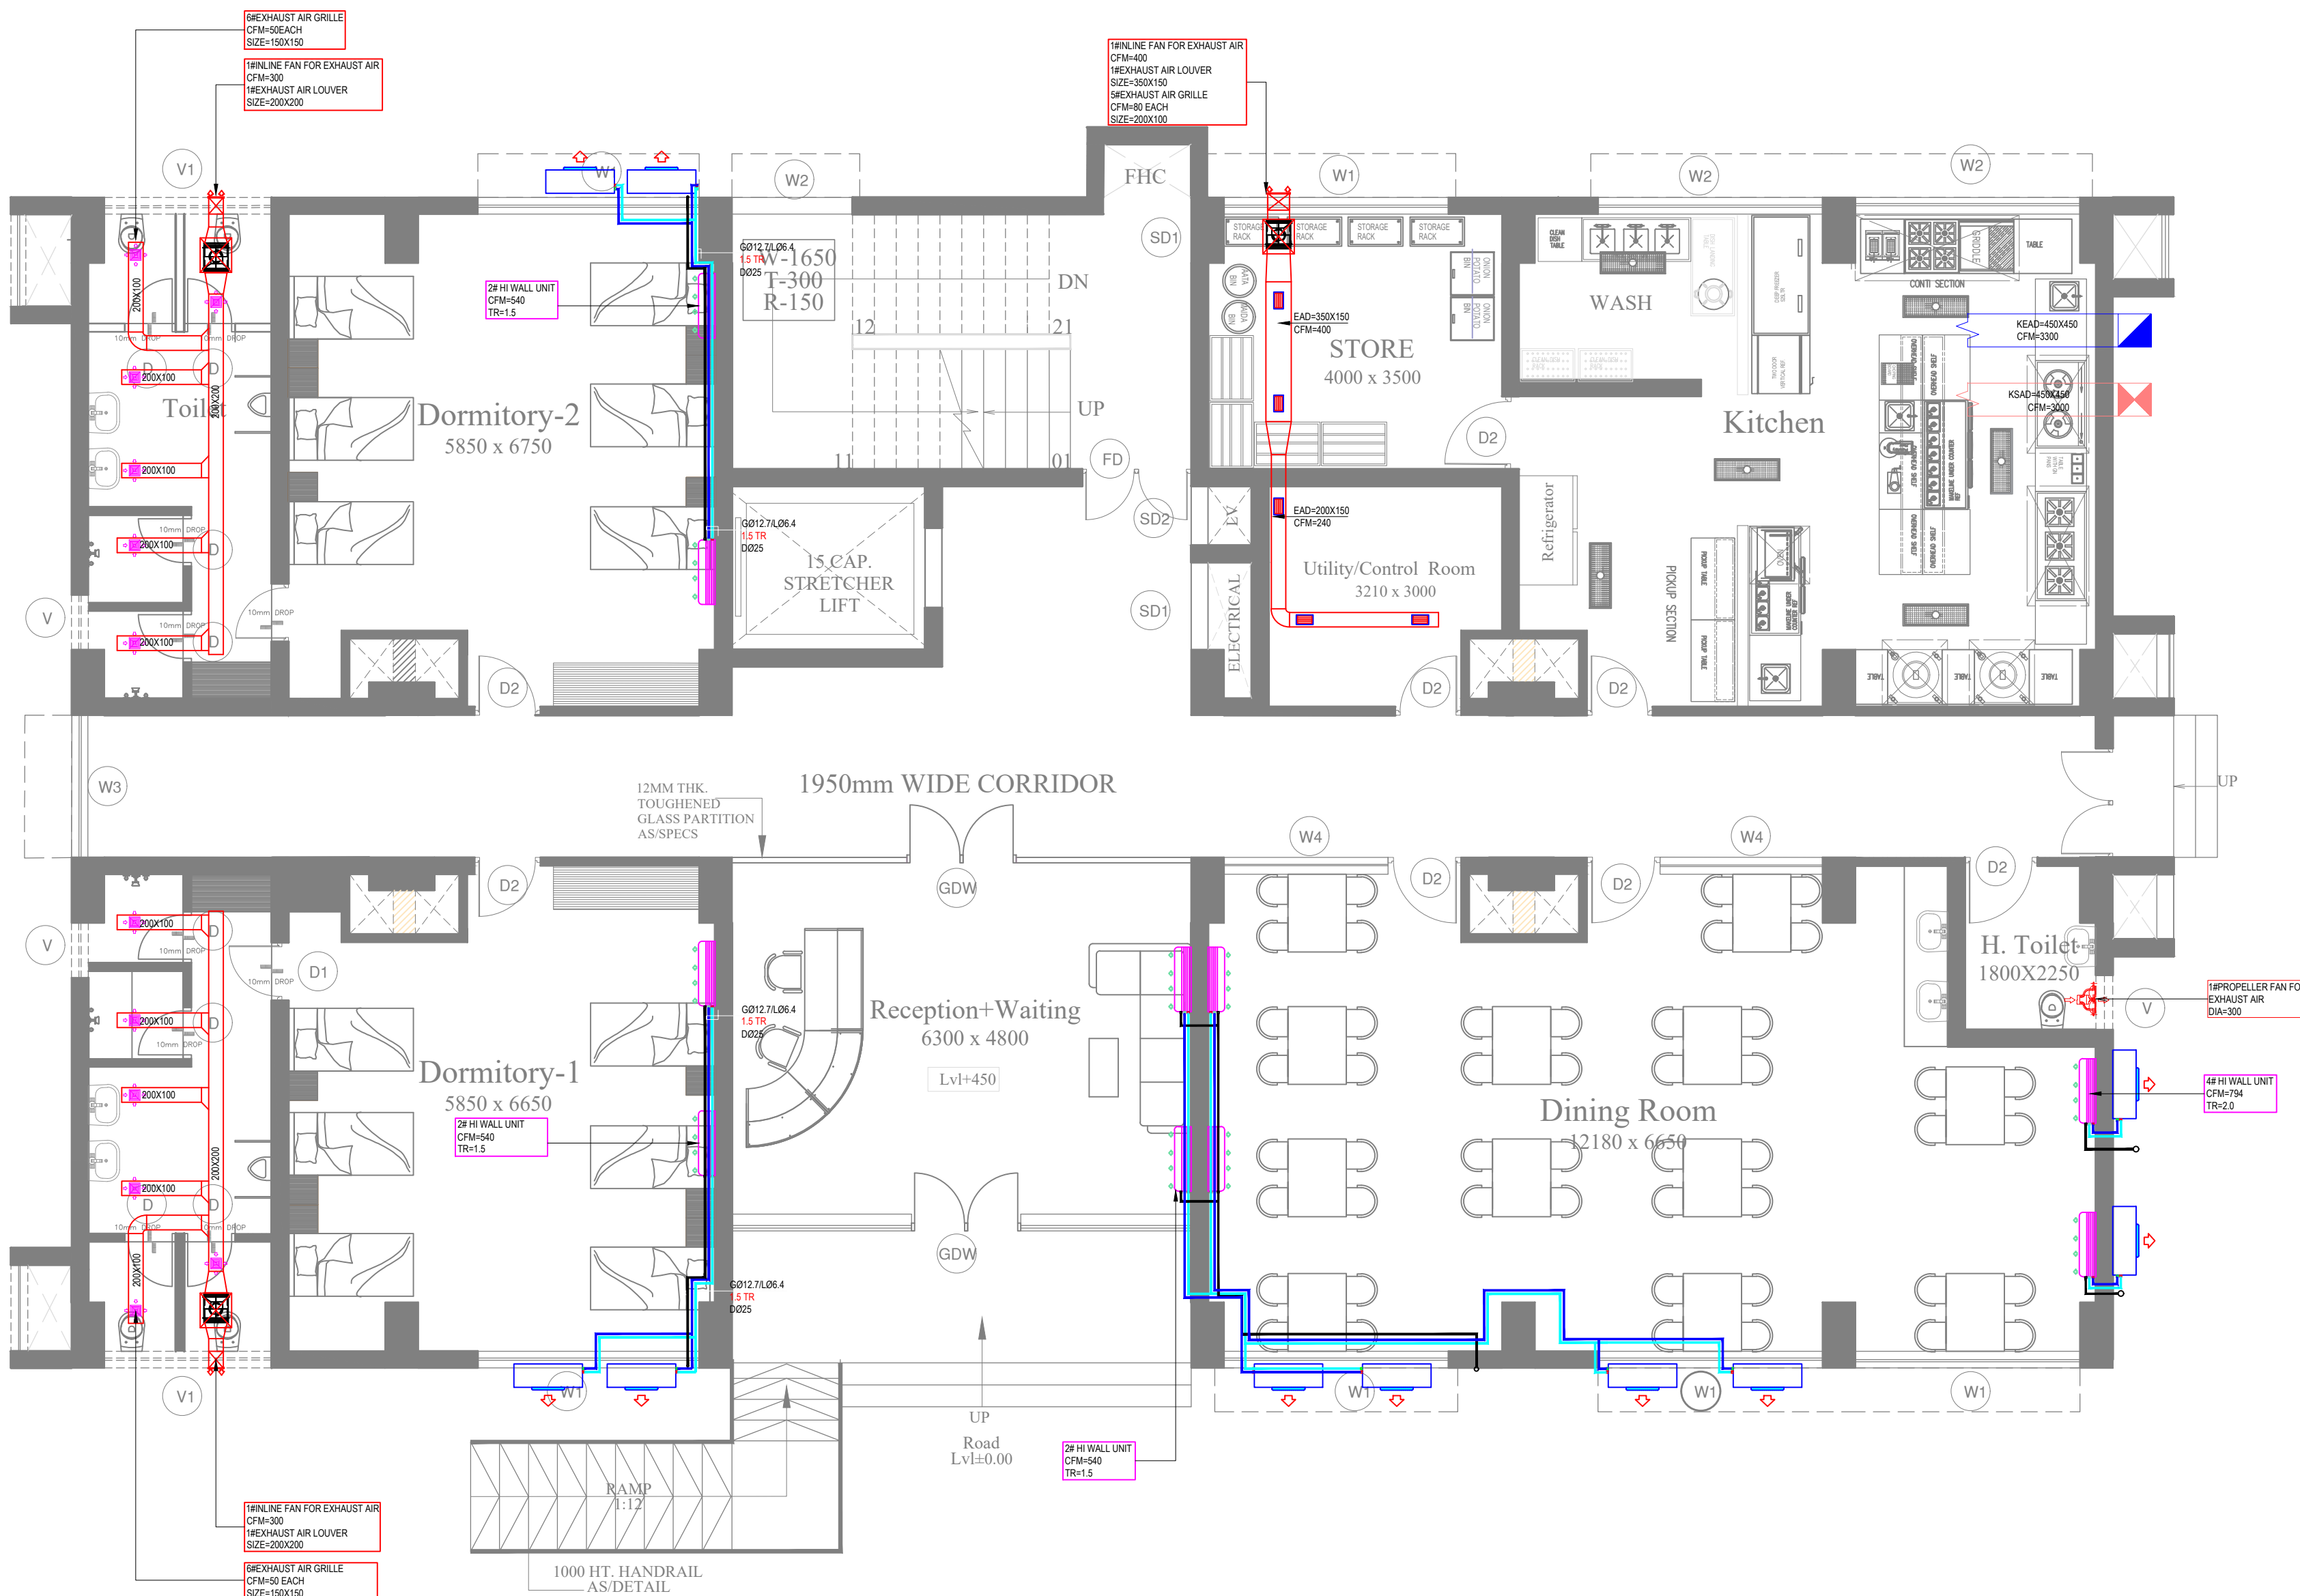

NOTES:-

1. ALL DIMENSIONS ARE IN MM; UNLESS NOTED OTHERWISE.
2. WRITTEN DIMENSIONS ARE TO BE FOLLOWED. DRAWINGS ARE NOT TO BE SCALED.
3. ANY DISCREPANCY IN THE DRAWING SHALL BE BROUGHT TO THE NOTICE OF THE ENGINEER-IN-CHARGE.
4. THIS DRAWING SHALL BE READ IN CONJUNCTION WITH OTHER RELEVANT DRAWINGS, TENDER DOCUMENT.
5. ALL ELECTRICAL WORKS SHALL BE COMPLETED AS PER CPWD SPECIFICATIONS, RELEVANT IS CODE & REGULATION OF THE ELECTRICAL AUTHORITIES ETC. AS REQUIRED.
6. EPC CONTRACTOR TO SUBMIT SHOP DRAWINGS FOR APPROVAL BEFORE EXECUTION OF WORK.
7. DISCREPANCY, IF ANY SHALL BE BROUGHT TO THE NOTICE OF ENGINEER-IN-CHARGE AND CLARIFICATION OBTAINED IN WRITING PRIOR TO EXECUTION OF THE WORK.

TENDER DRAWING

CLIENT



CONSULTANT



MEP CONSULTANT

PKV CONSULTING ENGINEERS(P)LTD.
C-815, DDA Flats, Loni Road, Delhi-110093
TELEFAX-011-22816297
E-mail: info@pkv.co.in
E-mail: pramod@pkv.co.in



JOB TITLE

BQ WORKMEN GROUP HOUSING
COMPLEX AT DULIAJAN ASSAM

DRAWING TITLE

**GROUND FLOOR HVAC PLAN
GUEST HOUSE**

SCALE

NTS.

DATE

JULY 2025

DRG. NO.

RITES/BLD/HVAC/TEN/303



NOTES:-

1. ALL DIMENSIONS ARE IN MM; UNLESS NOTED OTHERWISE.
2. WRITTEN DIMENSIONS ARE TO BE FOLLOWED. DRAWINGS ARE NOT TO BE SCALED.
3. ANY DISCREPANCY IN THE DRAWING SHALL BE BROUGHT TO THE NOTICE OF THE ENGINEER-IN-CHARGE.
4. THIS DRAWING SHALL BE READ IN CONJUNCTION WITH OTHER RELEVANT DRAWINGS, TENDER DOCUMENT.
5. ALL ELECTRICAL WORKS SHALL BE COMPLETED AS PER CPWD SPECIFICATIONS, RELEVANT IS CODE & REGULATION OF THE ELECTRICAL AUTHORITIES ETC. AS REQUIRED.
6. EPC CONTRACTOR TO SUBMIT SHOP DRAWINGS FOR APPROVAL BEFORE EXECUTION OF WORK.
7. DISCREPANCY, IF ANY SHALL BE BROUGHT TO THE NOTICE OF ENGINEER-IN-CHARGE AND CLARIFICATION OBTAINED IN WRITING PRIOR TO EXECUTION OF THE WORK.

TENDER DRAWING

CLIENT

OIL INDIA LIMITED
(A Govt. of India Enterprise)

CONSULTANT

IRITES
THE INFRASTRUCTURE PEOPLE
(A Govt. of India Enterprise)

MEP CONSULTANT

PKV CONSULTING ENGINEERS(P)LTD.
C-815, DDA Flats, Loni Road, Delhi-110093
TELEFAX-011-22816297
E-mail: info@pkv.co.in
E-mail: pramod@pkv.co.in



JOB TITLE

BQ WORKMEN GROUP HOUSING
COMPLEX AT DULIAJAN ASSAM

DRAWING TITLE

**FIRST FLOOR HVAC PLAN
GUEST HOUSE**

SCALE


DATE

JULY 2025

NTS.

DRG. NO.

IRITES/BLD/HVAC/TEN/304

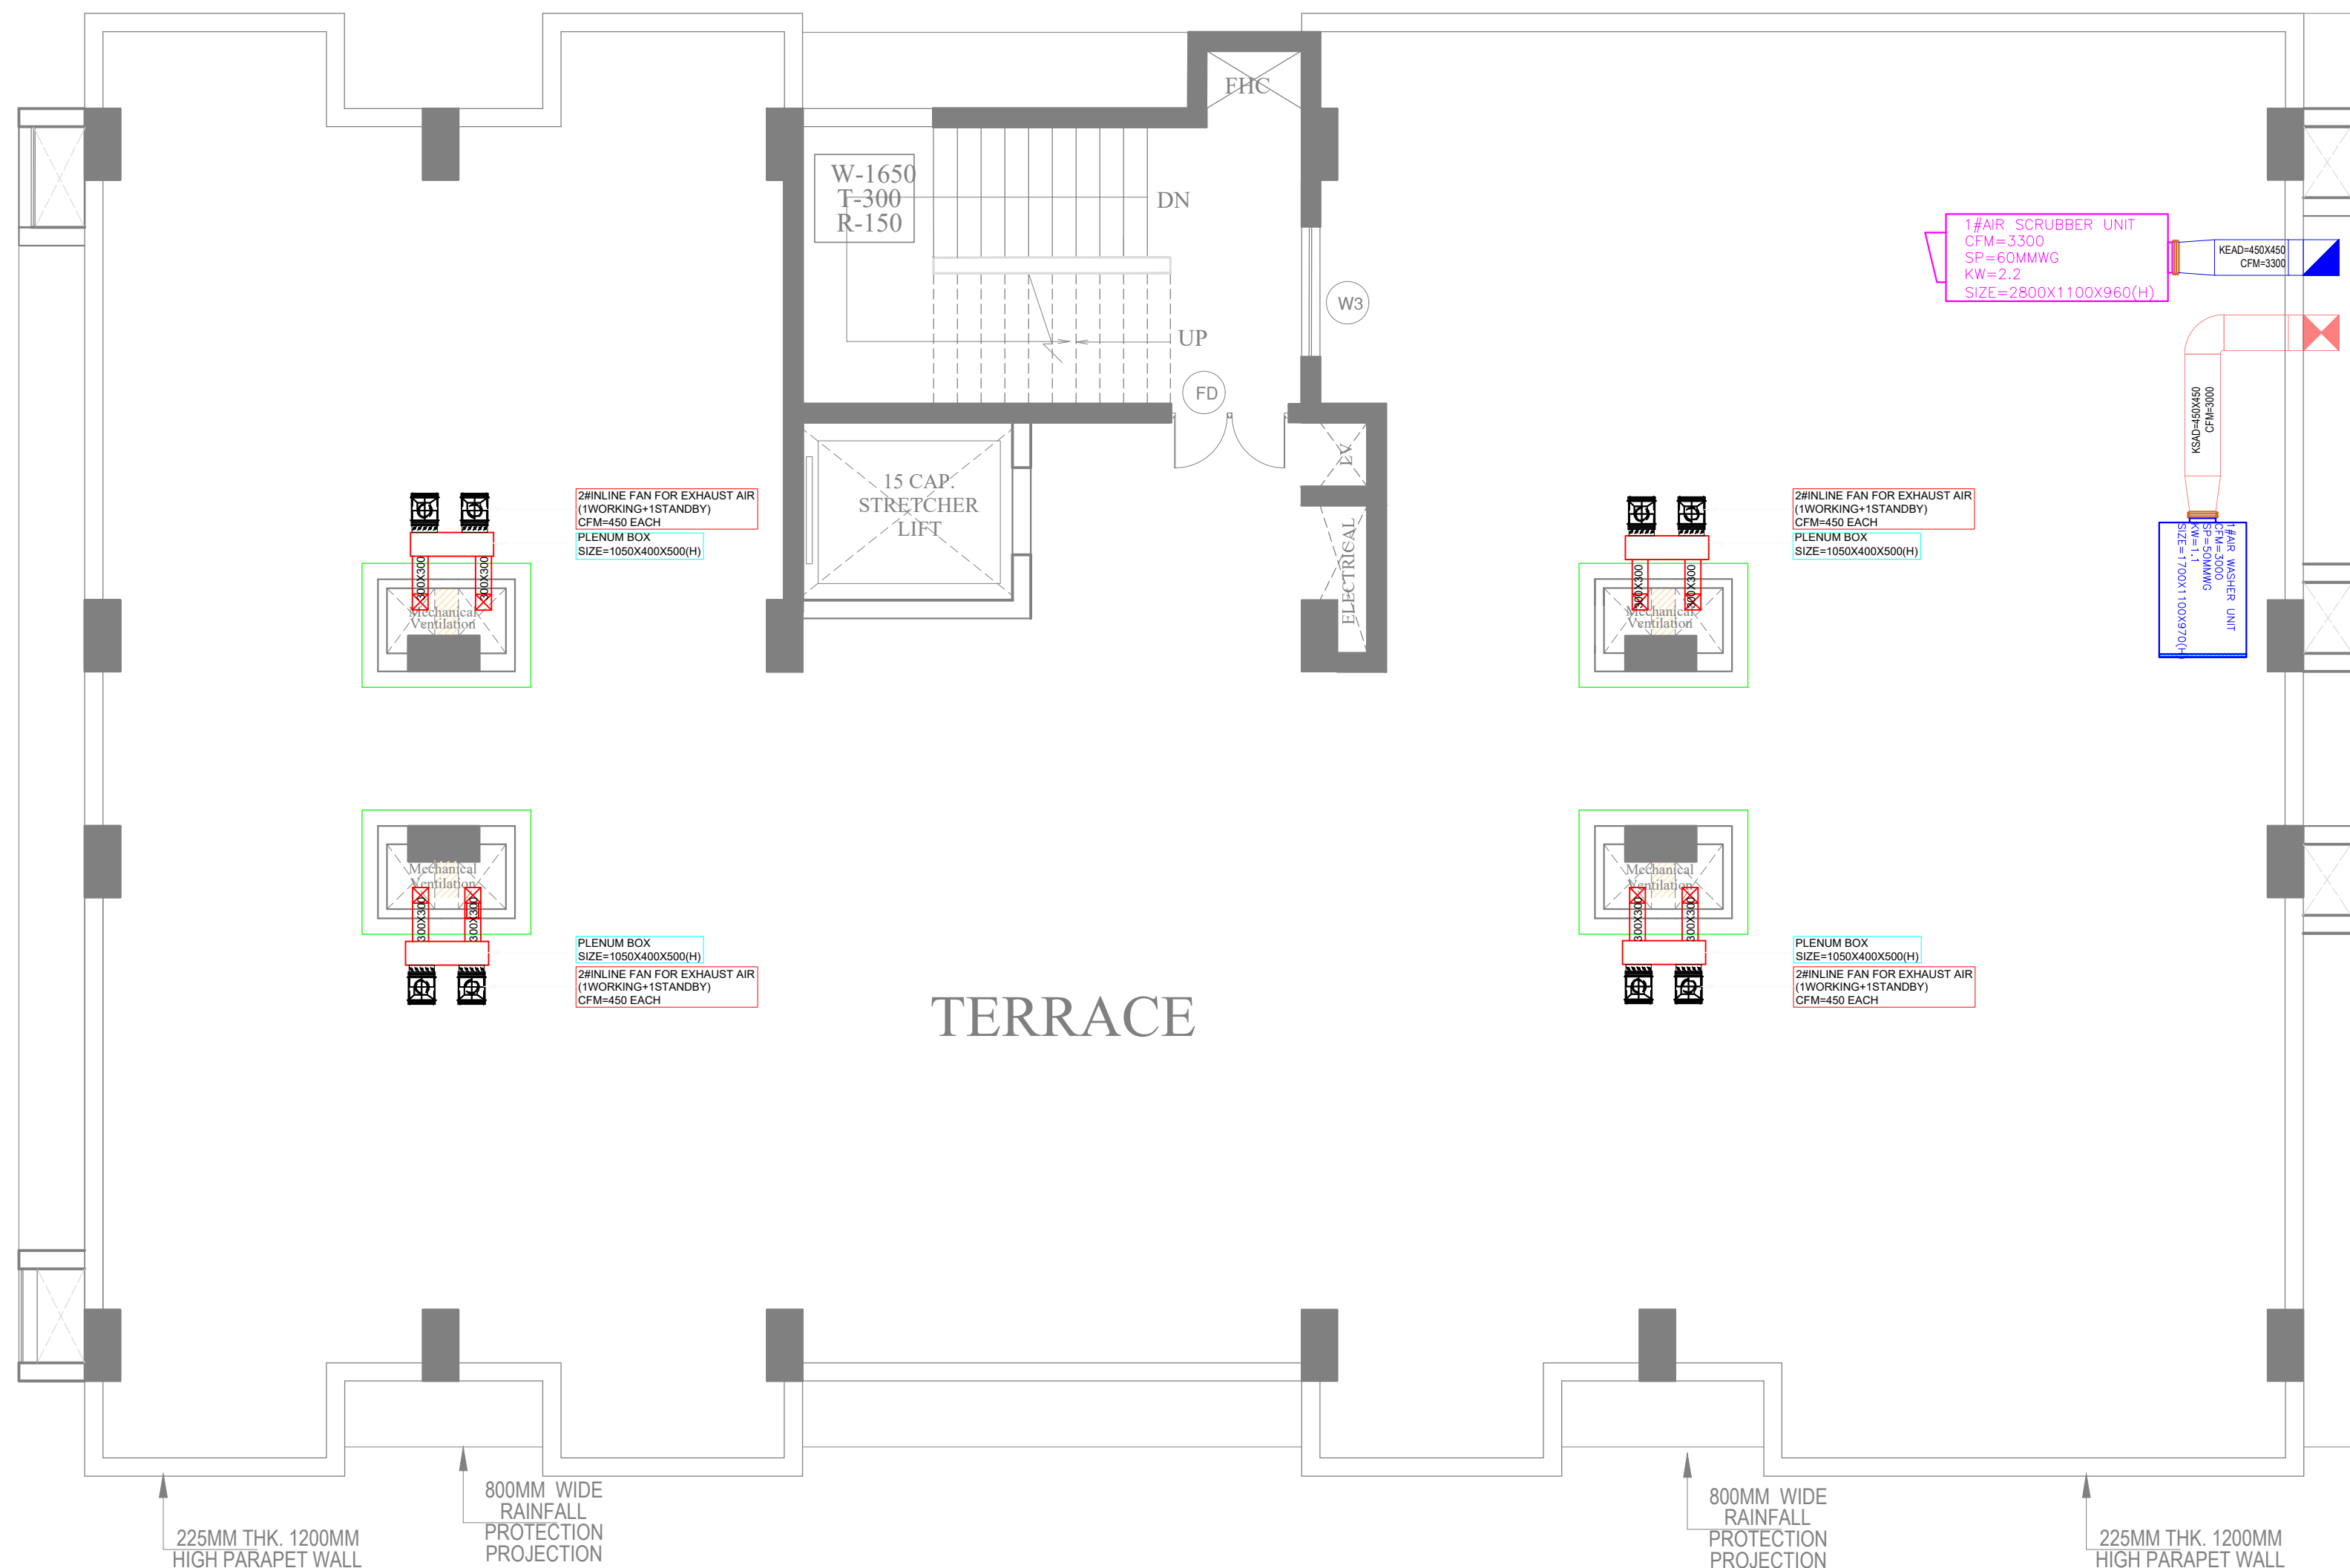

NOTES:-

1. ALL DIMENSIONS ARE IN MM; UNLESS NOTED OTHERWISE.
2. WRITTEN DIMENSIONS ARE TO BE FOLLOWED. DRAWINGS ARE NOT TO BE SCALED.
3. ANY DISCREPANCY IN THE DRAWING SHALL BE BROUGHT TO THE NOTICE OF THE ENGINEER-IN-CHARGE.
4. THIS DRAWING SHALL BE READ IN CONJUNCTION WITH OTHER RELEVANT DRAWINGS, TENDER DOCUMENT.
5. ALL ELECTRICAL WORKS SHALL BE COMPLETED AS PER CPWD SPECIFICATIONS, RELEVANT IS CODE & REGULATION OF THE ELECTRICAL AUTHORITIES ETC. AS REQUIRED.
6. EPC CONTRACTOR TO SUBMIT SHOP DRAWINGS FOR APPROVAL BEFORE EXECUTION OF WORK.
7. DISCREPANCY, IF ANY SHALL BE BROUGHT TO THE NOTICE OF ENGINEER-IN-CHARGE AND CLARIFICATION OBTAINED IN WRITING PRIOR TO EXECUTION OF THE WORK.

TENDER DRAWING

CLIENT



CONSULTANT



MEP CONSULTANT

PKV CONSULTING ENGINEERS(P)LTD.
C-815,DDA Flats,Loni Road,Delhi-110093
TELEFAX-011-22816297
E-mail:info@pkv.co.in
E-mail:pramod@pkv.co.in




JOB TITLE

BQ WORKMEN GROUP HOUSING
COMPLEX AT DULIAJAN ASSAM

DRAWING TITLE

TERRACE FLOOR HVAC PLAN
GUEST HOUSE

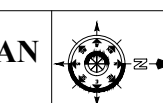

SCALE



DATE

DRG. NO.

NTS.




JULY 2025

RITES/BLD/HVAC/TEN/307

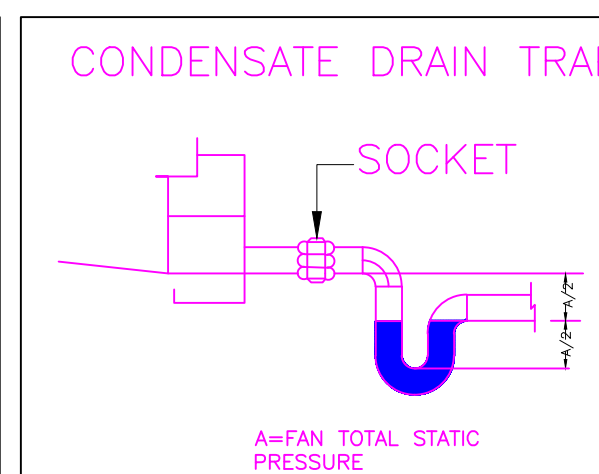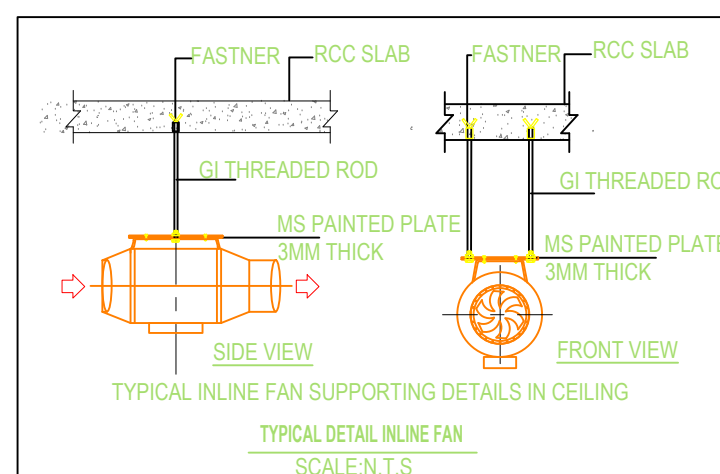

MECHANICAL LEGEND

SYMBOL	DESCRIPTION
	EXHUAUST AIR DUCT
	SPLIT HI WALL UNIT
	SPLIT OUTDOOR UNIT
	REFRIGERANT PIPE
	DRAIN PIPE
	PROPELLER FAN
	INLINE EXHAUST FAN
	EXHUAUST AIR GRILLE

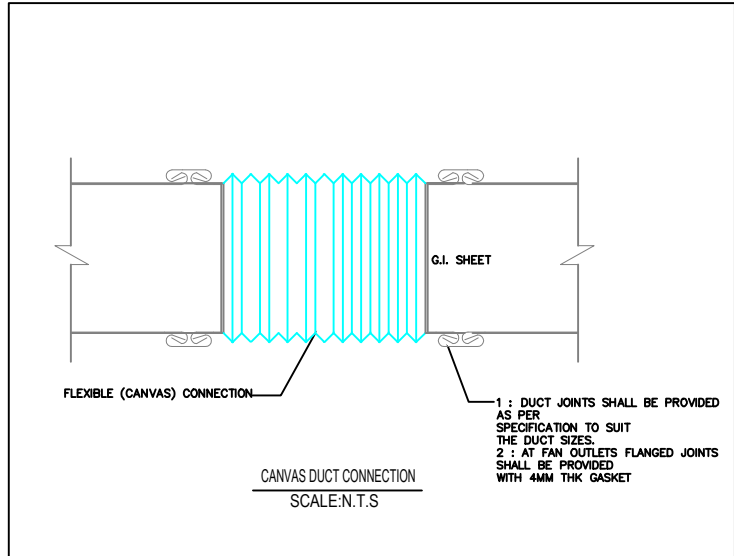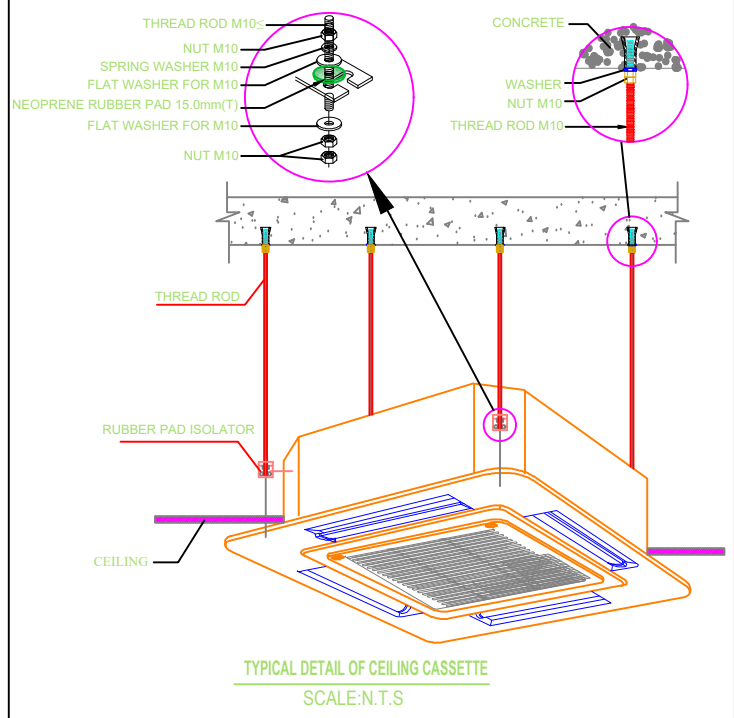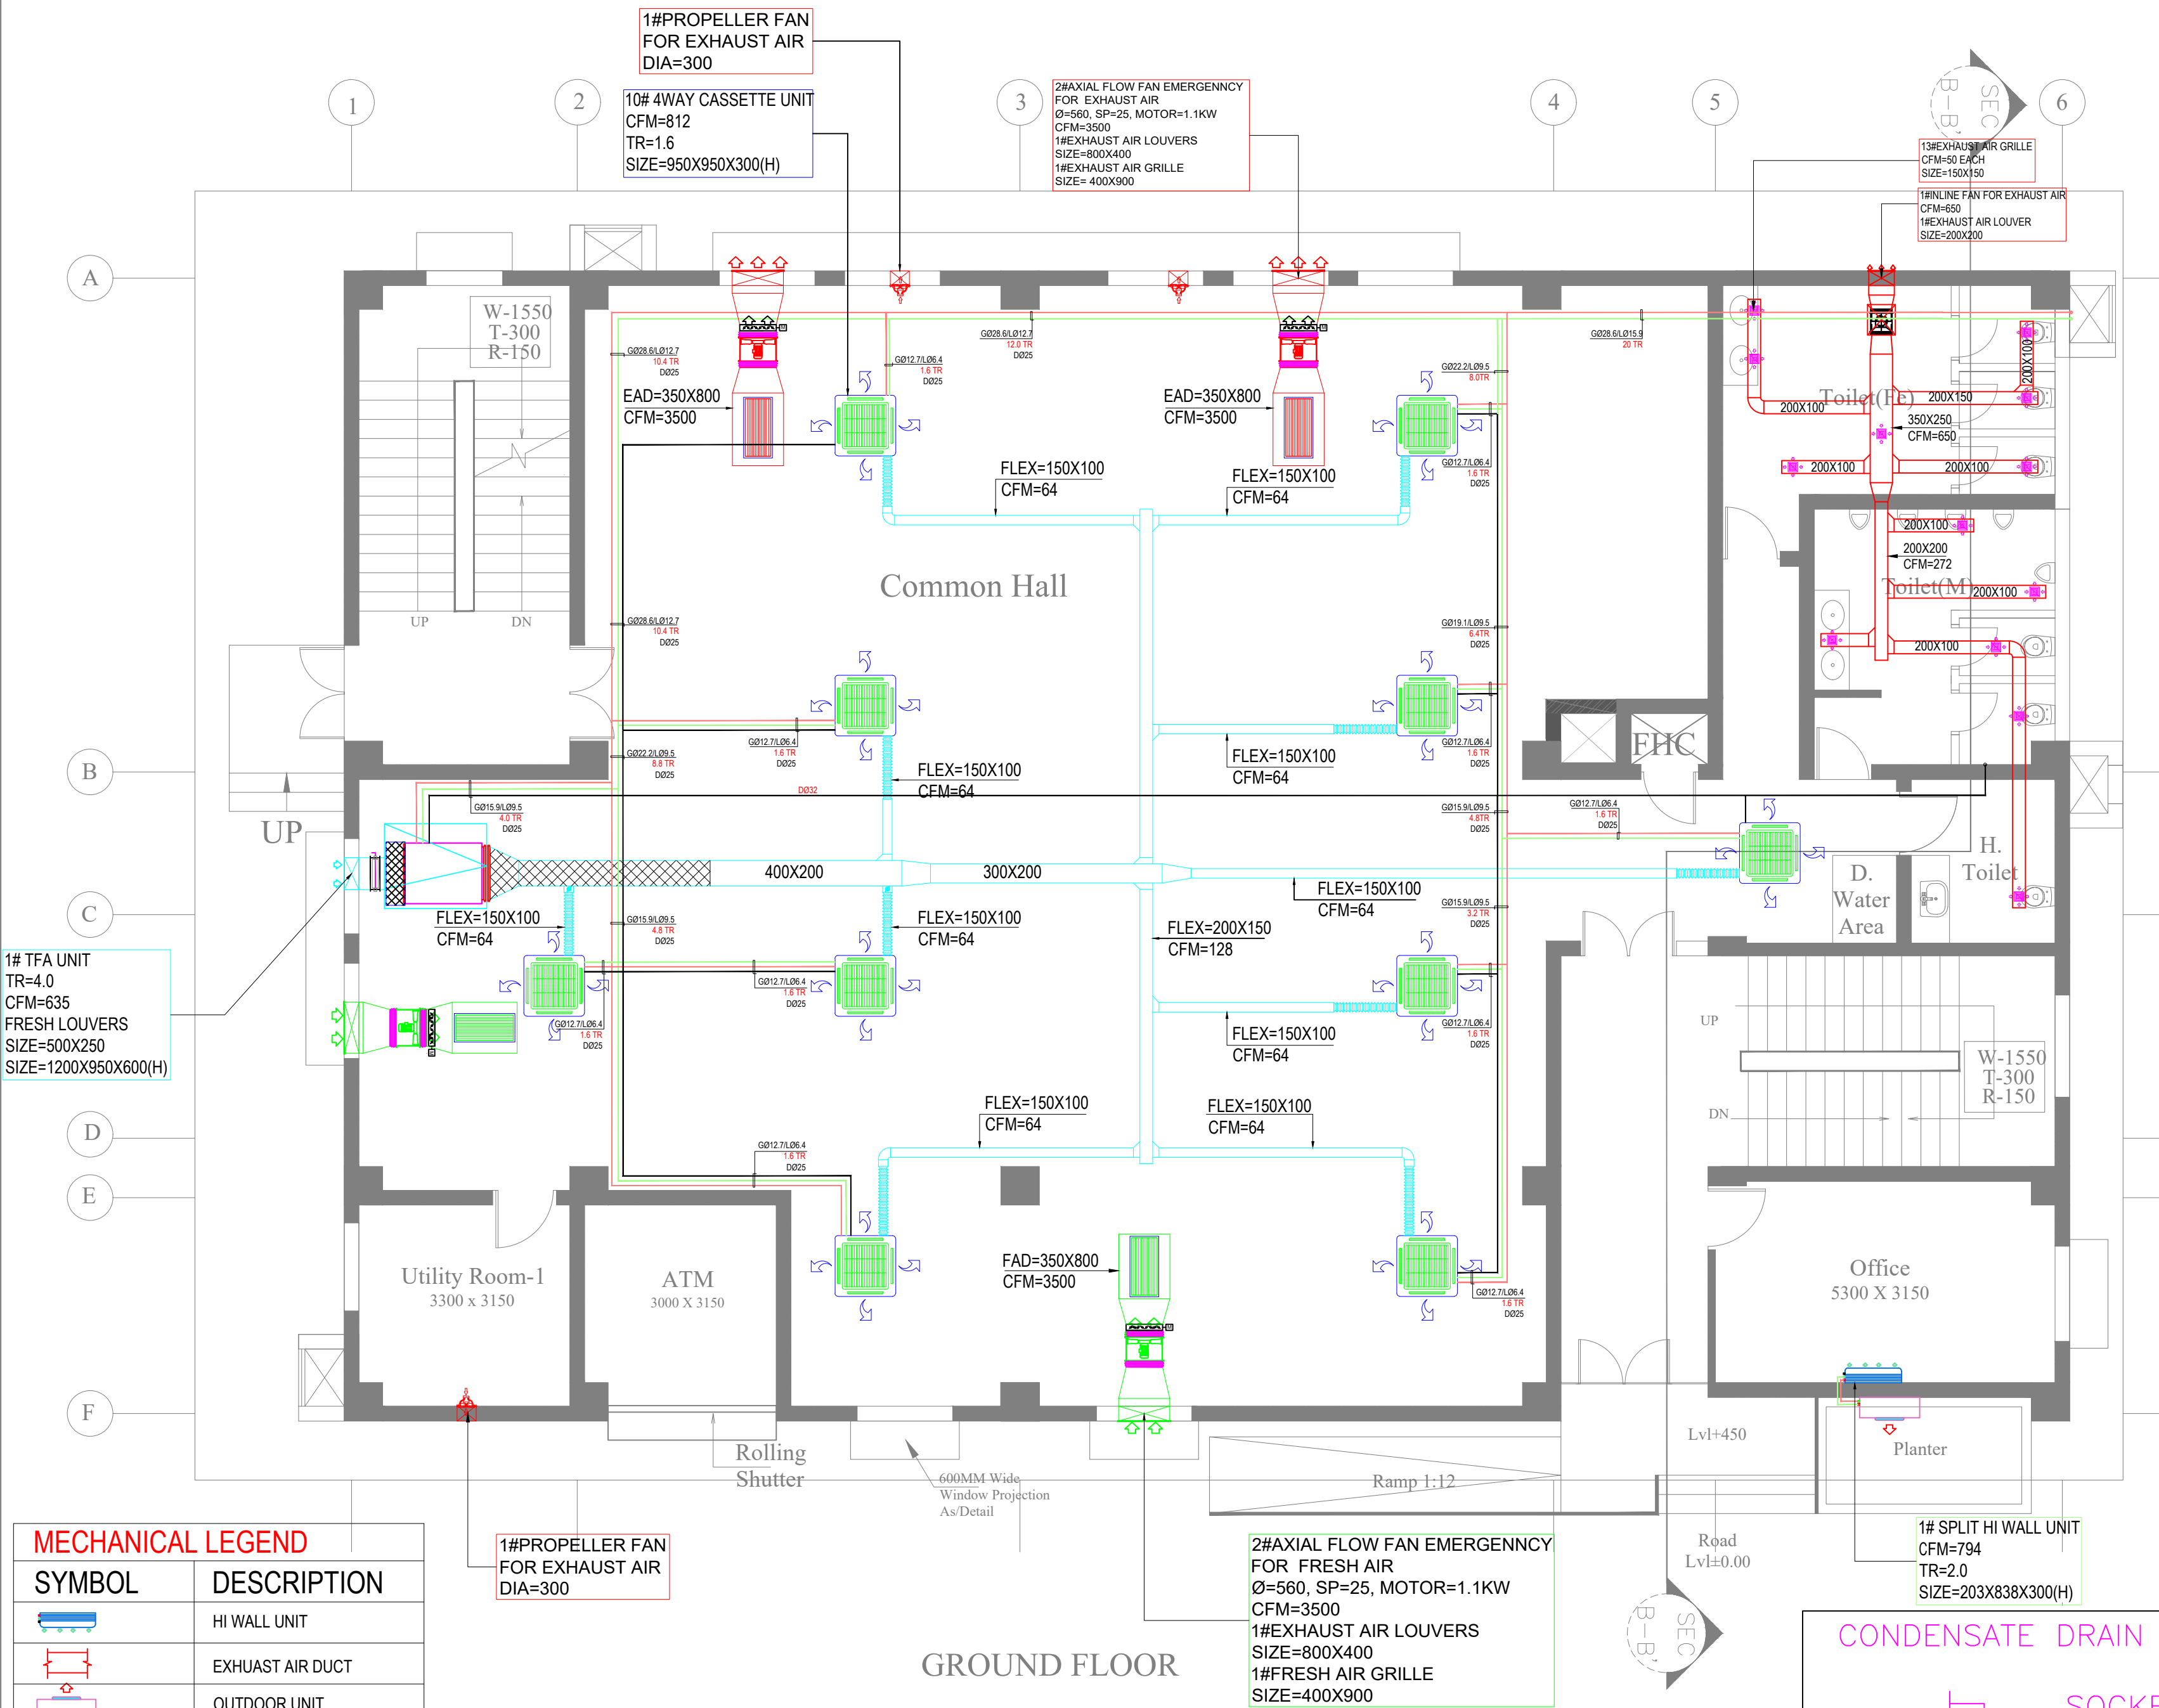



- NOTES: -
- ALL DIMENSIONS ARE IN MM. UNLESS NOTED OTHERWISE.
 - WRITTEN DIMENSIONS ARE TO BE FOLLOWED. DRAWINGS ARE NOT TO BE SCALED.
 - ANY DISCREPANCY IN THE DRAWING SHALL BE BROUGHT TO THE NOTICE OF THE ENGINEER-IN-CHARGE.
 - THIS DRAWING SHALL BE READ IN CONJUNCTION WITH OTHER RELEVANT DRAWINGS, TENDER DOCUMENT.
 - ALL ELECTRICAL WORKS SHALL BE COMPLETED AS PER CPWD SPECIFICATIONS RELEVANT IS CODE & REGULATION OF THE ELECTRICAL AUTHORITIES ETC. AS REQUIRED.
 - EPC CONTRACTOR TO SUBMIT SHOP DRAWINGS FOR APPROVAL BEFORE EXECUTION OF WORK.
 - DISCREPANCY, IF ANY SHALL BE BROUGHT TO THE NOTICE OF ENGINEER-IN-CHARGE AND CLARIFICATION OBTAINED IN WRITING PRIOR TO EXECUTION OF THE WORK.

TENDER DRAWING

CLIENT	OIL INDIA LIMITED (A Govt. of India Enterprise)	
CONSULTANT	IRITES THE INFRASTRUCTURE PEOPLE (A Govt. of India Enterprise)	
JOB TITLE	BQ WORKMEN GROUP HOUSING COMPLEX AT DULIAJAN ASSAM	
DRAWING TITLE	GROUND FLOOR HVAC PLAN COMMUNITY CENTRE	
SCALE	DATE	DRG. NO.
NTS	JULY 2025	MITES/BLD/HVAC/TEN/308

MECHANICAL LEGEND	
SYMBOL	DESCRIPTION
	HI WALL UNIT
	EXHAUST AIR DUCT
	OUTDOOR UNIT
	REFRIGERANT GAS PIPE
	REFRIGERANT LIQUID PIPE
	DRAIN PIPE
	PROPELLER FAN
	4 WAY CASSETTE UNIT

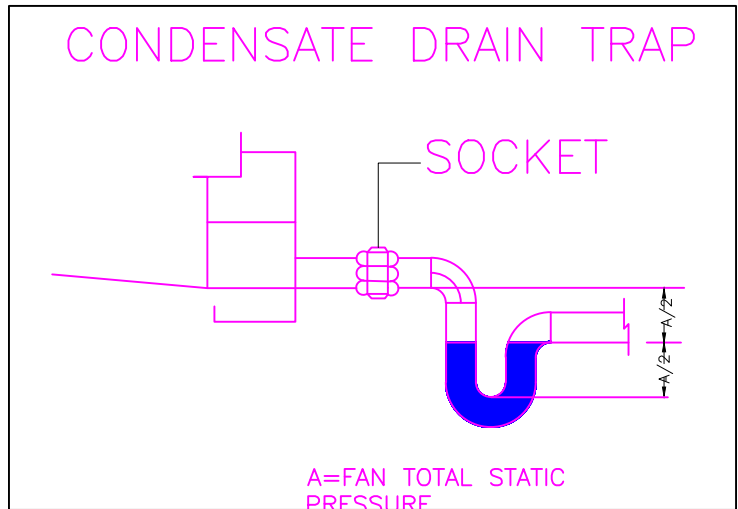

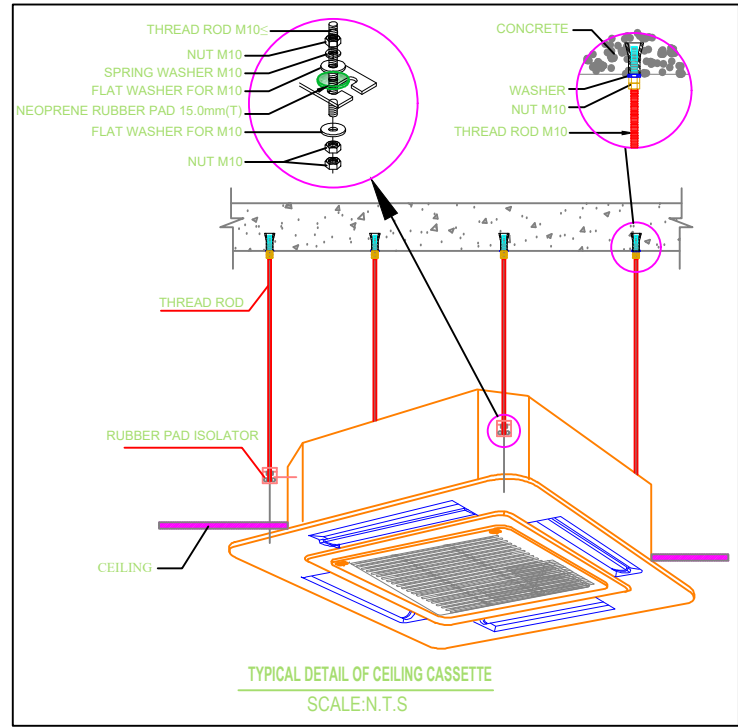

- NOTES:-
- ALL DIMENSIONS ARE IN MM. UNLESS NOTED OTHERWISE.
 - WRITTEN DIMENSIONS ARE TO BE FOLLOWED. DRAWINGS ARE NOT TO BE SCALED.
 - ANY DISCREPANCY IN THE DRAWING SHALL BE BROUGHT TO THE NOTICE OF THE ENGINEER-IN-CHARGE.
 - THIS DRAWING SHALL BE READ IN CONJUNCTION WITH OTHER RELEVANT DRAWINGS, TENDER DOCUMENT.
 - ALL ELECTRICAL WORKS SHALL BE COMPLETED AS PER CPWD SPECIFICATIONS, RELEVANT IS CODE & REGULATION OF THE ELECTRICAL AUTHORITIES ETC. AS REQUIRED.
 - EPC CONTRACTOR TO SUBMIT SHOP DRAWINGS FOR APPROVAL BEFORE EXECUTION OF WORK.
 - DISCREPANCY, IF ANY SHALL BE BROUGHT TO THE NOTICE OF ENGINEER-IN-CHARGE AND CLARIFICATION OBTAINED IN WRITING PRIOR TO EXECUTION OF THE WORK.

TENDER DRAWING

CLIENT
OIL INDIA LIMITED
(A Govt. of India Enterprise)

CONSULTANT
IRITES
THE INFRASTRUCTURE PEOPLE
(A Govt. of India Enterprise)


JOB TITLE
**BQ WORKMEN GROUP HOUSING
COMPLEX AT DULIAJAN ASSAM**

DRAWING TITLE
**FIRST FLOOR HVAC PLAN
COMMUNITY CENTRE**

SCALE	DATE	DRG. NO.
NTS	JULY 2025	MITES/BLD/HVAC/TEN/309


MECHANICAL LEGEND	
SYMBOL	DESCRIPTION
	HI WALL UNIT
	EXHAUST AIR DUCT
	OUTDOOR UNIT
	REFRIGERANT GAS PIPE
	REFRIGERANT LIQUID PIPE
	DRAIN PIPE
	PROPELLER FAN
	4 WAY CASSETTE UNIT

2#4WAY CASSETTE UNIT
CFM=812
TR=1.6
SIZE=950X950X300(H)

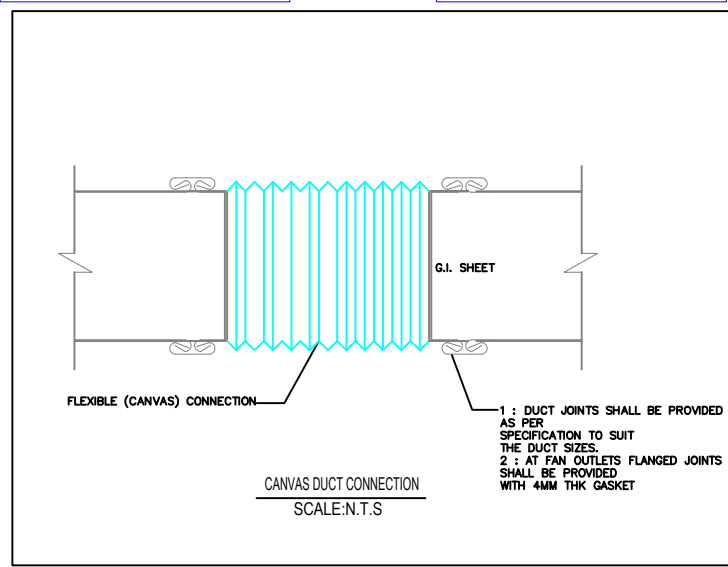


4#4WAY CASSETTE UNIT
CFM=830
TR=2.0
SIZE=950X950X300(H)




CONDENSATE DRAIN TRAP

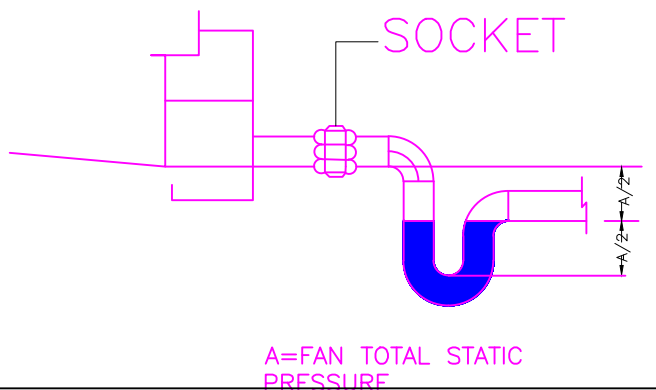

FIRST FLOOR

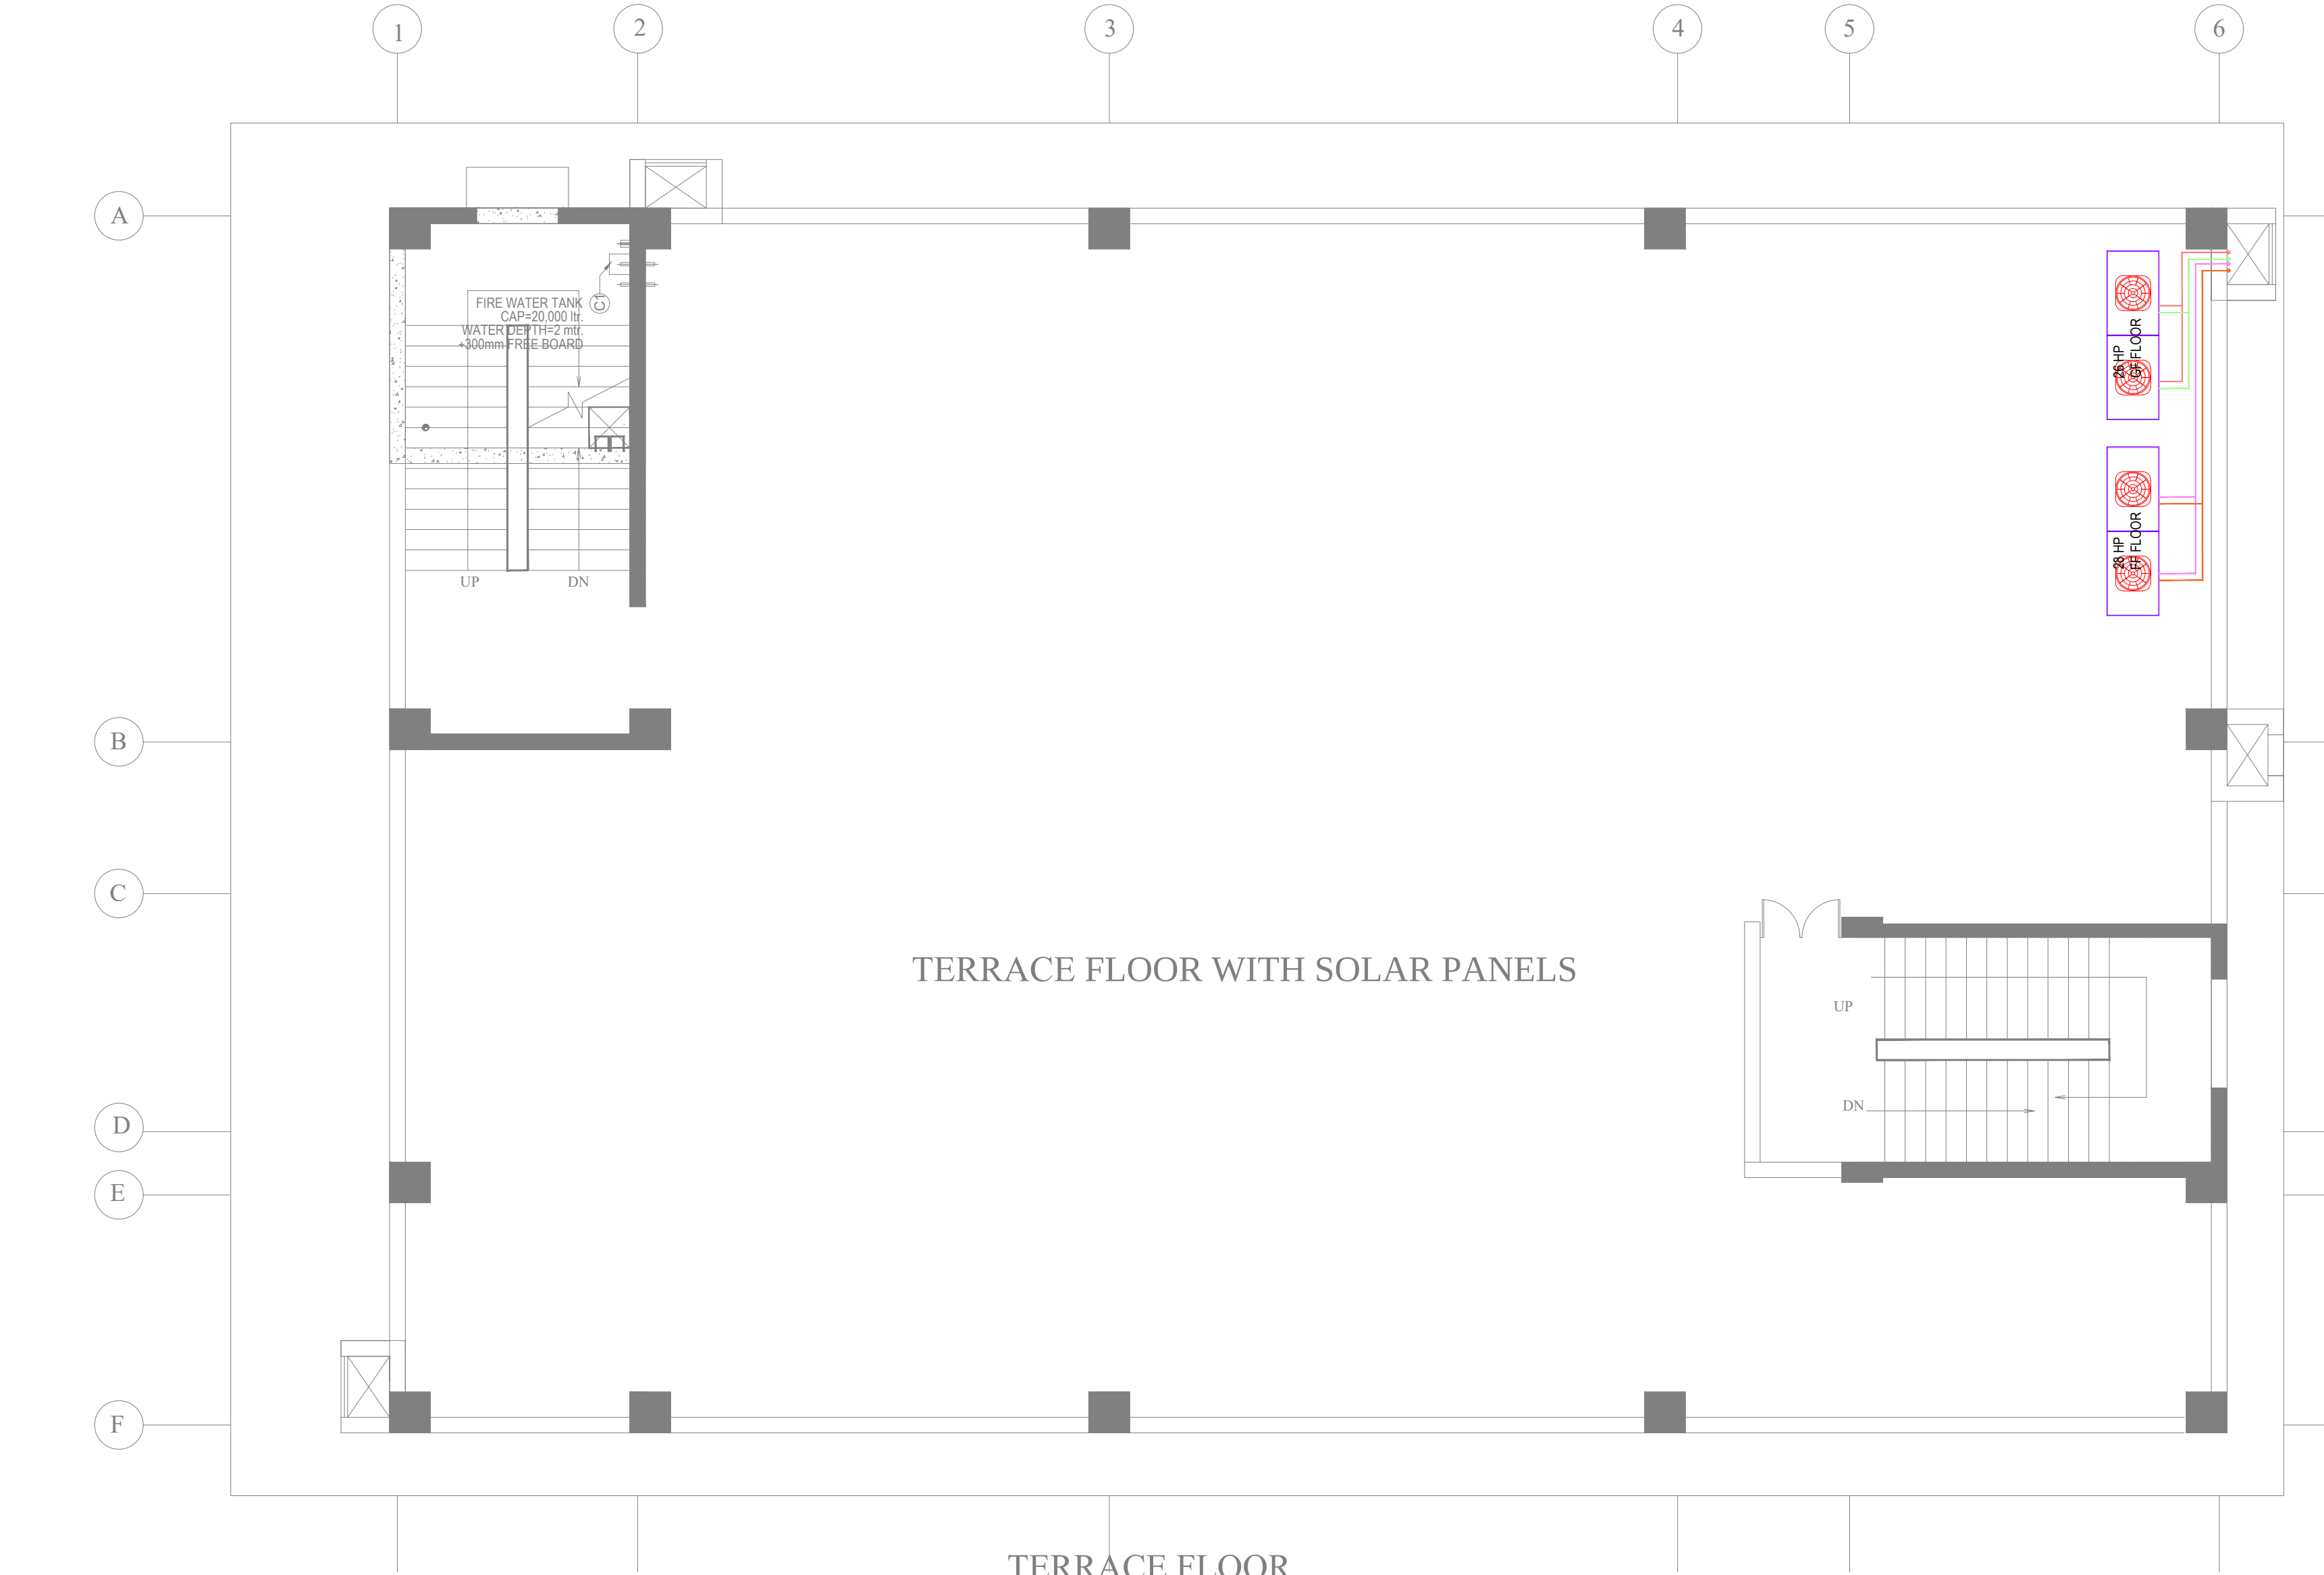


MECHANICAL LEGEND	
SYMBOL	DESCRIPTION
	HI WALL UNIT
	EXHUAUST AIR DUCT
	OUTDOOR UNIT
	REFRIGERANT GAS PIPE
	REFRIGERANT LIQUID PIPE
	DRAIN PIPE
	PROPELLER FAN
	4 WAY CASSETTE UNIT

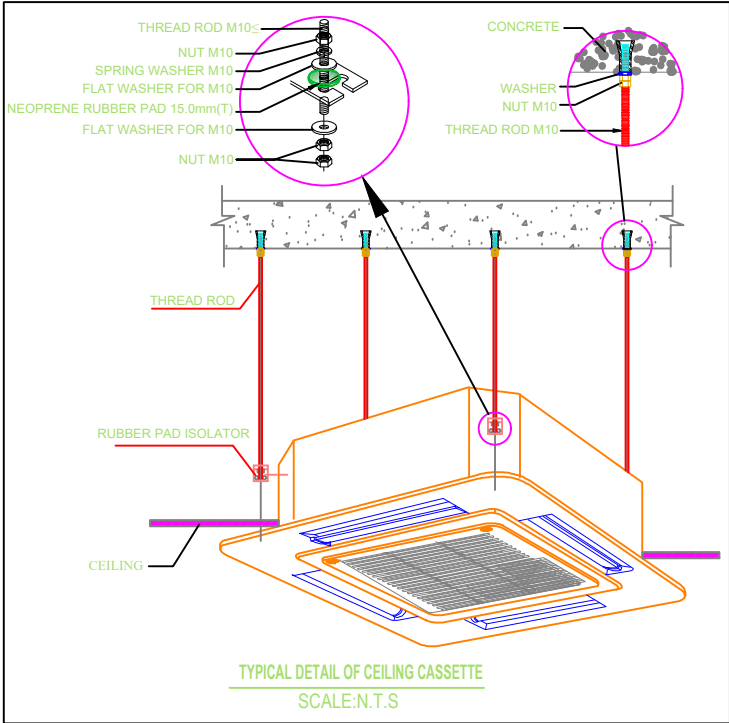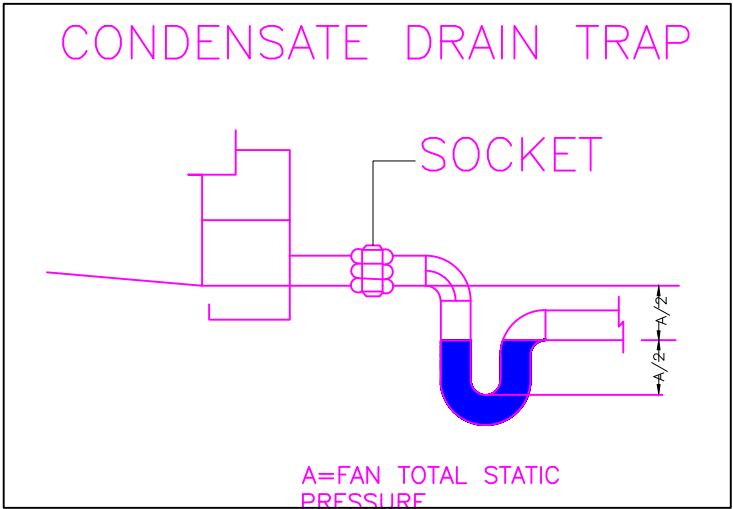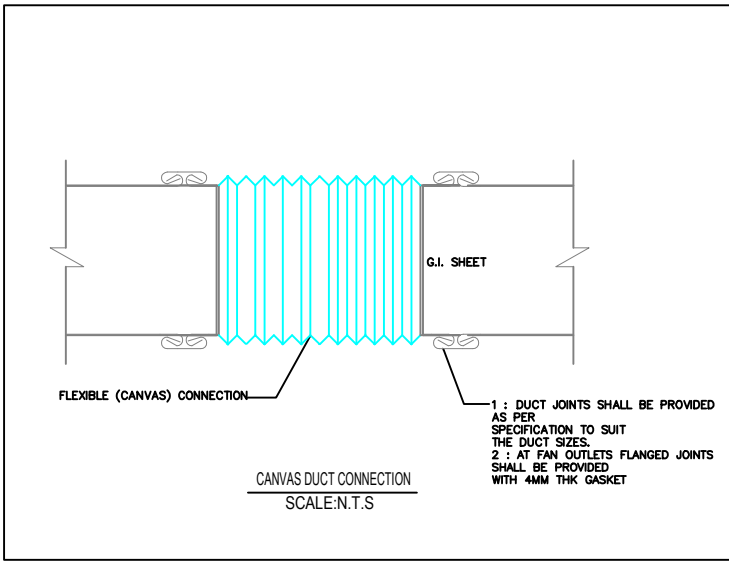


NOTES:—	
1.	ALL DIMENSIONS ARE IN MM, UNLESS NOTED OTHERWISE.
2.	WRITTEN DIMENSIONS ARE TO BE FOLLOWED. DRAWINGS ARE NOT TO BE SCALED.
3.	ANY DISCREPANCY IN THE DRAWING SHALL BE BROUGHT TO THE NOTICE OF THE ENGINEER-IN-CHARGE.
4.	THIS DRAWING SHALL BE READ IN CONJUNCTION WITH OTHER RELEVANT DRAWINGS, TENDER DOCUMENT.
5.	ALL ELECTRICAL WORKS SHALL BE COMPLETED AS PER CPWD SPECIFICATIONS,RELEVANT IS CODE & REGULATION OF THE ELECTRICAL AUTHORITIES ETC. AS REQUIRED.
6.	EPC CONTRACTOR TO SUBMIT SHOP DRAWINGS FOR APPROVAL BEFORE EXECUTION OF WORK.
7.	DISCREPANCY, IF ANY SHALL BE BROUGHT TO THE NOTICE OF ENGINEER IN CHARGE AND CLARIFICATION OBTAINED IN WRITING PRIOR TO EXECUTION OF THE WORK.

TENDER DRAWING		
CLIENT		
CONSULTANT		
JOB TITLE		
BQ WORKMEN GROUP HOUSING COMPLEX AT DULIAJAN ASSAM		
DRAWING TITLE		
TERRACE FLOOR HVAC PLAN COMMUNITY CENTRE		
SCALE	DATE	DRG. NO.
NTS	JULY2025	RITES/BLD/HVAC/TEN/310

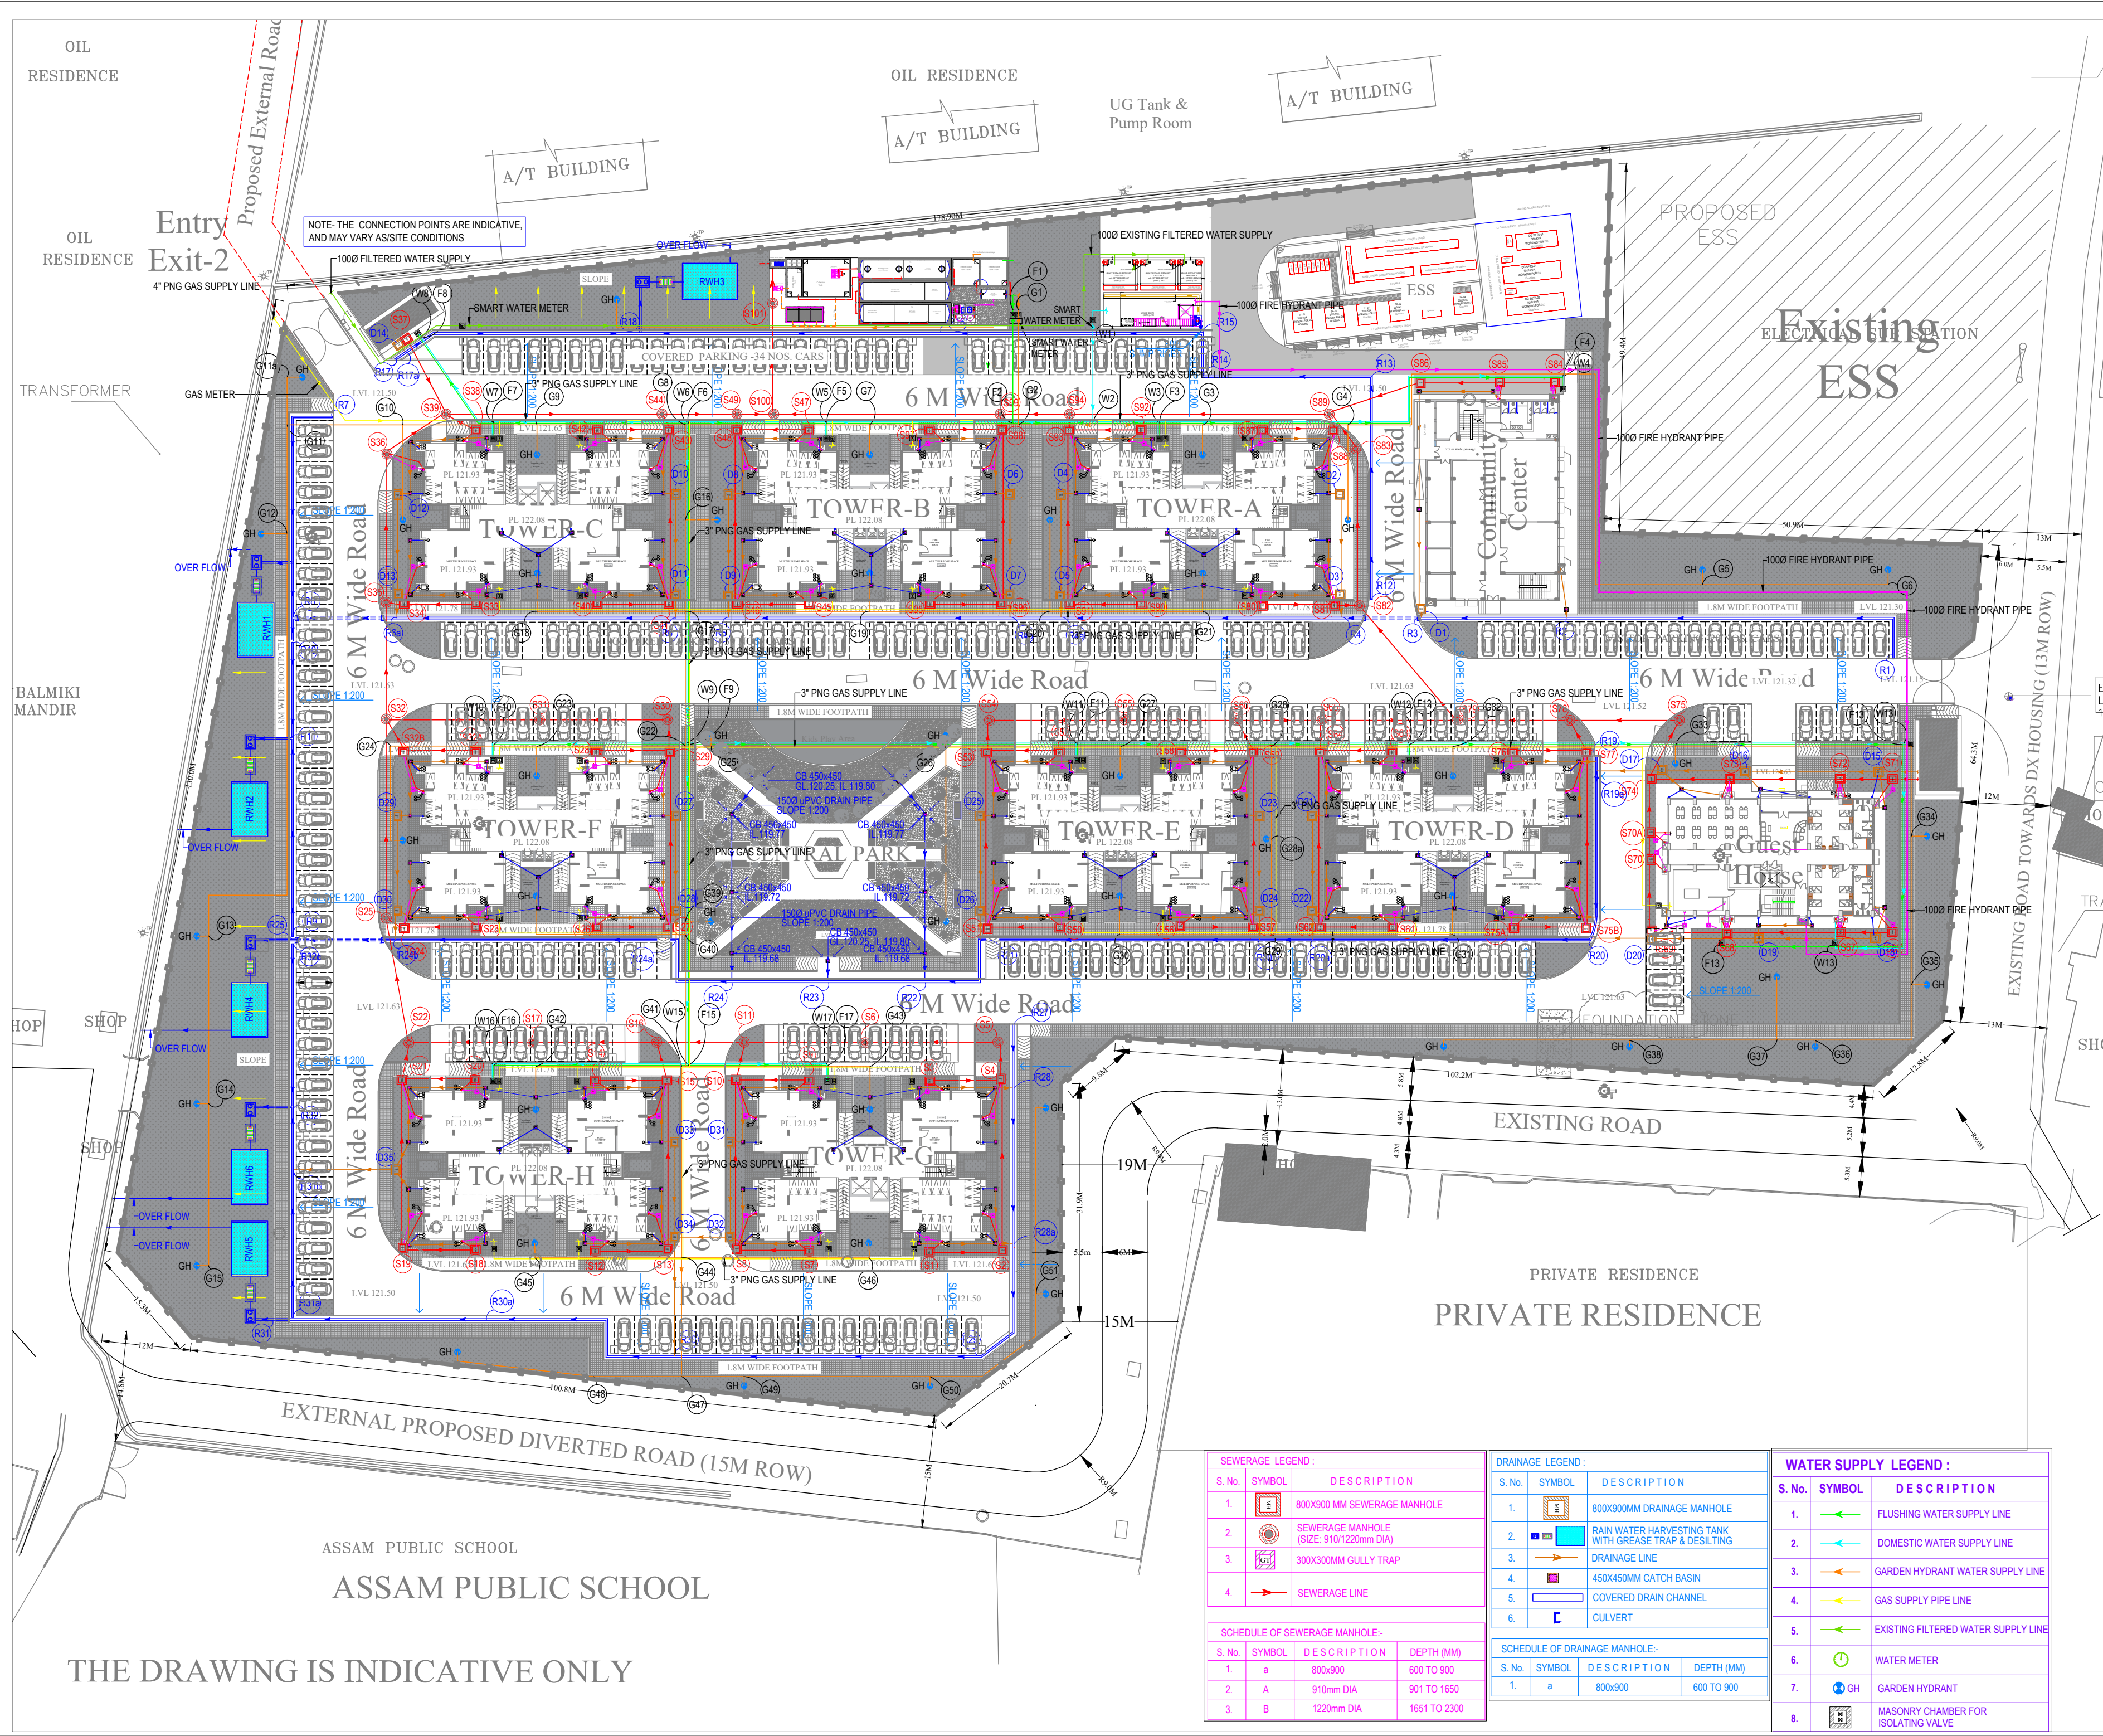

PRIVATE RESIDENCE

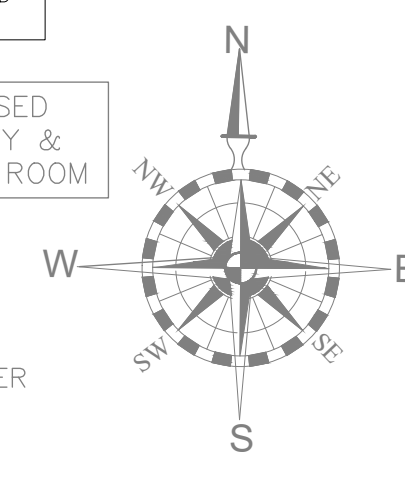

- NOTES:-
- 1. ALL DIMENSIONS ARE IN MM; UNLESS NOTED OTHERWISE.
 - 2. WRITTEN DIMENSIONS ARE TO BE FOLLOWED. DRAWINGS ARE NOT TO BE SCALED.
 - 3. ANY DISCREPANCY IN THE DRAWING SHALL BE BROUGHT TO THE NOTICE OF THE ENGINEER.
 - 4. THIS DRAWING SHALL BE READ IN CONJUNCTION WITH OTHER RELEVANT DRAWING TENDER DOCUMENT.
 - 5. DRAWINGS ARE INDICATIVE IN NATURE AND REPRESENT THE MINIMUM REQUIREMENTS. THE CONTRACTOR SHALL ENSURE COMPLIANCE WITH ALL APPLICABLE STANDARDS AND SITE CONDITIONS.
 - 6. WATER SUPPLY AND GAS LINE CONNECTIONS SHALL BE MADE FROM THE NEAREST AVAILABLE SOURCE POINTS AT SITE, AS PER ACTUAL CONDITIONS AND IN COORDINATION WITH LOCAL UTILITY AUTHORITIES.

TENDER DRAWING

CLIENT
 OIL INDIA LIMITED
(A Govt. of India Enterprise)

CONSULTANT
 RITES
THE INFRASTRUCTURE PEOPLE
(A Govt. of India Enterprise)

MEP CONSULTANT
 PKV CONSULTING ENGINEERS (P) LTD.
815 - C DDA FLATS
EAST OF LONI ROAD DELHI - 110093
email:-info@pkv.co.in



JOB TITLE		
BQ WORKMEN GROUP HOUSING COMPLEX AT DULIAJAN ASSAM		
DRAWING TITLE		
EXTERNAL PLUMBING SERVICES COORDINATED LAYOUT		
SCALE	DATE	DRG. NO.
NTS	JULY 2025	RITES/BLD/DR/TEN/401

SEWERAGE LEGEND :			
S. No.	SYMBOL	DESCRIPTION	
1.		800X900 MM SEWERAGE MANHOLE	
2.		SEWERAGE MANHOLE (SIZE: 910/1220mm DIA)	
3.		300X300MM GULLY TRAP	
4.		SEWERAGE LINE	
SCHEDULE OF SEWERAGE MANHOLE:-			
S. No.	SYMBOL	DESCRIPTION	DEPTH (MM)
1.	a	800x900	600 TO 900
2.	A	910mm DIA	901 TO 1650
3.	B	1220mm DIA	1651 TO 2300

DRAINAGE LEGEND :			
S. No.	SYMBOL	DESCRIPTION	
1.		800X900MM DRAINAGE MANHOLE	
2.		RAIN WATER HARVESTING TANK WITH GREASE TRAP & DESILTING	
3.		DRAINAGE LINE	
4.		450X450MM CATCH BASIN	
5.		COVERED DRAIN CHANNEL	
6.		CULVERT	
SCHEDULE OF DRAINAGE MANHOLE:-			
S. No.	SYMBOL	DESCRIPTION	DEPTH (MM)
1.	a	800x900	600 TO 900

WATER SUPPLY LEGEND :		
S. No.	SYMBOL	DESCRIPTION
1.		FLUSHING WATER SUPPLY LINE
2.		DOMESTIC WATER SUPPLY LINE
3.		GARDEN HYDRANT WATER SUPPLY LINE
4.		GAS SUPPLY PIPE LINE
5.		EXISTING FILTERED WATER SUPPLY LINE
6.		WATER METER
7.		GARDEN HYDRANT
8.		MASONRY CHAMBER FOR ISOLATING VALVE

THE DRAWING IS INDICATIVE ONLY

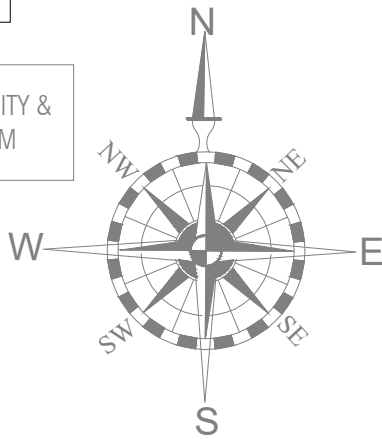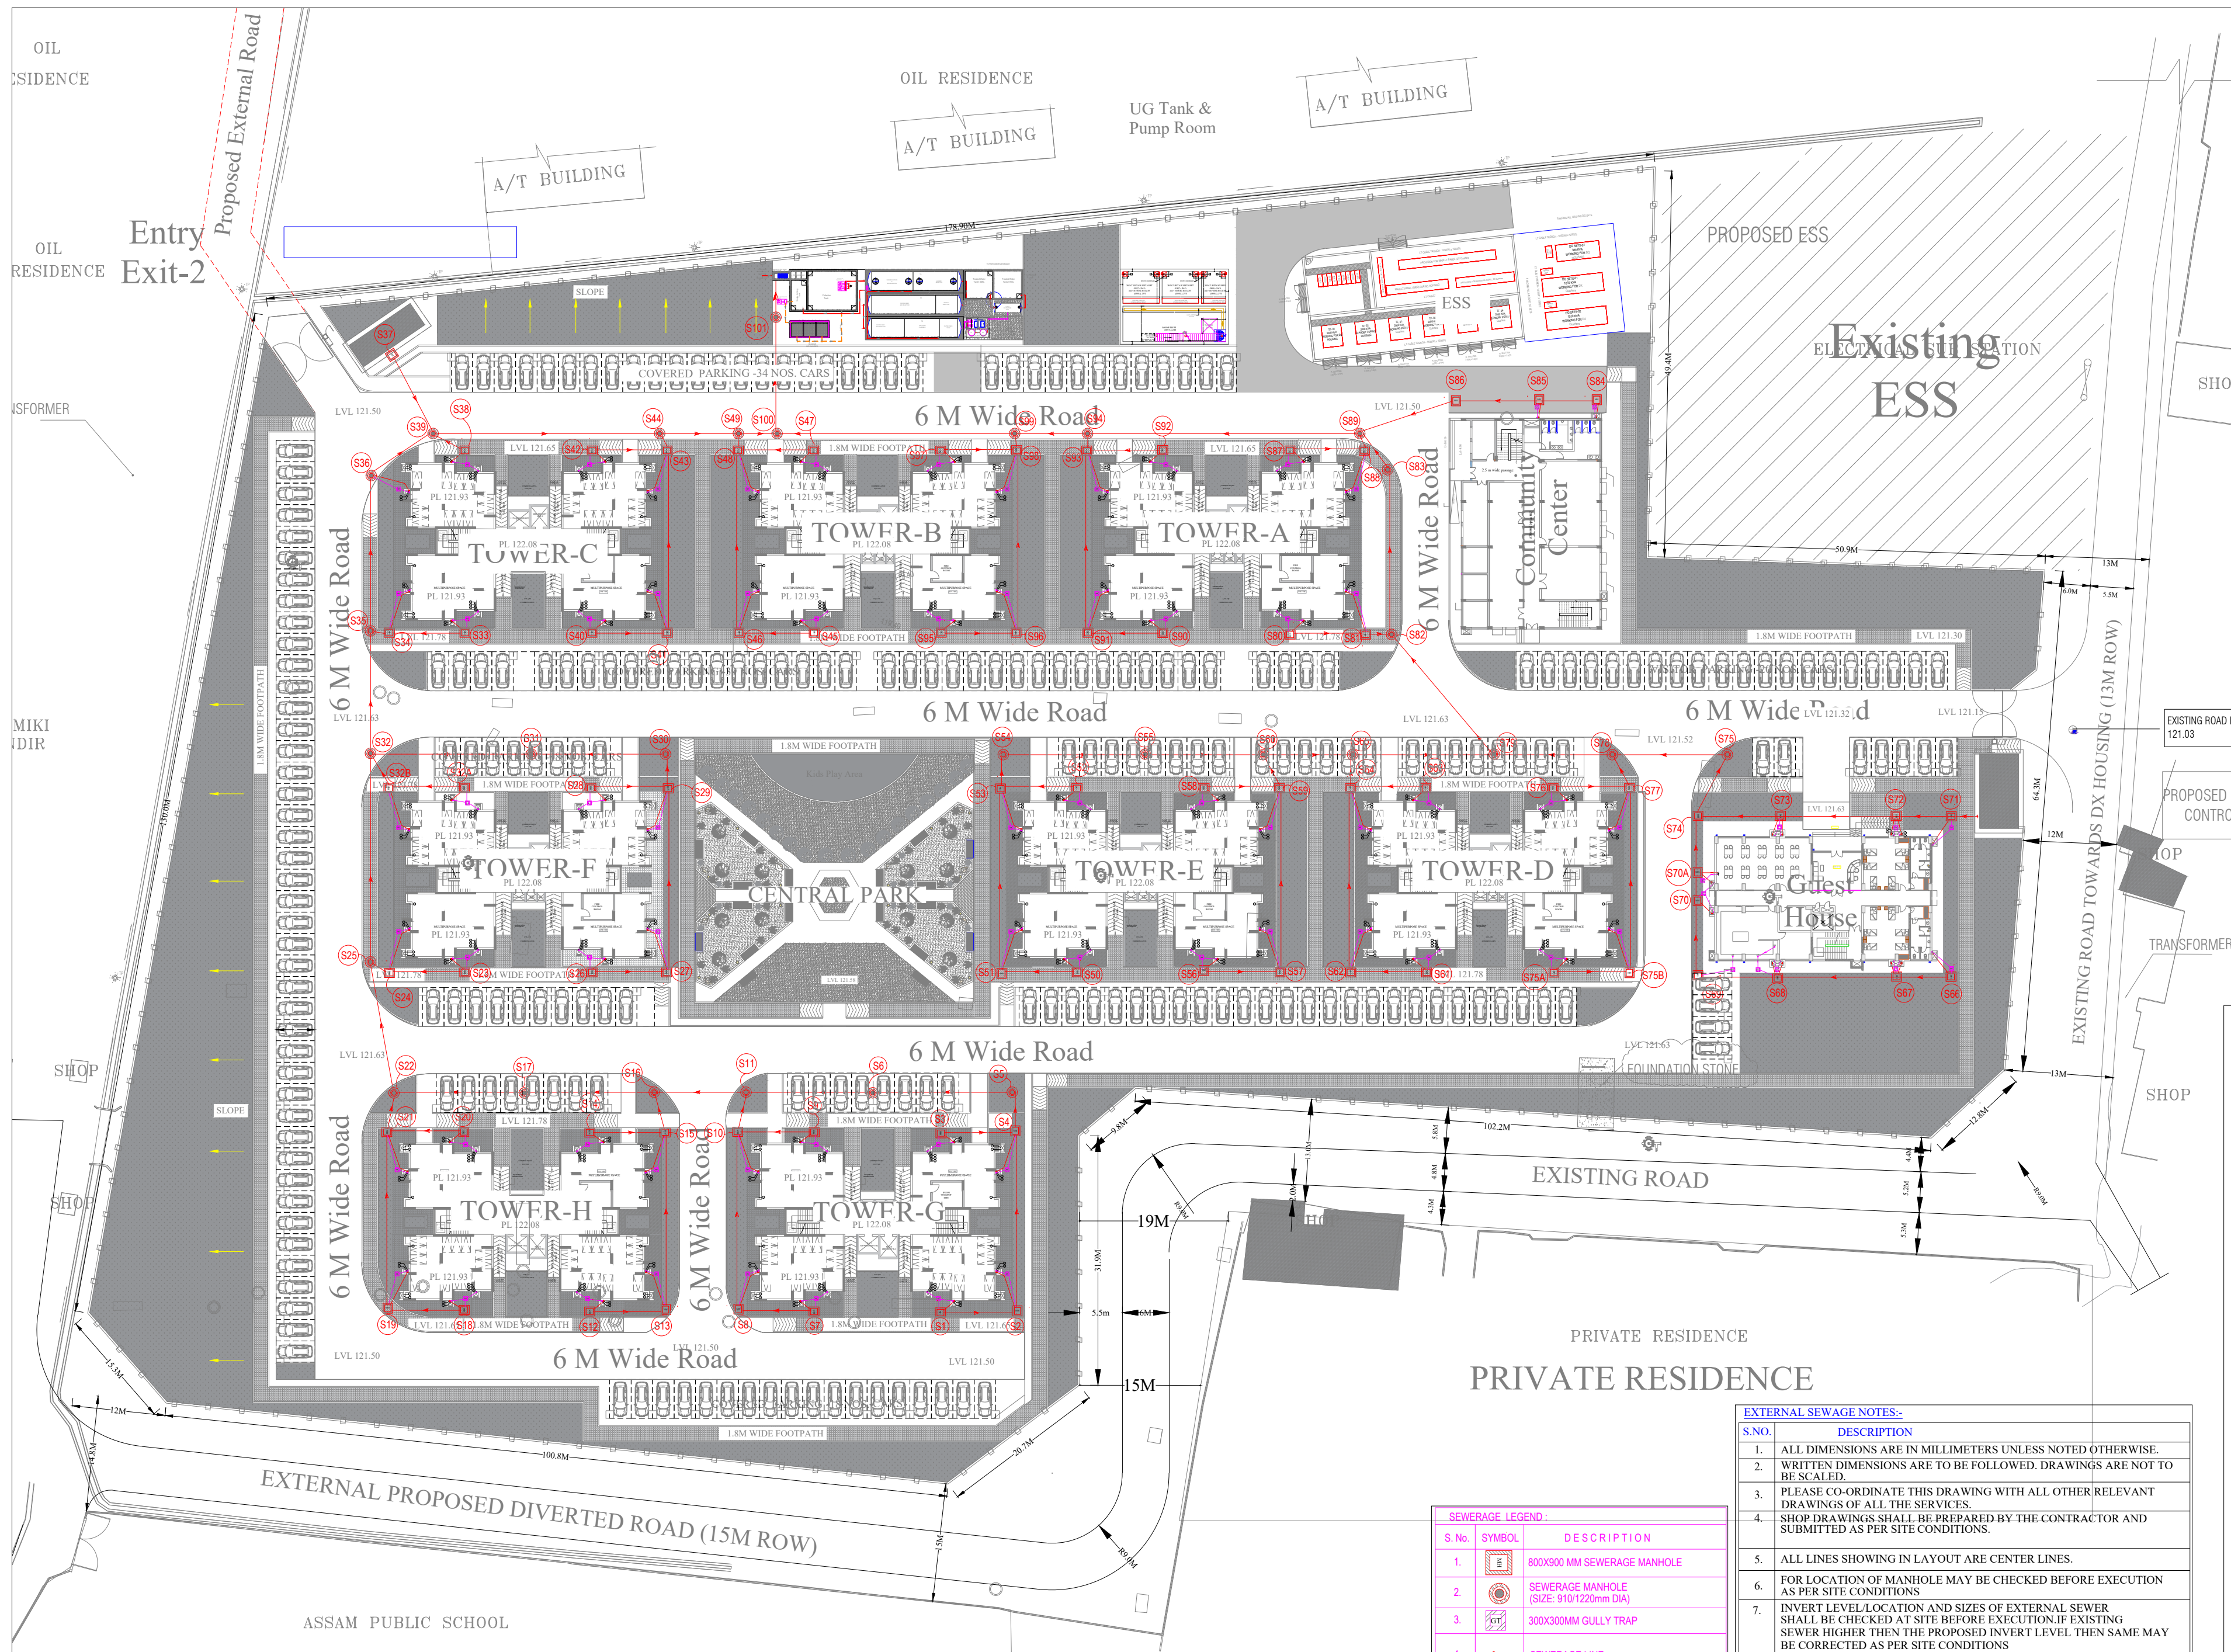

- NOTES:-
1. ALL DIMENSIONS ARE IN MM, UNLESS NOTED OTHERWISE.
 2. WRITTEN DIMENSIONS ARE TO BE FOLLOWED. DRAWINGS ARE NOT TO BE SCALED.
 3. ANY DISCREPANCY IN THE DRAWING SHALL BE BROUGHT TO THE NOTICE OF THE ENGINEER.
 4. THIS DRAWING SHALL BE READ IN CONJUNCTION WITH OTHER RELEVANT DRAWING, TENDER DOCUMENT.
 5. DRAWINGS ARE INDICATIVE IN NATURE AND REPRESENT THE MINIMUM REQUIREMENTS. THE CONTRACTOR SHALL ENSURE COMPLIANCE WITH ALL APPLICABLE STANDARDS AND SITE CONDITIONS.

TENDER DRAWING

REVISIONS

CLIENT

CONSULTANT

MEP CONSULTANT

PKV CONSULTING ENGINEERS (P) LTD.

815 - C DDA FLATS
EAST OF LONI ROAD DELHI - 110093
email:-info@pkv.co.in

BQ WORKMEN GROUP HOUSING
COMPLEX AT DULIAJAN ASSAM

EXTERNAL PLUMBING SERVICES
SEWERAGE LAYOUT


SCALE	DATE	DRG. NO.
NTS	JULY 2025	NTS/BLD/DR/TEN/402

EXTERNAL SEWERAGE NOTES:-	
S.NO.	DESCRIPTION
1.	ALL DIMENSIONS ARE IN MILLIMETERS UNLESS NOTED OTHERWISE.
2.	WRITTEN DIMENSIONS ARE TO BE FOLLOWED. DRAWINGS ARE NOT TO BE SCALED.
3.	PLEASE CO-ORDINATE THIS DRAWING WITH ALL OTHER RELEVANT DRAWINGS OF ALL THE SERVICES.
4.	SHOP DRAWINGS SHALL BE PREPARED BY THE CONTRACTOR AND SUBMITTED AS PER SITE CONDITIONS.
5.	ALL LINES SHOWING IN LAYOUT ARE CENTER LINES.
6.	FOR LOCATION OF MANHOLE MAY BE CHECKED BEFORE EXECUTION AS PER SITE CONDITIONS
7.	INVERT LEVEL/LOCATION AND SIZES OF EXTERNAL SEWER SHALL BE CHECKED AT SITE BEFORE EXECUTION. IF EXISTING SEWER HIGHER THEN THE PROPOSED INVERT LEVEL THEN SAME MAY BE CORRECTED AS PER SITE CONDITIONS
8.	ALL EXTERNAL SEWER LINE (MANHOLE TO MANHOLE CONNECTION) SHALL BE LAID IN DOUBLE WALL CORRUGATED DWV PIPE OF CLASS SN-8
9.	ALL SEWER LINE SHALL BE LAID ON PCC BED.
10.	ALL BURRIED PIPES SHALL BE TESTED FOR LEAKAGES AND STRAIGHTNESS AS PER SPECIFICATION.
11.	TRENCH SHALL BE REFILLED ONLY AFTER PIPE TESTING.
12.	THE DEPTH OF MANHOLE SHOULD BE MEASURED FROM F.G.L


SEWERAGE LEGEND :		
S. No.	SYMBOL	DESCRIPTION
1.		800X900 MM SEWERAGE MANHOLE
2.		SEWERAGE MANHOLE (SIZE: 910/1220mm DIA)
3.		300X300MM GULLY TRAP
4.		SEWERAGE LINE

SCHEDULE OF SEWERAGE MANHOLE:-			
S.No.	SYMBOL	DESCRIPTION	DEPTH (MM)
1.	a	800x900	600 TO 900
2.	A	910mm DIA	901 TO 1650
3.	B	1220mm DIA	1651 TO 2300

THE DRAWING IS INDICATIVE ONLY

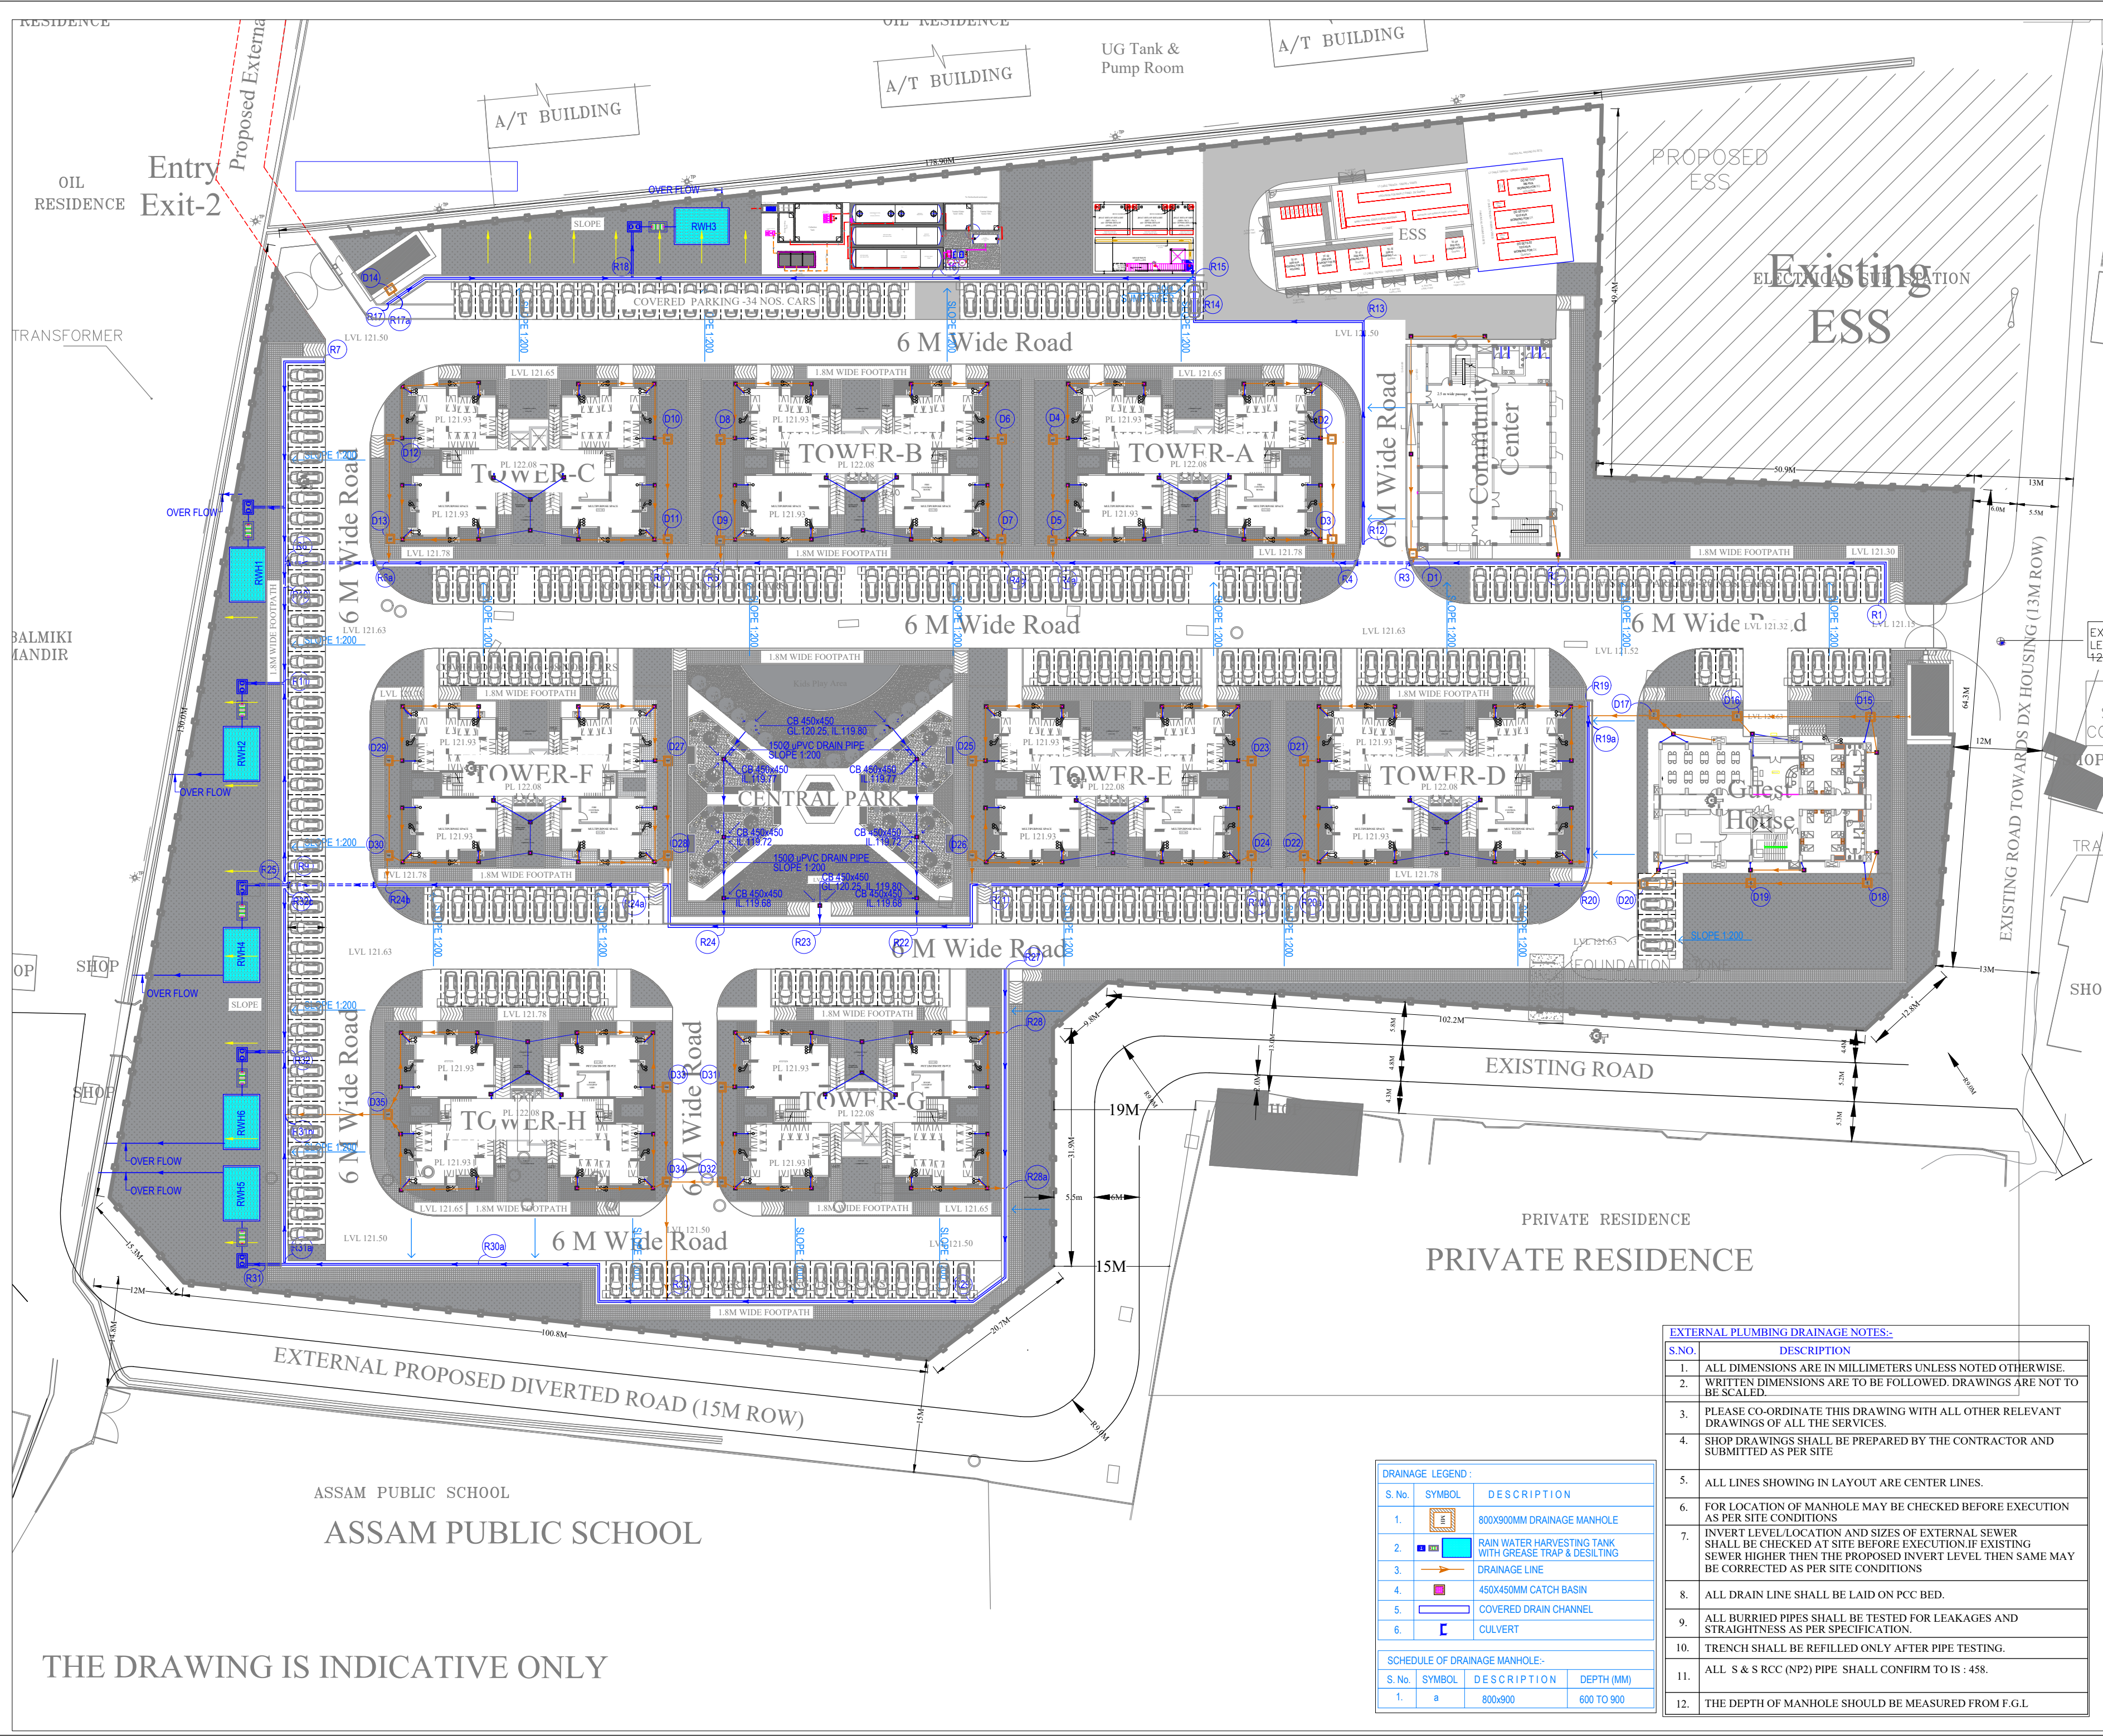

PRIVATE RESIDENCE

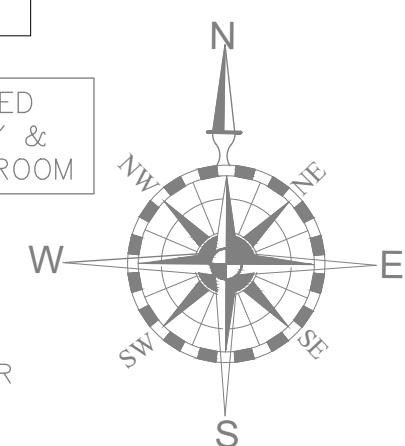

- NOTES:-
- 1. ALL DIMENSIONS ARE IN MM; UNLESS NOTED OTHERWISE.
 - 2. WRITTEN DIMENSIONS ARE TO BE FOLLOWED. DRAWINGS ARE NOT TO BE SCALED.
 - 3. ANY DISCREPANCY IN THE DRAWING SHALL BE BROUGHT TO THE NOTICE OF THE ENGINEER.
 - 4. THIS DRAWING SHALL BE READ IN CONJUNCTION WITH OTHER RELEVANT DRAWING, TENDER DOCUMENT.
 - 5. DRAWINGS ARE INDICATIVE IN NATURE AND REPRESENT THE MINIMUM REQUIREMENTS, THE CONTRACTOR SHALL ENSURE COMPLIANCE WITH ALL APPLICABLE STANDARDS AND SITE CONDITIONS.
 - 6. WATER SUPPLY AND GAS LINE CONNECTIONS SHALL BE MADE FROM THE NEAREST AVAILABLE SOURCE POINTS AT SITE, AS PER ACTUAL CONDITIONS AND IN COORDINATION WITH LOCAL UTILITY AUTHORITIES.

TENDER DRAWING

CLIENT	 OIL INDIA LIMITED (A Govt. of India Enterprise)	
CONSULTANT	 RITES THE INFRASTRUCTURE PEOPLE (A Govt. of India Enterprise)	
MEP CONSULTANT	 PKV CONSULTING ENGINEERS (P) LTD. 815 - C DDA FLATS EAST OF LONI ROAD DELHI - 110093 email:-info@pkv.co.in	
JOB TITLE	BQ WORKMEN GROUP HOUSING COMPLEX AT DULIAJAN ASSAM	
DRAWING TITLE	EXTERNAL PLUMBING SERVICES DRAINAGE LAYOUT	
SCALE	DATE	DRG. NO.
NTS	JULY 2025	RITES/BLD/DR/EN/403

EXTERNAL PLUMBING DRAINAGE NOTES:-	
S.NO.	DESCRIPTION
1.	ALL DIMENSIONS ARE IN MILLIMETERS UNLESS NOTED OTHERWISE.
2.	WRITTEN DIMENSIONS ARE TO BE FOLLOWED. DRAWINGS ARE NOT TO BE SCALED.
3.	PLEASE CO-ORDINATE THIS DRAWING WITH ALL OTHER RELEVANT DRAWINGS OF ALL THE SERVICES.
4.	SHOP DRAWINGS SHALL BE PREPARED BY THE CONTRACTOR AND SUBMITTED AS PER SITE
5.	ALL LINES SHOWING IN LAYOUT ARE CENTER LINES.
6.	FOR LOCATION OF MANHOLE MAY BE CHECKED BEFORE EXECUTION AS PER SITE CONDITIONS
7.	INVERT LEVEL/LOCATION AND SIZES OF EXTERNAL SEWER SHALL BE CHECKED AT SITE BEFORE EXECUTION. IF EXISTING SEWER HIGHER THEN THE PROPOSED INVERT LEVEL THEN SAME MAY BE CORRECTED AS PER SITE CONDITIONS
8.	ALL DRAIN LINE SHALL BE LAID ON PCC BED.
9.	ALL BURRIED PIPES SHALL BE TESTED FOR LEAKAGES AND STRAIGHTNESS AS PER SPECIFICATION.
10.	TRENCH SHALL BE REFILLED ONLY AFTER PIPE TESTING.
11.	ALL S & S RCC (NP2) PIPE SHALL CONFIRM TO IS : 458.
12.	THE DEPTH OF MANHOLE SHOULD BE MEASURED FROM F.G.L

DRAINAGE LEGEND :			
S. No.	SYMBOL	DESCRIPTION	
1.		800X900MM DRAINAGE MANHOLE	
2.		RAIN WATER HARVESTING TANK WITH GREASE TRAP & DESILTING	
3.		DRAINAGE LINE	
4.		450X450MM CATCH BASIN	
5.		COVERED DRAIN CHANNEL	
6.		CULVERT	
SCHEDULE OF DRAINAGE MANHOLE:-			
S. No.	SYMBOL	DESCRIPTION	DEPTH (MM)
1.	a	800/900	600 TO 900

THE DRAWING IS INDICATIVE ONLY