

SECTION-6-DRAWINGS

BQ WORKMEN HOUSING				
S. No.	DESCRIPTION	TYPE OF DWG	DOCUMENT NUMBER	REVISION
I	ARCHITECTURE			
1	SITE PLAN	TD	rites/BLD/AR/TD/001	R0
2	EXISTING TREE DETAILS	TD	rites/BLD/AR/TD/001A	R0
3	PARKING PLAN	TD	rites/BLD/AR/TD/002	R0
4	LANDSCAPE PLAN	TD	rites/BLD/AR/TD/003	R0
5	PART SECTION & DETAILS	TD	rites/BLD/AR/TD/004	R0
6	TYPICAL UNIT PLAN	TD	rites/BLD/AR/TD/005	R0
7	TYPICAL STILT FLOOR PLAN	TD	rites/BLD/AR/TD/006	R0
8	TYPICAL FLOOR PLAN	TD	rites/BLD/AR/TD/007	R0
9	TERRACE PLAN	TD	rites/BLD/AR/TD/008	R0
10	MUMTY PLAN	TD	rites/BLD/AR/TD/009	R0
11	FRONT & REAR ELEVATION	TD	rites/BLD/AR/TD/010	R0
12	SIDE ELEVATION	TD	rites/BLD/AR/TD/011	R0
13	SECTIONS AA	TD	rites/BLD/AR/TD/012	R0
14	SECTIONS BB	TD	rites/BLD/AR/TD/013	R0
15	DOOR AND WINDOW SCHEDULES & DETAILS-1	TD	rites/BLD/AR/TD/014	R0
16	DOOR AND WINDOW SCHEDULES & DETAILS-2	TD	rites/BLD/AR/TD/015	R0
17	FLOORING LAYOUT_STILT FLOOR	TD	rites/BLD/AR/TD/016	R0
18	FLOORING LAYOUT_TYPICAL FLOOR	TD	rites/BLD/AR/TD/017	R0
19	FLOORING LAYOUT_TERRACE FLOOR	TD	rites/BLD/AR/TD/018	R0
20	TYPICAL TOILET DETAILS	TD	rites/BLD/AR/TD/019	R0
21	TYPICAL BALCONY & MS LADDER DETAIL (HOUSING)	TD	rites/BLD/AR/TD/020	R0
22	TYPICAL RAMP AND STEPS DETAIL	TD	rites/BLD/AR/TD/021	R0
23	TYPICAL STAIRCASE DETAIL (HOUSING)	TD	rites/BLD/AR/TD/022	R0
24	TYPICAL LIFT DETAIL & LIFT LOBBY (HOUSING)	TD	rites/BLD/AR/TD/023	R0
25	TYPICAL KITCHEN DETAIL	TD	rites/BLD/AR/TD/024	R0
26	TYPICAL WARDROBE DETAIL	TD	rites/BLD/AR/TD/025	R0
27	GUARD ROOM & BOUNDARY WALL DETAIL	TD	rites/BLD/AR/TD/026	R0
28	GUARD ROOM FLOORING PLAN	TD	rites/BLD/AR/TD/027	R0
29	GUEST HOUSE PLAN_GROUND FLOOR	TD	rites/BLD/AR/TD/028	R0
30	GUEST HOUSE PLAN_FIRST FLOOR	TD	rites/BLD/AR/TD/029	R0
31	GUEST HOUSE PLAN_SECOND FLOOR	TD	rites/BLD/AR/TD/030	R0
32	GUEST HOUSE PLAN_THIRD FLOOR	TD	rites/BLD/AR/TD/031	R0
33	GUEST HOUSE PLAN_TERRACE FLOOR	TD	rites/BLD/AR/TD/032	R0
34	GUEST HOUSE PLAN_MUMTY LEVEL	TD	rites/BLD/AR/TD/033	R0
35	ELEVATIONS	TD	rites/BLD/AR/TD/034	R0
36	SECTIONS AA	TD	rites/BLD/AR/TD/035	R0
37	SECTION BB	TD	rites/BLD/AR/TD/036	R0
38	DOOR AND WINDOW SCHEDULES & DETAILS-1	TD	rites/BLD/AR/TD/037	R0
39	DOOR AND WINDOW SCHEDULES & DETAILS-2	TD	rites/BLD/AR/TD/038	R0
40	STAIRCASE & MS LADDER DETAIL	TD	rites/BLD/AR/TD/039	R0
41	TOILET DETAIL (GUEST HOUSE)	TD	rites/BLD/AR/TD/040	R0
42	FLOORING PLAN_GROUND FLOOR (GUEST HOUSE)	TD	rites/BLD/AR/TD/041	R0
43	FLOORING PLAN_FIRST FLOOR	TD	rites/BLD/AR/TD/042	R0
44	FLOORING PLAN_SECOND FLOOR	TD	rites/BLD/AR/TD/043	R0
45	FLOORING PLAN_THIRD FLOOR	TD	rites/BLD/AR/TD/044	R0
46	FLOORING PLAN_TERRACE	TD	rites/BLD/AR/TD/045	R0
47	COMMERICAL KITCHEN DETAIL_GUEST HOUSE	TD	rites/BLD/AR/TD/046	R0
47	GROUND FLOOR COMMUNITY CENTRE	TD	rites/BLD/AR/TD/047	R0
48	FIRST FLOOR COMMUNITY CENTRE	TD	rites/BLD/AR/TD/048	R0
49	TERRACE PLAN_COMMUNITY CENTRE	TD	rites/BLD/AR/TD/049	R0
50	MUMTY LEVEL_COMMUNITY CENTRE	TD	rites/BLD/AR/TD/050	R0
51	SECTIONS & MS LADDER DETAIL	TD	rites/BLD/AR/TD/051	R0
52	ELEVATIONS	TD	rites/BLD/AR/TD/052	R0
53	DOOR AND WINDOW SCHEDULES & DETAILS-1	TD	rites/BLD/AR/TD/053	R0
54	DOOR AND WINDOW SCHEDULES & DETAILS-2	TD	rites/BLD/AR/TD/054	R0
55	RCP LAYOUT_GROUND FLOOR COMMUNITY	TD	rites/BLD/AR/TD/055	R0
56	RCP LAYOUT_FIRST FLOOR COMMUNITY	TD	rites/BLD/AR/TD/056	R0
57	FLOORING PLAN_GROUND FLOOR COMMUNITY	TD	rites/BLD/AR/TD/057	R0
58	FLOORING PLAN_FIRST FLOOR COMMUNITY	TD	rites/BLD/AR/TD/058	R0
59	FLOORING PLAN_TERRACE FLOOR COMMUNITY	TD	rites/BLD/AR/TD/059	R0
60	ESS DETAIL	TD	rites/BLD/AR/TD/060	R0
61	ESS FLOORING PLAN	TD	rites/BLD/AR/TD/061	R0
II	STRUCTURE			
1	PILE LAYOUT PLAN-HOUSING BLOCK	TD	rites/BLD/STR/TD/HOUSING(G+6)/100	R0
2	PILE CAP LAYOUT PLAN AND REINFORCEMENT DETAILS--HOUSING BLOCK	TD	rites/BLD/STR/TD/HOUSING(G+6)/101	R0
3	TYPICAL DETAILS FOR PILE ,COLUMN AND BEAM--HOUSING BLOCK	TD	rites/BLD/STR/TD/HOUSING(G+6)/102	R0
4	COLUMN LAYOUT PLAN--HOUSING BLOCK	TD	rites/BLD/STR/TD/HOUSING(G+6)/103	R0
5	COLUMN REINFORCEMENT DETAILS-HOUSING BLOCK	TD	rites/BLD/STR/TD/HOUSING(G+6)/104	R0
6	PLINTH BEAM LAYOUT PLAN-HOUSING BLOCK	TD	rites/BLD/STR/TD/HOUSING(G+6)/105	R0
7	PLINTH BEAM REINFORCEMENT DETAILS-HOUSING BLOCK	TD	rites/BLD/STR/TD/HOUSING(G+6)/106	R0
8	BEAM LAYOUT PLAN FOR TYPICAL FLOORS-HOUSING BLOCK	TD	rites/BLD/STR/TD/HOUSING(G+6)/107	R0
9	BEAM REINFORCEMENT DETAILS FOR TYPICAL FLOORS-HOUSING BLOCK	TD	rites/BLD/STR/TD/HOUSING(G+6)/108	R0

10	MUMTY , WATER TANK BOTTOM AND LIFT OVERHEAD DETAILS-HOUSING BLOCK	TD	rites/BLD/STR/TD/HOUSING(G+6)/109	R0
11	STAIRCASE PLAN & DETAILS-HOUSING BLOCK	TD	rites/BLD/STR/TD/HOUSING(G+6)/110	R0
12	FOUNDATION LAYOUT PLAN-GUEST HOUSE	TD	rites/BLD/STR/TD/GH(G+3)/111	R0
13	TYPICAL DETAILS FOR PILE ,COLUMN AND BEAM-GUEST HOUSE	TD	rites/BLD/STR/TD/GH(G+3)/112	R0
14	COLUMN LAYOUT PLAN-GUEST HOUSE	TD	rites/BLD/STR/TD/GH(G+3)/113	R0
15	COLUMN REINFORCEMENT DETAILS-GUEST HOUSE	TD	rites/BLD/STR/TD/GH(G+3)/114	R0
16	BEAM LAYOUT PLAN AT PLINTH LEVEL-GUEST HOUSE	TD	rites/BLD/STR/TD/GH(G+3)/115	R0
17	PLINTH BEAMS REINFORCEMENT DETAILS-GUEST HOUSE	TD	rites/BLD/STR/TD/GH(G+3)/116	R0
18	PLINTH BEAMS REINFORCEMENT DETAILS-GUEST HOUSE	TD	rites/BLD/STR/TD/GH(G+3)/117	R0
19	BEAM LAYOUT PLAN AT FIRST FLOOR LEVEL-GUEST HOUSE	TD	rites/BLD/STR/TD/GH(G+3)/118	R0
20	FIRST FLOOR BEAMS REINFORCEMENT DETAILS-GUEST HOUSE	TD	rites/BLD/STR/TD/GH(G+3)/119	R0
21	FIRST FLOOR BEAMS REINFORCEMENT DETAILS-GUEST HOUSE	TD	rites/BLD/STR/TD/GH(G+3)/120	R0
22	BEAM LAYOUT PLAN AT SECOND AND THIRD FLOOR LEVEL-GUEST HOUSE	TD	rites/BLD/STR/TD/GH(G+3)/121	R0
23	SECOND AND THIRD FLOOR BEAMS REINFORCEMENT DETAILS-GUEST HOUSE	TD	rites/BLD/STR/TD/GH(G+3)/122	R0
24	SECOND AND THIRD FLOOR BEAMS REINFORCEMENT DETAILS-GUEST HOUSE	TD	rites/BLD/STR/TD/GH(G+3)/123	R0
25	BEAM LAYOUT PLAN AT TERRACE LEVEL-GUEST HOUSE	TD	rites/BLD/STR/TD/GH(G+3)/124	R0
26	BEAM LAYOUT PLAN AT TERRACE LEVEL-GUEST HOUSE	TD	rites/BLD/STR/TD/GH(G+3)/125	R0
27	BEAM LAYOUT PLAN AT TERRACE LEVEL-GUEST HOUSE	TD	rites/BLD/STR/TD/GH(G+3)/126	R0
28	MUMTY , WATER TANK BOTTOM AND LIFT OVERHEAD DETAILS-GUEST HOUSE	TD	rites/BLD/STR/TD/GH(G+3)/127	R0
29	STAIRCASE PLAN & DETAILS-GUEST HOUSE	TD	rites/BLD/STR/TD/GH(G+3)/128	R0
30	FOUNDATION LAYOUT PLAN-COMMUNITY CENTRE	TD	rites/BLD/STR/TD/CS/129	R0
31	TYPICAL DETAILS FOR PILE ,COLUMN AND BEAM-COMMUNITY CENTRE	TD	rites/BLD/STR/TD/CS/130	R0
32	COLUMN LAYOUT PLAN-COMMUNITY CENTRE	TD	rites/BLD/STR/TD/CS/131	R0
33	COLUMN REINFORCEMENT DETAILS-COMMUNITY CENTRE	TD	rites/BLD/STR/TD/CS/132	R0
34	PLINTH BEAM LAYOUT AND REINFORCEMENT DETAILS-COMMUNITY CENTRE	TD	rites/BLD/STR/TD/CS/133	R0
35	PLINTH BEAM REINFORCEMENT DETAILS-COMMUNITY CENTRE	TD	rites/BLD/STR/TD/CS/134	R0
36	PLINTH BEAM REINFORCEMENT DETAILS-COMMUNITY CENTRE	TD	rites/BLD/STR/TD/CS/135	R0
37	FIRST FLOOR BEAM LAYOUT AND REINFORCEMENT DETAILS-COMMUNITY CENTRE	TD	rites/BLD/STR/TD/CS/136	R0
38	FIRST FLOOR BEAM REINFORCEMENT DETAILS-COMMUNITY CENTRE	TD	rites/BLD/STR/TD/CS/137	R0
39	FIRST FLOOR BEAM REINFORCEMENT DETAILS-COMMUNITY CENTRE	TD	rites/BLD/STR/TD/CS/138	R0
40	ROOF BEAM LAYOUT AND REINFORCEMENT DETAILS-COMMUNITY CENTRE	TD	rites/BLD/STR/TD/CS/139	R0
41	ROOF BEAM REINFORCEMENT DETAILS-COMMUNITY CENTRE	TD	rites/BLD/STR/TD/CS/140	R0
42	ROOF BEAM REINFORCEMENT DETAILS-COMMUNITY CENTRE	TD	rites/BLD/STR/TD/CS/141	R0
43	MUMTY BEAM LAYOUT AND REINFORCEMENT DETAILS-COMMUNITY CENTRE	TD	rites/BLD/STR/TD/CS/142	R0
44	STAIRCASE DETAILS-COMMUNITY CENTRE	TD	rites/BLD/STR/TD/CS/143	R0
45	FOUNDATION LAYOUT PLAN-ESS BUILDING	TD	rites/BLD/STR/TD/CS/144	R0
46	TYPICAL DETAILS FOR PILE ,COLUMN AND BEAM-ESS BUILDING	TD	rites/BLD/STR/TD/CS/145	R0
47	COLUMN LAYOUT PLAN-ESS BUILDING	TD	rites/BLD/STR/TD/CS/146	R0
48	PLINTH BEAM LAYOUT PLAN AND GRADE SLAB SCHEDULE-ESS BUILDING	TD	rites/BLD/STR/TD/CS/147	R0
49	PLINTH BEAM REINFORCEMENT DETAILS-ESS BUILDING	TD	rites/BLD/STR/TD/CS/148	R0
50	ROOF BEAM LAYOUT AND SLAB SCHEDULE-ESS BUILDING	TD	rites/BLD/STR/TD/CS/149	R0
51	ROOF BEAM REINFORCEMENT DETAILS-ESS BUILDING	TD	rites/BLD/STR/TD/CS/150	R0
III	ELECTRICAL			
1	BQ HOUSING BLOCK, TYPICAL FLOOR LIGHTING & POWER LAYOUT	TD	rites/BLD/EL/TEN/201	R0
2	BQ HOUSING BLOCK, STILT FLOOR LIGHTING & POWER LAYOUT	TD	rites/BLD/EL/TEN/202	R0
3	BQ HOUSING BLOCK, TERRACE FLOOR LIGHTING LAYOUT	TD	rites/BLD/EL/TEN/203	R0
4	BQ HOUSING BLOCK, TYPICAL FLOOR CCTV & PA SYSTEM LAYOUT PLAN	TD	rites/BLD/EL/TEN/204	R0
5	BQ HOUSING BLOCK, STILT FLOOR CCTV & PA SYSTEM LAYOUT	TD	rites/BLD/EL/TEN/205	R0
6	SINGLE LINE DIAGRAM (SLD) OF ELECTRICAL WORK	TD	rites/BLD/EL/TEN/206	R0
7	SLD OF ESSENTIAL PANEL,COMMON AREA PANEL & UPS PANEL	TD	rites/BLD/EL/TEN/207	R0
8	SLD FOR RISING MAINS AND FLOOR DISTRIBUTION PANEL	TD	rites/BLD/EL/TEN/208	R0
9	EXTERNAL STREET LIGHTING LAYOUT PLAN	TD	rites/BLD/EL/TEN/209	R0
10	EXTERNAL CCTV LAYOUT PLAN	TD	rites/BLD/EL/TEN/210	R0
11	GUEST HOUSE, GROUND FLOOR LIGHTING & POWER LAYOUT	TD	rites/BLD/EL/TEN/211	R0
12	GUEST HOUSE, FIRST FLOOR LIGHTING & POWER LAYOUT	TD	rites/BLD/EL/TEN/212	R0
13	GUEST HOUSE, SECOND AND THIRD FLOOR LIGHTING & POWER LAYOUT	TD	rites/BLD/EL/TEN/213	R0
14	COMMUNITY CENTRE GROUND FLOOR LIGHTING & POWER LAYOUT	TD	rites/BLD/EL/TEN/214	R0
15	COMMUNITY CENTRE FIRST FLOOR LIGHTING & POWER LAYOUT	TD	rites/BLD/EL/TEN/215	R0
16	GUEST HOUSE GROUND FLOOR CCTV & PA SYSTEM FIRE ALARM LAYOUT	TD	rites/BLD/EL/TEN/216	R0
17	GUEST HOUSE,FIRST FLOOR CCTV & PA SYSTEM FIRE ALARM LAYOUT	TD	rites/BLD/EL/TEN/217	R0
18	GUEST HOUSE, SECOND AND THIRD FLOOR CCTV & PA SYSTEM FIRE ALARM LAYOUT	TD	rites/BLD/EL/TEN/218	R0
19	COMMUNITY CENTRE, GROUND FLOOR CCTV & PA SYSTEM LAYOUT	TD	rites/BLD/EL/TEN/219	R0
20	COMMUNITY CENTRE, FIRST FLOOR CCTV & PA SYSTEM LAYOUT	TD	rites/BLD/EL/TEN/220	R0
21	SCHEMATIC DIAGRAM OF CCTV AND EPABX SYSTEM	TD	rites/BLD/EL/TEN/221	R0
IV	HVAC			
1	HOUSING BLOCK, TYPICAL FLOOR HVAC LAYOUT	TD	rites/BLD/HVAC/TEN/301	R0
2	HOUSING BLOCK, TERRACE FLOOR HVAC LAYOUT	TD	rites/BLD/HVAC/TEN/302	R0
3	GROUND FLOOR HVAC PLAN GUEST HOUSE	TD	rites/BLD/HVAC/TEN/303	R0
4	FIRST FLOOR HVAC PLAN GUEST HOUSE	TD	rites/BLD/HVAC/TEN/304	R0
5	SECOND FLOOR HVAC PLAN GUEST HOUSE	TD	rites/BLD/HVAC/TEN/305	R0
6	THIRD FLOOR HVAC PLAN GUEST HOUSE	TD	rites/BLD/HVAC/TEN/306	R0
7	TERRACE LEVEL HVAC PLAN GUEST HOUSE	TD	rites/BLD/HVAC/TEN/307	R0
8	GROUND FLOOR HVAC PLAN COMMUNITY CENTRE	TD	rites/BLD/HVAC/TEN/308	R0
9	FIRST FLOOR HVAC PLAN COMMUNITY CENTRE	TD	rites/BLD/HVAC/TEN/309	R0
10	TERRACE FLOOR HVAC PLAN COMMUNITY CENTRE	TD	rites/BLD/HVAC/TEN/310	R0
V	DRAINAGE/PLUMBING			
1	EXTERNAL PLUMBING SERVICES COORDINATED LAYOUT	TD	rites/BLD/DR/TEN/401	R0
2	EXTERNAL PLUMBING SERVICES SEWERAGE LAYOUT	TD	rites/BLD/DR/TEN/402	R0
3	EXTERNAL PLUMBING SERVICES DRAINAGE LAYOUT	TD	rites/BLD/DR/TEN/403	R0
4	EXTERNAL PLUMBING SERVICES DUAL PLUMBING,FIRE LAYOUT	TD	rites/BLD/DR/TEN/404	R0
5	EXTERNAL WATER SUPPLY DESIGN CHART	TD	rites/BLD/DR/TEN/405	R0
6	TYPICAL PLUMBING DETAILS	TD	rites/BLD/DR/TEN/406	R0

7	EXTERNAL UGT PLAN & SECTION DETAIL	TD	rites/BLD/DR/TEN/406A	R0
8	EXTERNAL STP PLAN & DETAIL	TD	rites/BLD/DR/TEN/406B	R0
9	HOUSING BLOCK GROUND FLOOR PLUMBING DRAWING	TD	rites/BLD/DR/TEN/407	R0
10	HOUSING BLOCK TYPICAL FLOOR 1st to 6th PLUMBING DRAWING	TD	rites/BLD/DR/TEN/408	R0
11	HOUSING BLOCK TERRACE FLOOR PLUMBING DRAWING	TD	rites/BLD/DR/TEN/409	R0
12	HOUSING BLOCK WATER SUPPLY SCHEMATIC	TD	rites/BLD/DR/TEN/410	R0
13	GROUND FLOOR PLAN GUEST HOUSE PLUMBING DRAWING	TD	rites/BLD/DR/TEN/411	R0
14	FIRST FLOOR PLAN GUEST HOUSE PLUMBING DRAWING	TD	rites/BLD/DR/TEN/412	R0
15	SECOND FLOOR PLAN GUEST HOUSE PLUMBING DRAWING	TD	rites/BLD/DR/TEN/413	R0
16	THIRD FLOOR PLAN GUEST HOUSE PLUMBING DRAWING	TD	rites/BLD/DR/TEN/414	R0
17	TERRACE PLAN GUEST HOUSE PLUMBING DRAWING	TD	rites/BLD/DR/TEN/415	R0
18	GUEST HOUSE WATER SUPPLY SCHEMATIC	TD	rites/BLD/DR/TEN/416	R0
19	COMMUNITY CENTRE, GROUND FLOOR PLAN PLUMBING	TD	rites/BLD/DR/TEN/417	R0
20	COMMUNITY CENTRE, FIRST FLOOR PLAN PLUMBING	TD	rites/BLD/DR/TEN/418	R0
21	COMMUNITY CENTRE, TERRACE PLAN PLUMBING	TD	rites/BLD/DR/TEN/419	R0
22	COMMUNITY CENTRE, WATER SUPPLY SCHEMATIC	TD	rites/BLD/DR/TEN/420	R0
23	GUARD ROOM PLUMBING LAYOUT	TD	rites/BLD/DR/TEN/421	R0
VI	FIRE FIGHTING			
1	HOUSING BLOCK GROUND FLOOR FIRE DRAWING	TD	rites/BLD/FF/TEN/501	R0
2	HOUSING BLOCK TYPICAL FLOOR 1st to 6th FIRE DRAWING	TD	rites/BLD/FF/TEN/502	R0
3	HOUSING BLOCK TERRACE FLOOR FIRE DRAWING	TD	rites/BLD/FF/TEN/503	R0
4	HOUSING BLOCK TYPICAL FIRE SCHEMATIC	TD	rites/BLD/FF/TEN/504	R0
5	GROUND FLOOR PLAN GUEST HOUSE FIRE DRAWING	TD	rites/BLD/FF/TEN/505	R0
6	FIRST FLOOR PLAN GUEST HOUSE FIRE DRAWING	TD	rites/BLD/FF/TEN/506	R0
7	SECOND FLOOR PLAN GUEST HOUSE FIRE DRAWING	TD	rites/BLD/FF/TEN/507	R0
8	THIRD FLOOR PLAN GUEST HOUSE FIRE DRAWING	TD	rites/BLD/FF/TEN/508	R0
9	TERRACE PLAN GUEST HOUSE FIRE DRAWING	TD	rites/BLD/FF/TEN/509	R0
10	GUEST HOUSE FIRE SCHEMATIC	TD	rites/BLD/FF/TEN/510	R0
11	GROUND FLOOR PLAN COMMUNITY CENTRE FIRE DRAWING	TD	rites/BLD/FF/TEN/511	R0
12	FIRST FLOOR PLAN COMMUNITY CENTRE FIRE DRAWING	TD	rites/BLD/FF/TEN/512	R0
13	TERRACE PLAN COMMUNITY CENTRE FIRE DRAWING	TD	rites/BLD/FF/TEN/513	R0
14	COMMUNITY CENTRE FIRE SCHEMATIC	TD	rites/BLD/FF/TEN/514	R0
VII	WATER SUPPLY			
1	BQ HOUSING BLOCK, TYPICAL TOILET & KITCHEN WATER SUPPLY LAYOUT	TD	rites/BLD/WS/TEN/601	R0
2	GUEST HOUSE, TYPICAL TOILET & KITCHEN WATER SUPPLY LAYOUT	TD	rites/BLD/WS/TEN/602	R0
3	COMMUNITY CENTRE, GROUND & 1st FLOOR TOILET WATER SUPPLY LAYOUT	TD	rites/BLD/WS/TEN/603	R0
4	BQ HOUSING BLOCK, OHT DETAIL	TD	rites/BLD/WS/TEN/604	R0
5	GUEST HOUSE OHT DETAIL	TD	rites/BLD/WS/TEN/605	R0
6	COMMUNITY CENTRE, OHT DETAIL	TD	rites/BLD/WS/TEN/606	R0
VIII	GAS SUPPLY			
1	EXTERNAL PLUMBING SERVICES DUAL PLUMBING, GAS SUPPLY & FIRE LAYOUT	TD	rites/BLD/GS/TEN/701	R0
2	BQ HOUSING BLOCK, GAS SUPPLY SCHEMATIC	TD	rites/BLD/GS/TEN/702	R0
3	GUEST HOUSE GAS SUPPLY SCHEMATIC	TD	rites/BLD/GS/TEN/703	R0



SN	DESCRIPTION	AREA (SQM)/ NOS.	PERCENTAGE
01	TOTAL PLOT AREA (APPROX.)	29,400	100.00%
02	GROUND COVERAGE (Excluding STP, UGT & Other Utility)	5140	(18%)
03	TOTAL BUILT-UP AREA	30,823.40	
04	TOTAL NO. OF HOUSING BLOCKS	08	
05	TOTAL NO. OF HOUSING UNITS	192	
(A) HOUSING(G+6)		FOR EACH TOWER	TOTAL
I	STILT FLOOR AREA	467.70	3741.60
II	FIRST FLOOR AREA	483.60	3868.80
III	SECOND FLOOR AREA	483.60	3868.80
IV	THIRD FLOOR AREA	483.60	3868.80
V	FOURTH FLOOR AREA	483.60	3868.80
VI	FIFTH FLOOR AREA	483.60	3868.80
VII	SIXTH FLOOR AREA	483.60	3868.80
VIII	MUMTY AREA	50	400
(B) GUEST HOUSE (G+3)			
I	GROUND FLOOR AREA	465	465
II	FIRST FLOOR AREA	495	495
III	SECOND FLOOR AREA	500	500
IV	THIRD FLOOR AREA	500	500
V	MUMTY AREA	30	30
(C) COMMUNITY CENTRE (G+1)			
I	GROUND FLOOR AREA	490	490
II	FIRST FLOOR AREA	490	490
III	MUMTY AREA	55	55
(D) SERVICES: ESS, PUMP ROOM, STP ROOM & TWO GUARD ROOM, SECURITY HUT			
I	ESS BUILDING BLOCK	368	
II	GUARD ROOMS & SECURITY HUT	76	
III	PUMP ROOM & UGT (TENTATIVE)	205	
IV	STP (TENTATIVE)	270	
E	TOTAL BUILT-UP AREA EXCLUDING STILT & MUMTY FOR FAR		30,823.40
F	TOTAL BUILT-UP AREA EXCLUDING STILT & MUMTY FOR FAR		26,596.80
06	F.A.R (Excluding Stilt & Mumty Area)		0.90
07	Covered Parking (Housing Blocks)	192	
	Covered Parking (Guest House)	8	248 ECS
	Open Parking (Visitors)	48	
	Two Wheelers Parking	192	192

- NOTES
1. WRITTEN DIMENSIONS ARE TO BE FOLLOWED. DRAWINGS ARE NOT TO BE SCALED.
 2. ANY DISCREPANCY IN THE DRAWING SHALL BE BROUGHT TO THE NOTICE OF THE ENGINEER.
 3. THIS DRAWING SHALL BE READ IN CONJUNCTION WITH OTHER RELEVANT DRAWINGS.
 4. ALL LEVELS ARE IN METER UNLESS NOTED OTHERWISE.
 5. VISITORS PARKING IS NOT COVERED BY SHED
 6. BOUNDARY WALL HEIGHT IS 3.6M INCLUDING CONCERTINA

TENDER DRAWING

CLIENT	 OIL INDIA LIMITED (A Govt. of India Enterprise)		
CONSULTANT	 RITES THE INFRASTRUCTURE PEOPLE (A Govt. of India Enterprise)		
PROJECT	BQ WORKMEN HOUSING		
BUILDING	SITE LAYOUT		
DRAWING TITLE	PROPOSED SITE LAYOUT		
DRG. NO.	RITES/BLD/AR/TD/001		
NORTH	SCALE	DATE	
	NTS	JULY 2025	

DETAILS OF EXISTING TREES:				
SL. NO.	LOCAL NAME	ENGLISH QUEST	SCIENTIFIC	GIRTH IN MTR.
1	INDIAN CHERRY	CORDIA MYRTLE	LAGERSTROMIA SPECIOSA	0.35
2	INDIAN CHERRY	CORDIA MYRTLE	CORDIA MYXA	0.30
3	AM	MANGO	MANGIFERA INDICA	1.40
4	HEARTLEAF	HEARTLEAF	HOUTTUYNIA	0.80
5	INDIAN CHERRY	QUEEN'S GRAPE MYRTLE	LAGERSTROMIA SPECIOSA	1.50
6	SOM	SOM	PERSEA BOMBYCINA	1.00
7	PEEPAL	PEEPAL	FICUS RELIGIOSA	3.30
8	PEEPAL	PEEPAL	FICUS RELIGIOSA	1.00
9	PEEPAL	PEEPAL	FICUS RELIGIOSA	2.50
10	INDIAN CHERRY	MOUNTAIN BIRCH	FICUS INDICA	0.80
11	INDIAN CHERRY	MOUNTAIN BIRCH	PONGAMIA PINNATA	0.60
12	MANGROVE	INDIAN BEECH TREE	PONGAMIA PINNATA	0.80
13	INDIAN CHERRY	INDIAN CHERRY	CORDIA MYXA	0.80
14	INDIAN CHERRY	INDIAN CHERRY	CORDIA MYXA	0.80
15	AM	MANGO	MANGIFERA INDICA	0.85
16	AM	MANGO	MANGIFERA INDICA	0.80
17	BLACK MYROBALAN	BLACK MYROBALAN	TERMINALIA CHEBULA	1.50
18	INDIAN CHERRY	LAGERSTROMIA SPECIOSA	LAGERSTROMIA SPECIOSA	1.70
19	AM	MANGO	MANGIFERA INDICA	2.20
20	PEEPAL	PEEPAL	FICUS RELIGIOSA	2.50
21	AM	MANGO	FICUS RELIGIOSA	0.95
22	INDIAN CHERRY	INDIAN CHERRY	CORDIA MYXA	0.80
23	INDIAN CHERRY	INDIAN CHERRY	CORDIA MYXA	2.10
24	INDIAN CHERRY	INDIAN CHERRY	CORDIA MYXA	1.00
25	INDIAN CHERRY	INDIAN CHERRY	CORDIA MYXA	0.95

26	INDIAN CHERRY	CORDIA MYXA	0.80
27	INDIAN BEECH	PONGAMIA PINNATA	0.50
28	INDIAN BEECH	PONGAMIA PINNATA	0.80
29	INDIAN BEECH	PONGAMIA PINNATA	0.70
30	INDIAN BEECH	PONGAMIA PINNATA	1.08
31	INDIAN BEECH	PONGAMIA PINNATA	0.80
32	INDIAN BEECH	PONGAMIA PINNATA	0.35
33	INDIAN BEECH	PONGAMIA PINNATA	1.70
34	INDIAN BEECH	PONGAMIA PINNATA	0.80
35	INDIAN BEECH	PONGAMIA PINNATA	2.05
36	INDIAN BEECH	PONGAMIA PINNATA	0.70
37	INDIAN BEECH	PONGAMIA PINNATA	0.95
38	INDIAN BEECH	PONGAMIA PINNATA	0.80
39	INDIAN BEECH	PONGAMIA PINNATA	1.70
40	INDIAN BEECH	PONGAMIA PINNATA	0.70
41	INDIAN BEECH	PONGAMIA PINNATA	1.05
42	INDIAN BEECH	PONGAMIA PINNATA	2.00
43	INDIAN BEECH	PONGAMIA PINNATA	1.40
44	INDIAN BEECH	PONGAMIA PINNATA	0.80
45	INDIAN BEECH	PONGAMIA PINNATA	1.20
46	INDIAN BEECH	PONGAMIA PINNATA	1.50
47	INDIAN BEECH	PONGAMIA PINNATA	1.20
48	INDIAN BEECH	PONGAMIA PINNATA	1.20
49	INDIAN BEECH	PONGAMIA PINNATA	0.30
50	INDIAN BEECH	PONGAMIA PINNATA	1.45

51	INDIAN BEECH	PONGAMIA PINNATA	1.20
52	INDIAN BEECH	PONGAMIA PINNATA	0.30
53	INDIAN BEECH	PONGAMIA PINNATA	1.10
54	INDIAN BEECH	PONGAMIA PINNATA	1.00
55	INDIAN BEECH	PONGAMIA PINNATA	0.55
56	INDIAN BEECH	PONGAMIA PINNATA	0.85
57	INDIAN BEECH	PONGAMIA PINNATA	2.00
58	INDIAN BEECH	PONGAMIA PINNATA	0.70
59	INDIAN BEECH	PONGAMIA PINNATA	1.00
60	INDIAN BEECH	PONGAMIA PINNATA	1.80
61	INDIAN BEECH	PONGAMIA PINNATA	1.00
- PROPOSED SITE BOUNDARY
- PROTECTED TREES-26 NOS.
- TREES TO BE CUT-136 NOS.
- TREES OUTSIDE SITE BOUNDARY-13 NOS.

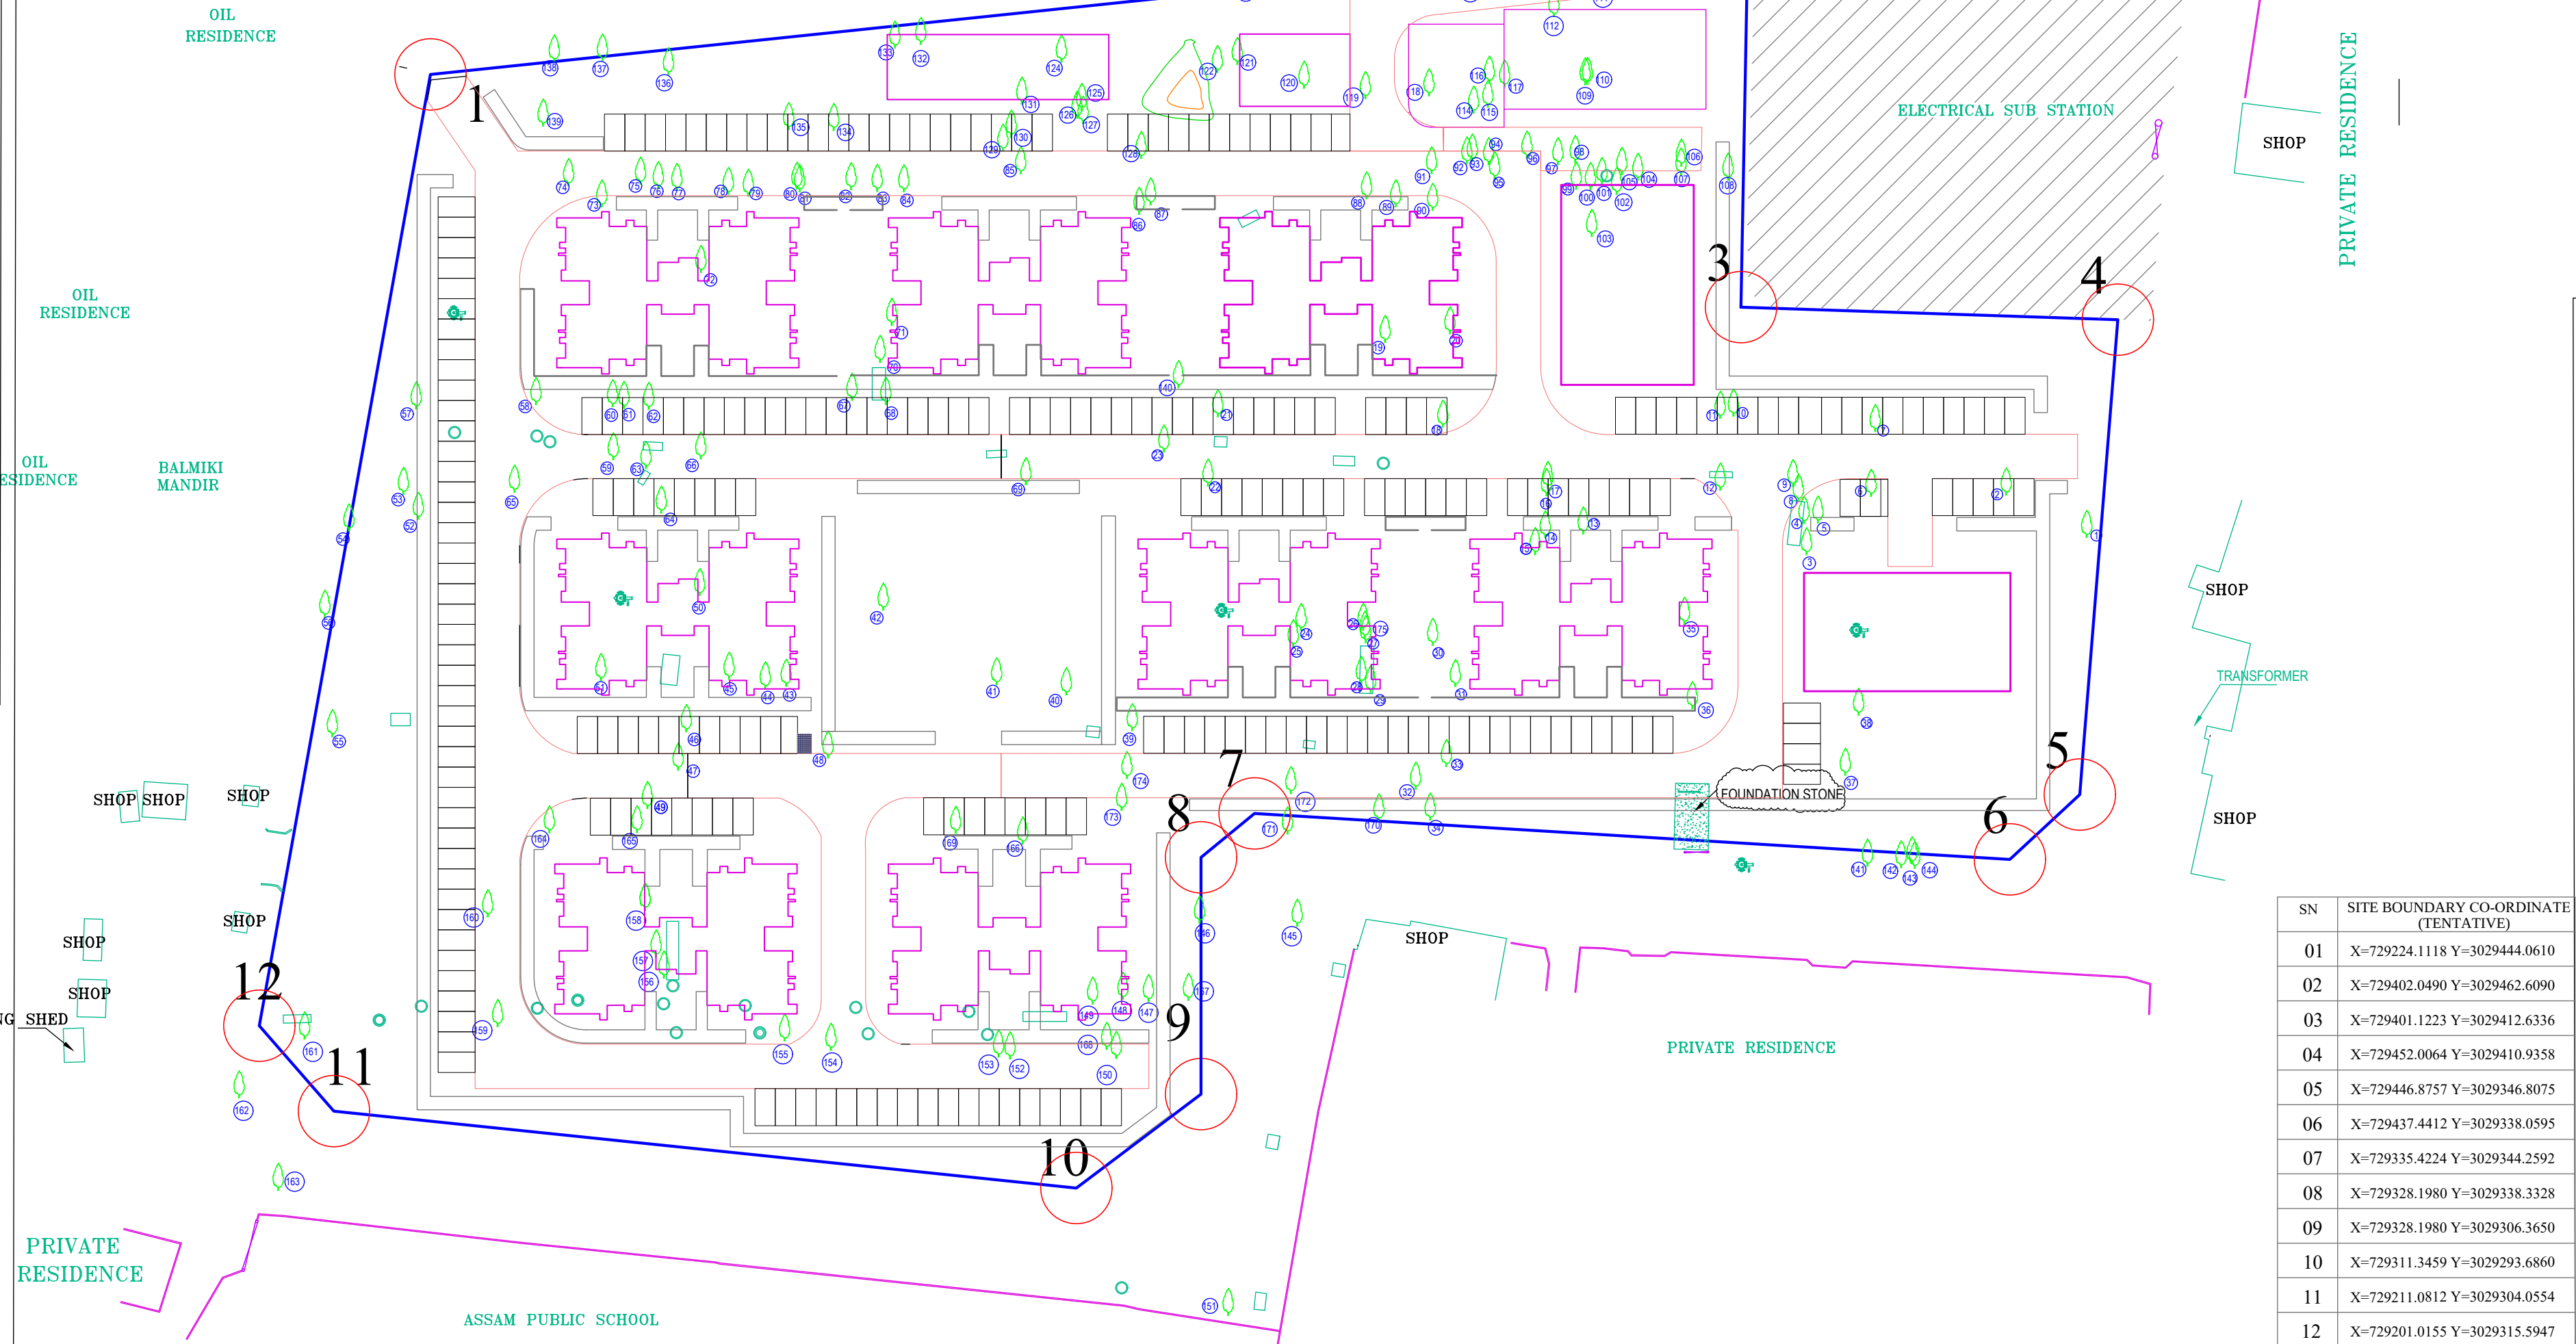


- NOTES
- ALL DIMENSIONS ARE IN MM; UNLESS NOTED OTHERWISE.
 - WRITTEN DIMENSIONS ARE TO BE FOLLOWED. DRAWINGS ARE NOT TO BE SCALED.
 - ANY DISCREPANCY IN THE DRAWING SHALL BE BROUGHT TO THE NOTICE OF THE ENGINEER.
 - THIS DRAWING SHALL BE READ IN CONJUNCTION WITH OTHER RELEVANT DRAWINGS.
 - THE INDICATED NUMBER OF PROTECTED TREES IS APPROXIMATE. ADDITIONAL EFFORTS SHALL BE MADE TO PRESERVE MORE TREES LOCATED ALONG THE BOUNDARY, FOOTPATHS, ROAD EDGES, AND NEARBY AREAS.


TENDER DRAWING

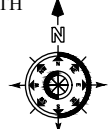CLIENT	 OIL INDIA LIMITED (A Govt. of India Enterprise)		
CONSULTANT	 RITES THE INFRASTRUCTURE PEOPLE (A Govt. of India Enterprise)		
PROJECT	BQ WORKMEN HOUSING		
BUILDING	SITE LAYOUT		
DRAWING TITLE	TREE DETAILS		
DRG. NO.	RITES/BLD/AR/TD/001A		
NORTH	SCALE	DATE	
	NTS	JULY 2025	

SN	SITE BOUNDARY CO-ORDINATE (TENTATIVE)
01	X=729224.1118 Y=3029444.0610
02	X=729402.0490 Y=3029462.6090
03	X=729401.1223 Y=3029412.6336
04	X=729452.0064 Y=3029410.9358
05	X=729446.8757 Y=3029346.8075
06	X=729437.4412 Y=3029338.0595
07	X=729335.4224 Y=3029344.2592
08	X=729328.1980 Y=3029338.3328
09	X=729328.1980 Y=3029306.3650
10	X=729311.3459 Y=3029293.6860
11	X=729211.0812 Y=3029304.0554
12	X=729201.0155 Y=3029315.5947

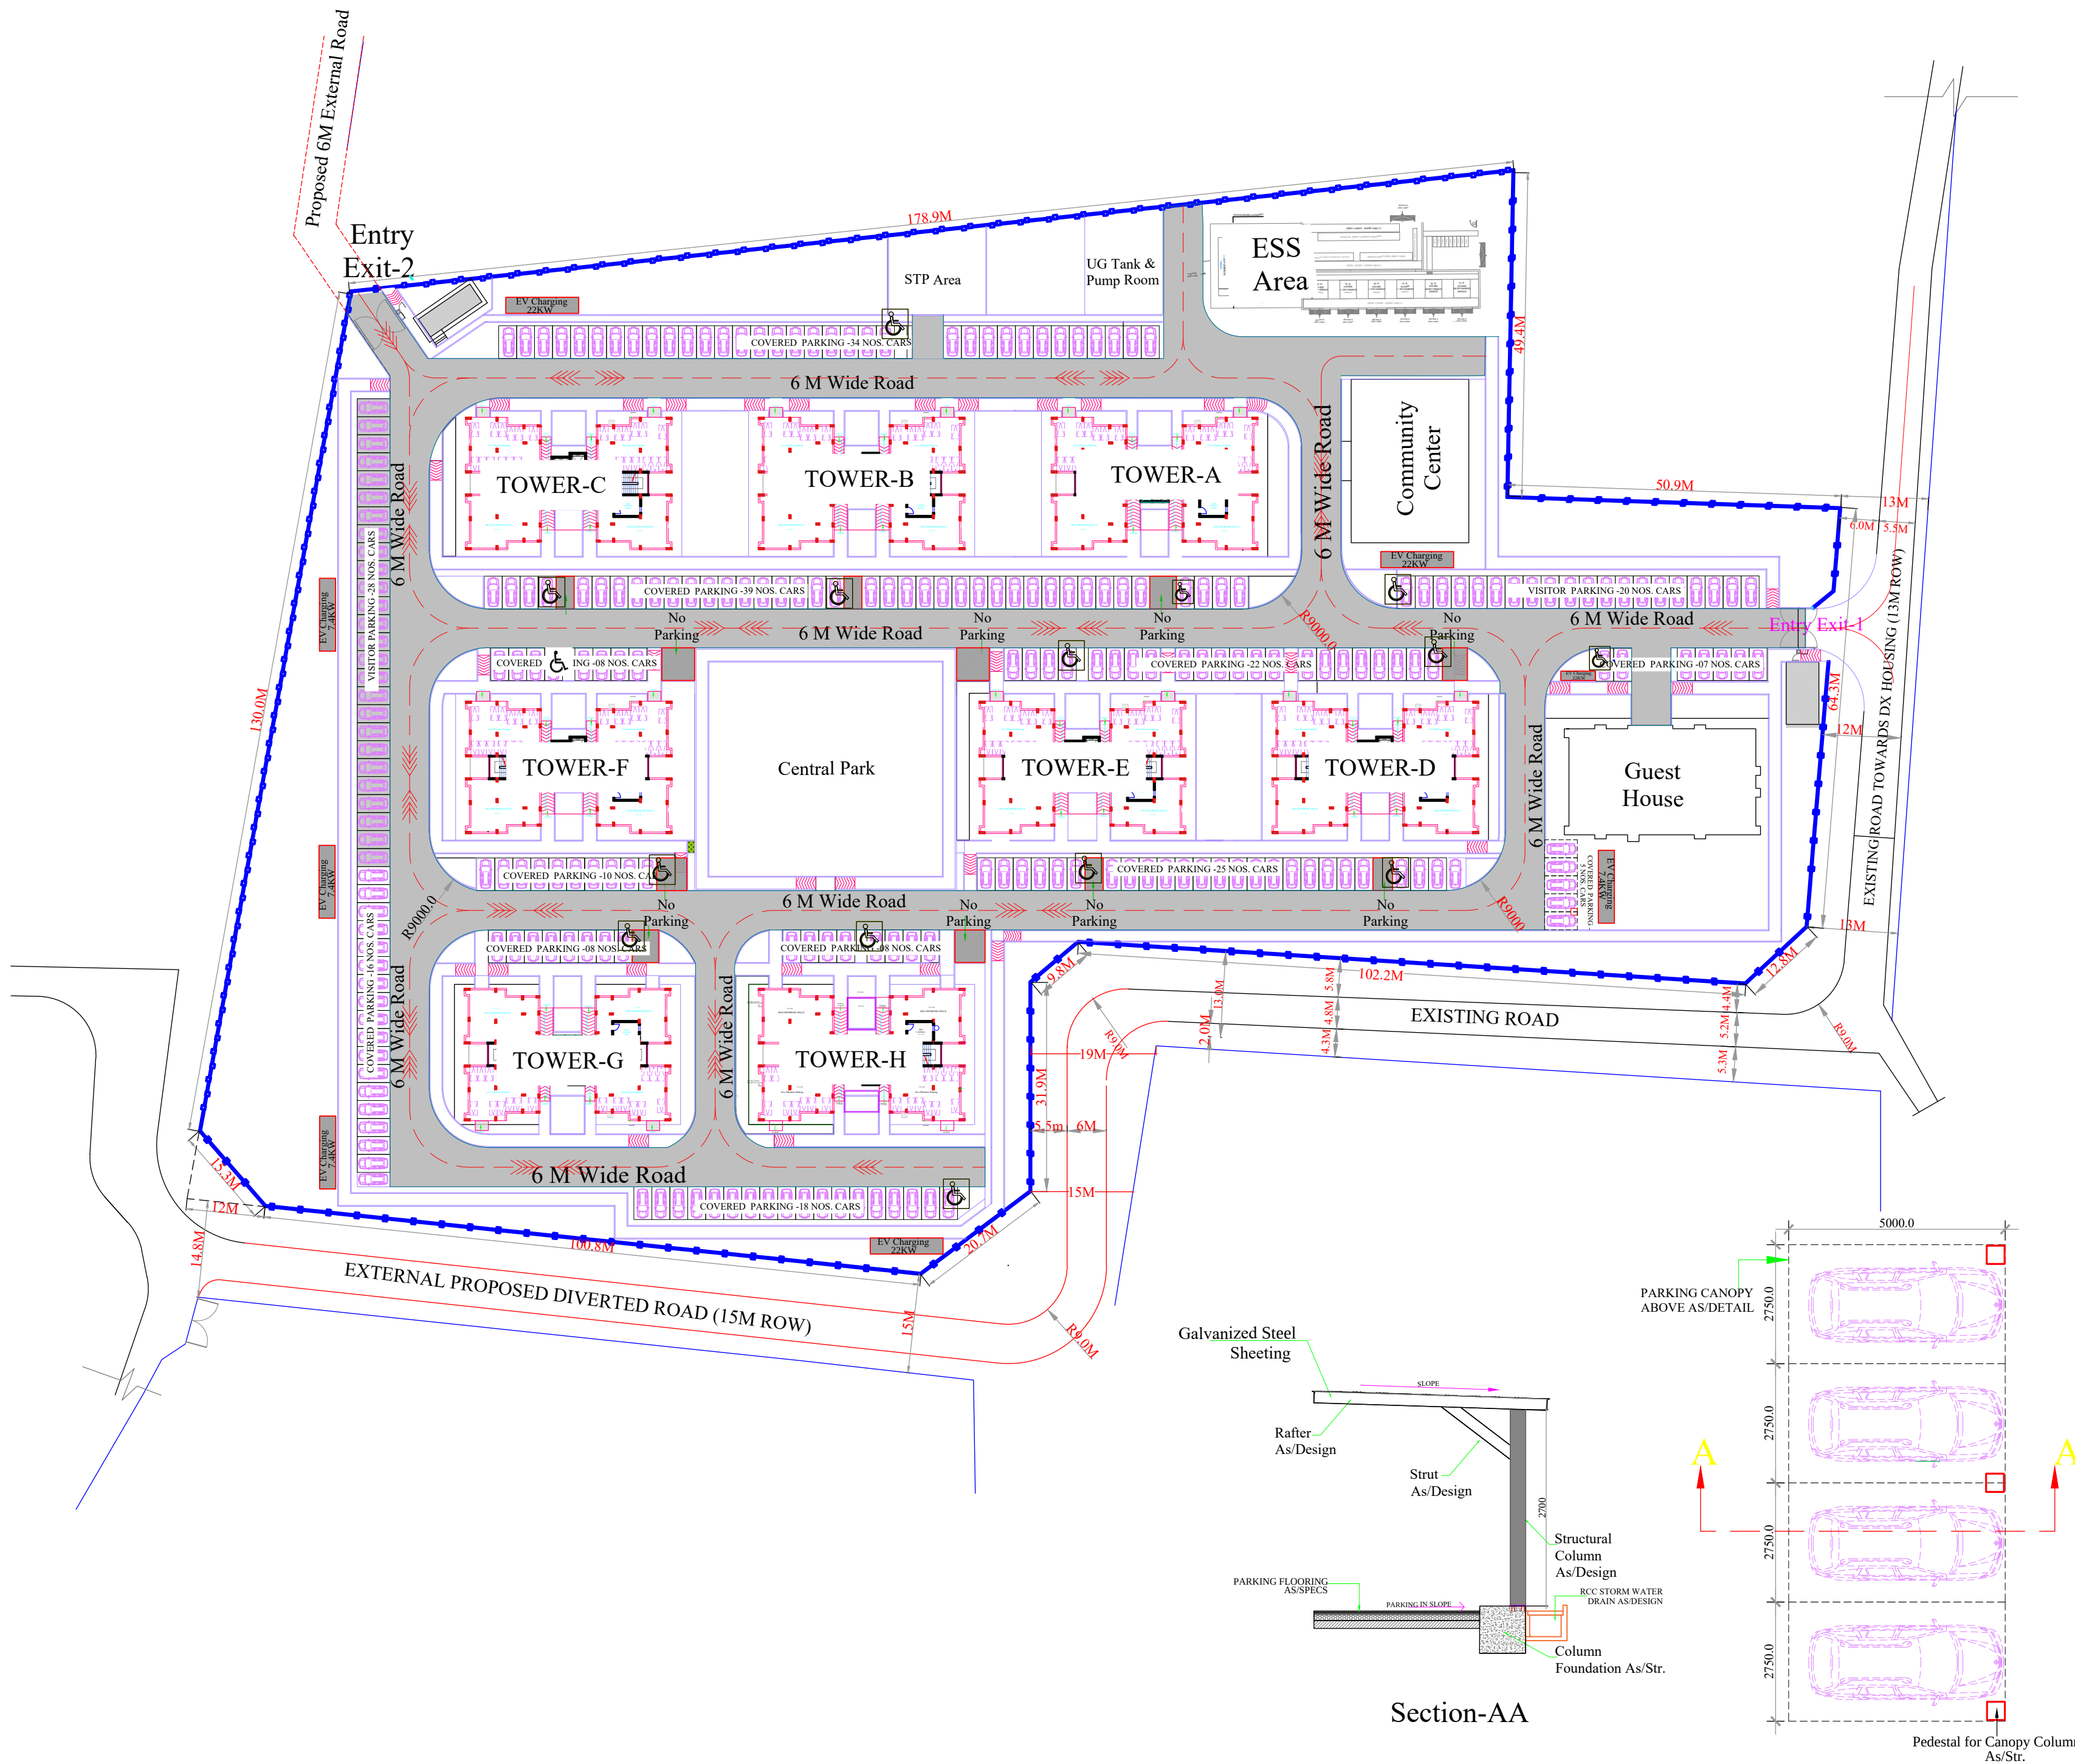




PARKING PROVISION			
01	Parking for Housing Blocks (Covered Parking)	192	248 ECS
02	Parking for Guest House (Covered Parking)	8	
03	Parking for Visitors (Open Parking)	48	192
04	Two Wheelers Parking (Stilt Parking)	192	

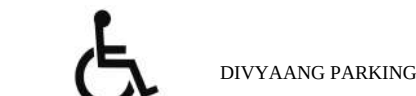

- NOTES
1. WRITTEN DIMENSIONS ARE TO BE FOLLOWED. DRAWINGS ARE NOT TO BE SCALED.
 2. ANY DISCREPANCY IN THE DRAWING SHALL BE BROUGHT TO THE NOTICE OF THE ENGINEER.
 3. THIS DRAWING SHALL BE READ IN CONJUNCTION WITH OTHER RELEVANT DRAWINGS.
 4. PARKING CANOPY DRAWING IS INDICATIVE ONLY. SHOP DRAWING TO BE PREPARED FOR APPROVAL.
 5. EV CHARGING LOCATION SHOWN IN DRAWING IS TENTATIVE AND FINAL LOCATION SHALL BE APPROVED BY ENGINEER IN CHARGE.

TENDER DRAWING

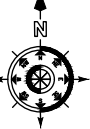CLIENT	 OIL INDIA LIMITED (A Govt. of India Enterprise)	
CONSULTANT	 RITES THE INFRASTRUCTURE PEOPLE (A Govt. of India Enterprise)	
PROJECT	BQ WORKMEN HOUSING	
BUILDING	SITE LAYOUT	
DRAWING TITLE	PARKING LAYOUT	
DRG. NO.	MITES/BLD/AR/TD/002	
NORTH	SCALE	DATE
	NTS	JULY 2025

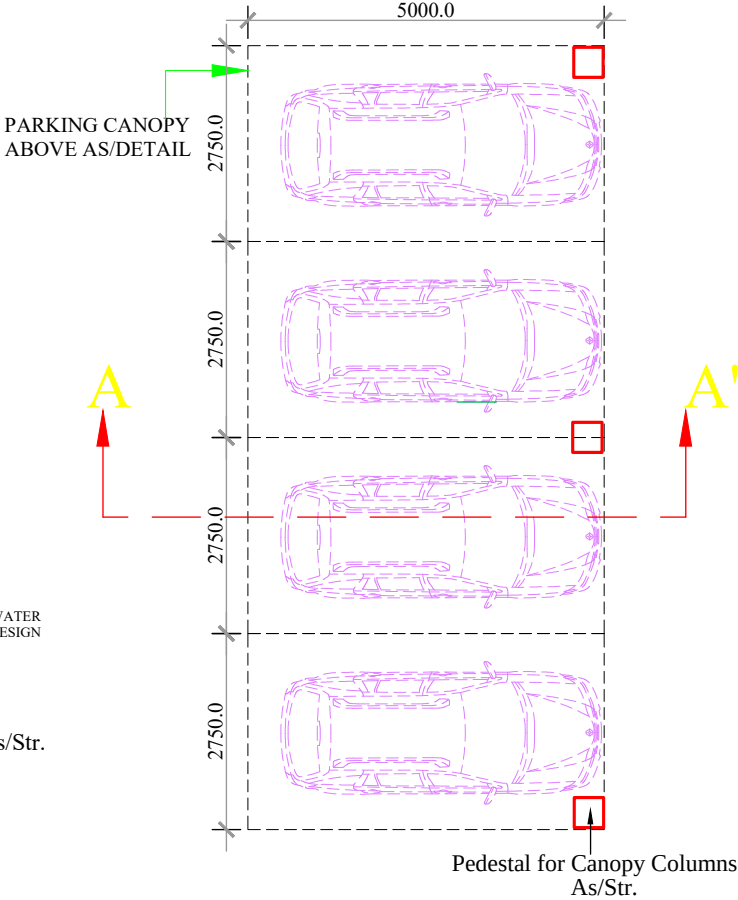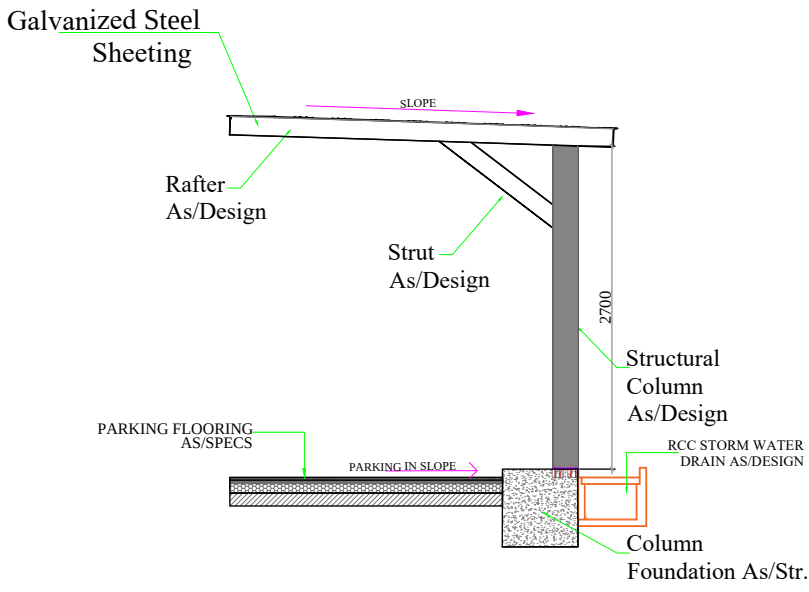



NAME	BOTNICAL NAME	SYMBOL	FOLIAGE DIA.	HEIGHT	NOS.
Ashoka	Polyalthia Longifolia		3 M	12 M	88
Maulsri (Bakul)	Mimusops Elengi		8 M	15 M	45
Queen's Crape Myrtle	Lagerstroemia Flosreginae		6 M	10 M	64
Arjuna	Terminalia Arjuna		6 M	10 M	32
Neem	Azadirachta Indica		8 M	12 M	45
Shrubs and Ground Cover	Ixora coccinea		-	-	-
	Hibiscus rosa-sinensis		-	-	-
	Duranta Erecta		-	-	-
FOXTAIL FERN (ASPARAGUS DENSIFLORUS)			-	-	-
EXISTING TREES PROTECTED APPROX.					26

NOTES

1. WRITTEN DIMENSIONS ARE TO BE FOLLOWED. DRAWINGS ARE NOT TO BE SCALED.
2. ANY DISCREPANCY IN THE DRAWING SHALL BE BROUGHT TO THE NOTICE OF THE ENGINEER.
3. THIS DRAWING SHALL BE READ IN CONJUNCTION WITH OTHER RELEVANT DRAWINGS.
4. THE DRAWING IS INDICATIVE ONLY
5. THE NUMBER OF PROPOSED TREES MAY VARY DEPENDING ON SITE DEVELOPMENT AND SPACE AVAILABILITY

GREEN AREA APPROX. : 6000 SQM

TENDER DRAWING

CLIENT
 OIL INDIA LIMITED
(A Govt. of India Enterprise)

CONSULTANT
 RITES
THE INFRASTRUCTURE PEOPLE
(A Govt. of India Enterprise)







PROJECT
BQ WORKMEN HOUSING

BUILDING
SITE LAYOUT

DRAWING TITLE
LANDSCAPE LAYOUT

DRG. NO.
RITES/BLD/AR/TD/003

NORTH 	SCALE NTS	DATE JULY 2025
-----------	--------------	-------------------

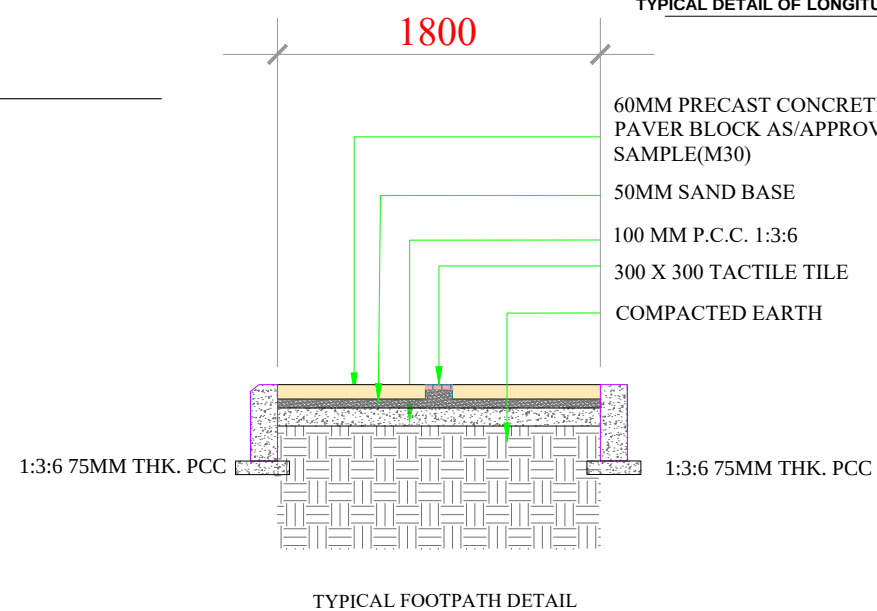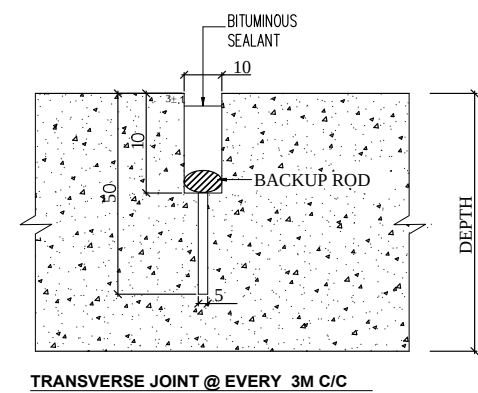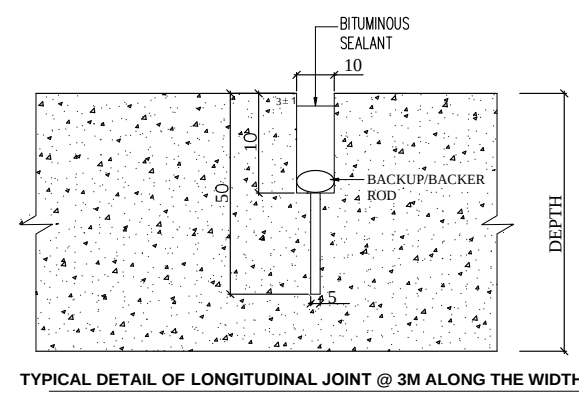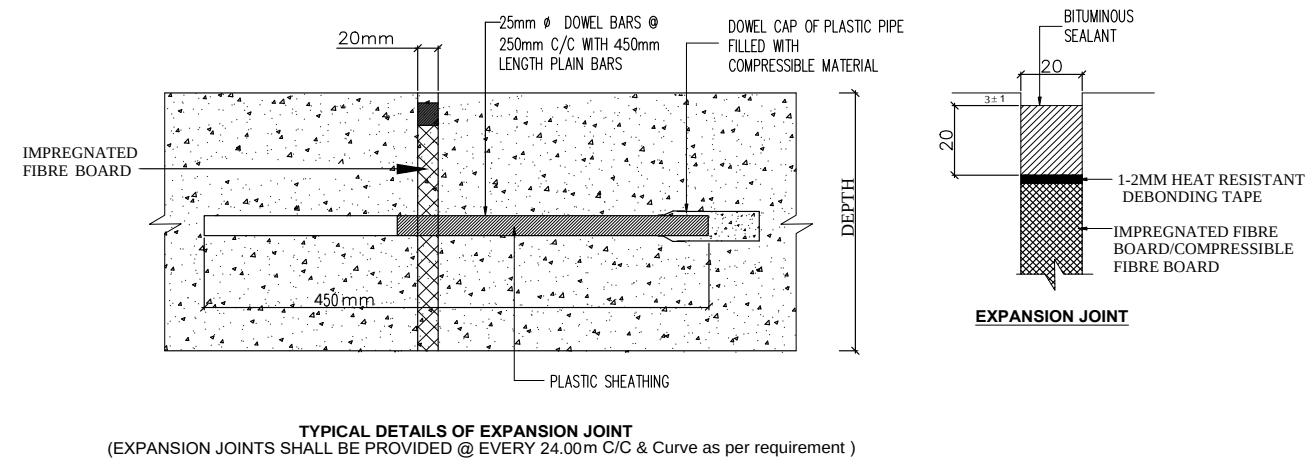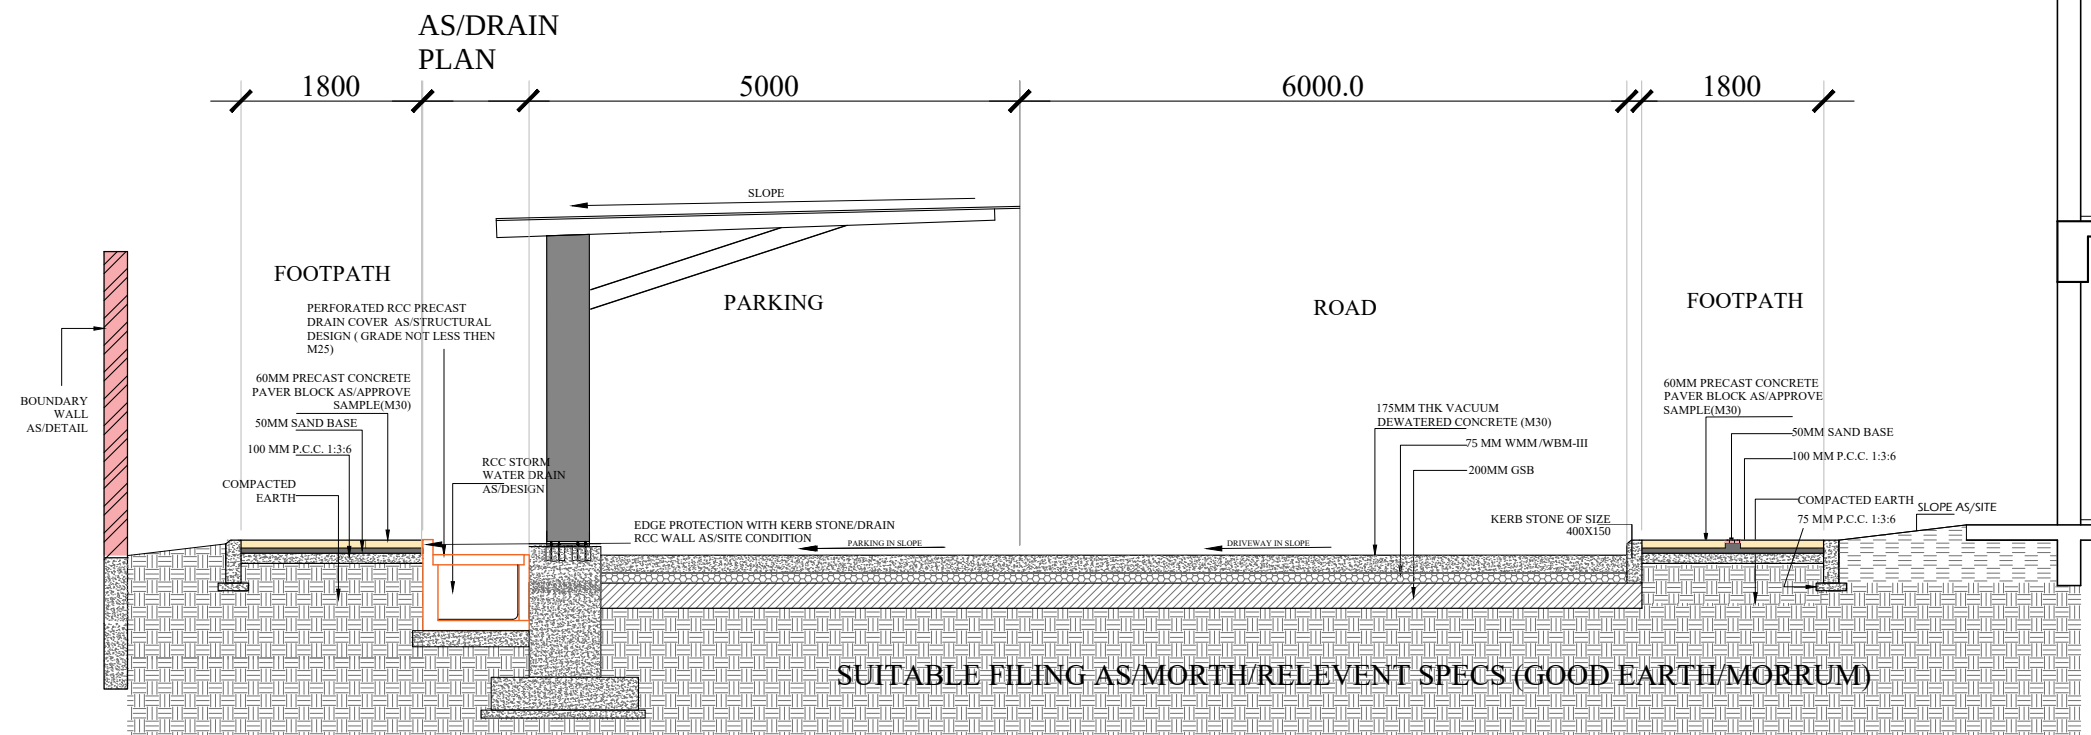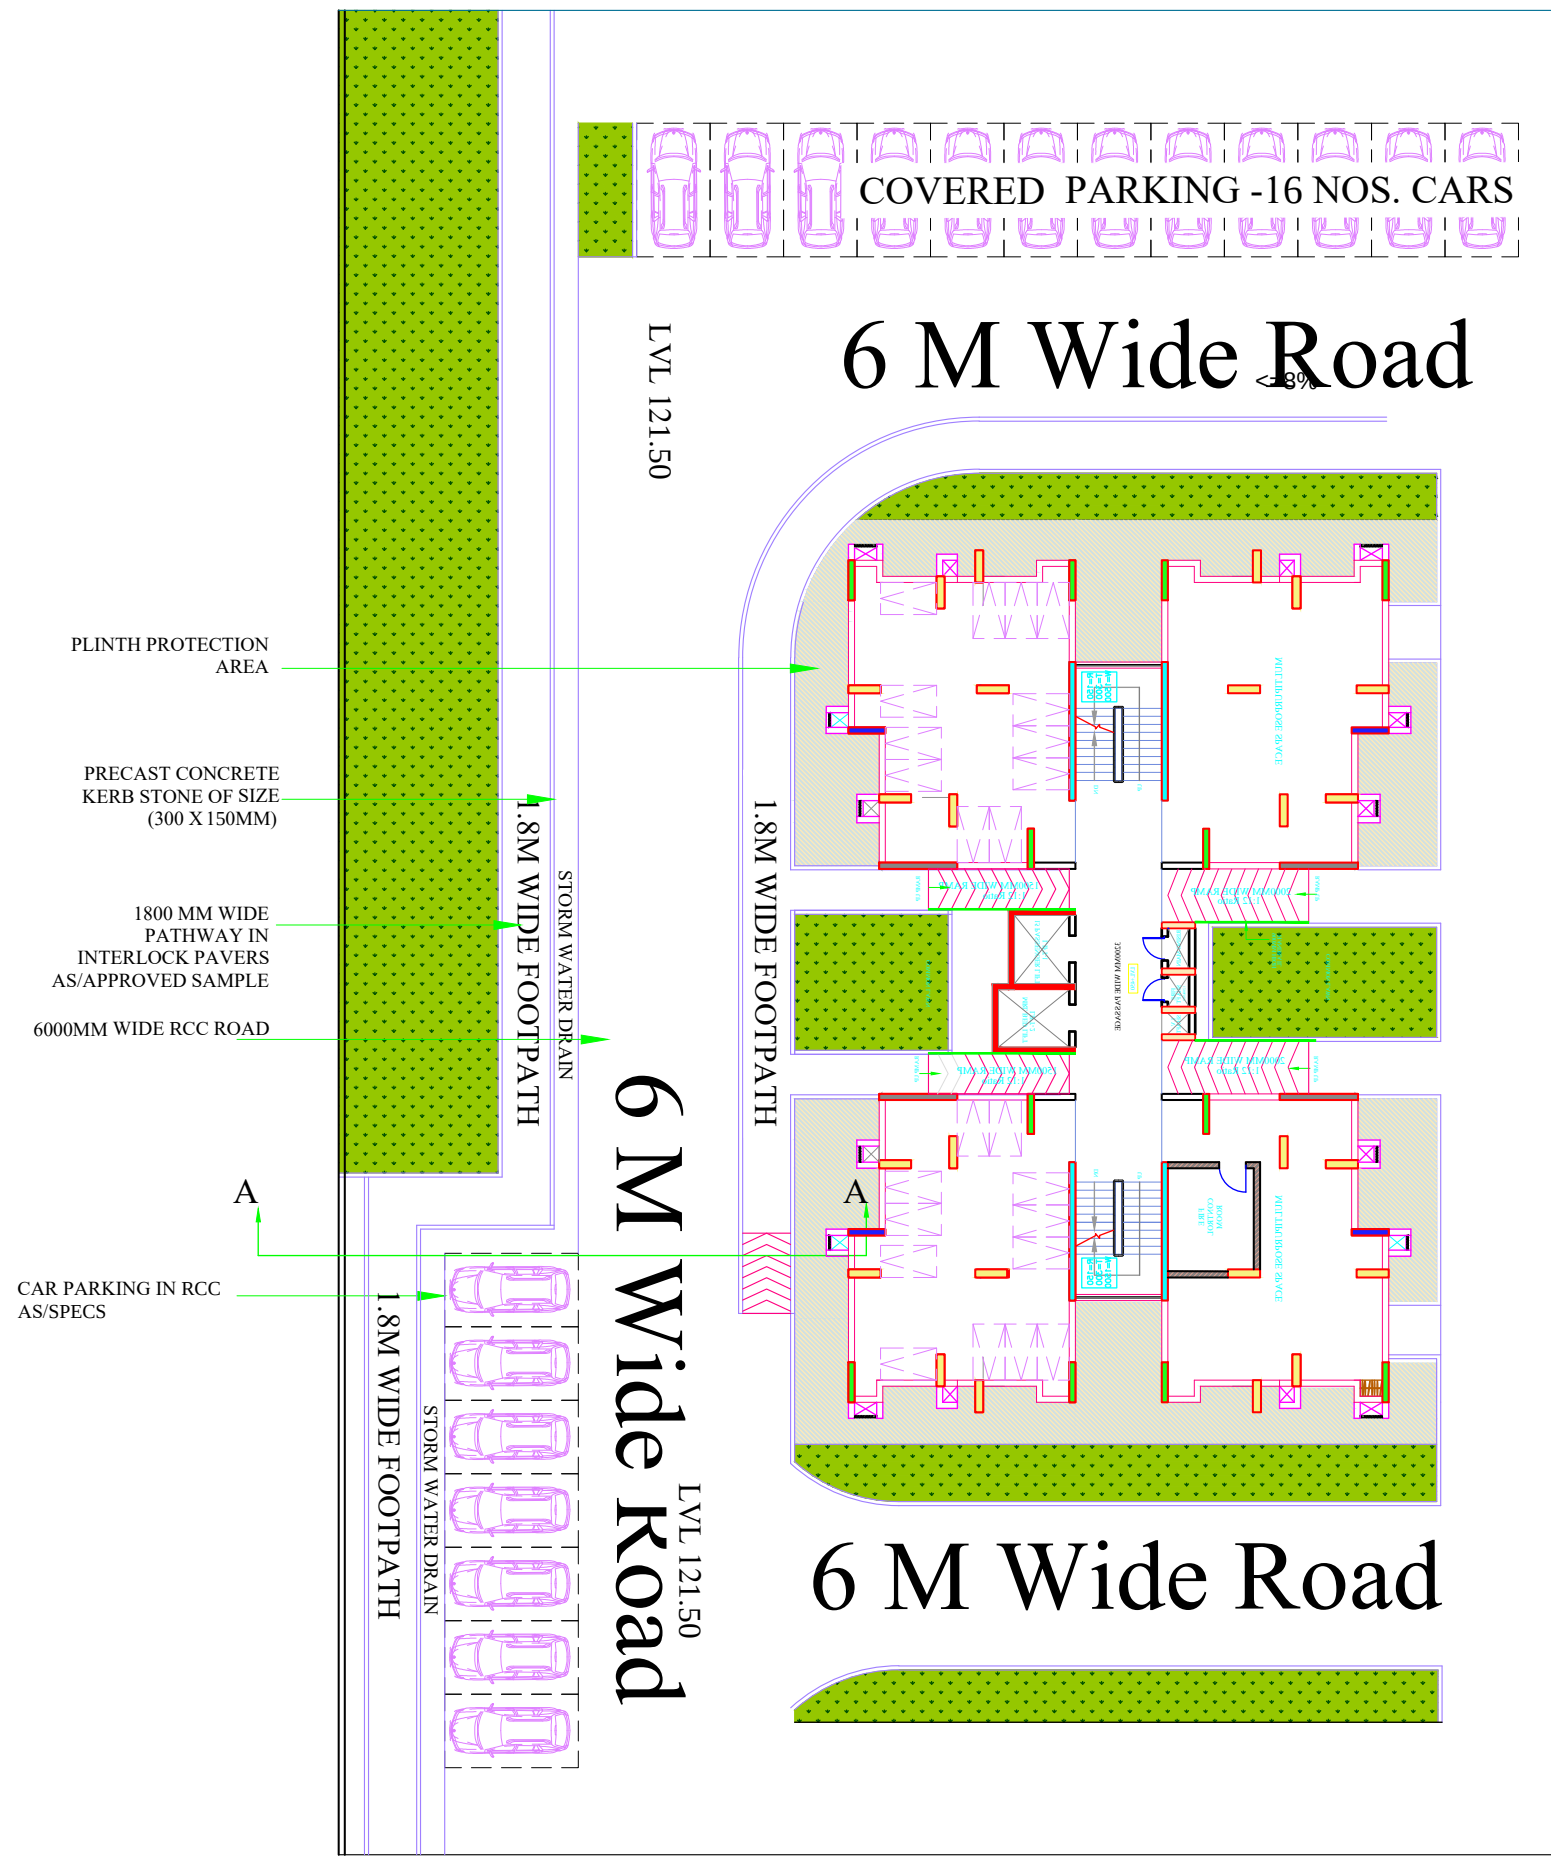

NOTES

1. ALL DIMENSIONS ARE IN MM; UNLESS NOTED OTHERWISE.
2. WRITTEN DIMENSIONS ARE TO BE FOLLOWED. DRAWINGS ARE NOT TO BE SCALED.
3. ANY DISCREPANCY IN THE DRAWING SHALL BE BROUGHT TO THE NOTICE OF THE ENGINEER.
4. THIS DRAWING SHALL BE READ IN CONJUNCTION WITH OTHER RELEVANT DRAWING AND SPECIFICATION.

TENDER DRAWING

CLIENT



CONSULTANT



PROJECT

BQ WORKMEN HOUSING

BUILDING

SITE LAYOUT


DRAWING TITLE

PART SECTION DETAIL

DRG. NO.

MITES/BLD/AR/TD/004

NORTH

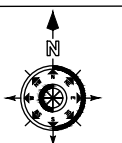


SCALE

NTS

DATE

JULY 2025

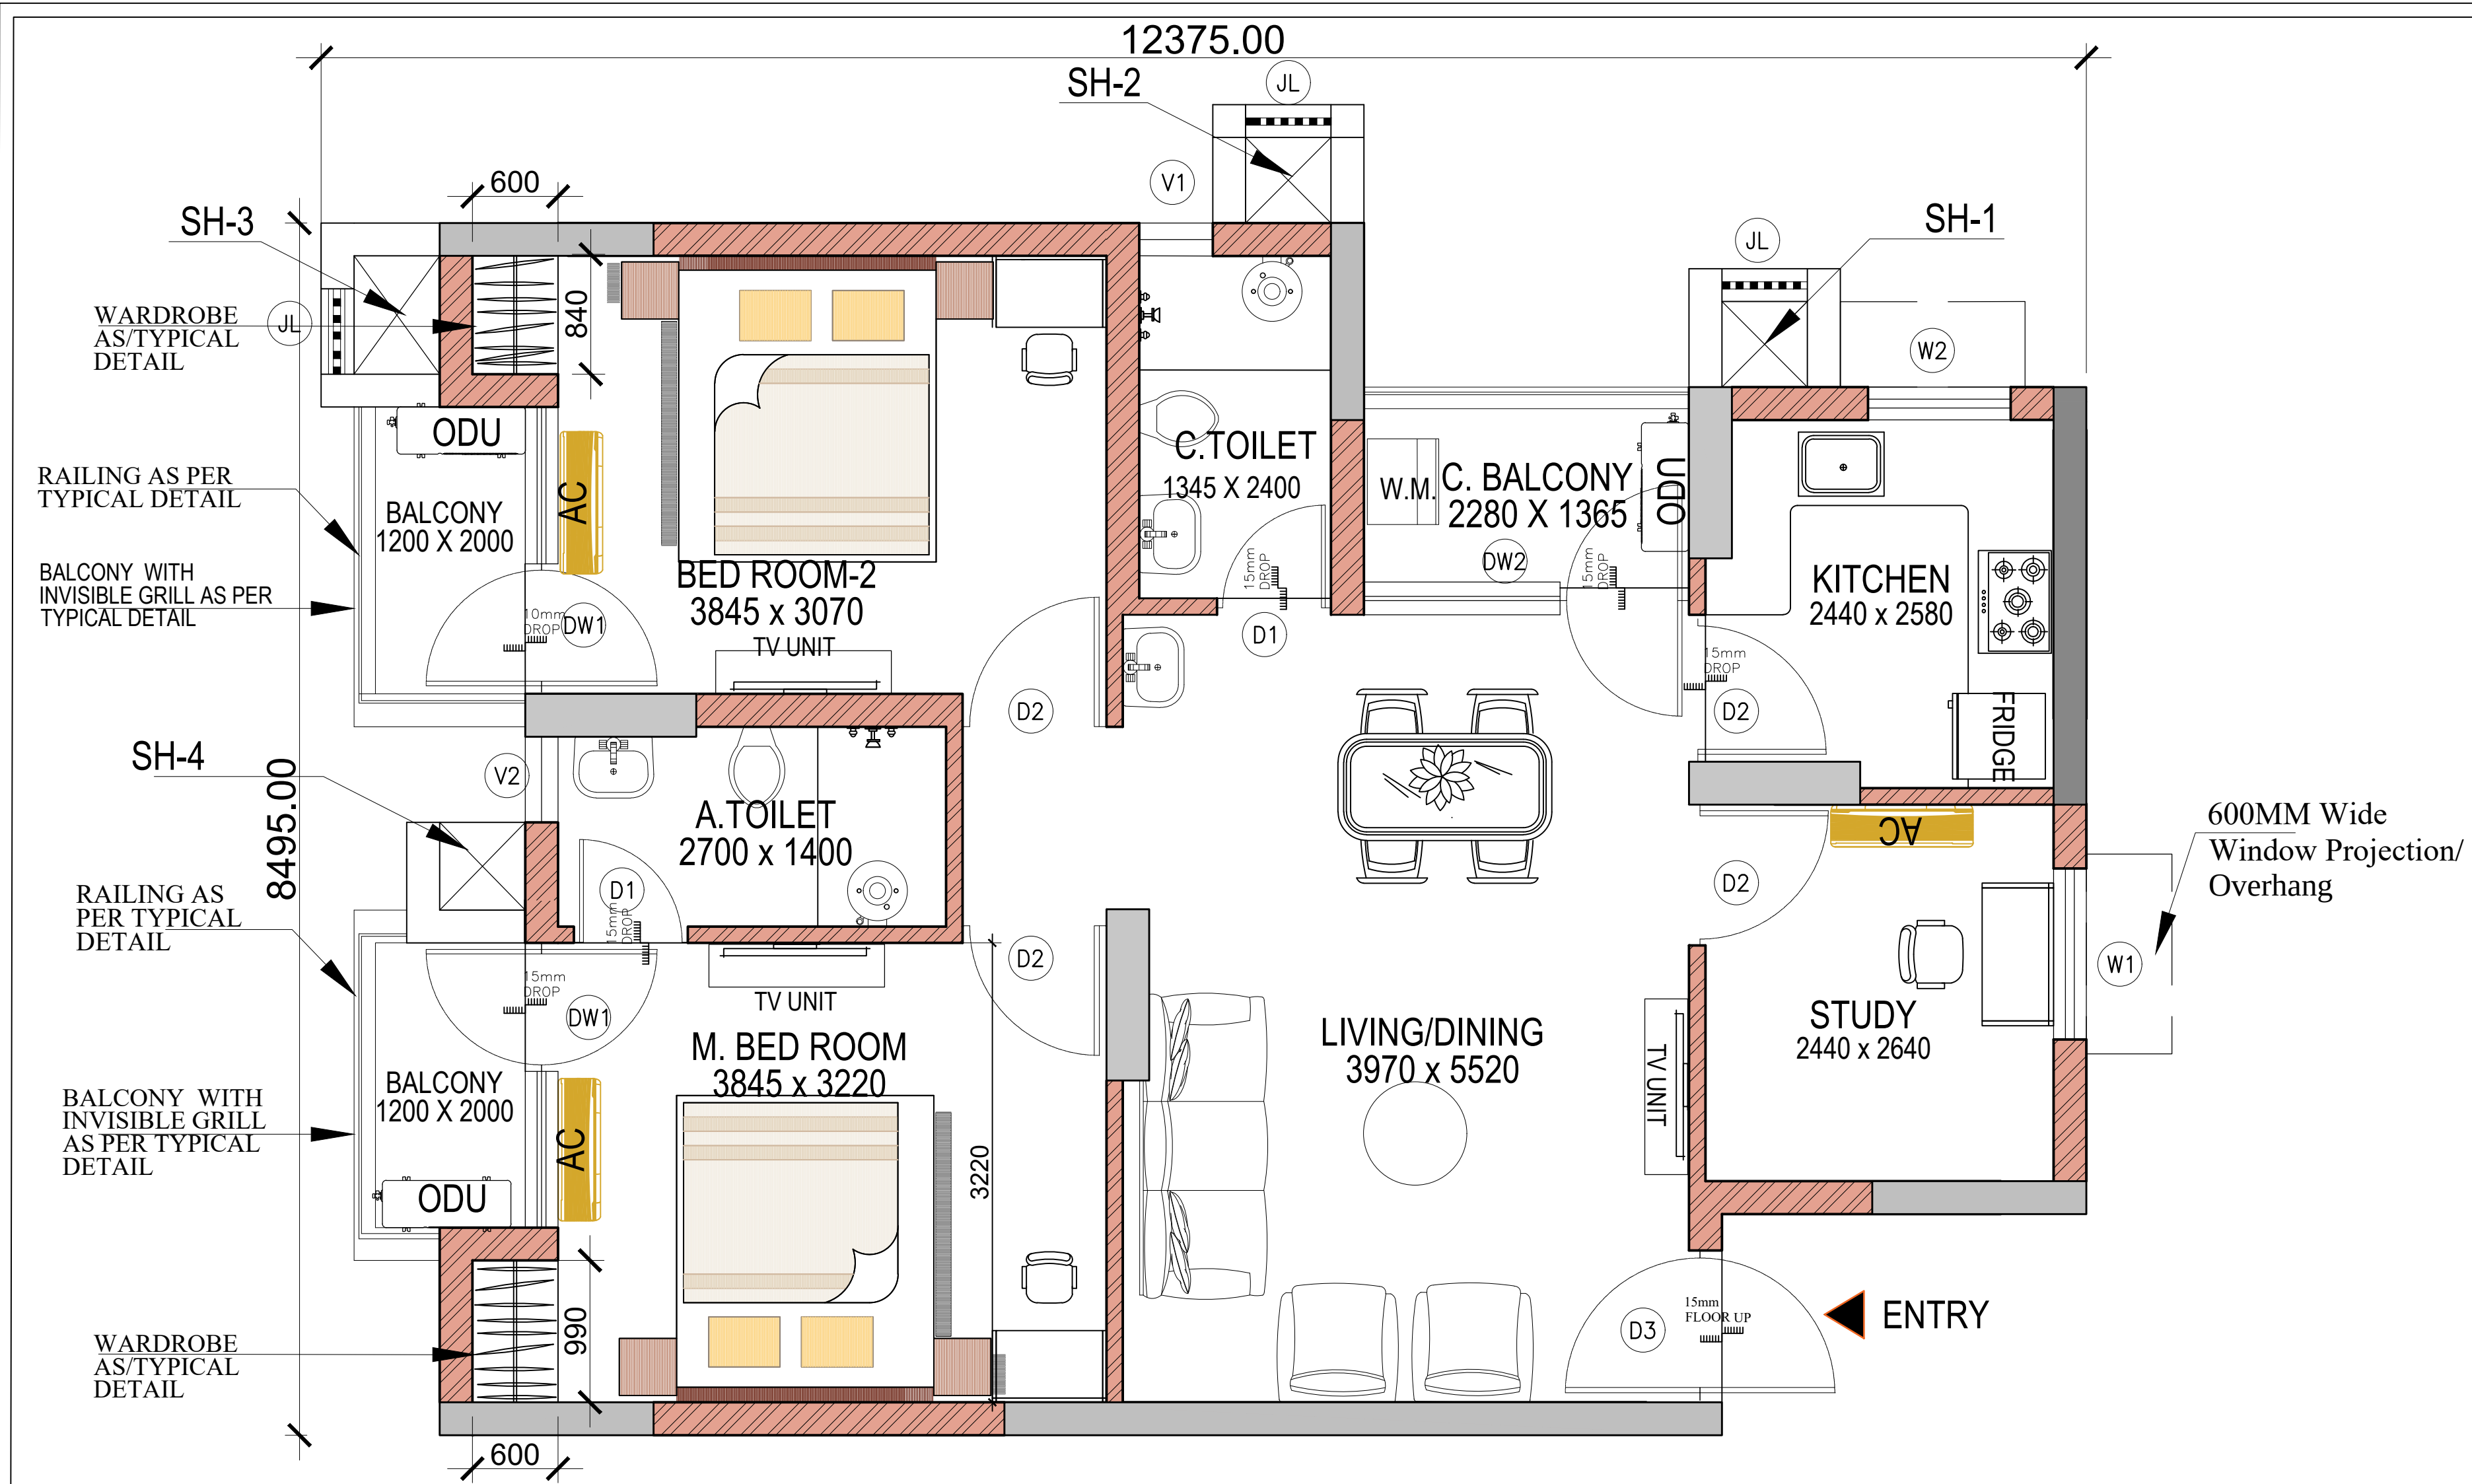

BQ HOUSING BLOCK SCHEDULE OF DOORS

SCHEDULE OF DOORS - (Ground floor to Terrace floor)							
SL. NO	TYPE	NOS.	WIDTH	HEIGHT (from FFL.)	CILL (from FFL.)	LINTEL (from FFL.)	LOCATION
REMARKS							
SCHEDULE OF DOORS							
1.	D1	---	800	2100	00	2100	TOILETS
2.	D2	---	1000	2100	00	2100	BED RM/KITCHEN/STUDY/ FIRE CONTROL ROOM
3.	D3	---	1050	2100	00	2100	MAIN ENTRY
4.	DW1	---	2000	2100	00	2100	BALCONY
5.	DW2	---	2295	2100	00	2100	C. BALCONY
6.	SD1	---	900	2100	100	2100	ELECT.SHAFT
7.	SD2	---	600	2100	100	2100	LV SHAFT
8.	SD3	---	900	2100	100	2100	FHC SHAFT
9.	SD4	---	1200	2100	100	2100	MUMTY
							SINGLE LEAF WPC FRAME, WPC FLUSH DOOR AS/DRAWING/SPECS
							SINGLE LEAF TEAK WOOD FRAME, FLUSH DOOR AS/DRAWING/SPECS
							SINGLE LEAF TEAK WOOD FRAME FOR DOUBLE SHUTTER, FLUSH DOOR & WIRE MESH DOOR SHUTTER AS/DRAWING/SPECS
							SINGLE LEAF TEAK WOOD FRAME FOR DOUBLE SHUTTER, FLUSH DOOR, WIRE MESH DOOR SHUTTER & CASEMENT WINDOW WITH WIRE MESH SHUTTER AS/DRAWING/SPECS
							SINGLE LEAF TEAK WOOD FRAME FOR DOUBLE SHUTTER, FLUSH DOOR, WIRE MESH DOOR SHUTTER & CASEMENT WINDOW WITH WIRE MESH SHUTTER AS/DRAWING/SPECS
							DOUBLE LEAF MS DOOR (Electrical Shaft Door as per NBC & latest CPWD guideline)
							SINGLE LEAF MS DOOR AS/DRAWING/SPECS
							M.S.SINGLE LEAF DOOR WITH GLASS (FHC Shaft Door as per NBC & latest CPWD Guideline)
							M.S. DOUBLE LEAF DOOR AS/DRAWING/SPECS

SCHEDULE OF WINDOWS - (First Floor to Terrace floor)							
SL. NO	TYPE	NOS.	WIDTH	HEIGHT	SILL (from FFL)	LINTEL (from FFL)	REMARKS
1.	W1	---	1200	1200	900	2100	ALUMINUM FRAME- SLIDING WITH WIRE MESH AND MS GRILL AS/DRAWING/SPECS
2.	W2	---	1000	1225	1225	2450	ALUMINUM FRAME- SLIDING WITH WIRE MESH AND MS GRILL AS/DRAWING/SPECS
3.	W3	---	2300	1100	1000 (from staircase landing FFL)	2100 (from staircase landing FFL)	ALUMINUM FRAME- PARTLY SLIDING CUM FIXED PANELS WINDOW & MS GRILL AS/DRAWING/SPECS
4.	W4	---	1200	1200	900	2100	ALUMINUM FRAME- SLIDING SHUTTERS AS/DRAWING/SPECS
SCHEDULE OF VENTILATORS - (First Floor to Terrace floor)							
SL. NO	TYPE	NOS.	WIDTH	HEIGHT	SILL (from FFL)	LINTEL (from FFL)	REMARKS
1.	V1	---	515	875	1225	2100	ALUMINUM FRAME- VENTILATORS FIXED FROSTED GLASS PANELS WITH EXHUST FAN AS/DRAWING/SPECS
2.	V2	---	615	875	1225	2100	ALUMINUM FRAME- VENTILATORS FIXED FROSTED GLASS PANELS WITH EXHUST FAN AS/DRAWING/SPECS
SCHEDULE OF SHAFT JALI - (Ground floor to Terrace floor)							
SL. NO	TYPE	NOS.	WIDTH	HEIGHT	CILL (from FFL)	LINTEL (from FFL)	REMARKS
1.	JL	---	600	2550	+00	BEAM BOTTOM	ALUMINUM FRAME- OPENABLE LOUVERED PANEL

KEY PLAN

NOTES

TYPICAL UNIT AREA= 90 SQ.M.

TYPICAL CARPET AREA= 69 SQ.M.

SHAFT SCHEDULE

SL. NO	TYPE	WIDTH	LENGTH	REMARKS
1.	SH-01	600	600	KITCHEN PLUMBING SHAFT
2.	SH-02	600	600	TOILET PLUMBING SHAFT
3.	SH- 03	600	840	RAIN WATER PIPE SHAFT
4.	SH- 04	600	600	TOILET PLUMBING SHAFT
5.	SH-05	1500	800	RISING MAIN SHAFT
6.	SH-06	1200	800	FIRE H.SHAFT
7.	SH- 07	800	800	LV SHAFT

TENDER DRAWING

CLIENT

CONSULTANT

PROJECT

BUILDING

DRAWING TITLE

ORG. NO.

NORTH

SCALE

DATE

OIL INDIA LIMITED
(A Govt. of India Enterprise)

RITES
THE INFRASTRUCTURE PEOPLE
(A Govt. of India Enterprise)

BQ WORKMEN HOUSING

HOUSING BLOCK (G+6)


TYPICAL UNIT PLAN

NTS

JULY 2025

600MM Wide Window Projection/Overhang

ENTRY

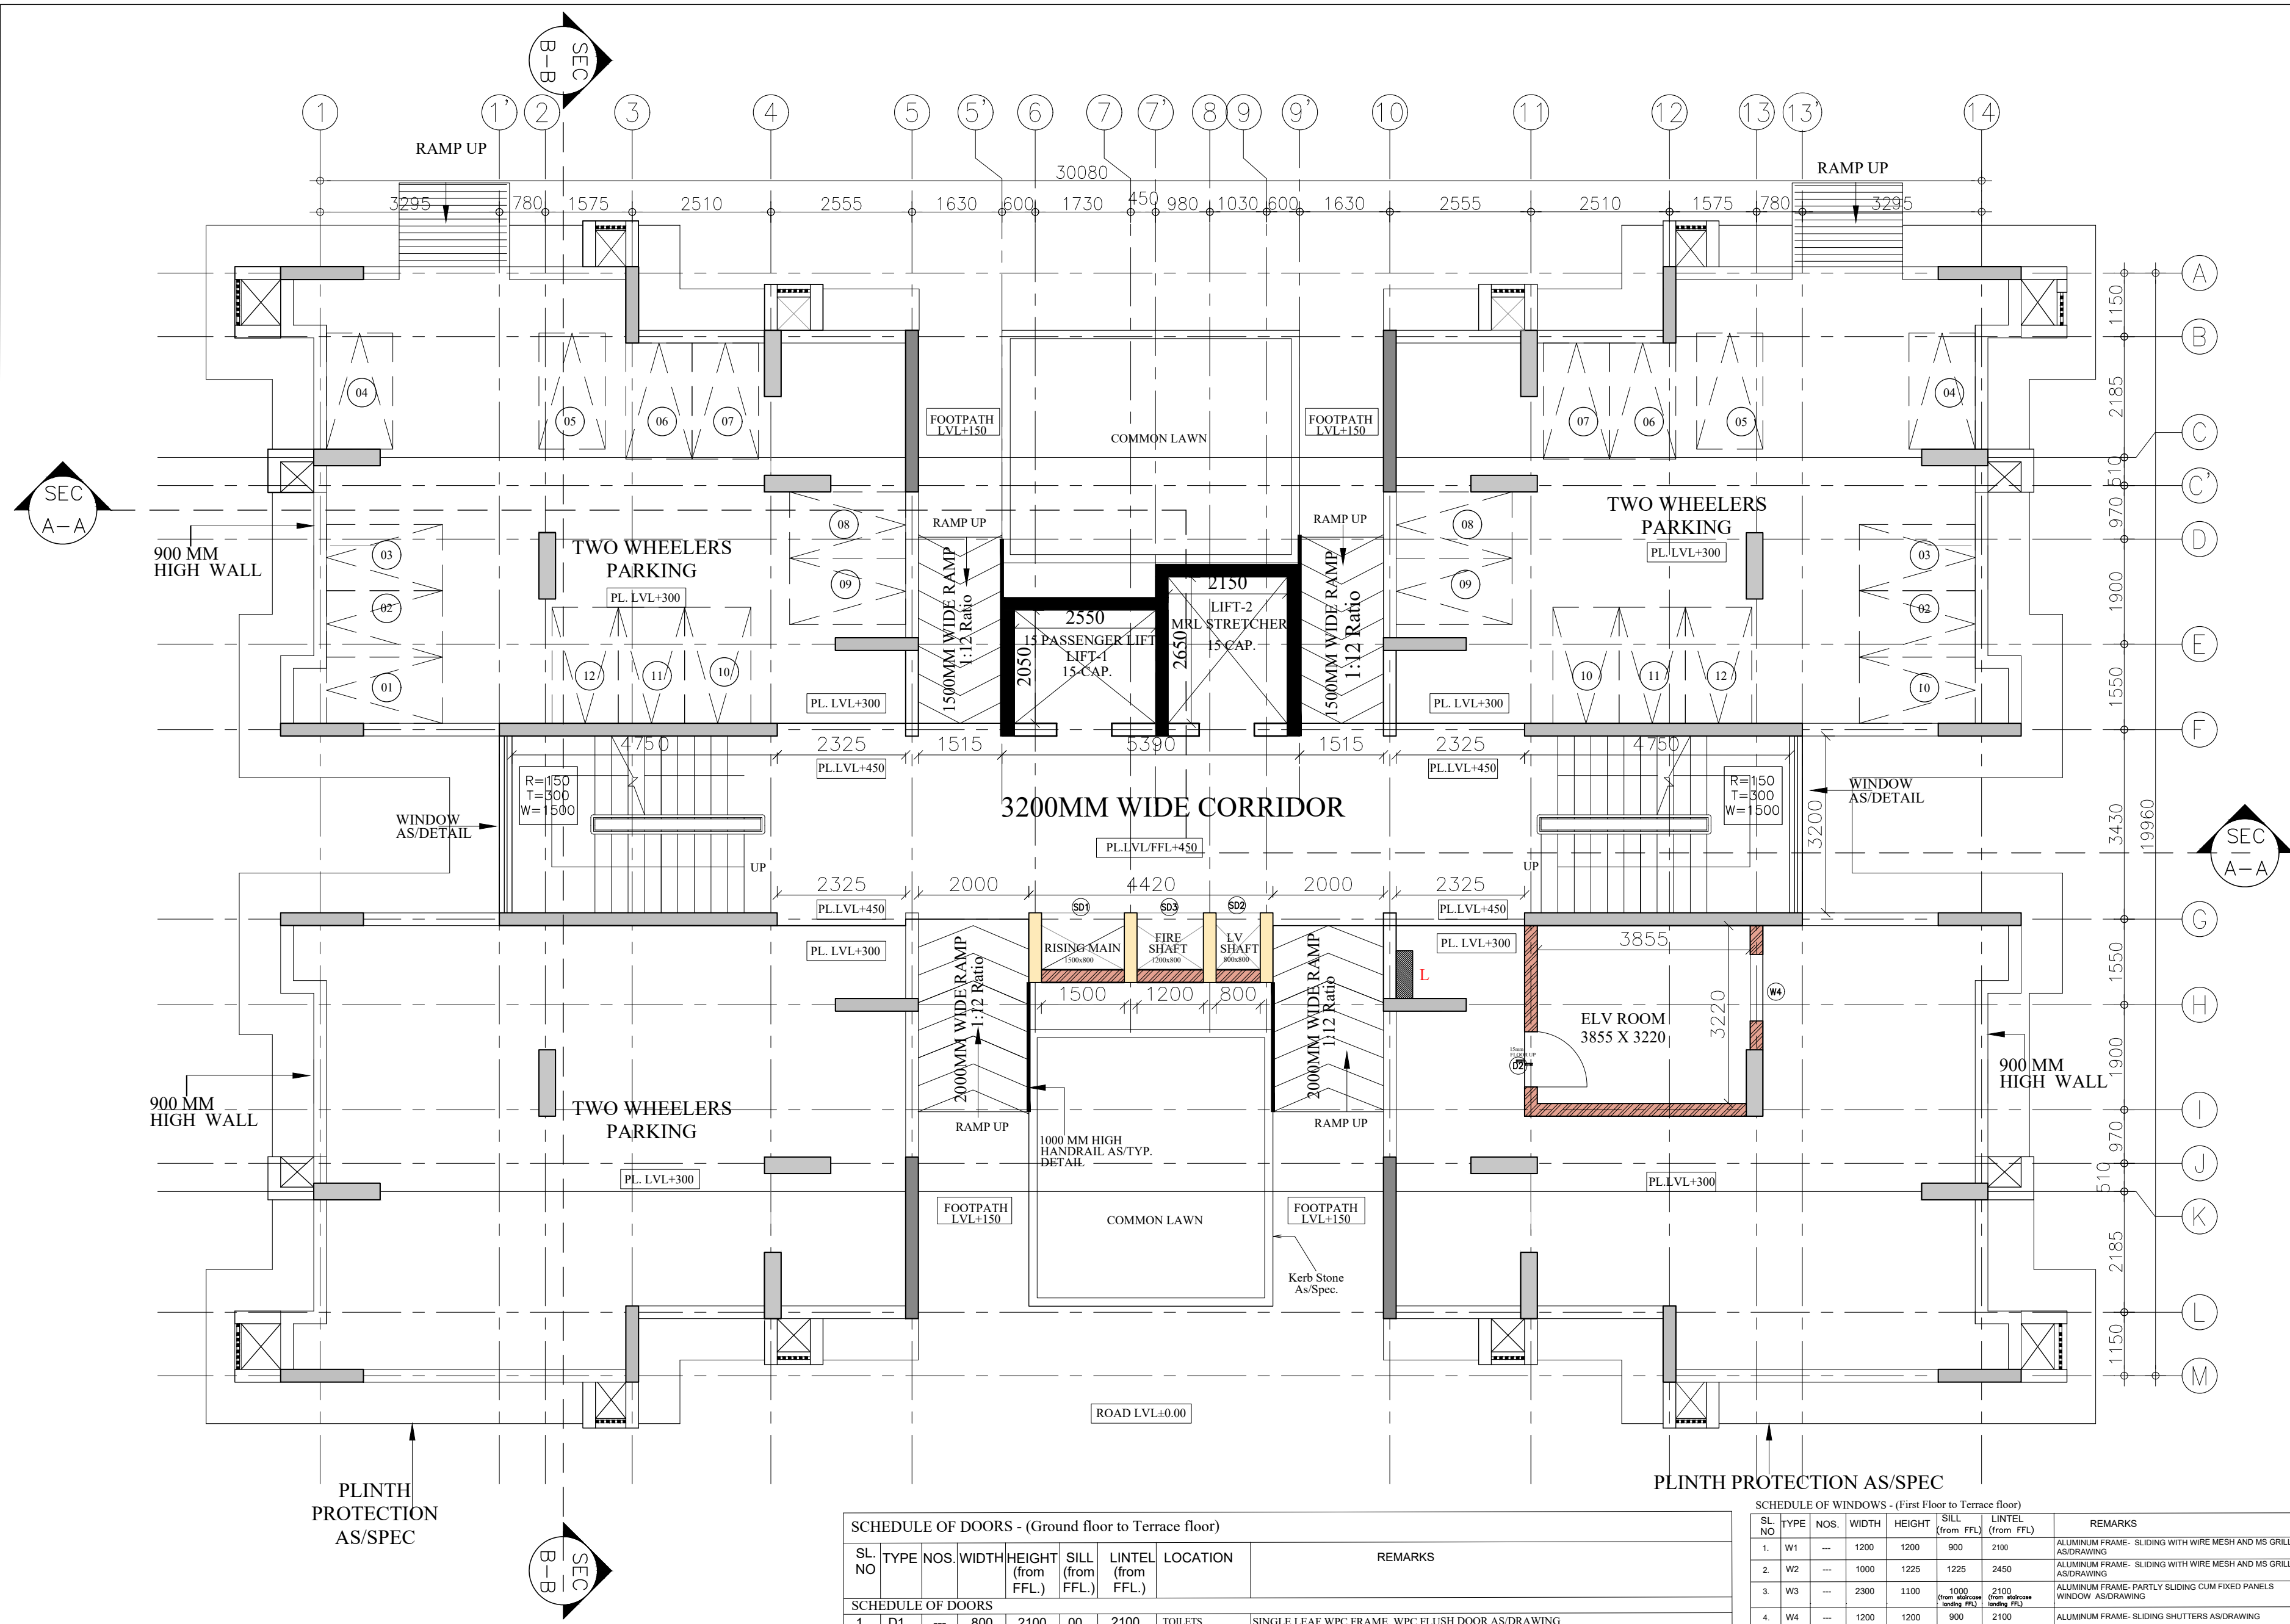

KEY PLAN

NOTES

TYPICAL FLOOR AREA= 483.60 SQ.M.

NO. OF TWO WHEELERS PARKING=24

SHAFT SCHEDULE

SL. NO	TYPE	WIDTH	LENGTH	REMARKS
1.	SH-01	600	600	KITCHEN PLUMBING SHAFT
2.	SH-02	600	600	TOILET PLUMBING SHAFT
3.	SH-03	600	840	RAIN WATER PIPE SHAFT
4.	SH-04	600	600	TOILET PLUMBING SHAFT
5.	SH-05	1500	800	RIISING MAIN SHAFT
6.	SH-06	1200	800	FIRE H.SHAFT
7.	SH-07	800	800	LV SHAFT

L- LETTER BOX TO BE PROVIDED AT EACH TOWER

TENDER DRAWING

CLIENT

OIL INDIA LIMITED
(A Govt. of India Enterprise)

CONSULTANT

RITES
THE INFRASTRUCTURE PEOPLE
(A Govt. of India Enterprise)

PROJECT

BQ WORKMEN HOUSING

BUILDING

HOUSING BLOCK (G+6)

DRAWING TITLE

TYPICAL STILT FLOOR PLAN

DRG. NO.

MITES/BLD/AR/TD/006

NORTH

SCALE


NTS

DATE

JULY 2025

SCHEDULE OF DOORS - (Ground floor to Terrace floor)							REMARKS
SL. NO	TYPE	NOS.	WIDTH	HEIGHT (from FFL.)	SILL (from FFL.)	LINTEL (from FFL.)	
SCHEDULE OF DOORS							
1.	D1	---	800	2100	00	2100	TOILETS SINGLE LEAF WPC FRAME, WPC FLUSH DOOR AS/DRAWING
2.	D2	---	1000	2100	00	2100	BEDROOM/KITCHEN STUDY SINGLE LEAF TEAK WOOD FRAME, FLUSH DOOR AS/DRAWING
3.	D3	---	1050	2100	00	2100	MAIN ENTRY SINGLE LEAF TEAK WOOD FRAME, FLUSH DOOR & WIRE MESH DOOR SHUTTER AS/DRAWING
4.	DW1	---	2000	2100	00	2100	BALCONY SINGLE LEAF TEAK WOOD FRAME, FLUSH DOOR, WIRE MESH DOOR SHUTTER & CASEMENT WINDOW WITH WIRE MESH SHUTTER
5.	DW2	---	2295	2100	00	2100	C. BALCONY SINGLE LEAF TEAK WOOD FRAME, FLUSH DOOR, WIRE MESH DOOR SHUTTER & CASEMENT WINDOW WITH WIRE MESH SHUTTER
6.	SD1	---	900	2100	100	2100	ELECT. SHAFT DOUBLE LEAF MS DOOR (Electrical Shaft Door as per NBC & latest CPWD guideline)
7.	SD2	---	600	2100	100	2100	LV. SHAFT SINGLE LEAF MS DOOR
8.	SD3	---	900	2100	100	2100	FHC SHAFT M.S. SINGLE LEAF DOOR WITH GLASS (FHC Shaft Door as per NBC & latest CPWD Guideline)
9.	SD4	---	1200	2100	100	2100	MUMTY M.S. DOUBLE LEAF DOOR

SCHEDULE OF WINDOWS - (First Floor to Terrace floor)							REMARKS
SL. NO	TYPE	NOS.	WIDTH	HEIGHT	SILL (from FFL)	LINTEL (from FFL)	
1.	W1	---	1200	1200	900	2100	ALUMINUM FRAME- SLIDING WITH WIRE MESH AND MS GRILL AS/DRAWING
2.	W2	---	1000	1225	1225	2450	ALUMINUM FRAME- SLIDING WITH WIRE MESH AND MS GRILL AS/DRAWING
3.	W3	---	2300	1100	1000 (from window bottom FFL)	2100 (from window bottom FFL)	ALUMINUM FRAME- PARTLY SLIDING CUM FIXED PANELS WINDOW AS/DRAWING
4.	W4	---	1200	1200	900	2100	ALUMINUM FRAME- SLIDING SHUTTERS AS/DRAWING
SCHEDULE OF VENTILATORS - (First Floor to Terrace floor)							REMARKS
SL. NO	TYPE	NOS.	WIDTH	HEIGHT	SILL (from FFL)	LINTEL (from FFL)	
1.	V1	---	515	875	1225	2100	ALUMINUM FRAME- VENTILATORS FIXED PANELS WITH EXHUST FAN AS/DRAWING
1.	V2	---	615	875	1225	2100	ALUMINUM FRAME- VENTILATORS FIXED PANELS WITH EXHUST FAN AS/DRAWING
SCHEDULE OF SHAFT OPENING - (Ground floor to Terrace floor)							REMARKS
SL. NO	TYPE	NOS.	WIDTH	HEIGHT	SILL (from FFL)	LINTEL (from FFL)	
1.	JL	---	600	2550	+00	BEAM BOTTOM	ALUMINUM FRAME- LOUVERED DOOR AS/DRAWING

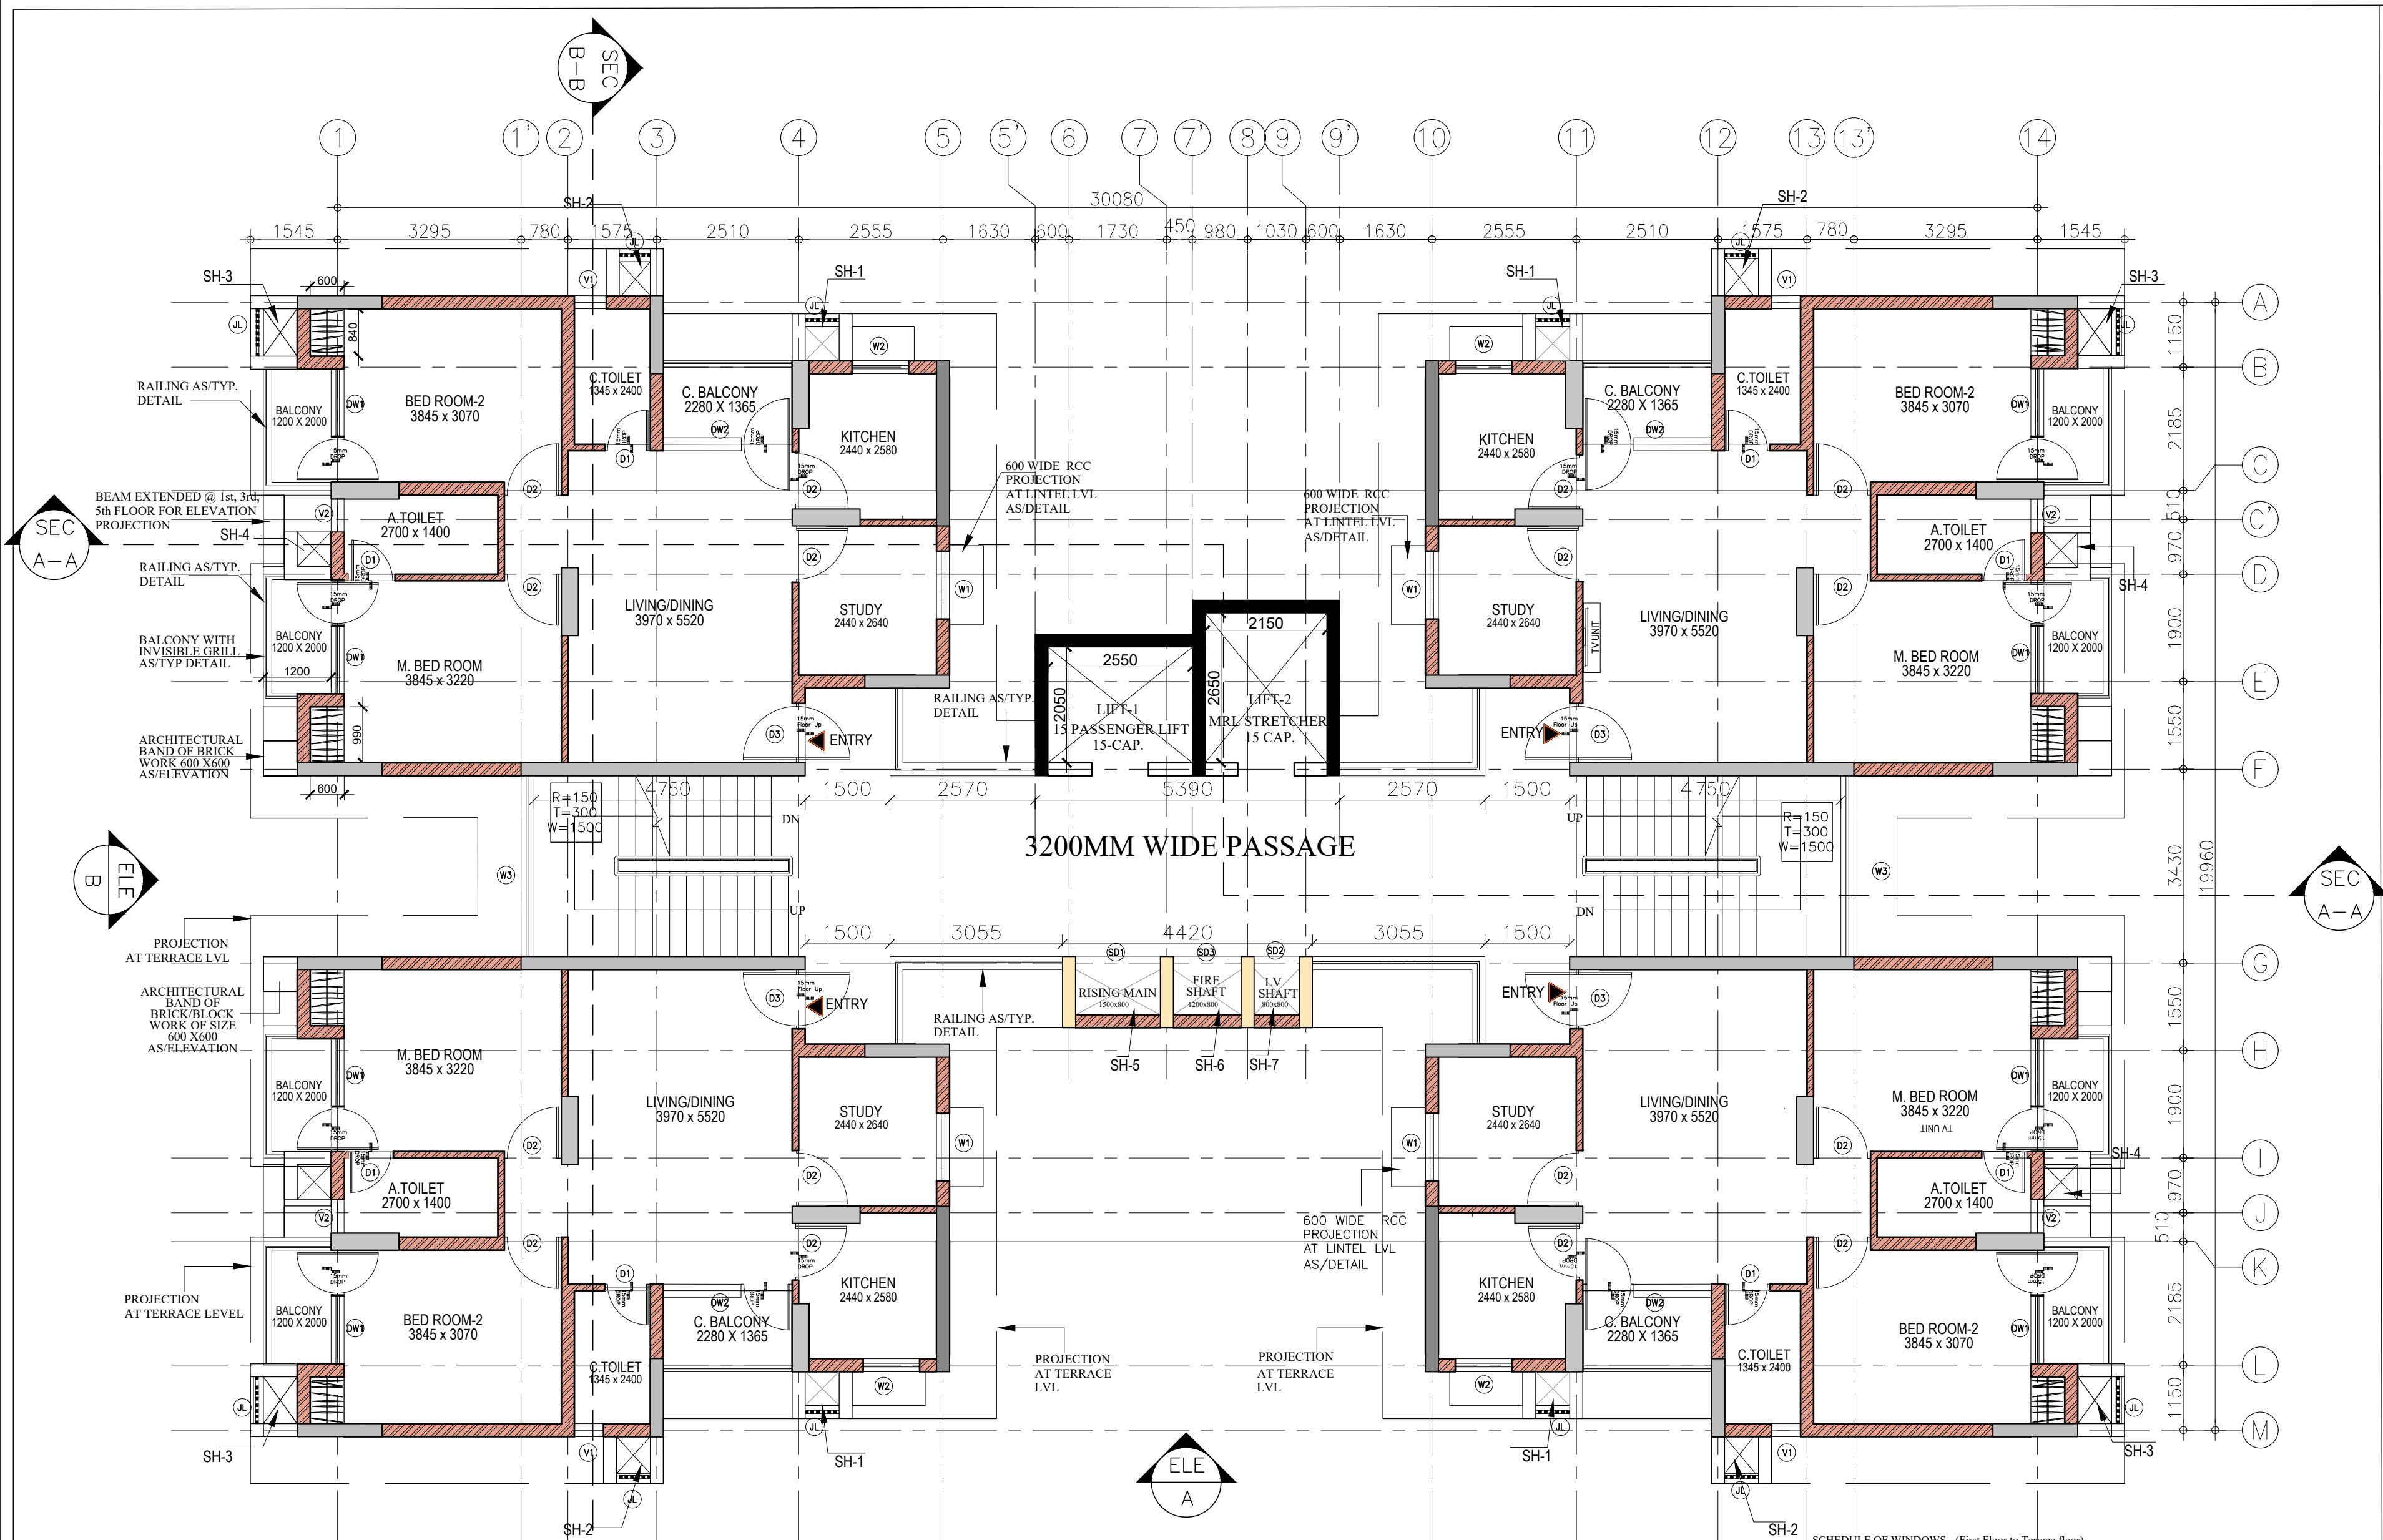

SCHEDULE OF DOORS - (Ground floor to Terrace floor)						
SL. NO	TYPE	NOS.	WIDTH	HEIGHT (from FFL.)	SILL (from FFL.)	REMARKS
1.	D1	---	800	2100	00	TOILETS
2.	D2	---	1000	2100	00	BEDROOM/KITCHEN
3.	D3	---	1050	2100	00	MAIN ENTRY
4.	DW1	---	2000	2100	00	BALCONY
5.	DW2	---	2295	2100	00	C. BALCONY
6.	SD1	---	900	2100	100	ELECT. SHAFT
7.	SD2	---	600	2100	100	LV. SHAFT
8.	SD3	---	900	2100	100	FHC SHAFT
9.	SD4	---	1200	2100	100	MUMTY

SCHEDULE OF DOORS - (Ground floor to Terrace floor)						
SL. NO	TYPE	NOS.	WIDTH	HEIGHT (from FFL.)	SILL (from FFL.)	REMARKS
1.	D1	---	800	2100	00	TOILETS
2.	D2	---	1000	2100	00	BEDROOM/KITCHEN
3.	D3	---	1050	2100	00	MAIN ENTRY
4.	DW1	---	2000	2100	00	BALCONY
5.	DW2	---	2295	2100	00	C. BALCONY
6.	SD1	---	900	2100	100	ELECT. SHAFT
7.	SD2	---	600	2100	100	LV. SHAFT
8.	SD3	---	900	2100	100	FHC SHAFT
9.	SD4	---	1200	2100	100	MUMTY

SCHEDULE OF WINDOWS - (First Floor to Terrace floor)						
SL. NO	TYPE	NOS.	WIDTH	HEIGHT	SILL (from FFL.)	REMARKS
1.	W1	---	1200	1200	900	ALUMINUM FRAME- SLIDING WITH WIRE MESH AND MS GRILL
2.	W2	---	1000	1225	1225	ALUMINUM FRAME- SLIDING WITH WIRE MESH AND MS GRILL
3.	W3	---	2300	1100	1000	ALUMINUM FRAME- PARTLY SLIDING CUM FIXED PANELS
4.	W4	---	1200	1200	900	ALUMINUM FRAME- SLIDING SHUTTERS

SCHEDULE OF VENTILATORS - (First Floor to Terrace floor)						
SL. NO	TYPE	NOS.	WIDTH	HEIGHT	SILL (from FFL.)	REMARKS
1.	V1	---	515	875	1225	ALUMINUM FRAME- VENTILATORS FIXED FROSTED GLASS PANELS
1.	V2	---	615	875	1225	ALUMINUM FRAME- VENTILATORS FIXED FROSTED GLASS PANELS

SCHEDULE OF SHAFT OPENING - (Ground floor to Terrace floor)						
SL. NO	TYPE	NOS.	WIDTH	HEIGHT	SILL (from FFL.)	REMARKS
1.	JL	---	600	2550	+00	ALUMINUM FRAME- LOUVERED DOOR

KEY PLAN

NOTES

TYPICAL FLOOR AREA= 483.60 SQ.M.

TOTAL NO. OF UNITS IN A BLOCK=24

SHAFT SCHEDULE

TENDER DRAWING

CLIENT

CONSULTANT

PROJECT

BUILDING

DRAWING TITLE

DRG. NO.

NORTH

SCALE

DATE

1. ALL DIMENSIONS ARE IN MM; UNLESS NOTED OTHERWISE.

2. WRITTEN DIMENSIONS ARE TO BE FOLLOWED. DRAWINGS ARE NOT TO BE SCALED.

3. ANY DISCREPANCY IN THE DRAWING SHALL BE BROUGHT TO THE NOTICE OF THE ENGINEER.

4. THIS DRAWING SHALL BE READ IN CONJUNCTION WITH OTHER RELEVANT DRAWINGS.

5. MOVABLE EQUIPMENT AND FURNISHINGS SUCH AS AIR CONDITIONERS, REFRIGERATORS, GAS STOVES, AND GEYSERS ETC.—ARE SHOWN FOR ILLUSTRATIVE PURPOSES ONLY AND ARE NOT TO BE PROVIDED. REFER TENDER DOCUMENT FOR DETAILS OF FURNITURE TO BE PROVIDED.

6. ONLY ELECTRICAL POINTS SHALL BE PROVIDED FOR AIR CONDITIONERS AND GEYSERS. PROVISION FOR DRAINAGE OF CONDENSATE WATER FROM AIR CONDITIONERS SHALL ALSO BE ENSURED.

TYPICAL FLOOR AREA= 483.60 SQ.M.

TOTAL NO. OF UNITS IN A BLOCK=24

SL. NO	TYPE	WIDTH	LENGTH	REMARKS
1.	SH-01	600	600	KITCHEN PLUMBING SHAFT
2.	SH-02	600	600	TOILET PLUMBING SHAFT
3.	SH-03	600	840	RAIN WATER PIPE SHAFT
4.	SH-04	600	600	TOILET PLUMBING SHAFT
5.	SH-05	1500	800	RISING MAIN SHAFT
6.	SH-06	1200	800	FIRE H. SHAFT
7.	SH-07	800	800	LV. SHAFT

TENDER DRAWING

CLIENT **OIL INDIA LIMITED**
(A Govt. of India Enterprise)

CONSULTANT **TRITES**
THE INFRASTRUCTURE PEOPLE
(A Govt. of India Enterprise)

PROJECT **BQ WORKMEN HOUSING**

BUILDING **HOUSING BLOCK (G+6)**

DRAWING TITLE **TYPICAL FLOOR PLAN**


DRG. NO. **BITES/BLD/AR/TD/006**

NORTH

SCALE **NTS**

DATE **JULY 2025**

KEY PLAN

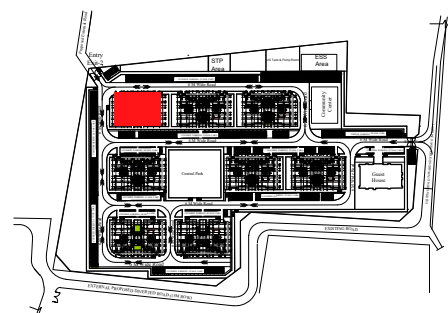

NOTES

- ALL DIMENSIONS ARE IN MM, UNLESS NOTED OTHERWISE.
- WRITTEN DIMENSIONS ARE TO BE FOLLOWED. DRAWINGS ARE NOT TO BE SCALED.
- ANY DISCREPANCY IN THE DRAWING SHALL BE BROUGHT TO THE NOTICE OF THE ENGINEER.
- THIS DRAWING SHALL BE READ IN CONJUNCTION WITH OTHER RELEVANT DRAWINGS.

TYPICAL FLOOR AREA= 483.60 SQ.M.

TOTAL NO. OF UNITS IN A BLOCK=24

SHAFT SCHEDULE

SL. NO	TYPE	WIDTH	LENGTH	REMARKS
1.	SH-01	600	600	KITCHEN PLUMBING SHAFT
2.	SH-02	600	600	TOILET PLUMBING SHAFT
3.	SH-03	600	840	RAIN WATER PIPE SHAFT
4.	SH-04	600	600	TOILET PLUMBING SHAFT
5.	SH-05	1500	800	RISEING MAIN SHAFT
6.	SH-06	1200	800	FIRE H.SHAFT
7.	SH-07	800	800	LV SHAFT

TENDER DRAWING

CLIENT



CONSULTANT



PROJECT

BQ WORKMEN HOUSING

BUILDING

HOUSING BLOCK (G+6)

DRAWING TITLE

TYPICAL TERRACE PLAN

DRG. NO.

RITES/BLD/AR/TD/008

NORTH



SCALE

NTS

DATE

JULY 2025

SCHEDULE OF DOORS - (Ground floor to Terrace floor)

SL. NO	TYPE	NOS.	WIDTH	HEIGHT (from FFL.)	SILL (from FFL.)	LINTEL (from FFL.)	LOCATION	REMARKS
SCHEDULE OF DOORS								
1.	D1	---	800	2100	00	2100	TOILETS	SINGLE LEAF WPC FRAME, WPC FLUSH DOOR AS/DRAWING
2.	D2	---	1000	2100	00	2100	BEDROOM/KITCHEN STUDY	SINGLE LEAF TEAK WOOD FRAME, FLUSH DOOR AS/DRAWING
3.	D3	---	1050	2100	00	2100	MAIN ENTRY	SINGLE LEAF TEAK WOOD FRAME, FLUSH DOOR & WIRE MESH DOOR SHUTTER AS/DRAWING
4.	DW1	---	2000	2100	00	2100	BALCONY	SINGLE LEAF TEAK WOOD FRAME, FLUSH DOOR, WIRE MESH DOOR SHUTTER & CASEMENT WINDOW WITH WIRE MESH SHUTTER
5.	DW2	---	2295	2100	00	2100	C. BALCONY	SINGLE LEAF TEAK WOOD FRAME, FLUSH DOOR, WIRE MESH DOOR SHUTTER & CASEMENT WINDOW WITH WIRE MESH SHUTTER
6.	SD1	---	900	2100	100	2100	ELECT. SHAFT	DOUBLE LEAF MS DOOR (Electrical Shaft Door as per NBC & latest CPWD guideline)
7.	SD2	---	600	2100	100	2100	LV. SHAFT	SINGLE LEAF MS DOOR
8.	SD3	---	900	2100	100	2100	FHC SHAFT	M.S. SINGLE LEAF DOOR WITH GLASS (FHC Shaft Door as per NBC & latest CPWD Guideline)
9.	SD4	---	1200	2100	100	2100	MUMTY	M.S. DOUBLE LEAF DOOR

SCHEDULE OF WINDOWS - (First Floor to Terrace floor)



SL. NO	TYPE	NOS.	WIDTH	HEIGHT	SILL (from FFL.)	LINTEL (from FFL.)	REMARKS
1.	W1	---	1200	1200	900	2100	ALUMINIUM FRAME- SLIDING WITH WIRE MESH AND MS GRILL AS/DRAWING
2.	W2	---	1000	1225	1225	2450	ALUMINIUM FRAME- SLIDING WITH WIRE MESH AND MS GRILL AS/DRAWING
3.	W3	---	2300	1100	1000 (from Terrace Slab level, FFL)	2100 (from Terrace Slab level, FFL)	ALUMINIUM FRAME- PARTLY SLIDING CUM FIXED PANELS WINDOW AS/DRAWING
4.	W4	---	1200	1200	900	2100	ALUMINIUM FRAME- SLIDING SHUTTERS AS/DRAWING

SCHEDULE OF VENTILATORS - (First Floor to Terrace floor)

SL. NO	TYPE	NOS.	WIDTH	HEIGHT	SILL (from FFL.)	LINTEL (from FFL.)	REMARKS
1.	V1	---	515	875	1225	2100	ALUMINIUM FRAME- VENTILATORS FIXED PANELS WITH EXHUST FAN AS/DRAWING
1.	V2	---	615	875	1225	2100	ALUMINIUM FRAME- VENTILATORS FIXED PANELS WITH EXHUST FAN AS/DRAWING

SCHEDULE OF SHAFT OPENING - (Ground floor to Terrace floor)

SL. NO	TYPE	NOS.	WIDTH	HEIGHT	SILL (from FFL.)	LINTEL (from FFL.)	REMARKS
1.	JL	---	600	2550 (standard)	+00	BEAM BOTTOM	ALUMINIUM FRAME- LOUVERED DOOR AS/DRAWING

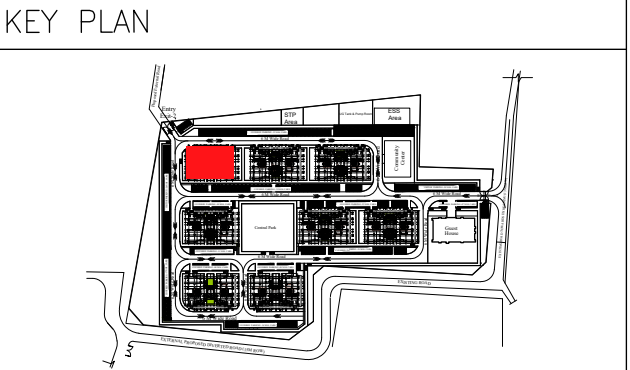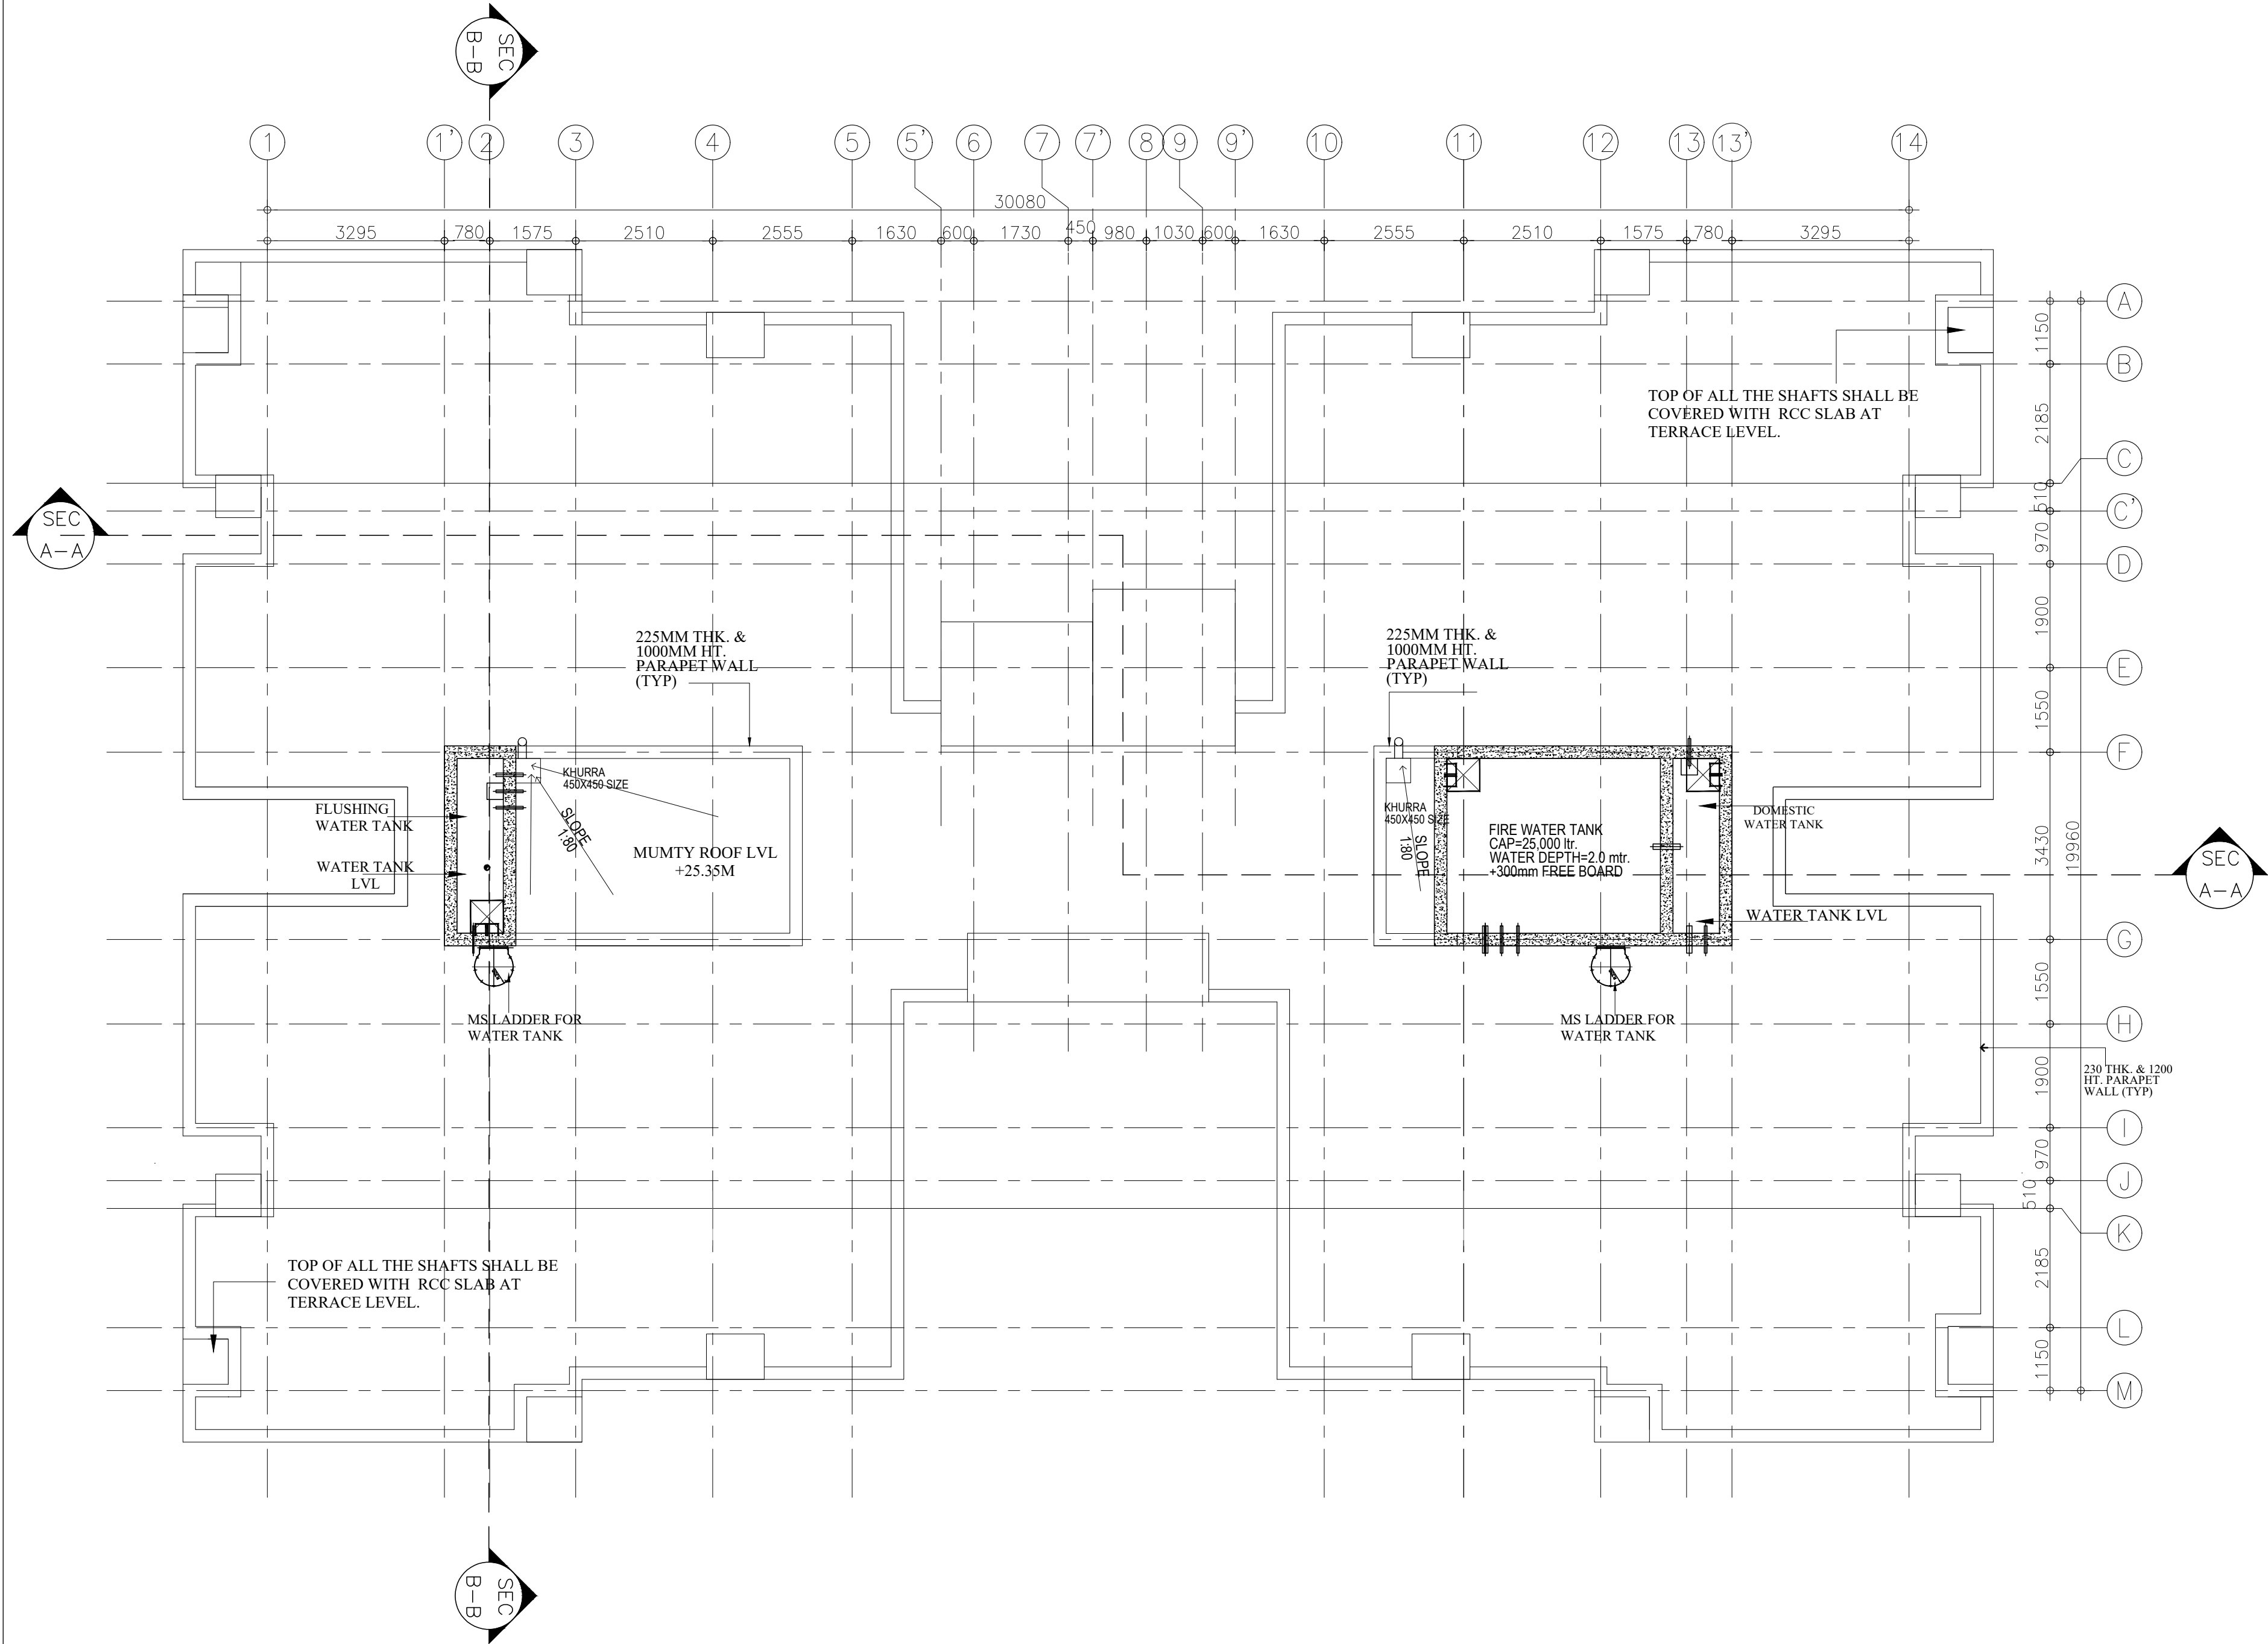



- NOTES
1. ALL DIMENSIONS ARE IN MM, UNLESS NOTED OTHERWISE.
 2. WRITTEN DIMENSIONS ARE TO BE FOLLOWED. DRAWINGS ARE NOT TO BE SCALED.
 3. ANY DISCREPANCY IN THE DRAWING SHALL BE BROUGHT TO THE NOTICE OF THE ENGINEER.
 4. THIS DRAWING SHALL BE READ IN CONJUNCTION WITH OTHER RELEVANT DRAWINGS.

TYPICAL FLOOR AREA= 483.60 SQ.M.





TOTAL NO. OF UNITS IN A BLOCK=24

TENDER DRAWING

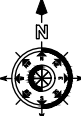CLIENT	 OIL INDIA LIMITED (A Govt. of India Enterprise)	
CONSULTANT	 IRITES THE INFRASTRUCTURE PEOPLE (A Govt. of India Enterprise)	
PROJECT	BQ WORKMEN HOUSING	
BUILDING	HOUSING BLOCK (G+6)	
DRAWING TITLE	TYPICAL MUMTY LVL PLAN	
DRG. NO.	BITES/BLD/AR/TD/009	
NORTH	SCALE	DATE
	NTS	JULY 2025

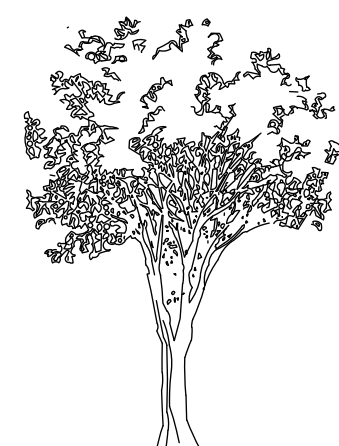

TYPICAL ELEVATION (A)

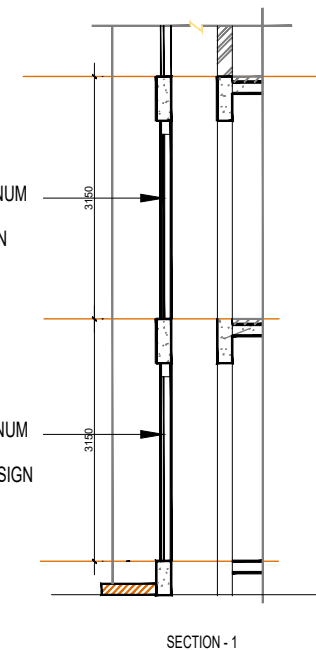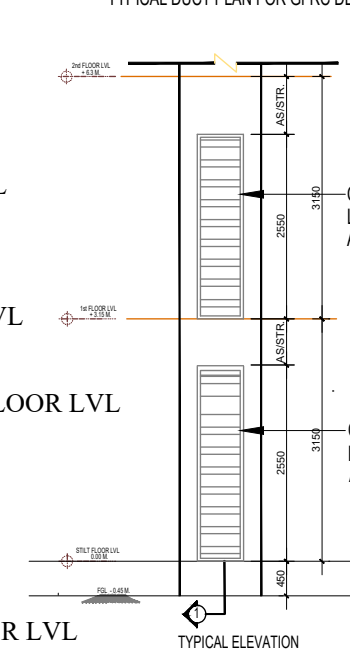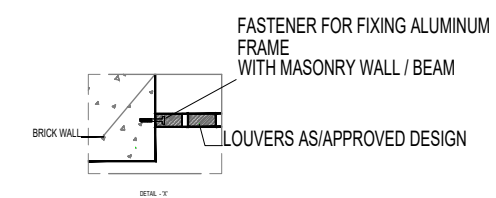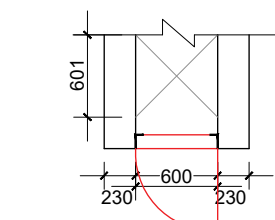

TYPICAL LOUVERS DETAIL AT SHAFT

TYPICAL FLOOR AREA= 483.70 SQ.M.				
TOTAL NO. OF UNITS IN A BLOCK=24				
SHAFT SCHEDULE				
SL. NO	TYPE	WIDTH	LENGTH	REMARKS
1.	SH-01	600	600	KITCHEN PLUMBING SHAFT
2.	SH-02	600	600	TOILET PLUMBING SHAFT
3.	SH- 03	600	840	RAIN WATER PIPE SHAFT
4.	SH- 04	600	600	TOILET PLUMBING SHAFT
5.	SH-05	1500	800	RIISING MAIN SHAFT
6.	SH-06	1200	800	FIRE H.SHAFT
7.	SH- 07	800	800	LV SHAFT

CLIENT		OIL INDIA LIMITED <i>(A Govt. of India Enterprise)</i>
--------	---	--

CONSULTANT


THE INFRASTRUCTURE PEOPLE
(A Govt. of India Enterprise)

PROJECT

BQ WORKMEN HOUSING

BUILDING


HOUSING BLOCK (G+6)

DRAWING TITLE	TYPICAL ELEVATION(A)
---------------	----------------------

DRG. NO.
RITES/BLD/AR/TD/010

NORTH 	SCALE NTS	DATE JULY 2025
--	-------------------------	------------------------------

[illegible]

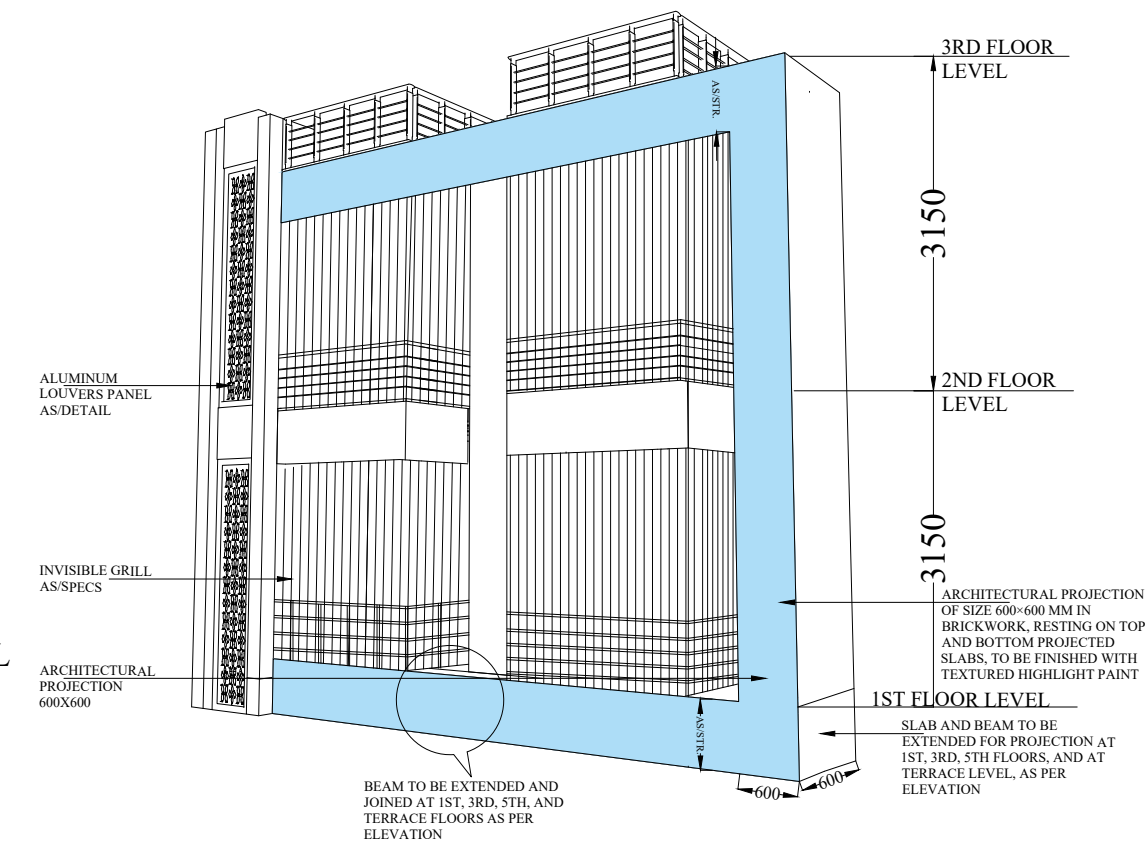


PROJECTION DETAIL









TYPICAL FLOOR AREA= 483.70 SQ.M.				
TOTAL NO. OF UNITS IN A BLOCK=24				
SHAFT SCHEDULE				
SL. NO	TYPE	WIDTH	LENGTH	REMARKS
1.	SH-01	600	600	KITCHEN PLUMBING SHAFT
2.	SH-02	600	600	TOILET PLUMBING SHAFT
3.	SH- 03	600	840	RAIN WATER PIPE SHAFT
4.	SH- 04	600	600	TOILET PLUMBING SHAFT
5.	SH-05	1500	800	RIISING MAIN SHAFT
6.	SH-06	1200	800	FIRE H.SHAFT
7.	SH- 07	800	800	LV SHAFT
TENDER DRAWING				
CLIENT		 OIL INDIA LIMITED (A Govt. of India Enterprise)		
CONSULTANT		 RITES THE INFRASTRUCTURE PEOPLE (A Govt. of India Enterprise)		
PROJECT		BQ WORKMEN HOUSING		
BUILDING		HOUSING BLOCK (G+6)		
DRAWING TITLE		TYPICAL ELEVATION (B)		
DRG. NO.		RITES/BLD/AR/TD/011		
NORTH		SCALE	DATE	
		NTS	JULY 2025	



SECTION A-A

- NOTES
1. ALL DIMENSIONS ARE IN MM; UNLESS NOTED OTHERWISE.
 2. WRITTEN DIMENSIONS ARE TO BE FOLLOWED. DRAWINGS ARE NOT TO BE SCALED.
 3. ANY DISCREPANCY IN THE DRAWING SHALL BE BROUGHT TO THE NOTICE OF THE ENGINEER.
 4. THIS DRAWING SHALL BE READ IN CONJUNCTION WITH OTHER RELEVANT DRAWINGS.
 5. THE FINISHED FLOOR LEVEL (FFL) SHALL BE MAINTAINED MINIMUM 50MM OR AS PER APPLICABLE CODES/SPECIFICATIONS/ SITE REQUIREMENTS ABOVE THE STRUCTURAL SLAB LEVEL OF ALL BUILDINGS. REFER TENDER DOCUMENT FOR DETAILS

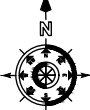TENDER DRAWING		
CLIENT	 OIL INDIA LIMITED (A Govt. of India Enterprise)	
CONSULTANT	 RITES THE INFRASTRUCTURE PEOPLE (A Govt. of India Enterprise)	
PROJECT	BQ WORKMEN HOUSING	
BUILDING	HOUSING BLOCK (G+6)	
DRAWING TITLE	SECTION A-A'	
DRG. NO.	MITES/BLD/AR/TD/012	
NORTH	SCALE	DATE
	NTS	JULY 2025

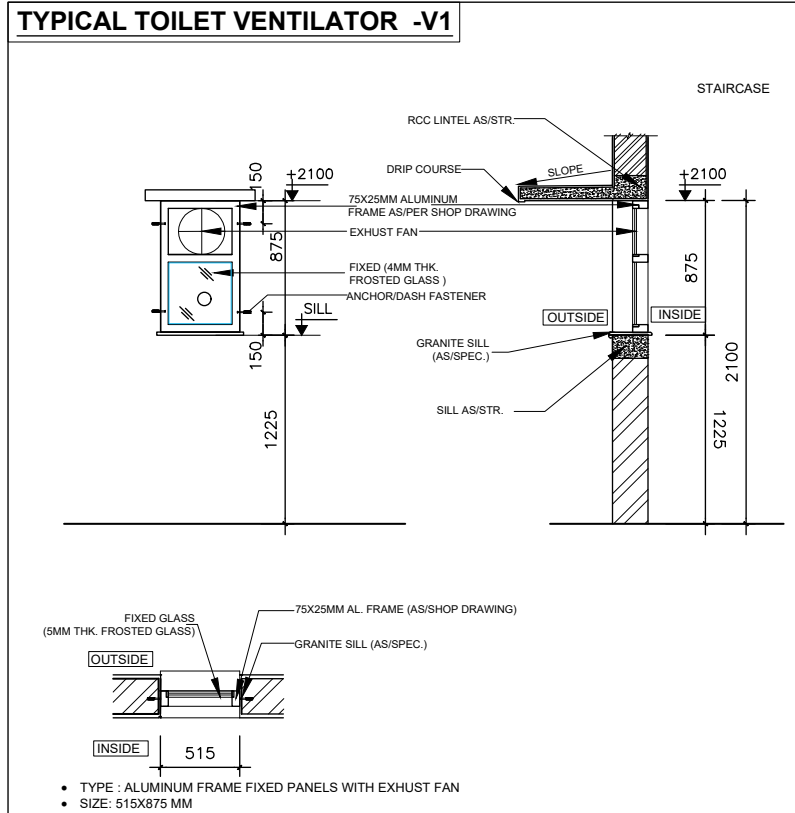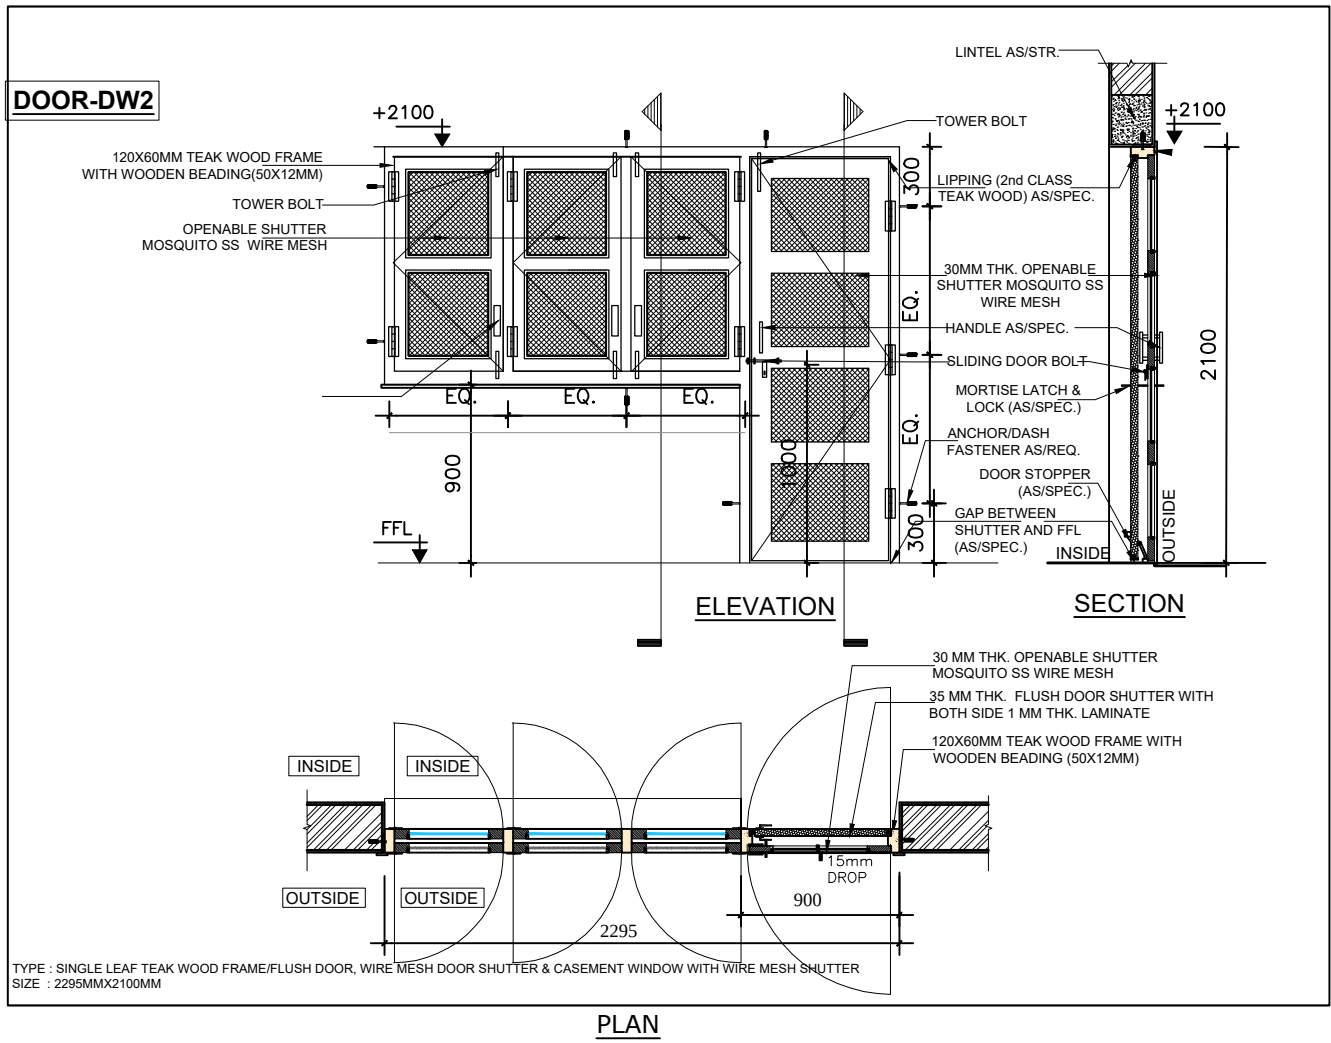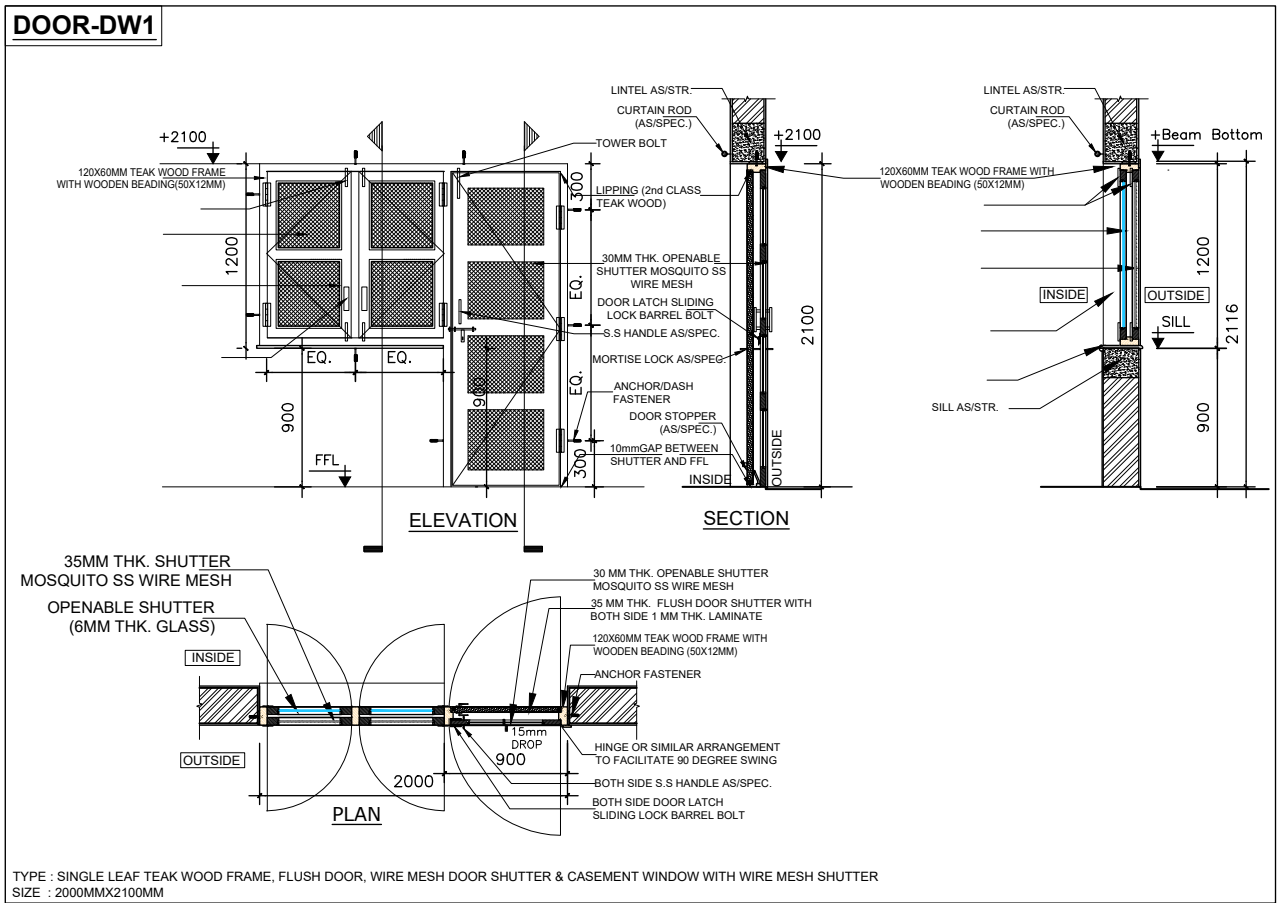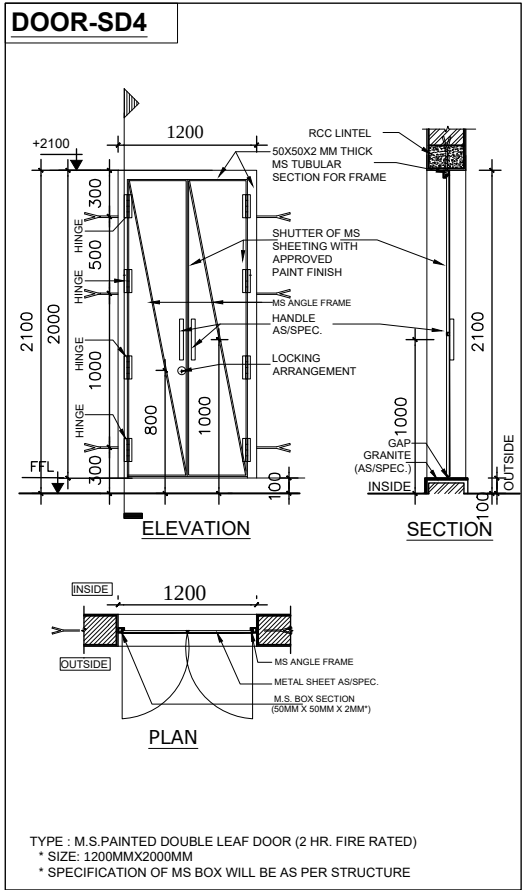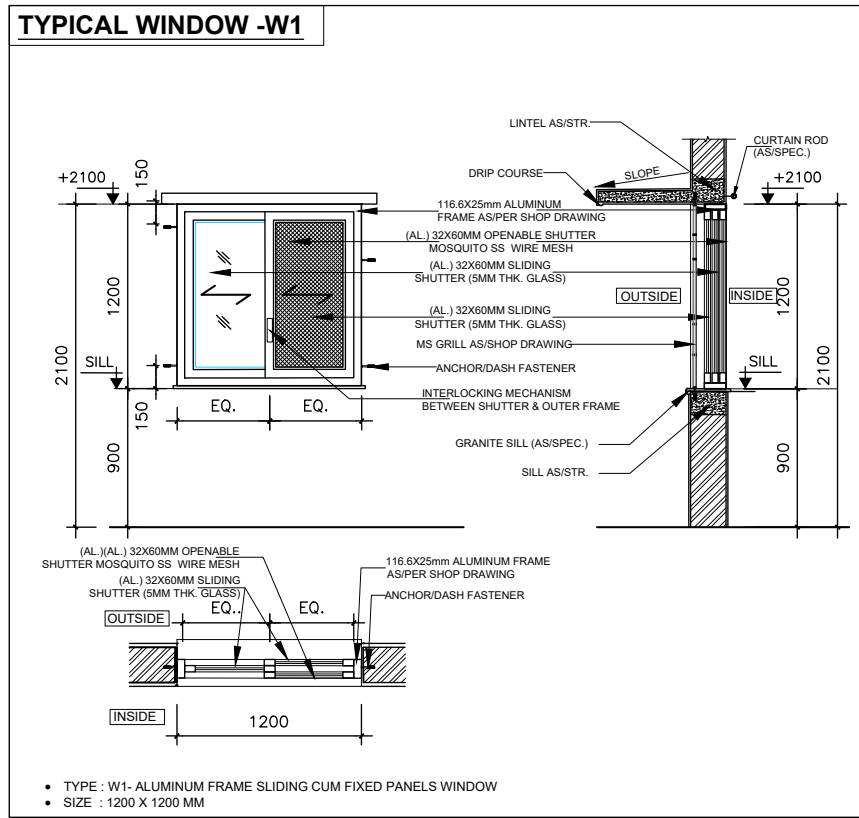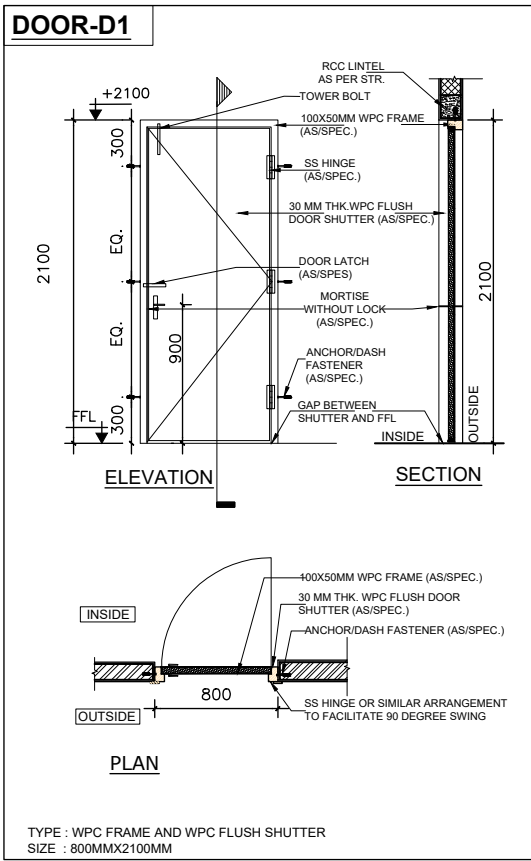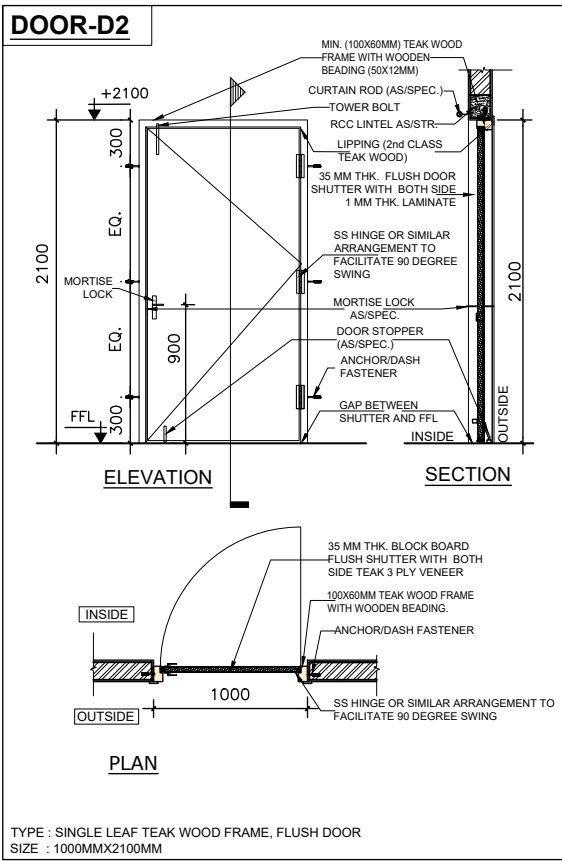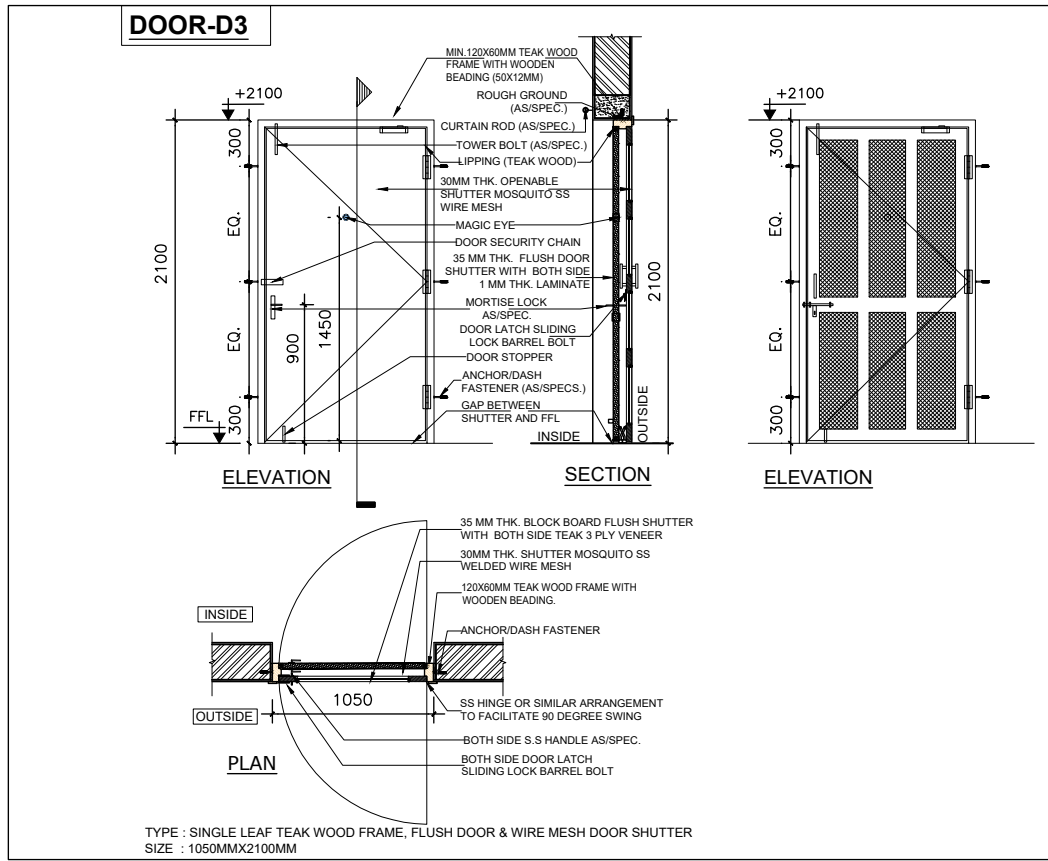

NOTES

- ALL DIMENSIONS ARE IN MM; UNLESS NOTED OTHERWISE.
- WRITTEN DIMENSIONS ARE TO BE FOLLOWED. DRAWINGS ARE NOT TO BE SCALED.
- ANY DISCREPANCY IN THE DRAWING SHALL BE BROUGHT TO THE NOTICE OF THE ENGINEER.
- THIS DRAWING SHALL BE READ IN CONJUNCTION WITH OTHER RELEVANT DRAWINGS.
- THE DRAWING IS INDICATIVE ONLY.
- SHOP DRAWING TO BE PREPARED FOR APPROVAL.
- REFER SPECIFICATION AND SCHEDULE OF FINISH.

TENDER DRAWING

CLIENT
OIL INDIA LIMITED
(A Govt. of India Enterprise)

CONSULTANT
IRITES
THE INFRASTRUCTURE PEOPLE
(A Govt. of India Enterprise)

PROJECT
BQ WORKMEN HOUSING

BUILDING
HOUSING BLOCK (G+6)

DRAWING TITLE
DOOR-WINDOW DETAIL

DRG. NO.
MITES/BLD/AR/TD/014

NORTH

SCALE
NTS
DATE
JULY 2025

SCHEDULE OF DOORS - (Ground floor to Terrace floor)							
SL. NO	TYPE	NOS.	WIDTH	HEIGHT (from FFL.)	SILL (from FFL.)	LINTEL (from FFL.)	LOCATION
1.	D1	---	800	2100	00	2100	TOILETS
2.	D2	---	1000	2100	00	2100	BEDROOM/KITCHEN /STUDY
3.	D3	---	1050	2100	00	2100	MAIN ENTRY
4.	DW1	---	2000	2100	00	2100	BALCONY
5.	DW2	---	2295	2100	00	2100	C. BALCONY
6.	SD1	---	900	2100	100	2100	ELECT.SHAFT
7.	SD2	---	600	2100	100	2100	LV.SHAFT
8.	SD3	---	900	2100	100	2100	FHC SHAFT
8.	SD4	---	1200	2100	100	2100	MUMTY

SCHEDULE OF WINDOWS - (First Floor to Terrace floor)

SL. NO	TYPE	NOS.	WIDTH	HEIGHT	SILL (from FFL)	LINTEL (from FFL)	REMARKS
1.	W1	---	1200	1200	900	2100	ALUMINUM FRAME- SLIDING WITH WIRE MESH AND MS GRILL AS/DRAWING/SPECS
2.	W2	---	1000	1225	1225	2450	ALUMINUM FRAME- SLIDING WITH WIRE MESH AND MS GRILL AS/DRAWING/SPECS
3.	W3	---	2300	1100	1000 (from staircase landing FFL)	2100 (from staircase landing FFL)	ALUMINUM FRAME- PARTLY SLIDING CUM FIXED PANELS WINDOW AS/DRAWING/SPECS
4.	W4	---	1200	1200	900	2100	ALUMINUM FRAME- SLIDING SHUTTERS AS/DRAWING/SPECS


SCHEDULE OF VENTILATORS - (First Floor to Terrace floor)

SL. NO	TYPE	NOS.	WIDTH	HEIGHT	SILL (from FFL)	LINTEL (from FFL)	REMARKS
1.	V1	---	515	875	1225	2100	ALUMINUM FRAME- VENTILATORS FIXED FROSTED GLASS PANELS WITH EXHAUST FAN AS/DRAWING/SPECS
1.	V2	---	615	875	1225	2100	ALUMINUM FRAME- VENTILATORS FIXED FROSTED GLASS PANELS WITH EXHAUST FAN AS/DRAWING/SPECS

SCHEDULE OF SHAFT OPENING - (Ground floor to Terrace floor)


SL. NO	TYPE	NOS.	WIDTH	HEIGHT	SILL (from FFL)	LINTEL (from FFL)	REMARKS
1.	JL	----	600	2550 (estimated)	+00	BEAM BOTTOM	ALUMINUM FRAME- LOUVERED DOOR AS/DRAWING

JL-TYPICAL ALUMINUM FRAME- OPENABLE LOUVERED PANEL

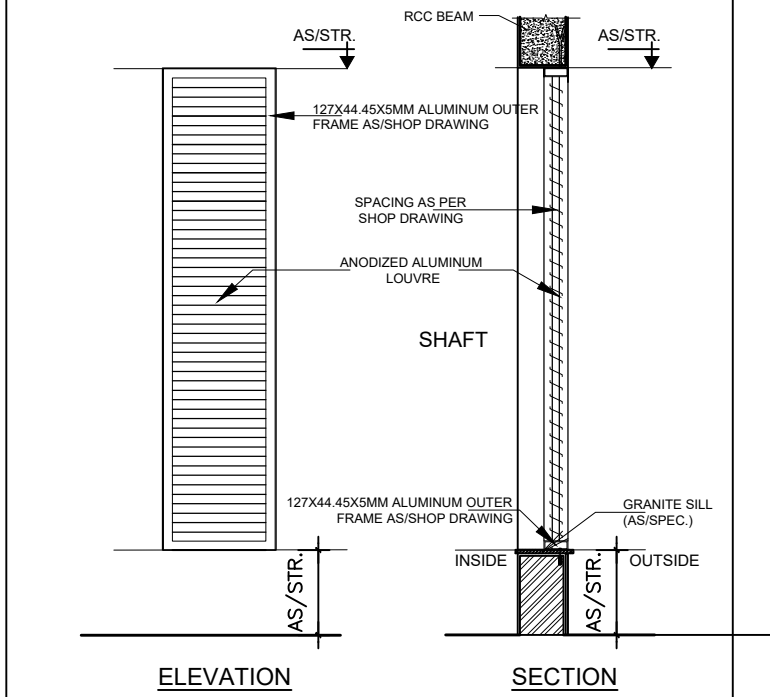


- TYPE : ALUMINUM FRAME- OPENABLE LOUVERED PANEL
- SIZE : 600 X 2550 MM

DOOR-SD2

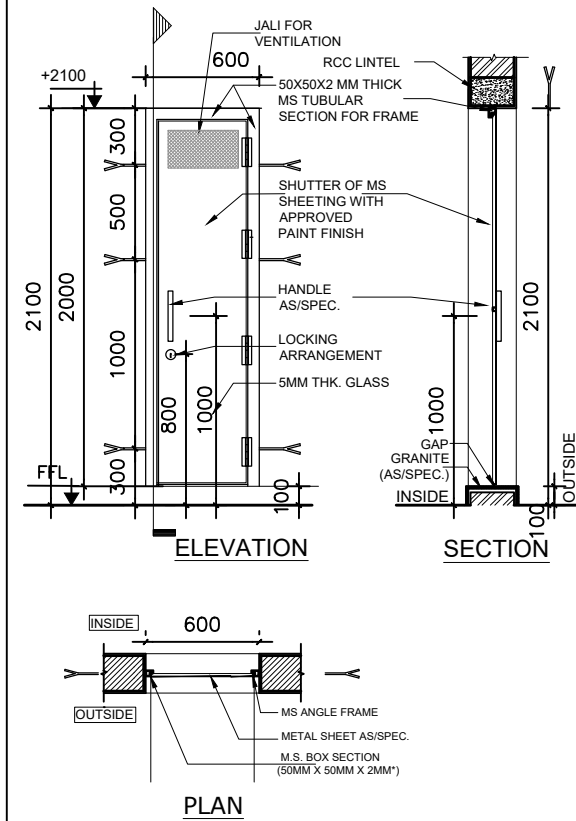


- TYPE : M.S. PAINTED SINGLE LEAF DOOR WITH GLASS (2 HR. FIRE RATED)
- SIZE: 600MMX2000MM
- * SPECIFICATION OF MS BOX WILL BE AS PER STRUCTURE

WINDOW -W3

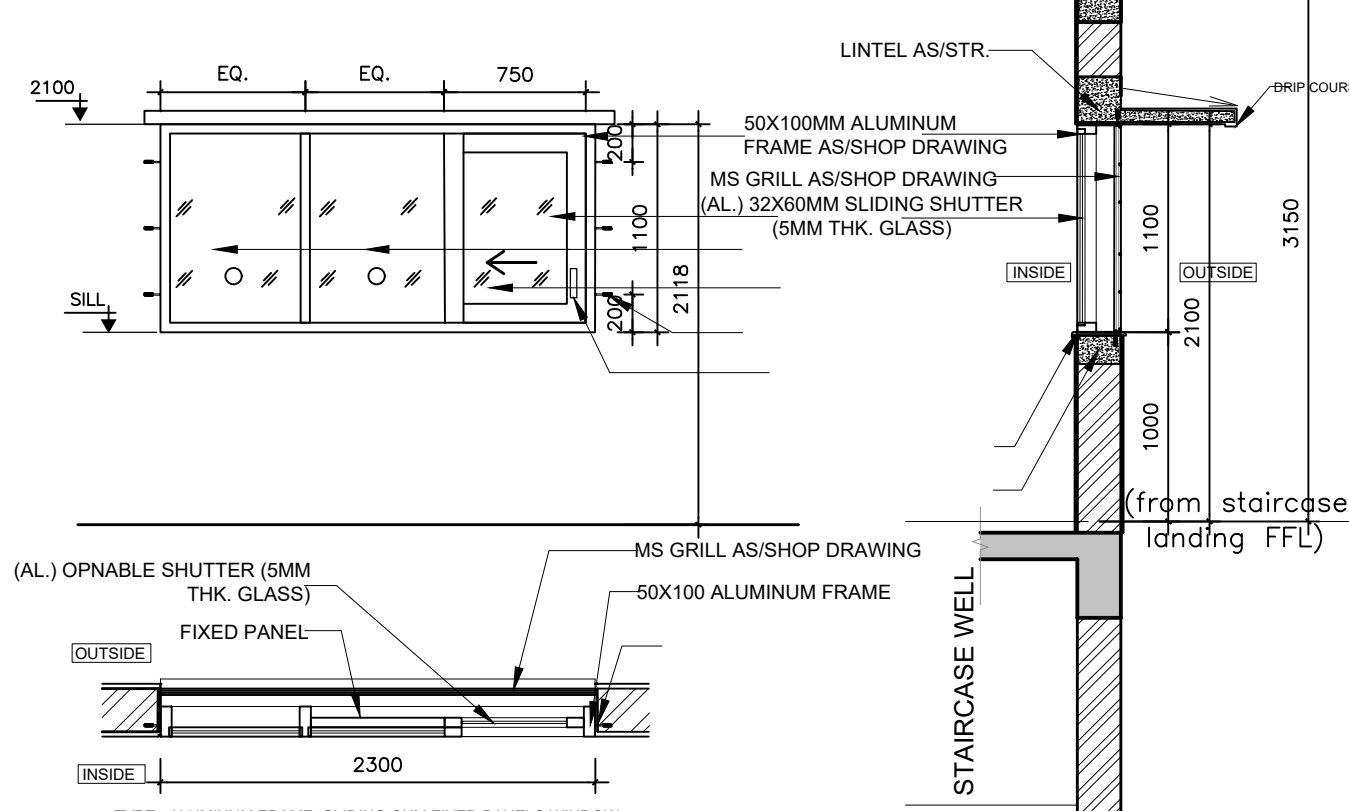


- TYPE : ALUMINUM FRAME- SLIDING CUM FIXED PANELS WINDOW
- SIZE : 2300 X 1100 MM

TYPICAL MS GRILL ALL AROUND WINDOW OPENING

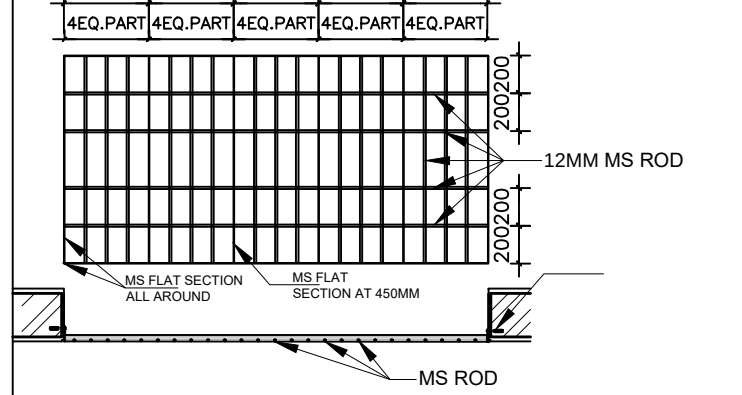


TYPICAL KITCHEN WINDOW -W2

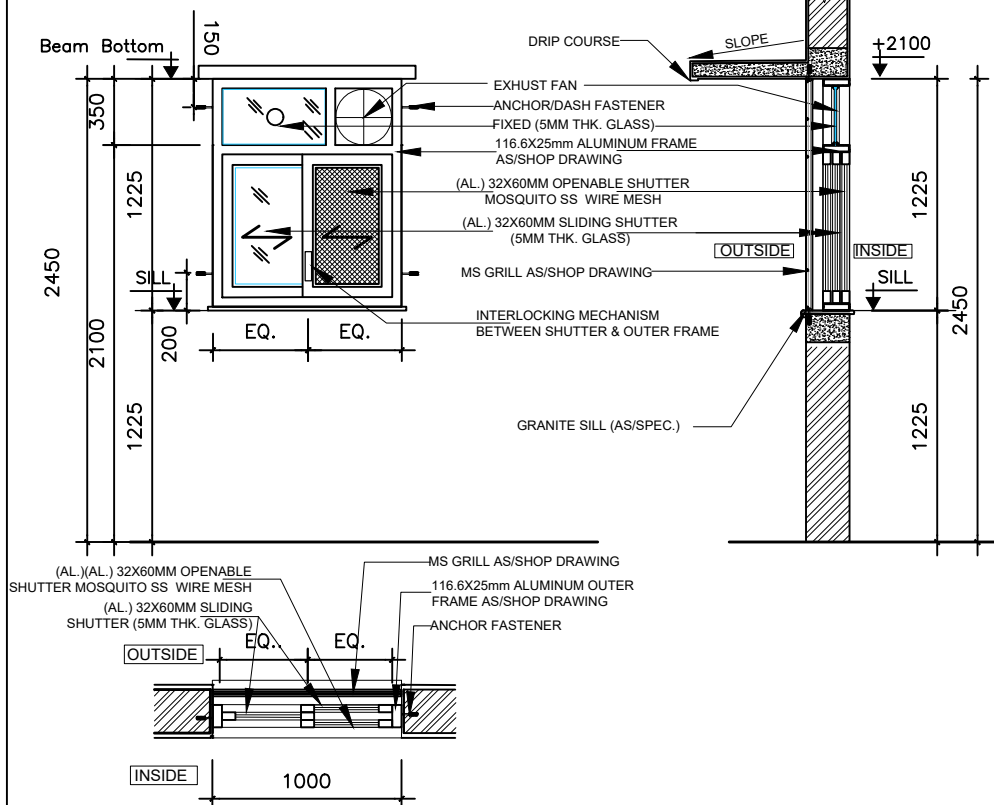


- TYPE : ALUMINUM FRAME- SLIDING WITH WIRE MESH AND MS GRILL
- SIZE : 1000 X 1500 MM

TYPICAL TOILET VENTILATOR -V2

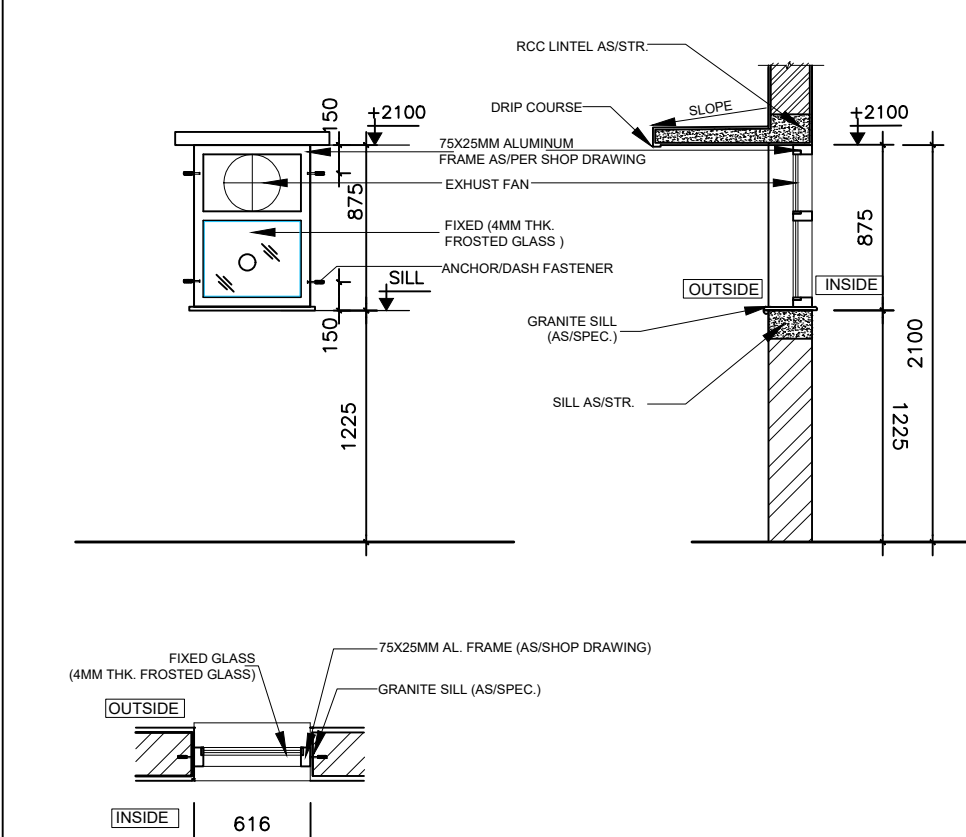

- TYPE : ALUMINUM FRAME FIXED PANELS FROSTED GLASS WITH EXHUST FAN AS/DRAWING
- SIZE: 615X875 MM

TYPICAL WINDOW -W4

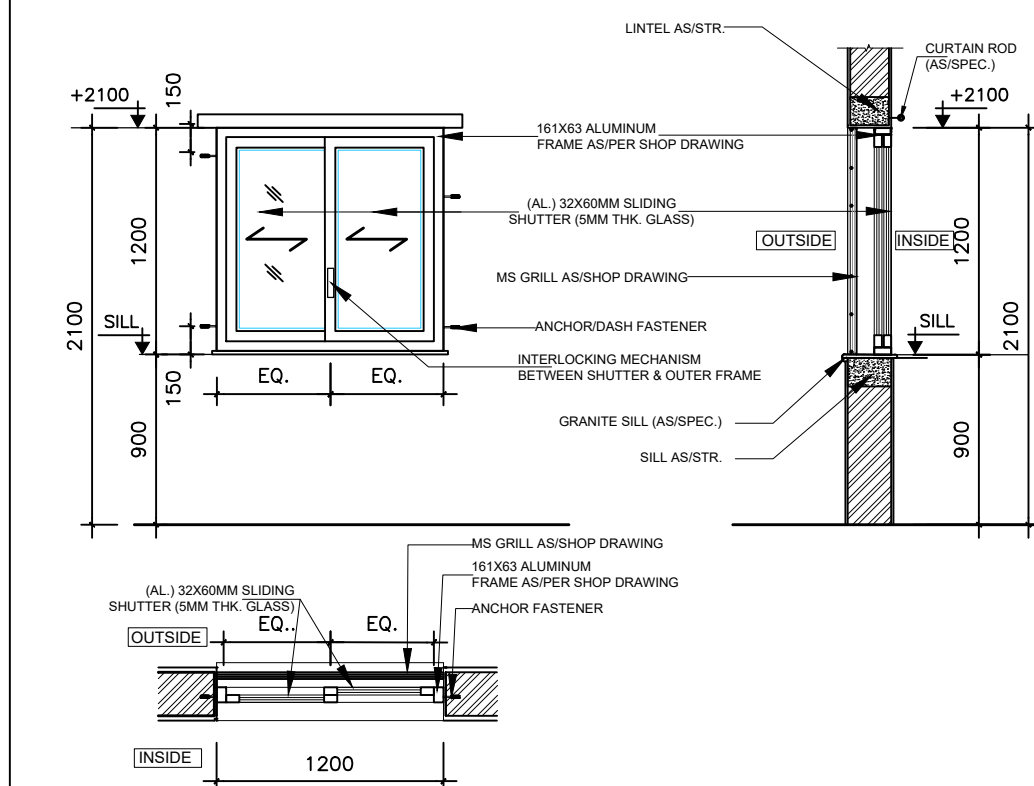

- TYPE : W1- ALUMINUM FRAME SLIDING CUM FIXED PANELS WINDOW
- SIZE : 1200 X 1200 MM

NOTES

1. ALL DIMENSIONS ARE IN MM; UNLESS NOTED OTHERWISE.
2. WRITTEN DIMENSIONS ARE TO BE FOLLOWED. DRAWINGS ARE NOT TO BE SCALED.
3. ANY DISCREPANCY IN THE DRAWING SHALL BE BROUGHT TO THE NOTICE OF THE ENGINEER.
4. THIS DRAWING SHALL BE READ IN CONJUNCTION WITH OTHER RELEVANT DRAWINGS.
5. THE DRAWING IS INDICATIVE ONLY.
6. SHOP DRAWING TO BE PREPARED FOR APPROVAL.
7. REFER SPECIFICATION AND SCHEDULE OF FINISH.

TENDER DRAWING

CLIENT



CONSULTANT



PROJECT

BQ WORKMEN HOUSING

BUILDING

HOUSING BLOCK (G+6)


DRAWING TITLE

DOOR-WINDOW DETAIL

DRG. NO.

MITES/BLD/AR/TD/015

NORTH

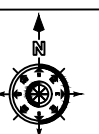

SCALE

NTS

DATE

JULY 2025

SCHEDULE OF DOORS - (Ground floor to Terrace floor)								
SL. NO	TYPE	NOS.	WIDTH	HEIGHT	SILL (from FFL.)	LINTEL (from FFL.)	LOCATION	REMARKS
SCHEDULE OF DOORS								
1.	D1	---	800	2100	00	2100	TOILETS	SINGLE LEAF WPC FRAME, WPC FLUSH DOOR AS/DRAWING/SPECS
2.	D2	---	1000	2100	00	2100	BEDROOM/KITCHEN/STUDY	SINGLE LEAF TEAK WOOD FRAME, FLUSH DOOR AS/DRAWING/SPECS
3.	D3	---	1050	2100	00	2100	MAIN ENTRY	SINGLE LEAF TEAK WOOD FRAME, FLUSH DOOR & WIRE MESH DOOR SHUTTER AS/DRAWING
4.	DW1	---	2000	2100	00	2100	BALCONY	SINGLE LEAF TEAK WOOD FRAME, FLUSH DOOR, WIRE MESH DOOR SHUTTER & CASEMENT WINDOW WITH WIRE MESH SHUTTER AS/DRAWING/SPECS
5.	DW2	---	2295	2100	00	2100	C. BALCONY	SINGLE LEAF TEAK WOOD FRAME, FLUSH DOOR, WIRE MESH DOOR SHUTTER & CASEMENT WINDOW WITH WIRE MESH SHUTTER AS/DRAWING/SPECS
6.	SD1	---	900	2100	100	2100	ELECT.SHAFT	DOUBLE LEAF MS DOOR (Electrical Shaft Door as per NBC & latest CPWD guideline)
7.	SD2	---	600	2100	100	2100	LV.SHAFT	SINGLE LEAF MS DOOR AS/DRAWING/SPECS
8.	SD3	---	900	2100	100	2100	FHC SHAFT	M.S.SINGLE LEAF DOOR WITH GLASS (FHC Shaft Door as per NBC & latest CPWD Guideline)
8.	SD4	---	900	2100	100	2100	MUMTY	M.S. DOUBLE LEAF DOOR AS/DRAWING/SPECS

SCHEDULE OF WINDOWS - (First Floor to Terrace floor)


SL. NO	TYPE	NOS.	WIDTH	HEIGHT	SILL (from FFL)	LINTEL (from FFL)	REMARKS
1.	W1	---	1200	1200	900	2100	ALUMINUM FRAME- SLIDING WITH WIRE MESH AND MS GRILL AS/DRAWING/SPECS
2.	W2	---	1000	1225	1225	2450	ALUMINUM FRAME- SLIDING WITH WIRE MESH AND MS GRILL AS/DRAWING/SPECS
3.	W3	---	2300	1100	1000 (from staircase landing, FFL)	2100 (from staircase landing, FFL)	ALUMINUM FRAME- PARTLY SLIDING CUM FIXED PANELS WINDOW AS/DRAWING/SPECS
4.	W4	---	1200	1200	900	2100	ALUMINUM FRAME- SLIDING SHUTTERS AS/DRAWING/SPECS

SCHEDULE OF VENTILATORS - (First Floor to Terrace floor)

SL. NO	TYPE	NOS.	WIDTH	HEIGHT	SILL (from FFL)	LINTEL (from FFL)	REMARKS
1.	V1	---	515	875	1225	2100	ALUMINUM FRAME- VENTILATORS FIXED FROSTED GLASS PANELS WITH EXHUST FAN AS/DRAWING
1.	V2	---	615	875	1225	2100	ALUMINUM FRAME- VENTILATORS FIXED FROSTED GLASS PANELS WITH EXHUST FAN AS/DRAWING

SCHEDULE OF SHAFT OPENING - (Ground floor to Terrace floor)

SL. NO	TYPE	NOS.	WIDTH	HEIGHT	SILL (from FFL)	LINTEL (from FFL)	REMARKS
1.	JL	----	600	2550 (minimum)	+00	BEAM BOTTOM	ALUMINUM FRAME- LOUVERED DOOR AS/DRAWING

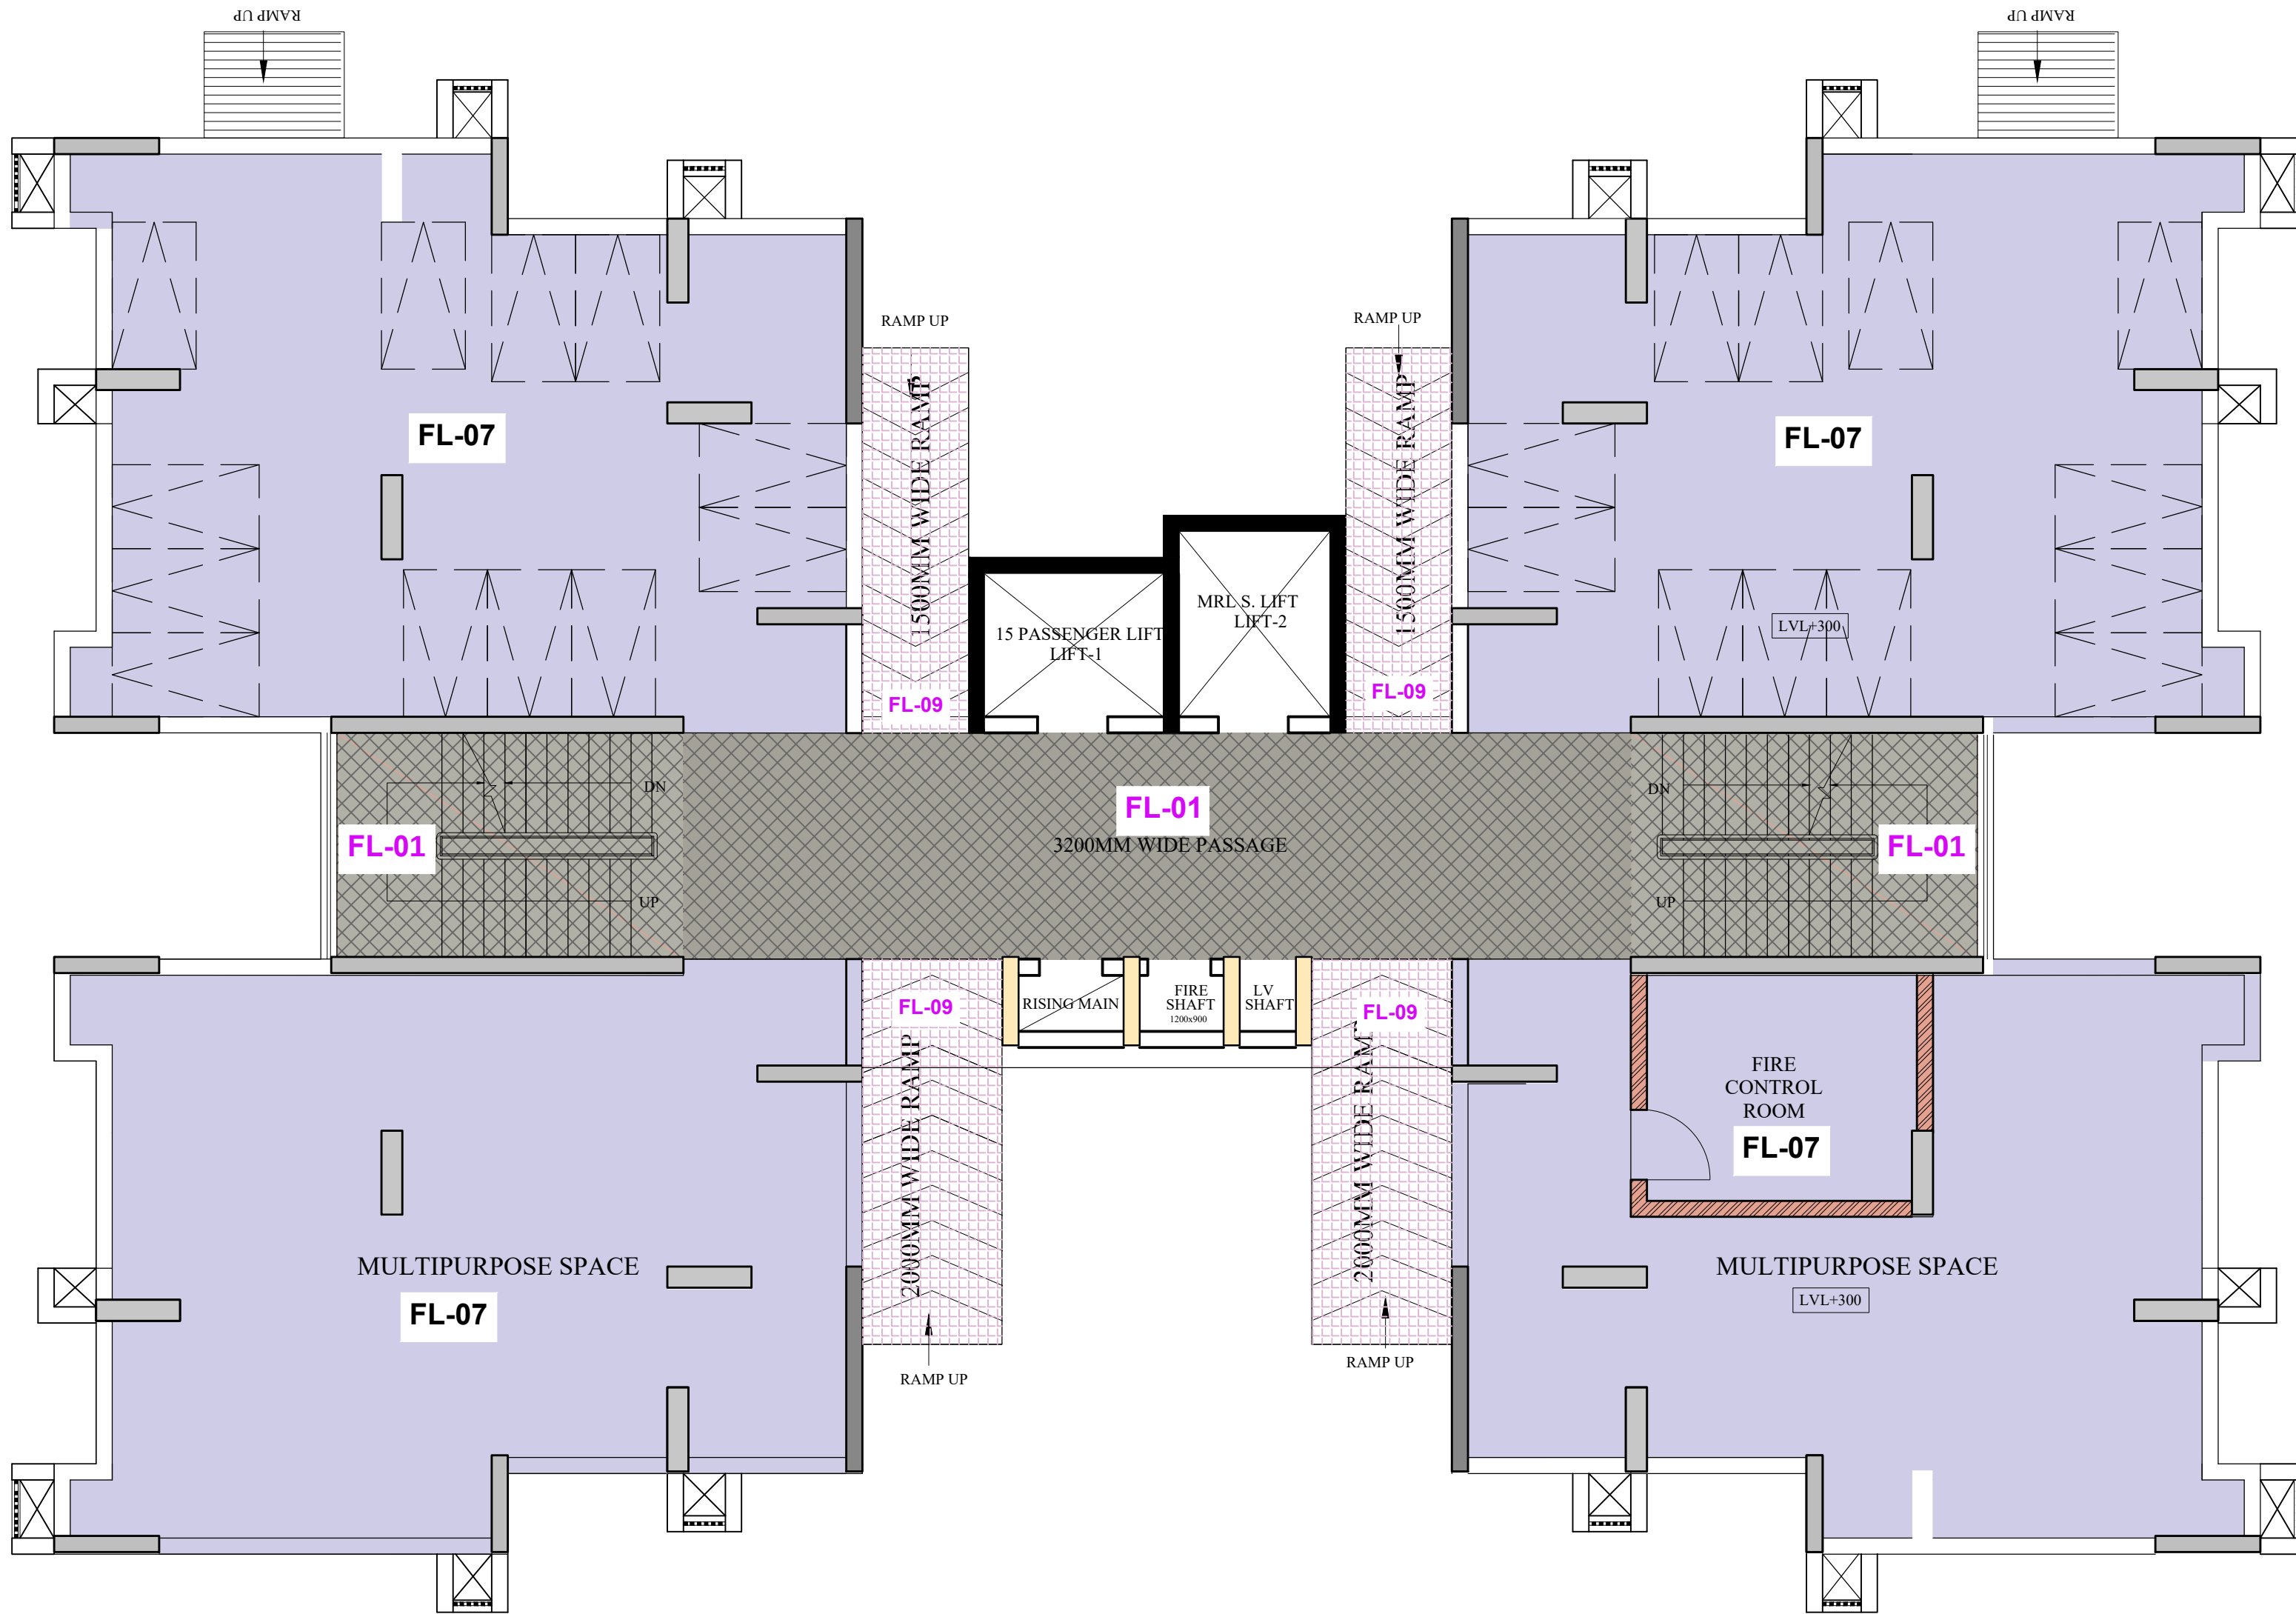

01		FL-07	25mm THK. KOTA STONE	• STILT PARKING • MULTIPURPOSE SPACE • FIRE CONTROL ROOM
02		FL-01	18MM THK POLISHED GRANITE FLOORING AS PER SPECS	• LOBBY
03		FL-01	18MM THK POLISHED GRANITE FLOORING WITH ANTI SKID GROOVE AS PER SPECS	• STAIRCASE
04		FL-09	60MM THK. CEMENT CONCRETE PAVER BLOCK WITH TACTILE TILE OF SIZE 300 X 300 AS/APPROVED SHAPE & COLOR	• RAMP

NOTES

1. ALL DIMENSIONS ARE IN MM; UNLESS NOTED OTHERWISE.
2. WRITTEN DIMENSIONS ARE TO BE FOLLOWED. DRAWINGS ARE NOT TO BE SCALED.
3. ANY DISCREPANCY IN THE DRAWING SHALL BE BROUGHT TO THE NOTICE OF THE ENGINEER.
4. THIS DRAWING SHALL BE READ IN CONJUNCTION WITH OTHER RELEVANT DRAWINGS.
5. THE FINISHED FLOOR LEVEL (FFL) SHALL BE MAINTAINED MINIMUM 50MM OR AS PER APPLICABLE CODES/SPECIFICATIONS/ SITE REQUIREMENTS ABOVE THE STRUCTURAL SLAB LEVEL OF ALL BUILDINGS. REFER TENDER DOCUMENT FOR DETAILS.

TENDER DRAWING

CLIENT		OIL INDIA LIMITED (A Govt. of India Enterprise)
CONSULTANT		RITES THE INFRASTRUCTURE PEOPLE (A Govt. of India Enterprise)
PROJECT	BQ WORKMEN HOUSING	
BUILDING	HOUSING BLOCK (G+6)	
DRAWING TITLE	TYPICAL FLOORING STILT FLOOR	
DRG. NO.	RITES/BLD/AR/TD/016	
NORTH	SCALE	DATE
	NTS	JULY 2025



LEGEND FOR FLOORING				
S.NO.	HATCH SYMBOL	ICON	MATERIAL	AREA OF APPLICATION
01		FL-01	18MM THK POLISHED GRANITE FLOORING PER SPECS	- LIFT AND ENTRANCE - LOBBY
02		FL-01	18MM THK POLISHED GRANITE FLOORING ANTI SKID GROOVE AS PER SPECS	STAIRCASE
03		FL-02	POLISHED VITRIFIED TILE (600 X 600)	- BEDROOMS, STUDY ROOM - LIVING/DINING
04		FL-03	MATT/ANTI SKID VITRIFIED TILE (600 X 600)	- KITCHEN - BALCONY
05		FL-04	RECTIFIED ANTI SKID CERAMIC TILES (300X300)	TOILETS
06	SKIRTING 100 MM HIGH, MATCHING THE FLOOR FINISH; DADO IN TOILETS (UP TO FALSE CEILING) /WASH BASIN AREA IN DINING (2.1M HIGH) ALL AS PER SPECIFICATIONS			

NOTES

- ALL DIMENSIONS ARE IN MM; UNLESS NOTED OTHERWISE.
- WRITTEN DIMENSIONS ARE TO BE FOLLOWED. DRAWINGS ARE NOT TO BE SCALED.
- ANY DISCREPANCY IN THE DRAWING SHALL BE BROUGHT TO THE NOTICE OF THE ENGINEER.
- THIS DRAWING SHALL BE READ IN CONJUNCTION WITH OTHER RELEVANT DRAWINGS.
- THE FINISHED FLOOR LEVEL (FFL) SHALL BE MAINTAINED MINIMUM 50MM OR AS PER APPLICABLE CODES/SPECIFICATIONS/ SITE REQUIREMENTS ABOVE THE STRUCTURAL SLAB LEVEL OF ALL BUILDINGS. REFER TENDER DOCUMENT FOR DETAILS.

TENDER DRAWING

CLIENT **OIL INDIA LIMITED**
(A Govt. of India Enterprise)

CONSULTANT **RITES**
THE INFRASTRUCTURE PEOPLE
(A Govt. of India Enterprise)


PROJECT **BQ WORKMEN HOUSING**



BUILDING **HOUSING BLOCK (G+6)**

DRAWING TITLE **TYPICAL FLOOR FLOORING LAYOUT**

DRG. NO. **BITES/BLD/AR/TD/017**

NORTH SCALE **NTS** DATE **JULY 2025**

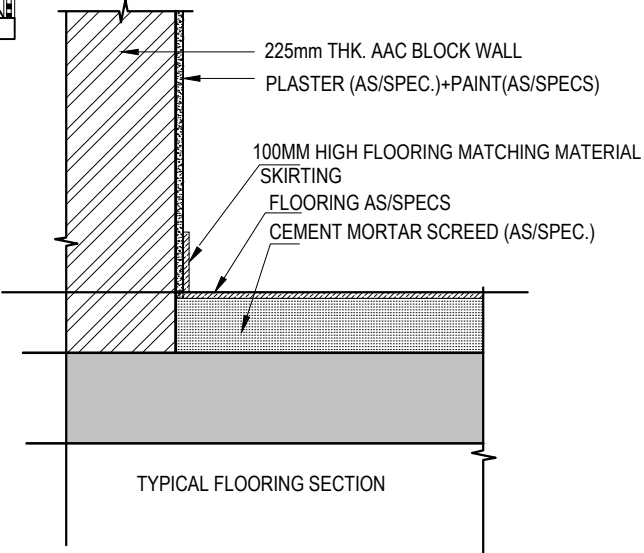

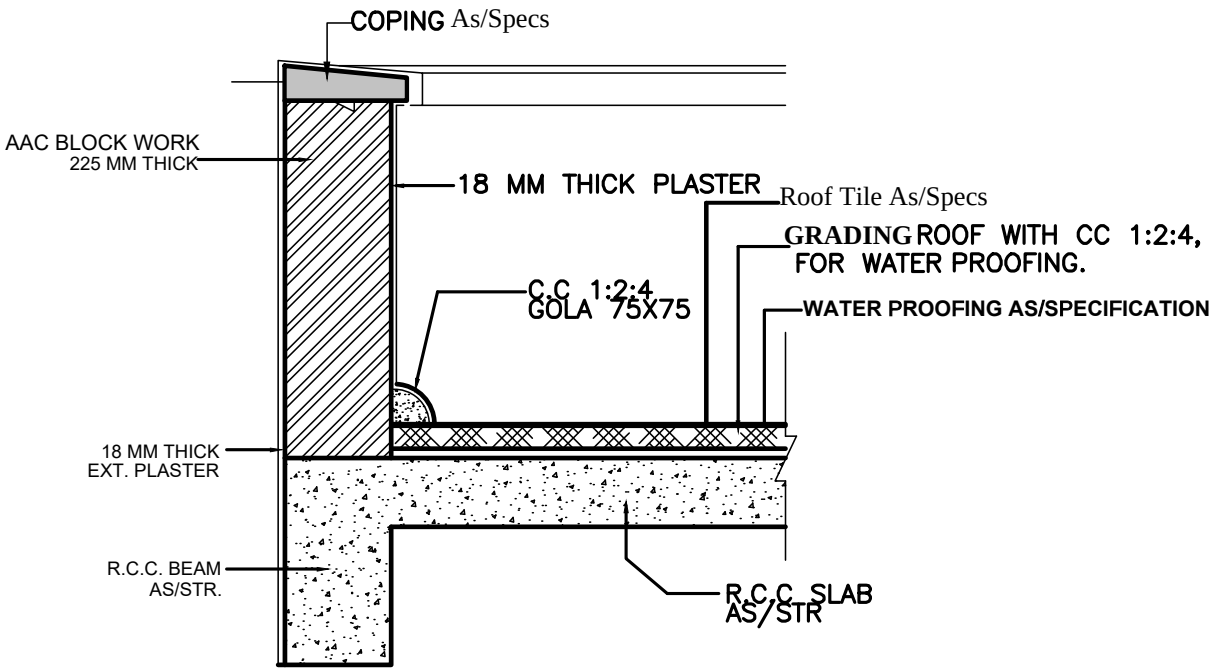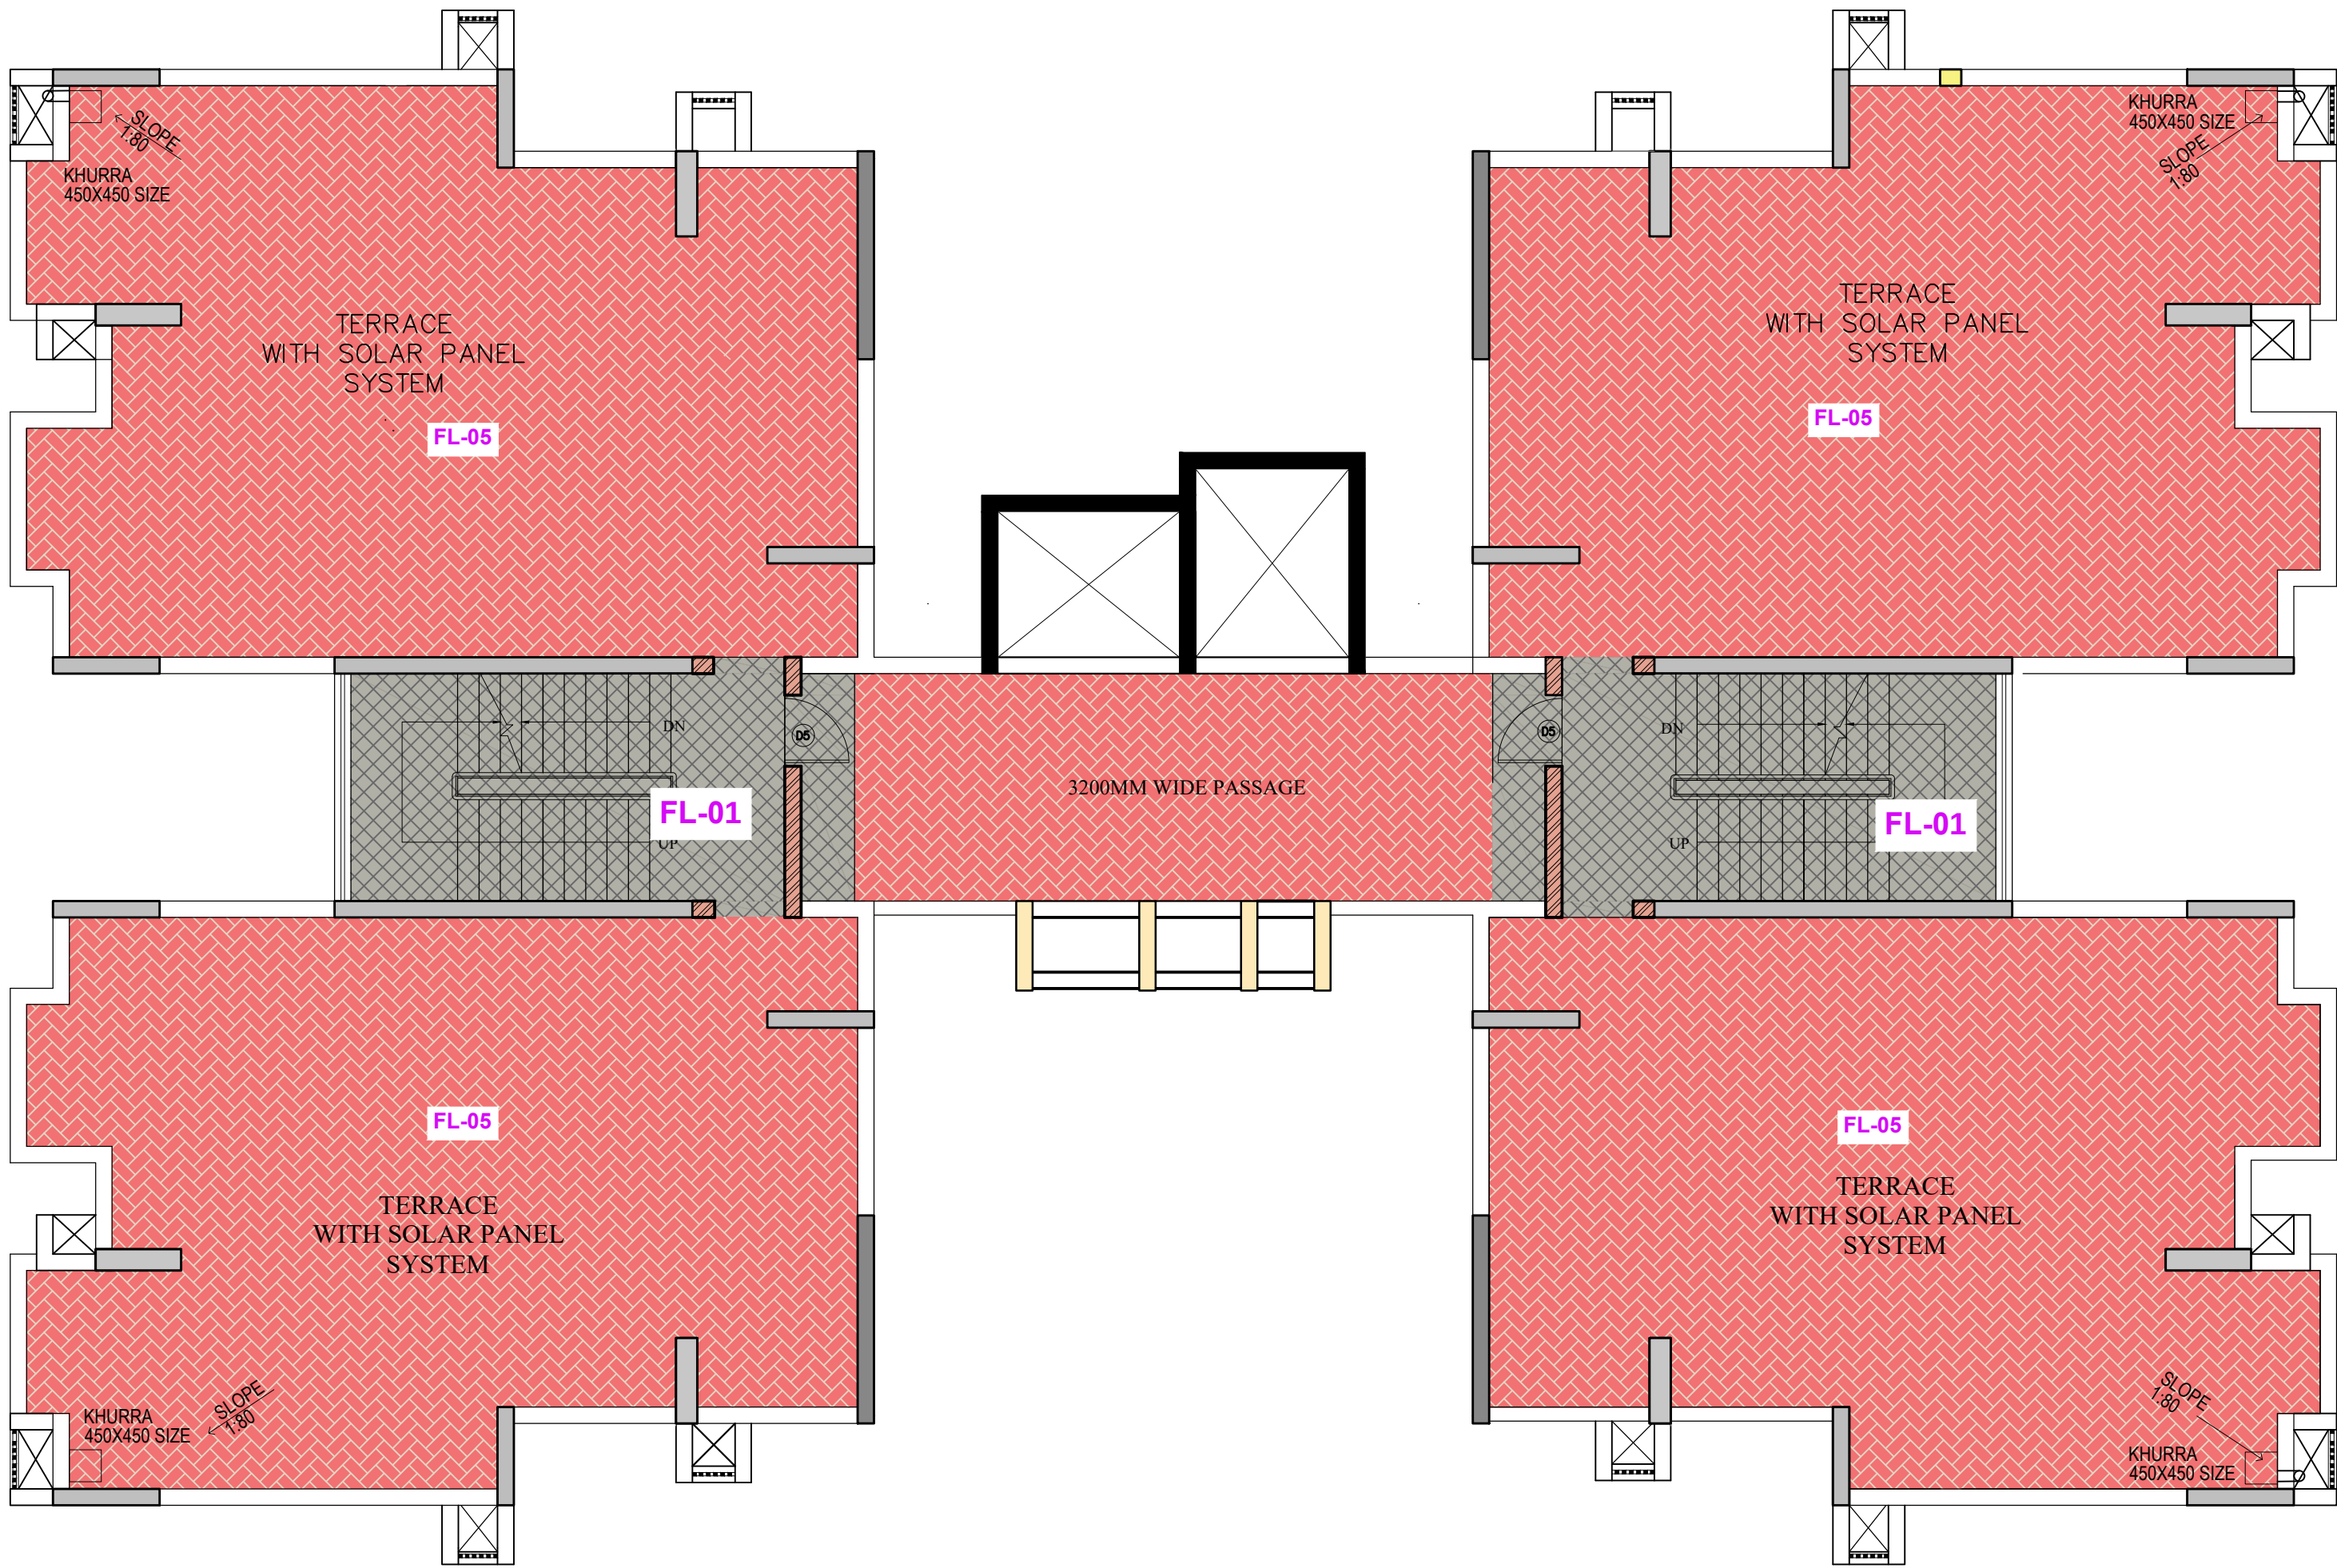


TERRACE WATER PROOFING

01		FL-05	LIQUID RUBBER WATER PROOFING, LAYING CC 1:2:4 CONCRETE FOR ROOF GRADING, HEAT RESISTANT SRI TILES AS PER SPECIFICATIONS.	• TERRACE
02		FL-01	18MM THK POLISHED GRANITE FLOORING AS PER SPECS	• STAIRCASE


- NOTES
- ALL DIMENSIONS ARE IN MM; UNLESS NOTED OTHERWISE.
 - WRITTEN DIMENSIONS ARE TO BE FOLLOWED. DRAWINGS ARE NOT TO BE SCALED.
 - ANY DISCREPANCY IN THE DRAWING SHALL BE BROUGHT TO THE NOTICE OF THE ENGINEER.
 - THIS DRAWING SHALL BE READ IN CONJUNCTION WITH OTHER RELEVANT DRAWINGS.
 - THE FINISHED FLOOR LEVEL (FFL) SHALL BE MAINTAINED MINIMUM 50MM OR AS PER APPLICABLE CODES/SPECIFICATIONS/ SITE REQUIREMENTS ABOVE THE STRUCTURAL SLAB LEVEL OF ALL BUILDINGS. REFER TENDER DOCUMENT FOR DETAILS.

TENDER DRAWING


CLIENT	 OIL INDIA LIMITED (A Govt. of India Enterprise)	
CONSULTANT	 RITES THE INFRASTRUCTURE PEOPLE (A Govt. of India Enterprise)	
PROJECT	BQ WORKMEN HOUSING	
BUILDING	HOUSING BLOCK (G+6)	
DRAWING TITLE	TYPICAL FLOOR FLOORING LAYOUT	
DRG. NO.	RITES/BLD/AR/TD/018	
NORTH	SCALE	DATE
	NTS	JULY 2025

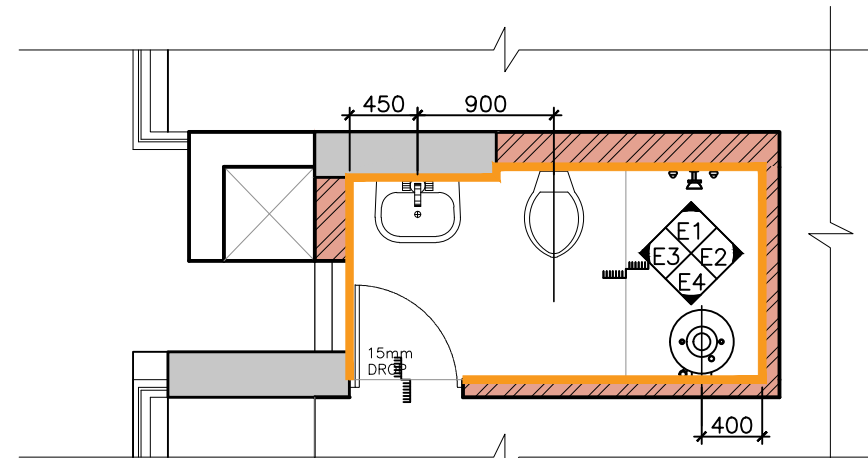


ATTACHED TOILET

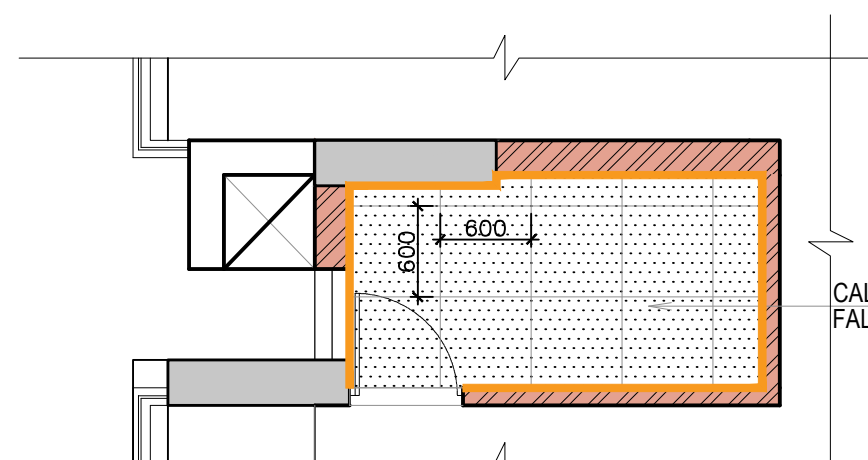


02 PLAN_RCP

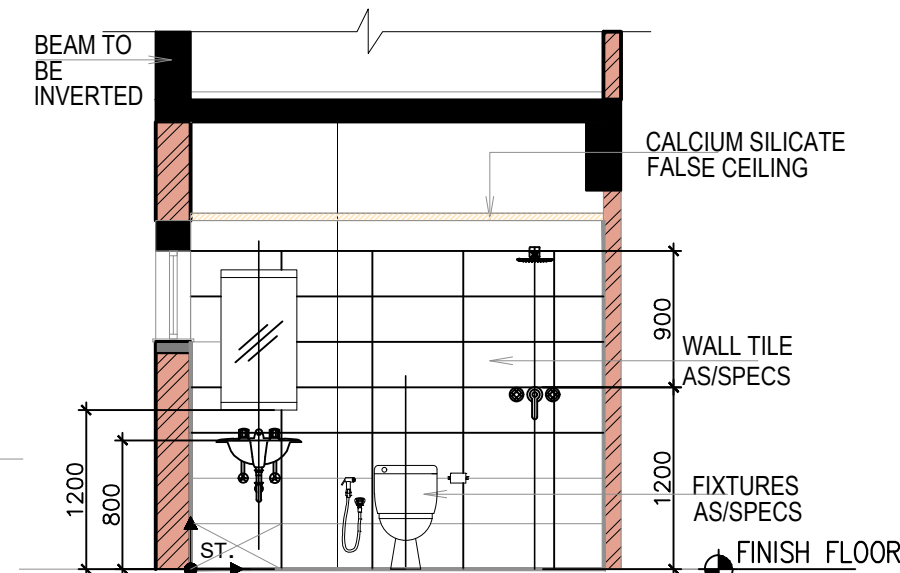


E1 ELEVATION

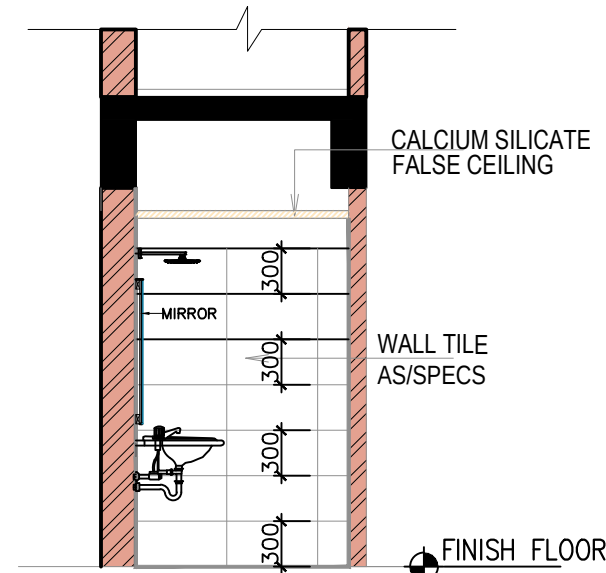

E2 ELEVATION

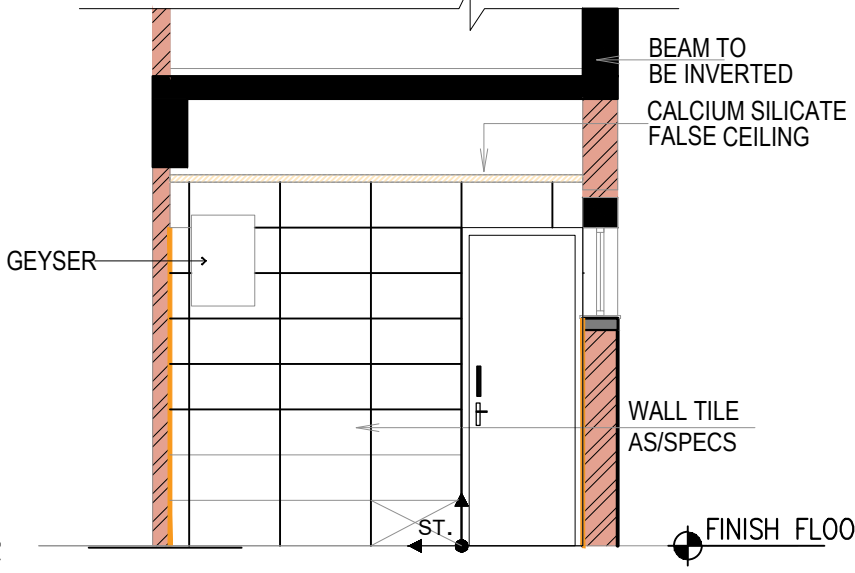


E4 ELEVATION

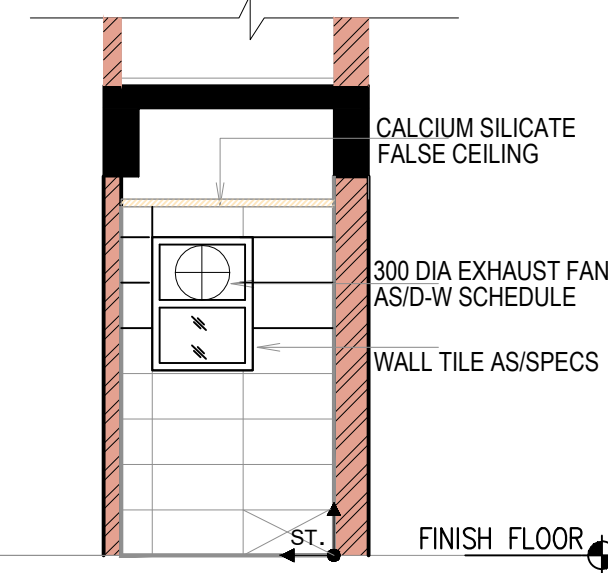


E3 ELEVATION

GRAB BARS IN COMMON TOILETS SHALL BE PROVIDED FOR SPECIALLY ABLED/ELDERLY MEMBERS IN AT LEAST 16 FLATS OF FIRST FLOOR.

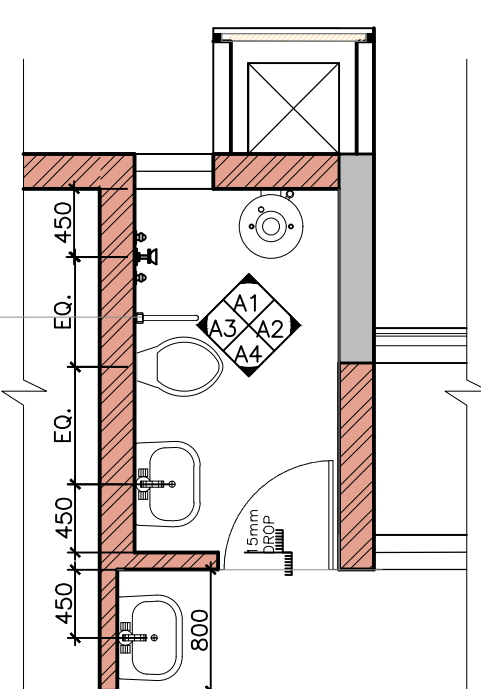

01 COMMON TOILET PLAN

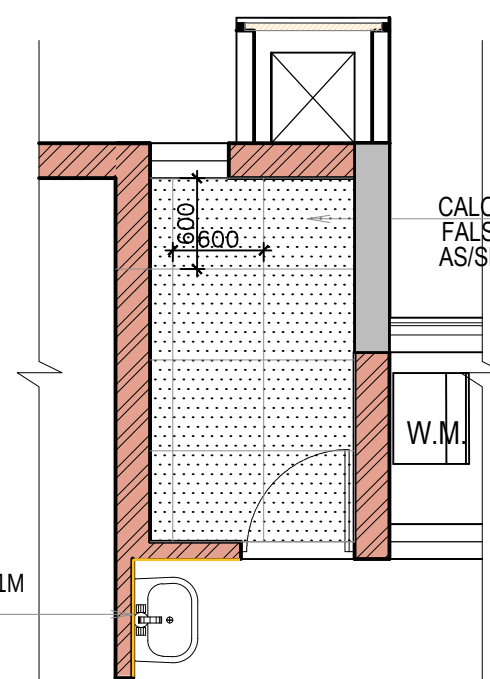


02 PLAN_RCP


COMMON TOILET

LEGEND FOR CLADDING/FLOORING


S. NO.	MATERIAL	HEIGHT FROM FFL
01	CERAMIC WALL TILES AS/SPECS	UPTO CEILING HT.
02	RECTIFIED ANTI SKID CERAMIC TILES (300 X 300)	FLOORING

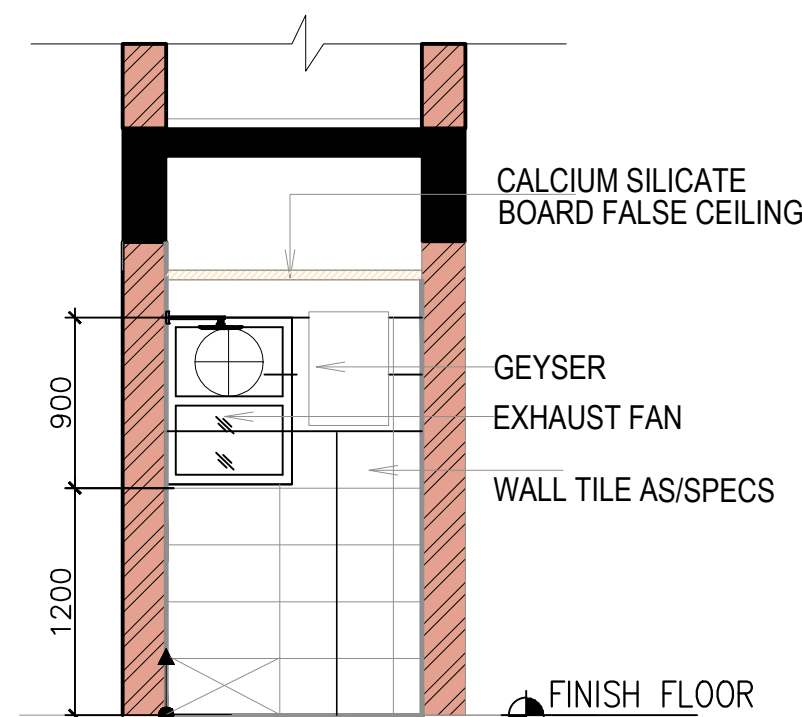


A1 ELEVATION

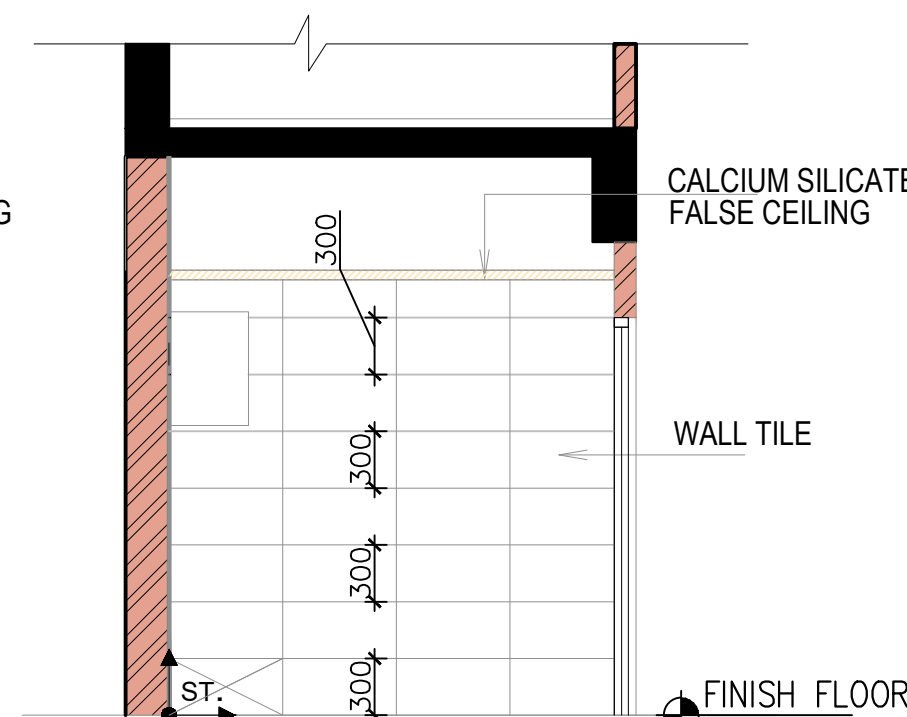

A2 ELEVATION

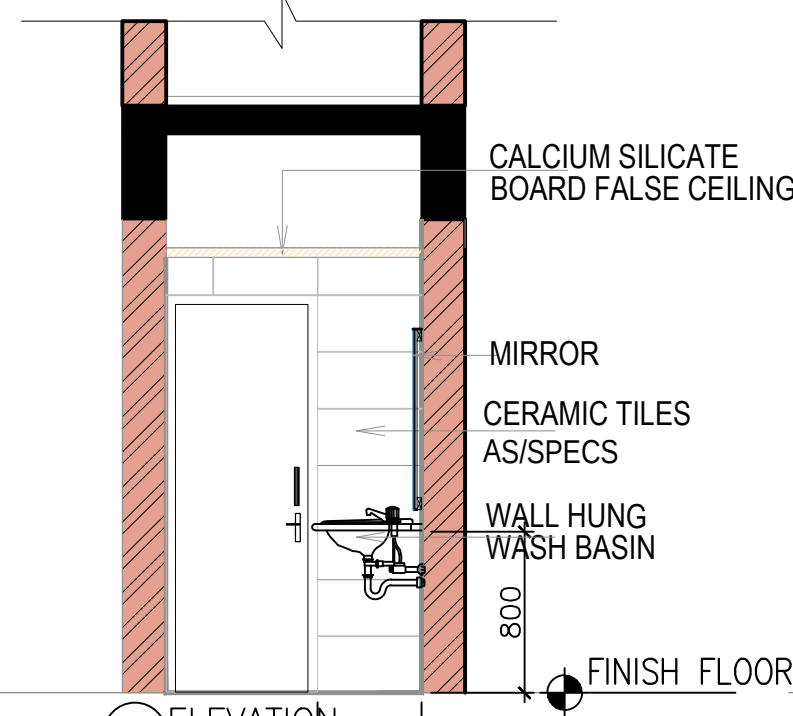

A4 ELEVATION

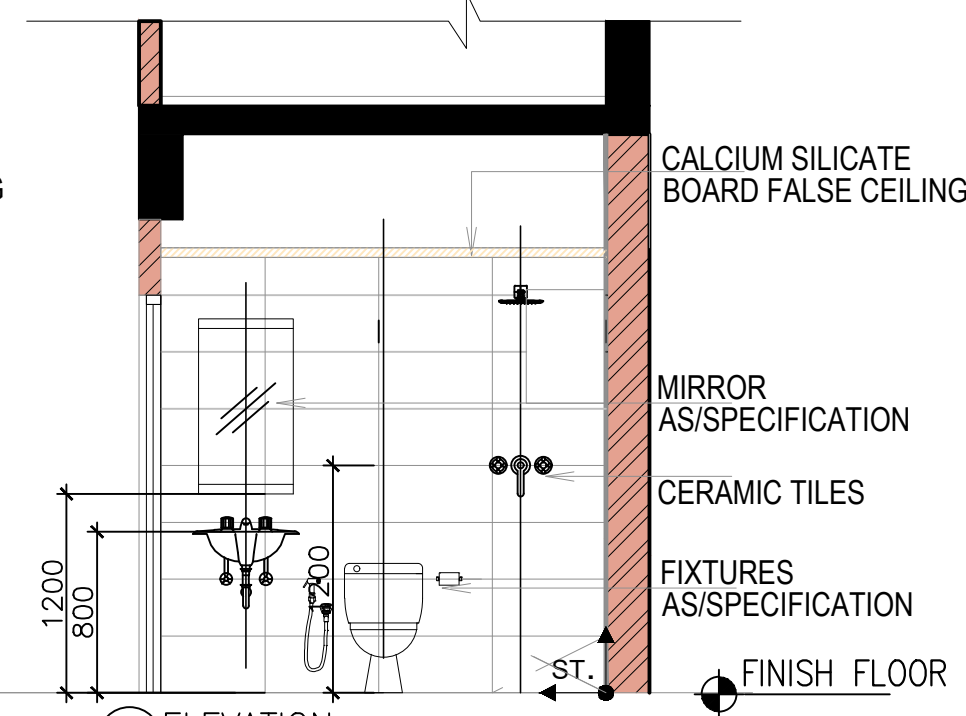

A3 ELEVATION

NOTES

- ALL DIMENSIONS ARE IN MM; UNLESS NOTED OTHERWISE.
- WRITTEN DIMENSIONS ARE TO BE FOLLOWED. DRAWINGS ARE NOT TO BE SCALED.
- ANY DISCREPANCY IN THE DRAWING SHALL BE BROUGHT TO THE NOTICE OF THE ENGINEER.
- THIS DRAWING SHALL BE READ IN CONJUNCTION WITH OTHER RELEVANT DRAWINGS.
- GRAB BARS IN COMMON TOILETS SHALL BE PROVIDED FOR SPECIALLY ABLED/ELDERLY MEMBERS IN AT LEAST 16 FLATS OF FIRST FLOOR.

TENDER DRAWING

CLIENT **OIL INDIA LIMITED**
(A Govt. of India Enterprise)

CONSULTANT **RITES**
THE INFRASTRUCTURE PEOPLE
(A Govt. of India Enterprise)


PROJECT **BQ WORKMEN HOUSING**

BUILDING **HOUSING BLOCK (G+6)**


DRAWING TITLE **TYPICAL TOILET DETAILS**

DRG. NO. **MITES/BLD/AR/TD/019**

NORTH SCALE **NTS** DATE **JULY 2025**

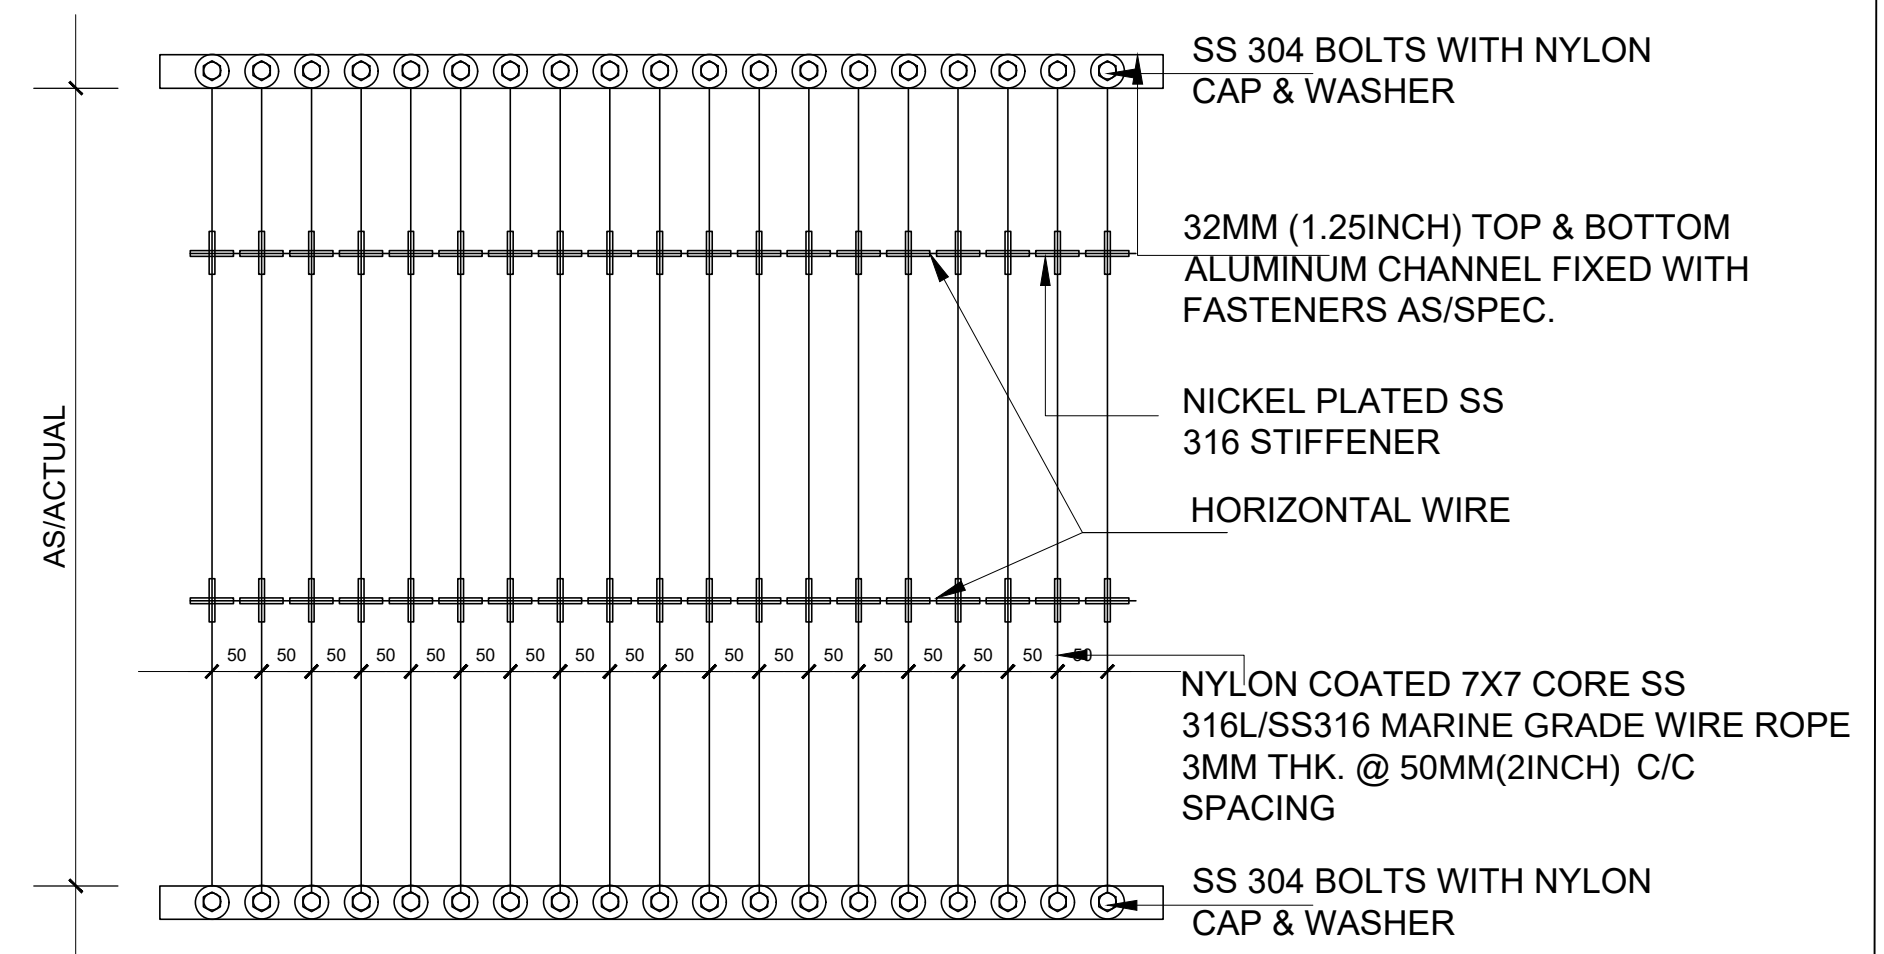

A(INVISIBLE GRILL)

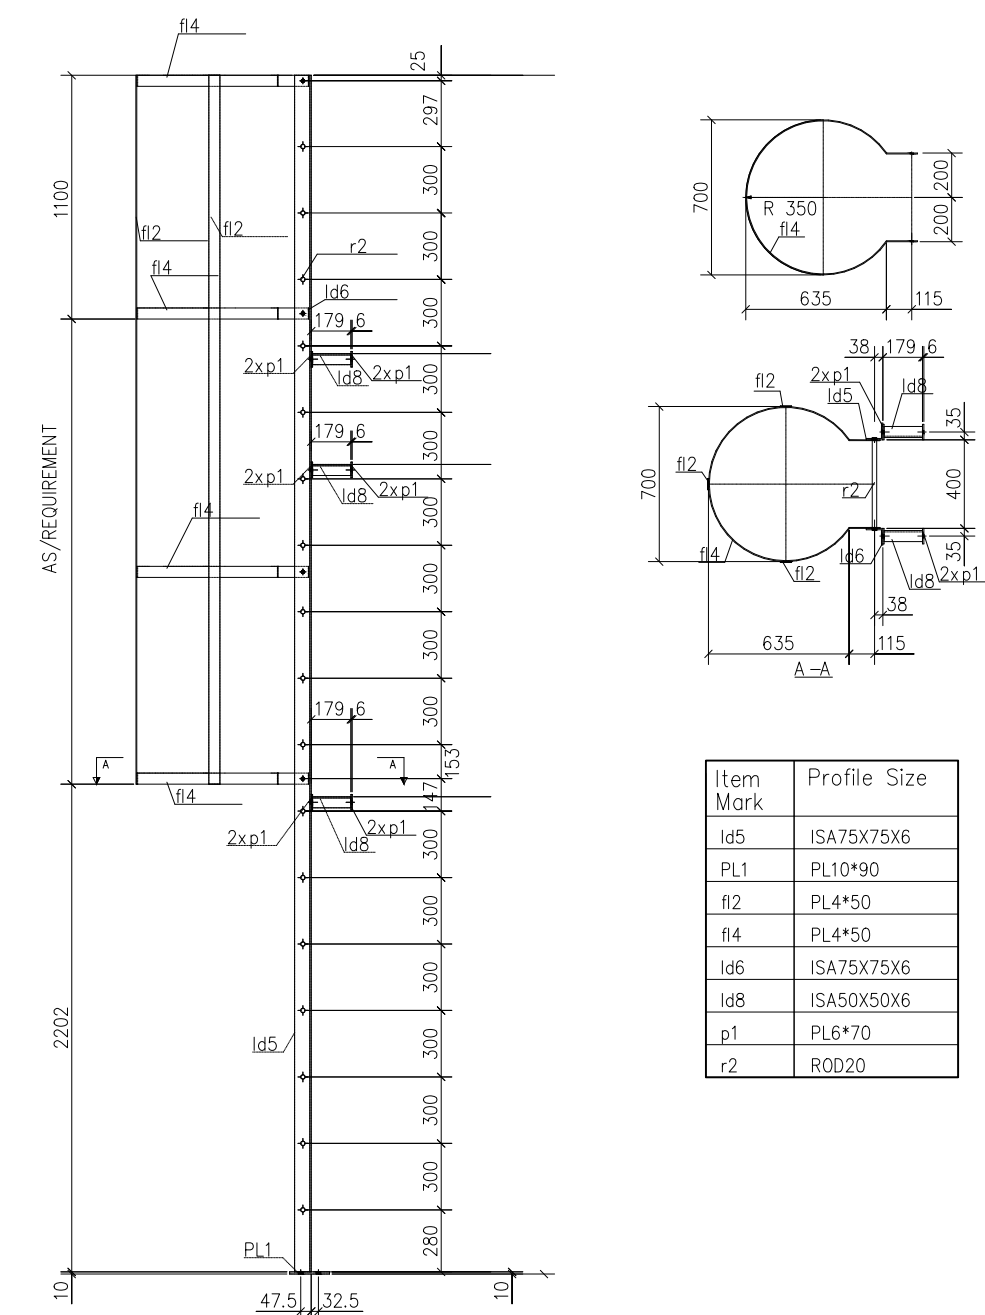

NOTES

1. ALL DIMENSIONS ARE IN MM; UNLESS NOTED OTHERWISE.
2. WRITTEN DIMENSIONS ARE TO BE FOLLOWED. DRAWINGS ARE NOT TO BE SCALED.
3. ANY DISCREPANCY IN THE DRAWING SHALL BE BROUGHT TO THE NOTICE OF THE ENGINEER.
4. THIS DRAWING SHALL BE READ IN CONJUNCTION WITH OTHER RELEVANT DRAWINGS.
5. THE DRAWING IS INDICATIVE ONLY.
6. SHOP DRAWING TO BE PREPARED FOR APPROVAL.
7. REFER SPECIFICATION AND SCHEDULE OF FINISH.

TENDER DRAWING

	CLIENT
--	--------



OIL INDIA LIMITED
(A Govt. of India Enterprise)

CONSULTANT	
------------	--



PROJECT	
---------	--

BQ WORKMEN HOUSING

BUILDING

HOUSING BLOCK (G+6)


	DRAWING TITLE
--	---------------

TYPICAL BALCONY & MS LADDER DETAIL

DRG. NO.	
----------	--

RITES/BLD/AR/TD/019

NORTH

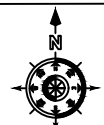

SCALE

NTS

DATE _____

JULY 2025



JULY 2025