


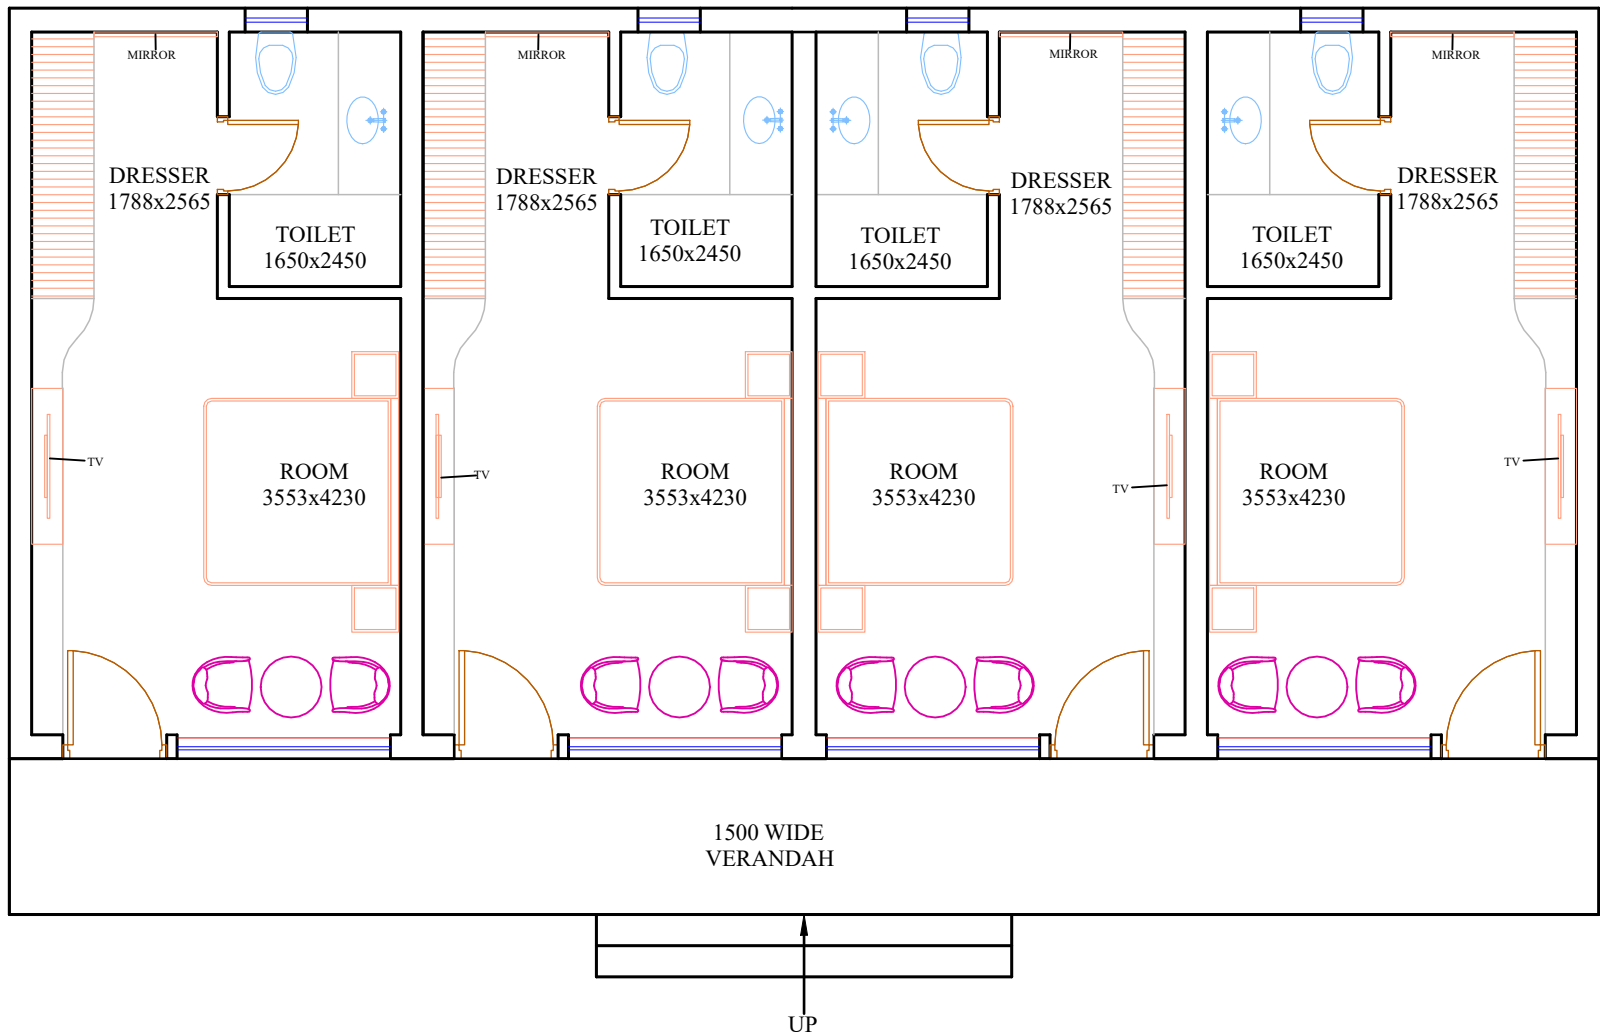

GUEST HOUSE

TOTAL PLINTH AREA = 133.49 SQ.M
ONE UNIT = 27.63 SQ.M
VERANDAH = 22.95 SQ.M

NOTES:-

1. THIS DRAWING IS THE PROPERTY OF M/S TRIPATHI & ASSOCIATES & IT SHALL NOT BE REPRODUCED IN ANY FORM WHATSOEVER WITHOUT THE WRITTEN PERMISSION
2. ALL DIMENSION ARE GIVEN IN MM. & ONLY WRITTEN DIMENSIONS TO BE FOLLOWED.
3. ANY DISCREPANCY IN THE DRW. SHALL BE BROUGHT TO THE NOTICE OF THE ARCHITECTS BEFORE EXECUTION OF THE WORK.
4. RELEASE FOR CONSTRUCTION.
5. THIS DRW. SHOULD BE EXECUTED IN COORDINATION WITH THE STRUCTURAL DRW. BEFORE ENSURING COMPLETE SAFETY OF THE WORK.

ARCHITECT SIGN

TRIPATHI & ASSOCIATES
 ARCHITECTS, PLANNERS & INTERIOR DESIGNERS
 D-136, SECTOR-50, NOIDA-201301
 MOB: 9350184847, 9910006931
 CLIENT

NAVODAYA VIDYALAYA SAMITI

PROJECT
 JAWAHAR NAVODAYA VIDYALAYA,
 AZAMGARH, U.P.

DWG.

GUEST HOUSE (G)

DWG TITLE:

GROUND FLOOR PLAN

DATE: 12-05-2026

DWG.NO.: -

DRN BY: BHAGWAN PRASAD

SCALE:

CONSTRUCTION AGENCY:

TELECOMMUNICATIONS CONSULTANTS INDIA LIMITED
 (A Government of India Enterprise)
 TCIL Bhawan, Greater Kailash-I, New Delhi-110048
 Tel: +91-11-26202020
 www.tcil-india.com Fax: +91-11-26242266
 Email: otuljoin@tcil-india.com
 CIN No.: U74999DL1978GOI008911